

New Residence, 74 Grafton Street, Goulburn, NSW


DA00	Title
DA01	Location Plan
DA02	Site Plan
DA03	Floor & Area Plans
DA04	Elevations
DA05	Elevations
DA06	Section
DA07	3d Views
DA08	Roof Plan
DA09	Solar Diagrams
DA10	Solar Diagrams
DA11	Shadow Digrams
DA12	Shadow Diagrams
DA13	Shadow Diagrams
DA14	Shadow Diagrams








1 LOCATION PLAN
1 : 500

PROJECT TYPE: NEW RESIDENCE DRAWING TITLE: Location Plan VERIFY ALL DIMENSIONS ON SITE. COPYRIGHT © HUGH GORDON ARCHITECT P/L NOT TO BE USED OR COPIED WITHOUT WRITTEN PERMISSION.	CLIENT: DALE CUMMINS PROJECT ADDRESS: PART LOT 1 DP 744621, LOT 3 DP 744621, & LOT 1 DP 197998, 74 GRAFTON STREET, GOULBURN, NSW	DATE: NOV. '25	SHEET ID: DA01				CANBERRA SYDNEY SOUTH COAST P (02) 62626433 M 0410 625 701 E design@hughgordon.com.au W www.hughgordon.com.au HUGH GORDON ARCHITECTS	
		DRAWN: Author						
		SCALE: 1 : 500 @ A3						
		PROJECT #: 74 GRAFTON ST						

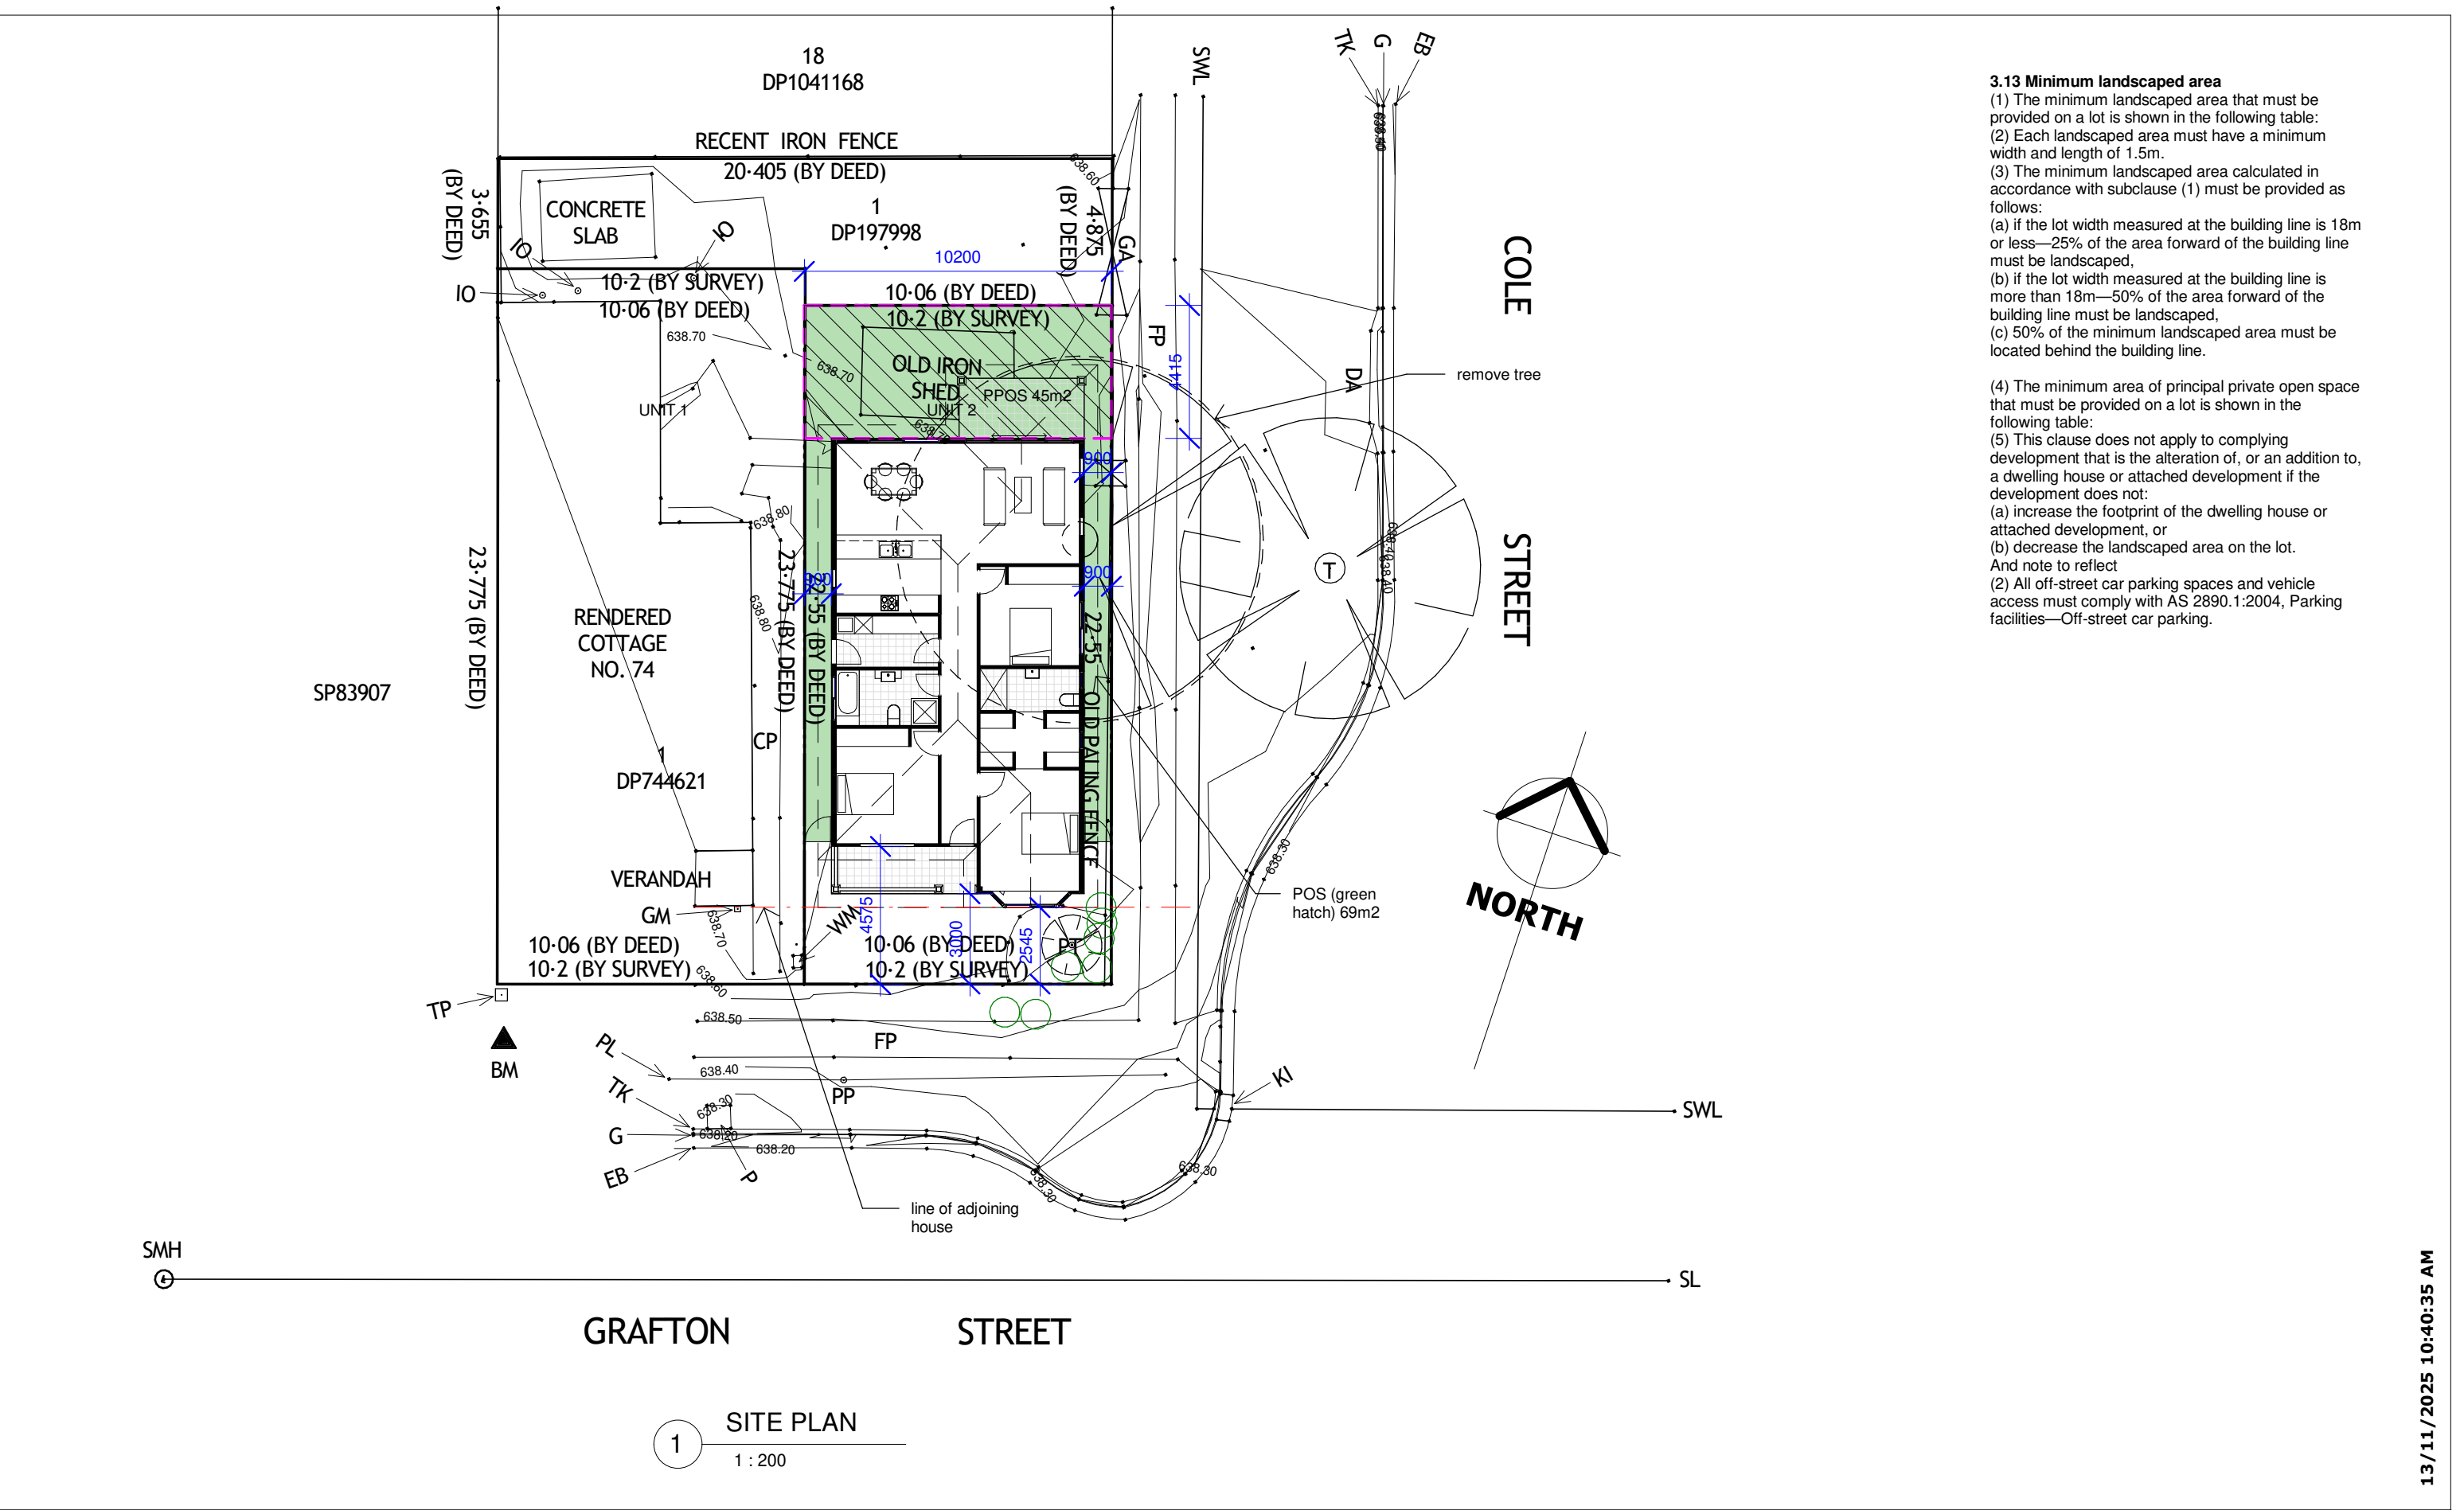

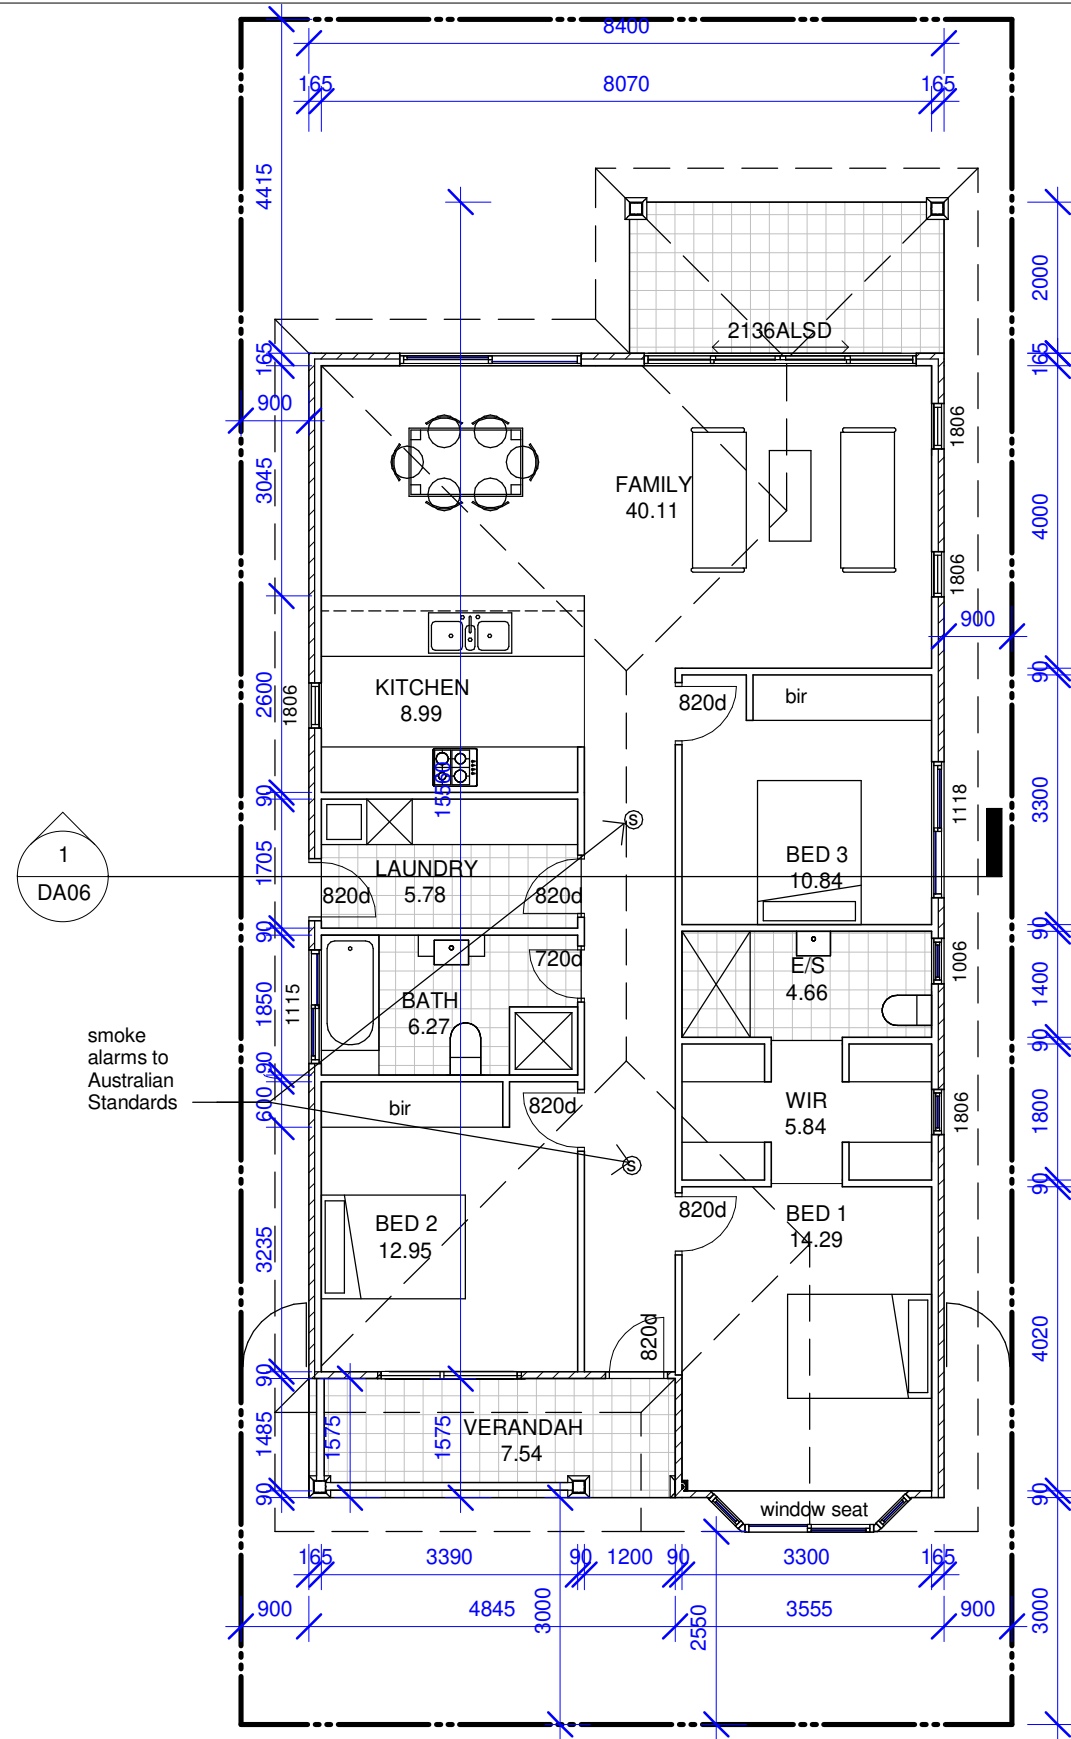

1 GROUND FLOOR PLAN
1 : 100

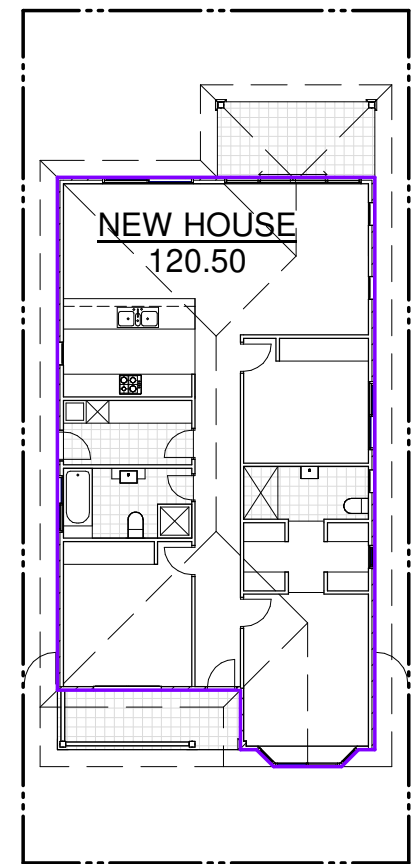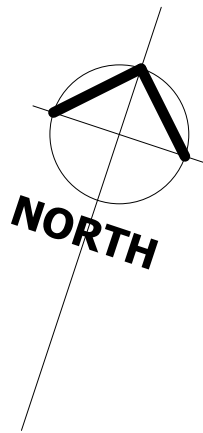

2 AREAS-01
1 : 200

PROJECT TYPE:
NEW RESIDENCE

DRAWING TITLE:
Floor & Area Plans

VERIFY ALL DIMENSIONS ON SITE.
COPYRIGHT © HUGH GORDON ARCHITECT P/L
NOT TO BE USED OR COPIED WITHOUT WRITTEN PERMISSION.

CLIENT:
DALE CUMMINS

PROJECT ADDRESS:
PART LOT 1 DP 744621, LOT 3 DP 744621, & LOT 1 DP 197998, 74 GRAFTON STREET, GOULBURN, NSW

DATE:
NOV. '25

DRAWN:
HG

SCALE:
As indicated @ A3

PROJECT #:
74 GRAFTON ST

SHEET ID:
DA03


Rev	Date	Description

CANBERRA | SYDNEY
SOUTH COAST

P (02) 62626433
M 0410 625 701


E design@hughgordon.com.au
W www.hughgordon.com.au



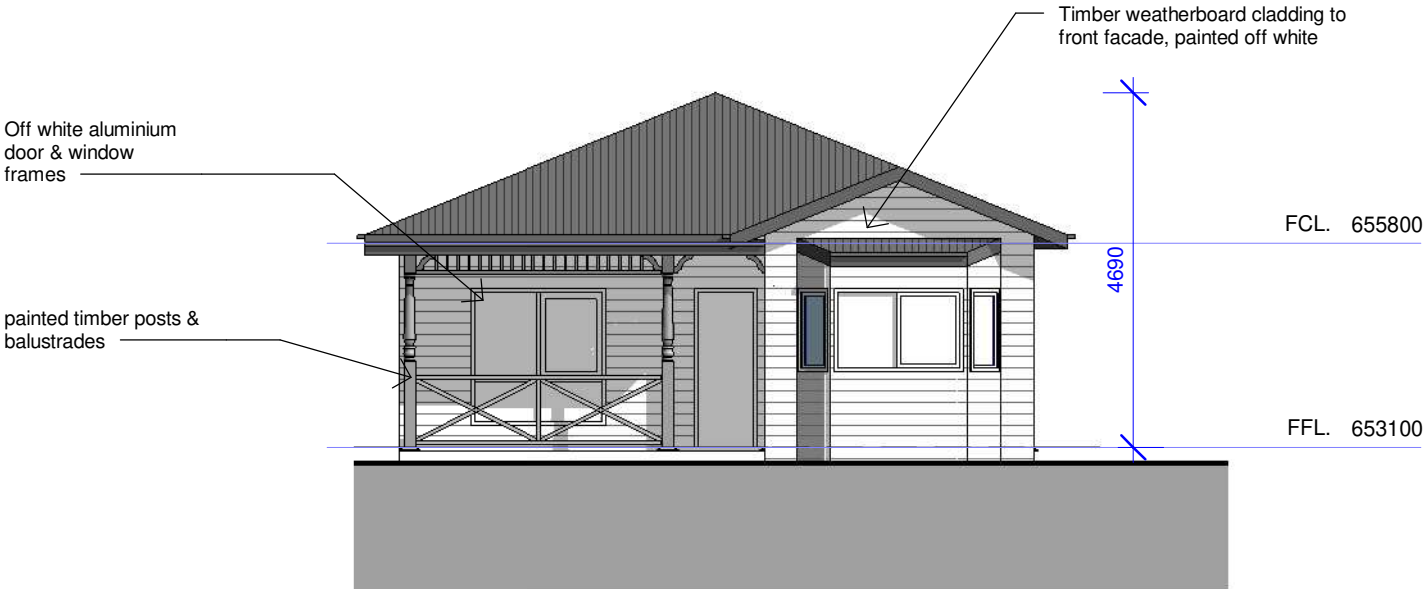

1 SOUTH ELEVATION
1 : 100

BASIX COMMITMENTS			
ITEM	TYPE	INSULATION / RATING/ SIZE	
FLOOR-1	CSOG	SEE NATHERS	
FLOOR-2	NA	NA	
EXTERNAL WALL	NG/FC	R2	
INTERNAL WALL	STUD/SB	NIL	
PARTY WALL	NA	NA	
ROOF	NA	R1.3	
CEILING	MDR	R 4	
WINDOWS	ALFRAME -CLEAR GLASS	SEE LOCATION IN NATHERS	
Windows			
Type	U-Value	SHGC	Area (m²)
ALM-002-01 A Aluminium B SG Clear	6.70	0.70	17.46
ALM-001-01 A Aluminium A SG Clear	6.70	0.57	6.72
WATER	ALL SHOWER HEAD	4 STAR	
	ALL TOILET FLUSHING SYSTEMS	4 STAR	
	ALL KITCHEN TAPS	4 STAR	
	ALL BATH ROOM TAPS	4 STAR	
	RAINWATER TANK	1000 L	
ENERGY	RECYCLING	yes	
	HOT WATER SYSTEMS	GAS	
	AIR CONDITION -LIVING	3	
	COOKING	Ind -ELECTRIC	
	LIGHTING	LED	

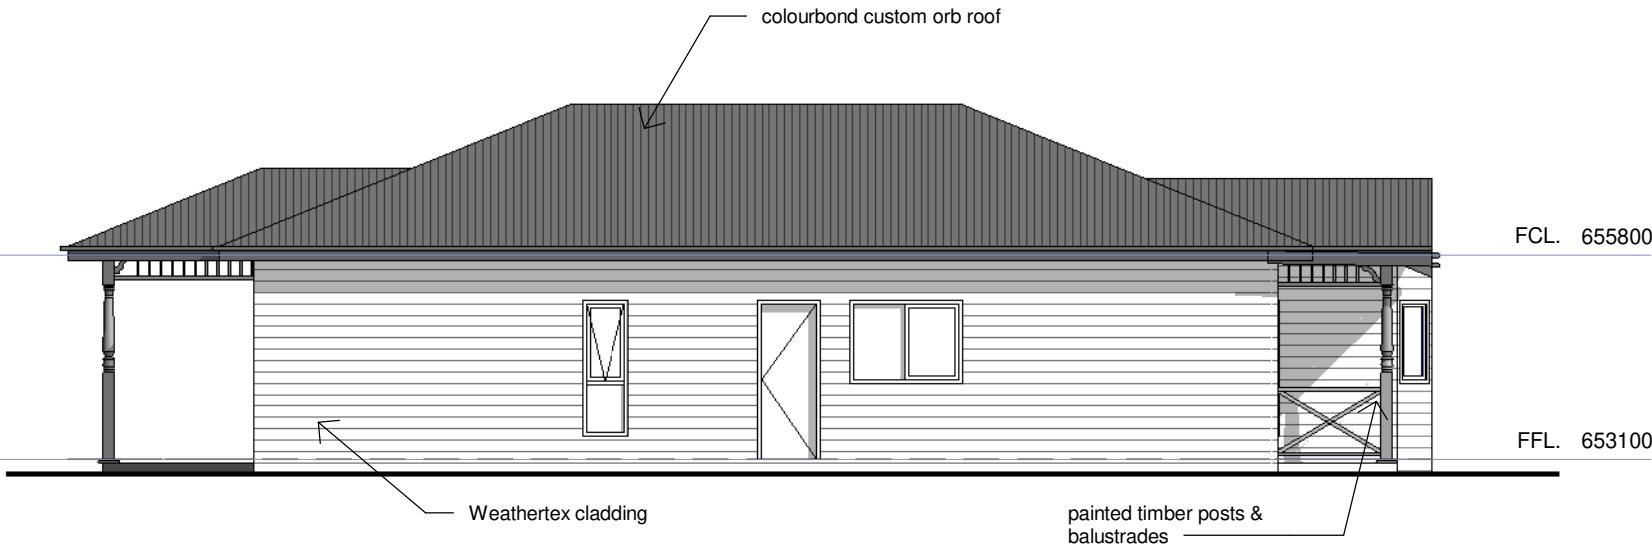


2 WEST ELEVATION
1 : 100



1 NORTH ELEVATION
1 : 100



2 EAST ELEVATION
1 : 100

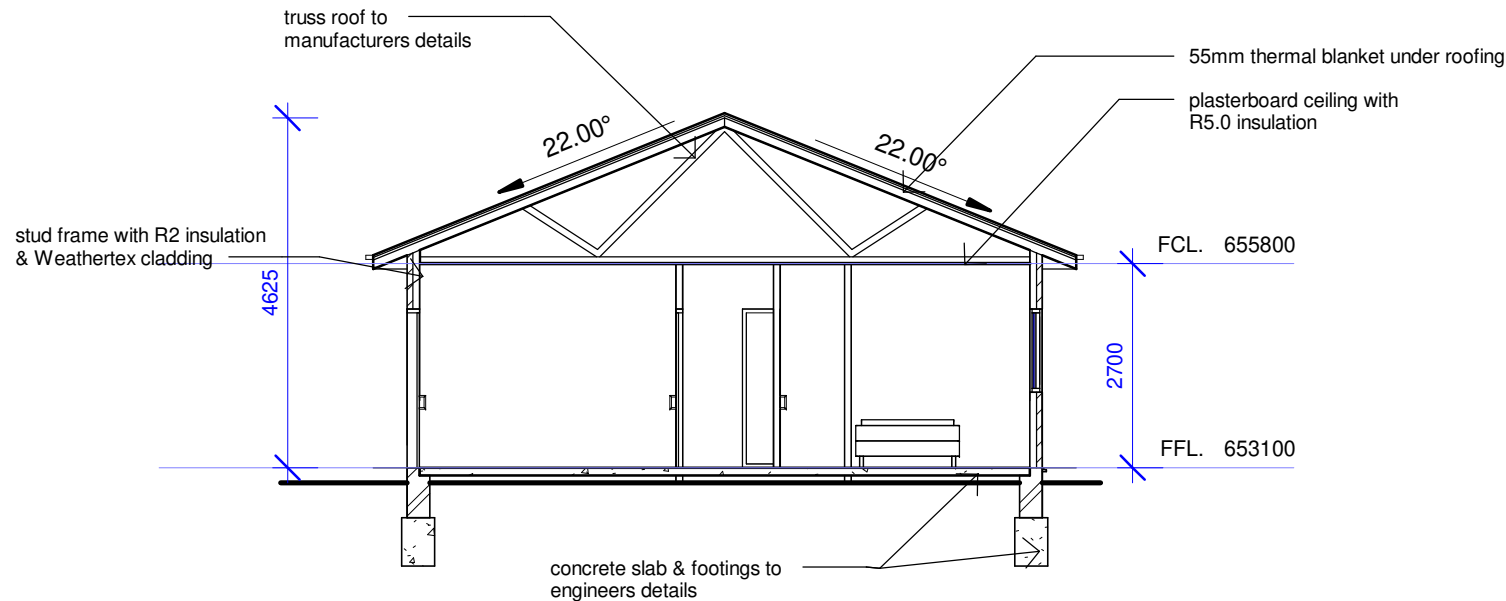

1 SECTION A
1 : 100

NOTES & GENERAL CONDITIONS

ALL CONSTRUCTION IN ACCORDANCE WITH BCA AND RELEVANT SAA CODES

COMPLETE THE WORKS WITHIN THE CONTRACT PERIOD IN ACCORDANCE WITH THE DRAWINGS.

COMPLY WITH REGULATIONS AND BY-LAWS OF AUTHORITIES WITH JURISDICTION OVER THE WORKS AND INCLUDING THOSE RELATING TO WATER SUPPLY, GAS, SEWERAGE, HEALTH AND ELECTRICITY. GIVE ALL NOTICES AND PAY ALL FEES REQUIRED BY THE AUTHORITIES.

WORK SHOWN OR DESCRIBED ON THE DRAWINGS OR IN THE SCHEDULE IS TO BE CARRIED OUT WHETHER DRAWN AND NOT SPECIFIED OR VICE VERSA. THE REQUIREMENTS OF REGULATIONS TAKE PRECEDENCE OVER THE DRAWINGS. DETAIL DRAWINGS TAKE PRECEDENCE OVER GENERAL DRAWINGS.

BUILDER TO VERIFY ALL DIMENSIONS ON SITE PRIOR TO COMMENCEMENT OF CONSTRUCTION WORKS, PRODUCING SHOP DRAWINGS OR FABRICATING COMPONENTS. REPORT ANY DISCREPANCIES TO ARCHITECT FOR DECISION BEFORE PROCEEDING WITH WORK.

WRITTEN DIMENSIONS ARE IN MILLIMETRES AND TAKE PRECEDENCE OVER SCALED ONES

BUILDER TO CHECK WINDOW DIMENSIONS BEFORE ORDERING

GROUND LINES SHOWN ARE INDICATIVE ONLY AND SHOULD BE VERIFIED ON SITE

LINTELS TO TRUSS MANUFACTURERS TABLES, NEW TIMBER ROOF TRUSSES TO MANUFACTURER'S SPECIFICATION.

CONCRETE SLABS AND FOOTINGS TO AS. 2870-1998 ENGINEERING OPTION ADOPTED. ALL FOOTINGS TO BE TAKEN DOWN TO SOLID GROUND, TERMITE PROTECTION TO COMPLY WITH AS.1694 'PHYSICAL BARRIERS' & AS. 3660 'APPENDIX D'. FRAMING TO AS. 1684-1992 'NATIONAL TIMBER FRAMING CODE' AND SUPPLIMENTS. HARDWOOD TO AS.3000, BRICKWORK TO AS.3700 'SAA MASONRY CODE AND AS.1640 'SAA BRICKWORK CODE', STRUCTURAL STEEL TO AS.1170 & AS.4100, SMOKE ALARMS TO AS.3786, WET SEAL TO AS.3740, PLUMBING TO AS3500.

ALUMINIUM FRAMED WINDOWS WITH OPENING STYLES IN ACCORDANCE WITH ELEVATIONS AND FROM APPROVED MANUFACTURER UNO.

ENGINEERING DOCUMENTATION TAKES PRECEDENCE OVER ARCHITECTURAL STRUCTURAL SIZINGS.

GRADE SITES TO ALLOW FOR SURFACE DRAINAGE

SMOKE ALARMS CONNECTED TO MAINS POWER SUPPLY, WITH BATTERY BACKUP, ARE TO BE INSTALLED IN ACCORDANCE WITH AS 3786-2014

PROJECT TYPE:
NEW RESIDENCE

DRAWING TITLE:
Section

VERIFY ALL DIMENSIONS ON SITE.

COPYRIGHT © HUGH GORDON ARCHITECT P/L

NOT TO BE USED OR COPIED WITHOUT WRITTEN PERMISSION.

CLIENT:
DALE CUMMINS

PROJECT ADDRESS:
PART LOT 1 DP 744621, LOT 3 DP 744621, & LOT 1 DP 197998, 74 GRAFTON STREET, GOULBURN, NSW

DATE:
NOV. '25

DRAWN:
Author

SCALE:
1 : 100 @ A3

PROJECT #:
74 GRAFTON ST

SHEET ID:
DA06

Rev	Date	Description



CANBERRA | SYDNEY
SOUTH COAST


P (02) 62626433
M 0410 625 701

E design@hughgordon.com.au
W www.hughgordon.com.au



HUGH GORDON ARCHITECTS

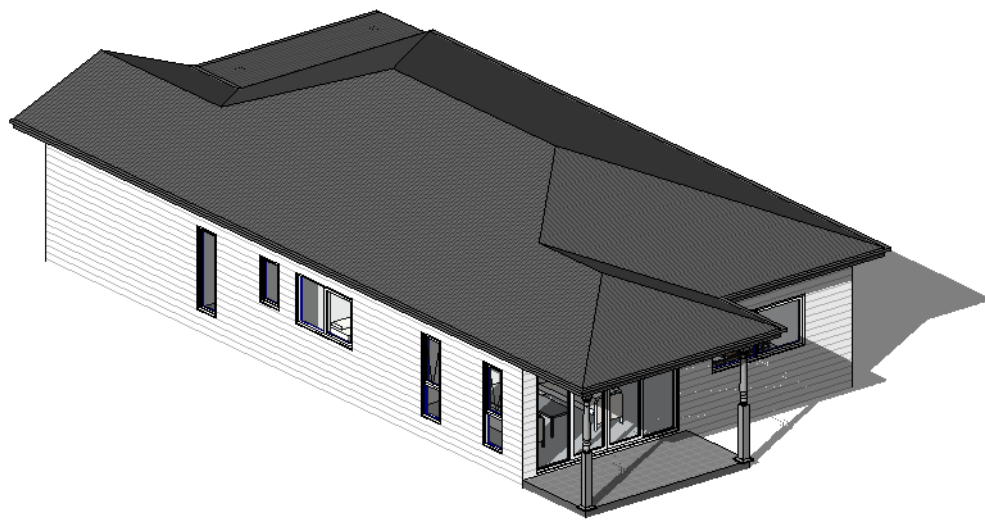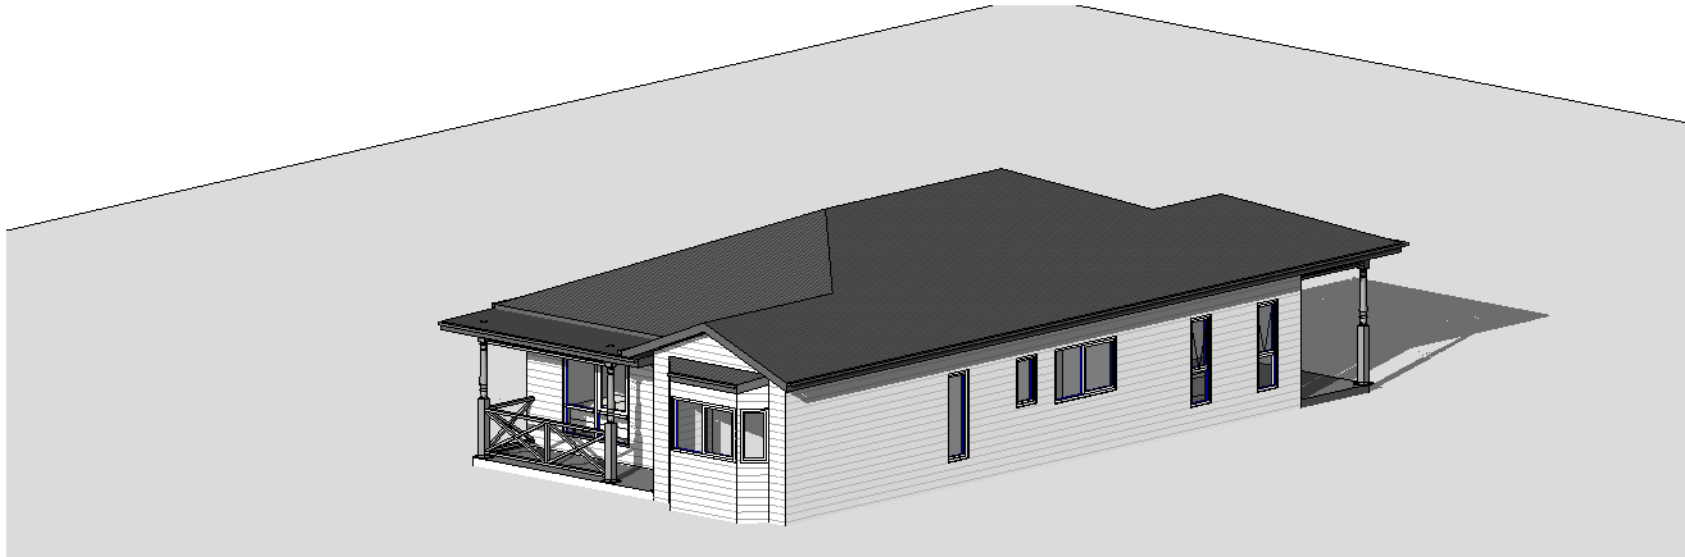

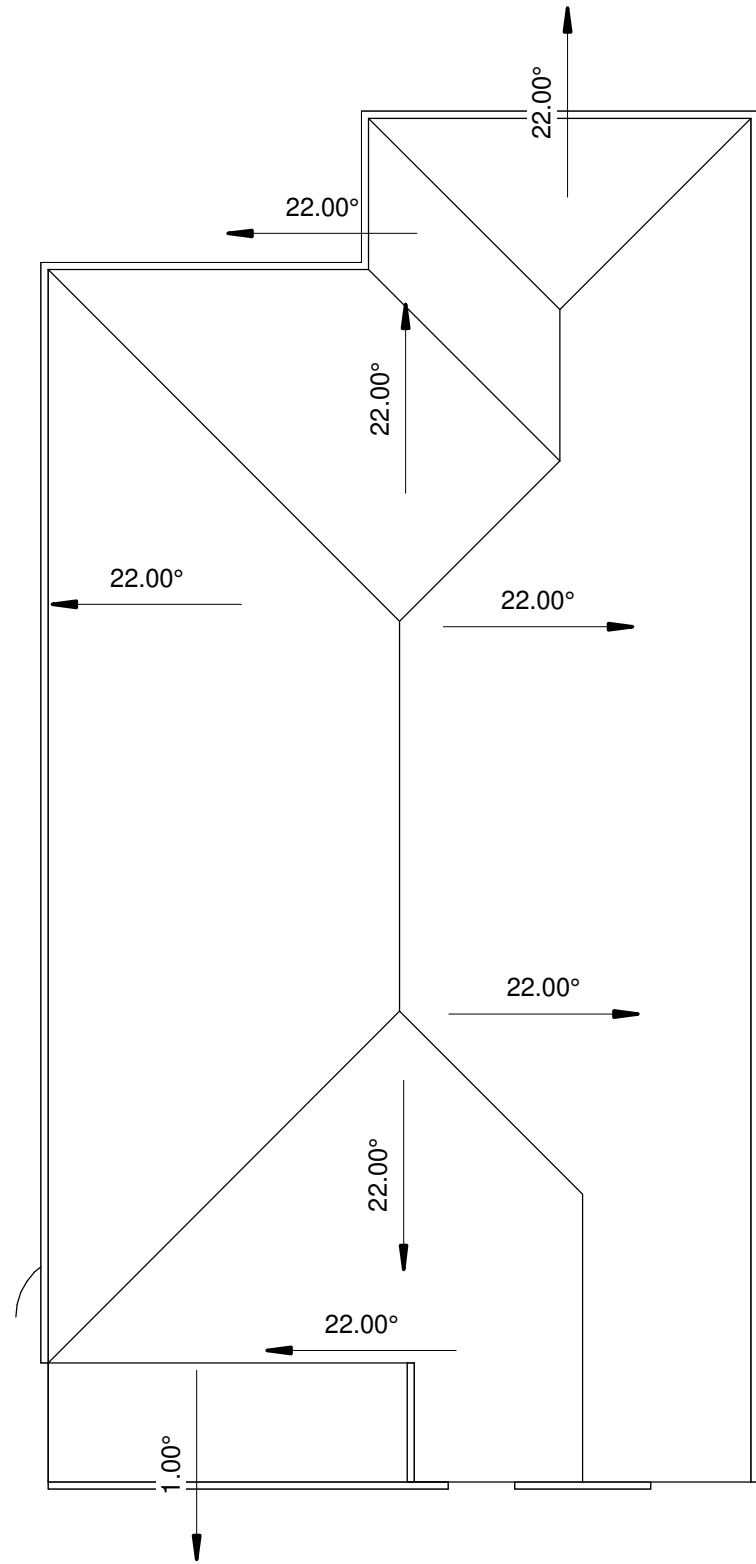


1 ROOF PLANS
1 : 100


13/11/2025 10:40:37 AM

PROJECT TYPE: NEW RESIDENCE DRAWING TITLE: Roof Plan VERIFY ALL DIMENSIONS ON SITE. COPYRIGHT © HUGH GORDON ARCHITECT P/L NOT TO BE USED OR COPIED WITHOUT WRITTEN PERMISSION.	CLIENT: DALE CUMMINS PROJECT ADDRESS: PART LOT 1 DP 744621, LOT 3 DP 744621, & LOT 1 DP 197998, 74 GRAFTON STREET, GOULBURN, NSW	DATE: NOV. '25	SHEET ID: DA08				CANBERRA SYDNEY SOUTH COAST P (02) 62626433 M 0410 625 701 E design@hughgordon.com.au W www.hughgordon.com.au HUGH GORDON ARCHITECTS
		DRAWN: HG					
		SCALE: 1 : 100 @ A3					
		PROJECT #: 74 GRAFTON ST					
				Rev	Date	Description	


Solar Diagrams 21 June

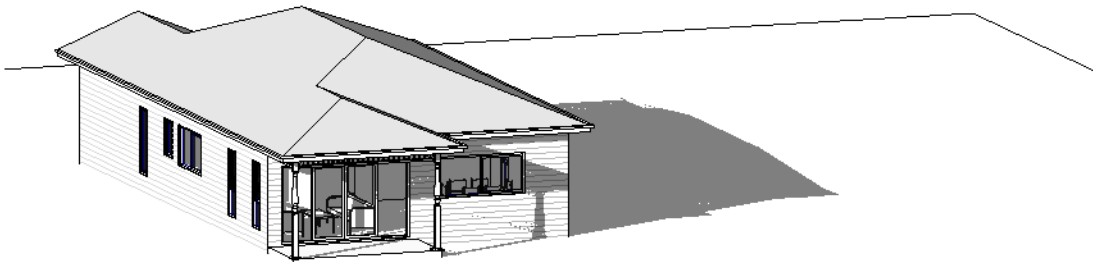


1 SOLAR DIAGRAM 9am

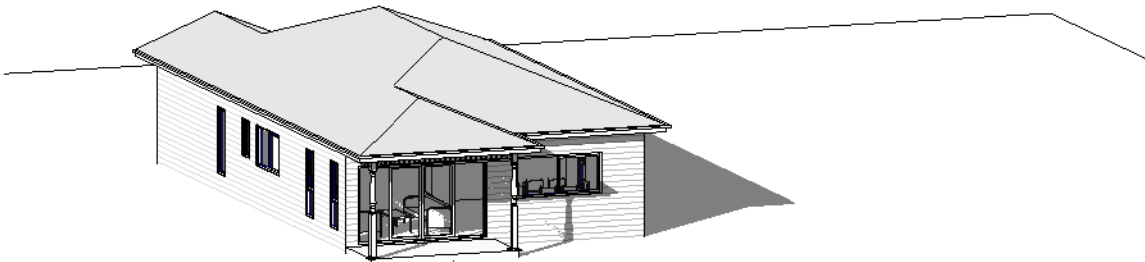

2 SOLAR DIAGRAM 10am

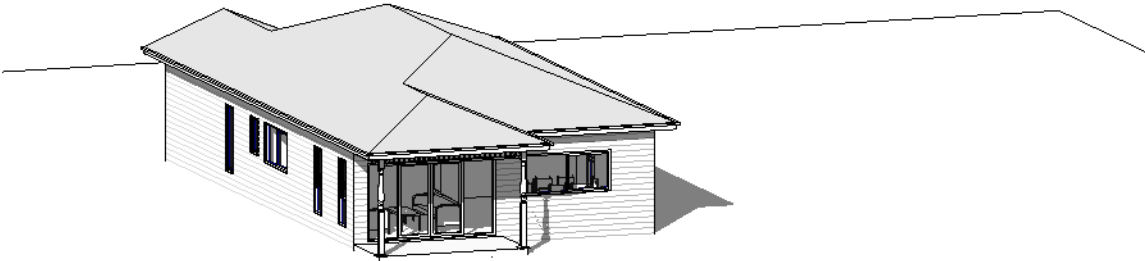


3 SOLAR DIAGRAM 11am

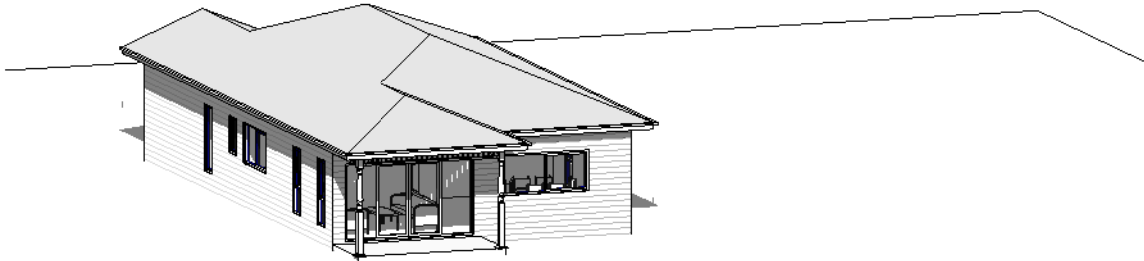


4 SOLAR DIAGRAM 12pm

13/11/2025 10:40:37 AM


Solar Diagrams 21 June

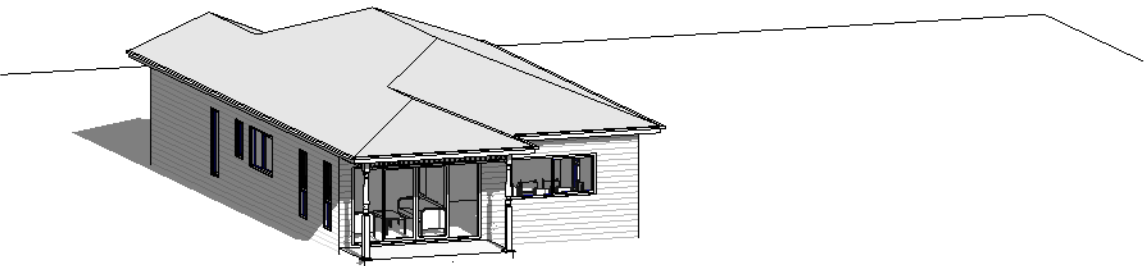

1 SOLAR DIAGRAM 1pm


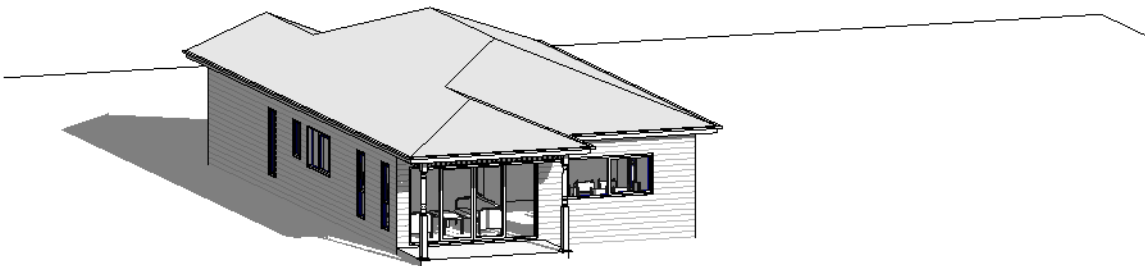


2 SOLAR DIAGRAM 2pm


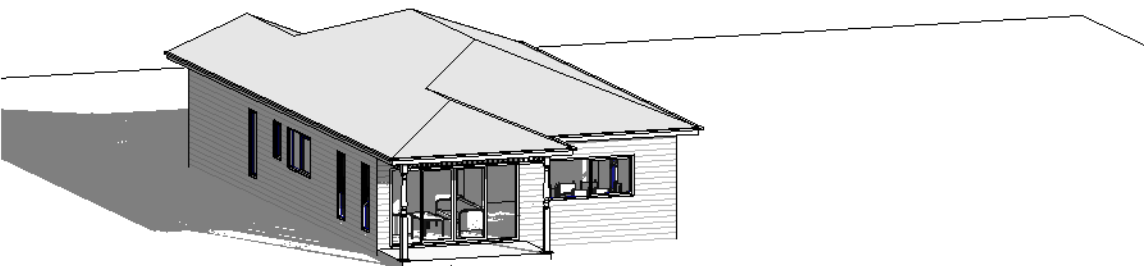


3 SOLAR DIAGRAM 3pm

13/11/2025 10:40:37 AM

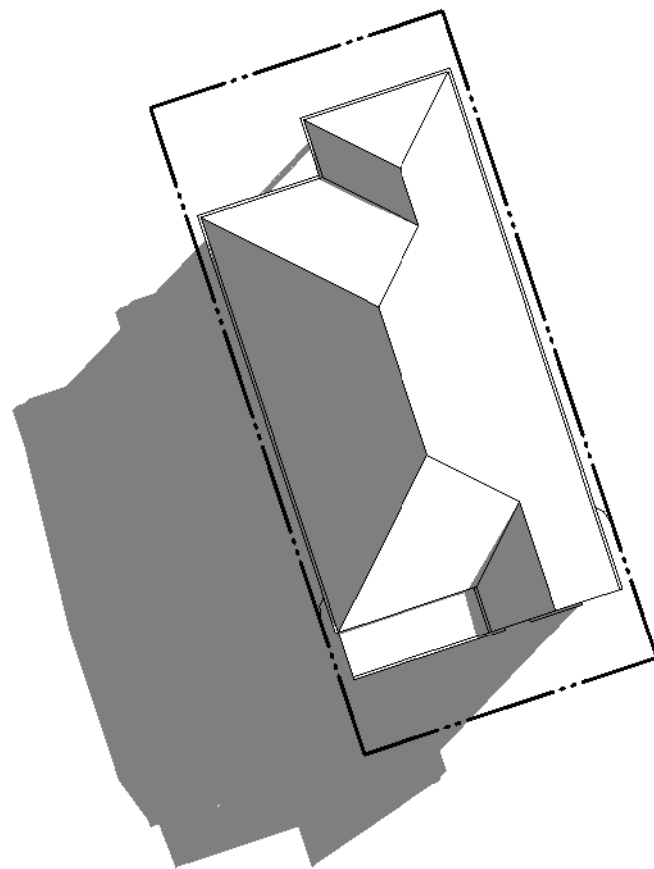
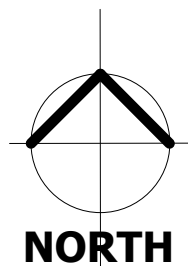


1 SHADOW DIAGRAM 9am 21 JUNE
1 : 250

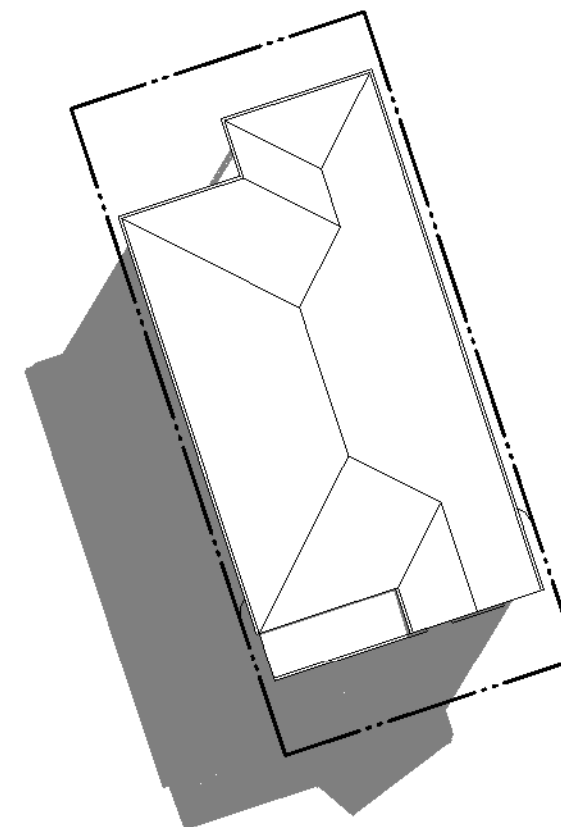
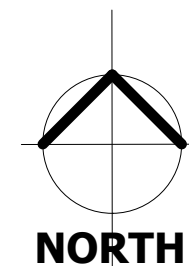


2 SHADOW DIAGRAM 10am 21 JUNE
1 : 250

13/11/2025 10:40:38 AM

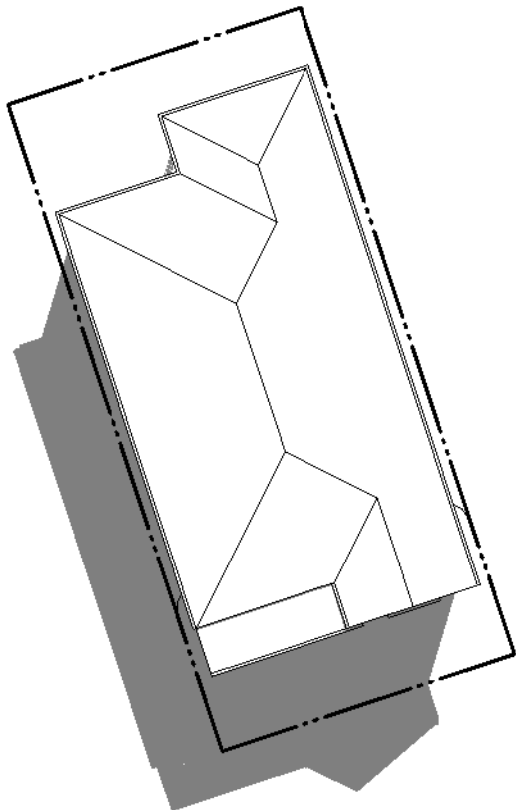
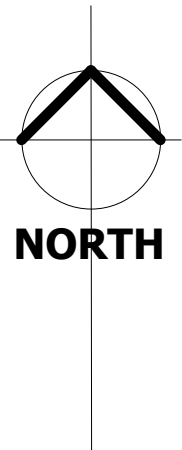


1 SHADOW DIAGRAM 11am 21 JUNE
1 : 250

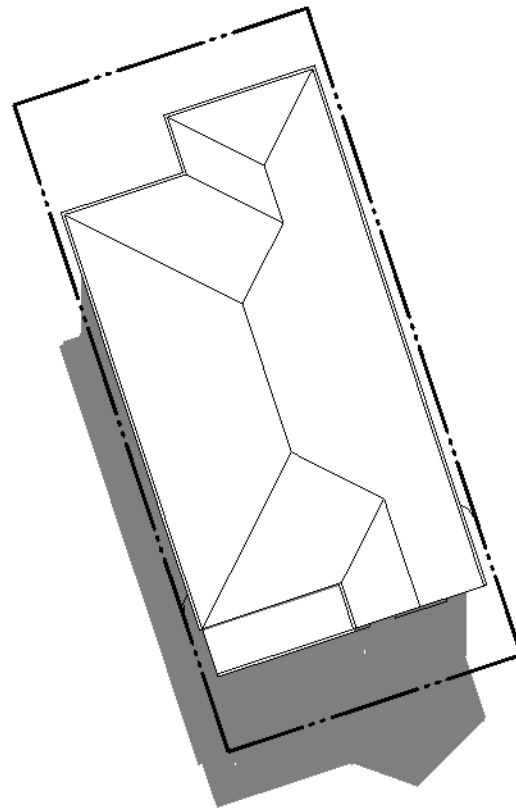
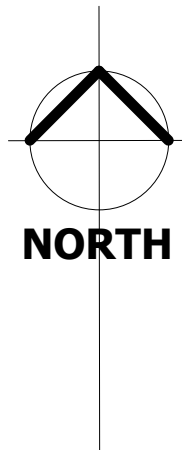


2 SHADOW DIAGRAM 12pm 21 JUNE
1 : 250

13/11/2025 10:40:38 AM

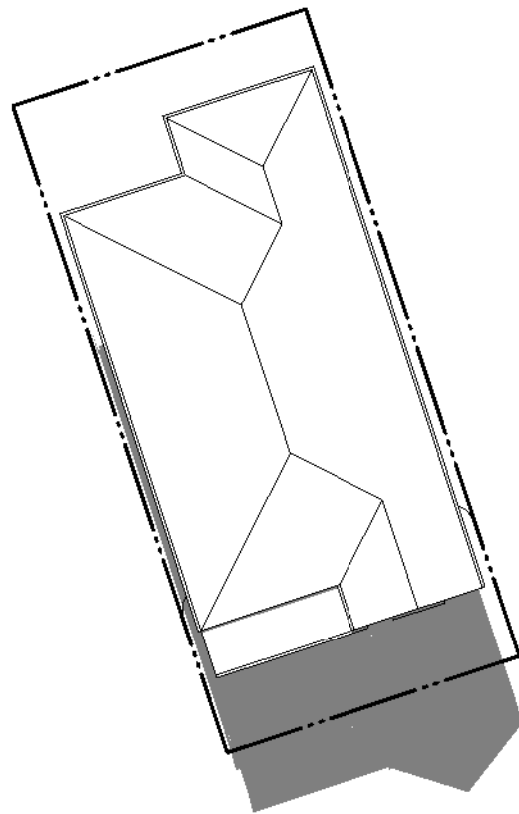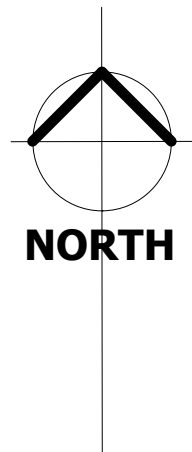

1 SHADOW DIAGRAM 1pm 21 JUNE
1 : 250

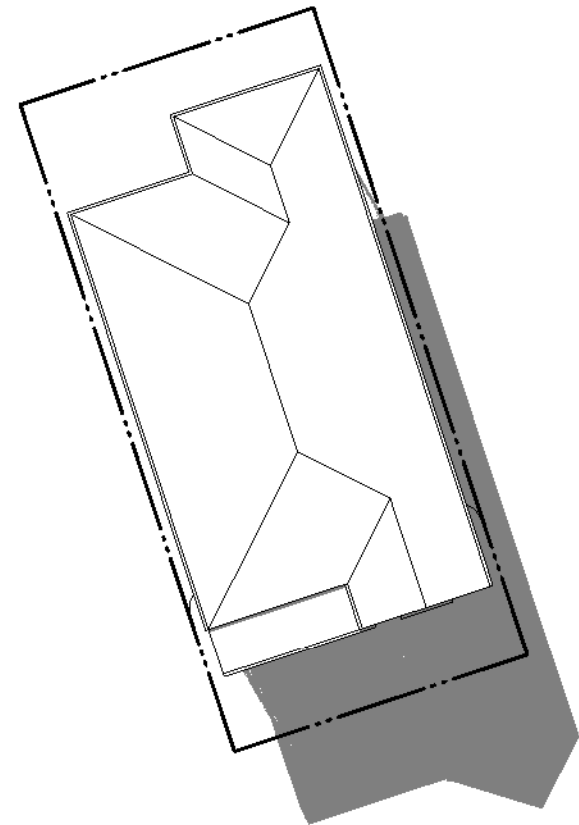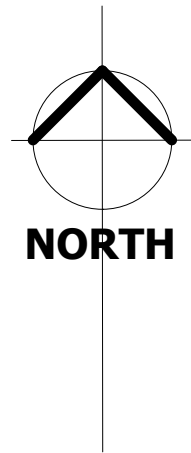

2 SHADOW DIAGRAM 2pm 21 JUNE
1 : 250

PROJECT TYPE:
NEW RESIDENCE

DRAWING TITLE:
Shadow Diagrams

VERIFY ALL DIMENSIONS ON SITE.
COPYRIGHT © HUGH GORDON ARCHITECT P/L
NOT TO BE USED OR COPIED WITHOUT WRITTEN PERMISSION.

CLIENT:
DALE CUMMINS

PROJECT ADDRESS:
PART LOT 1 DP 744621, LOT 3 DP 744621, & LOT 1 DP 197998, 74 GRAFTON STREET, GOULBURN, NSW

DATE:
NOV. '25

DRAWN:
Author

SCALE:
1 : 250 @ A3

PROJECT #:
74 GRAFTON ST

SHEET ID:
DA13



Rev	Date	Description

CANBERRA | SYDNEY
SOUTH COAST

P (02) 62626433
M 0410 625 701

E design@hughgordon.com.au
W www.hughgordon.com.au



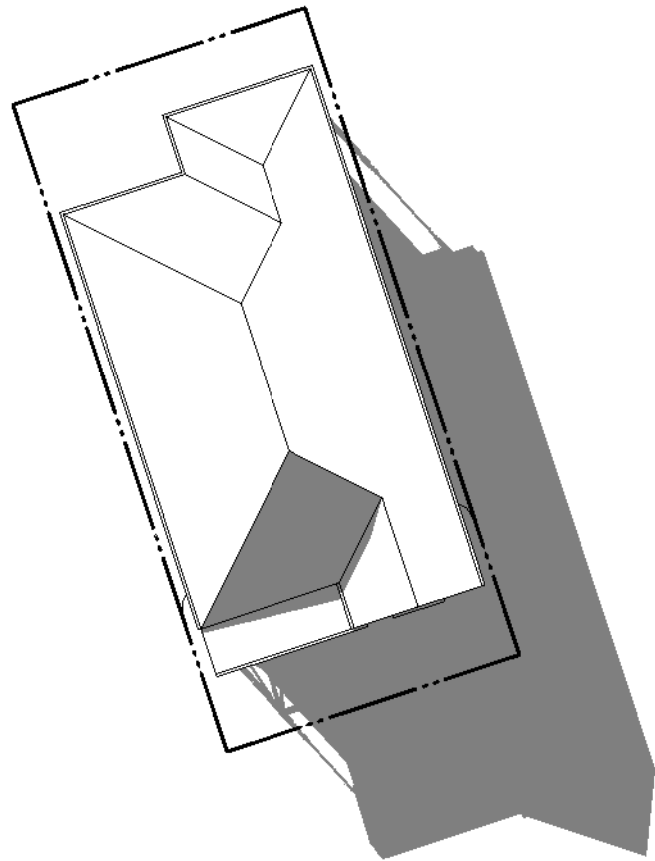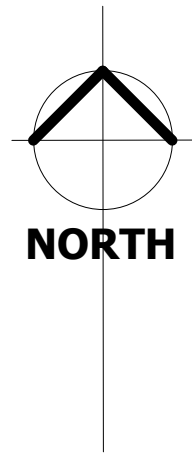

1 SHADOW DIAGRAM 3pm 21 JUNE
1 : 250