

THIS DRAWING IS SUBJECT TO COPYRIGHT LAWS AND
MAY NOT BE COPIED WITHOUT THE WRITTEN PERMISSION
OF THRIVE HOMES PTY LTD-ACN 613 679 333

©

NOTES:

* ALL DIMENSIONS ARE IN MILLIMETERS

* DO NOT SCALE THE DRAWING - USE WRITTEN DIMENSIONS

* IT IS THE RESPONSIBILITY OF THE OWNER TO ENSURE THAT THE LAYOUT AND ALL SPECIAL INCLUSIONS ARE CORRECT

* THRIVE HOMES PTY. LIMITED WILL TAKE NO RESPONSIBILITY FOR ANY VERBAL DISCUSSIONS OR INSTRUCTIONS. ALL CHANGES AND SPECIAL INCLUSIONS MUST BE DOCUMENTED IN WRITING.

* THIS DRAWING IS SUBJECT TO COPYRIGHT LAWS AND MAY NOT BE COPIED WITHOUT THE WRITTEN PERMISSION OF THRIVE HOMES PTY. LIMITED - ACN 613 679 333

SCHEDULE OF DRAWINGS:

SHEET

CONTENTS

01

COVER SHEET

02

SITE PLAN

03

FLOOR PLAN

04

ROOF PLAN

05

ELEVATIONS 1-2

06

ELEVATIONS 3-4

07

SECTIONS & BASIX

08

WET AREA PLANS

09

SLAB SETOUT PLAN

10

SEDIMENT CONTROL PLAN

11

STORMWATER PLAN

D1

SLAB DETAILS 1

D2

SLAB DETAILS 2

D3

WALL OPENINGS DETAILS

D4

TYPICAL EAVES DETAILS

KP

KITCHEN PLAN

KV

KITCHEN VIEWS

AMENDMENTS

ISS	DESCRIPTION	BY	DATE
A	LODGEMENT PLANS	PG (BM)	28.10.25
B	AMENDED LODGEMENT PLANS	PG (BM)	09.02.26
C	AMENDED LODGEMENT PLANS (HYBRID FRAME CONSTRUCTION WITH PODS)	PG (BM)	04.03.26

AMENDED LODGEMENT PLANS - CDC
SIGNATURE: _____

THRIVE HOMES

HYBRID FRAME CONSTRUCTION WITH PODS

NOTES:

PLEASE NOTE: DETAILS SHOWN ON THESE PLANS ARE INTENDED TO BE ACCURATE - HOWEVER INFORMATION WRITTEN INTO INDIVIDUAL CONTRACTS WILL TAKE PRECEDENCE OVER PLANS

* ALL DIMENSIONS ARE IN MILLIMETRES

* DO NOT SCALE - USE WRITTEN DIMENSIONS

* ALL DIMENSIONS ARE TO STRUCTURAL FRAMES ONLY EXCLUDING FINISHED SURFACES

ThriveHomes

LEVEL 7, 5 RIDER BOULEVARD
RHODES NSW 2138
TELEPHONE 02 8758 4800
FAX 02 9300 5646

Builder's licence No. 301349C

CLIENT:

THRIVE HOMES

SITE ADDRESS:

LOT 175 (DP 1304135)
NO. 17 KEIGHTLEY AVENUE
WINDRADYNE, NSW 2795

HOUSE TYPE:

ALLIRA 25

FACADE:

VOGUE

TYPE:

DOUBLE GARAGE

SPECIFICATION:

STANDARD

DRAWING TITLE:

COVER SHEET

DRAWN BY:

DH

COUNCIL AREA:

BATHURST

JOB No:

T001732

SCALE:

DATE DRAWN:

04.03.26

DRWG No:

01

ISSUE:

C

LEGEND

-  HOT WATER TANK
-  WATER NETTER
-  TELECOM PIT
-  MANHOLE (SEWER/STORMWATER)
-  SEWER TERMINAL MAINTENANCE SHAFT
-  SEWER MAINTENANCE SHAFT
-  VEHICLE CROSSING
-  KERB INLET PIT
-  LIGHT POLE
-  ELECTRICITY POLE
-  ELECTRICITY PILLAR
-  HYDRANT
-  STOP VALVE
-  KERB OUTLET
-  SERVICE CONDUIT
-  TREE (DIA/HEIGHT)
-  GARDEN BED
-  SHRUB
-  DENOTES TELEPHONE BOOTH

****B.A.S****
(BUILDING ADJACENT TO SEWER)
ORDER SEWER PEGOUT

SITE CALCULATIONS CDC (EXCLUDING EXTERNAL WALLS & VOIDS)		
GROUND FLOOR	171.17	m ²
GARAGE AREA	20.25	m ²
TOTAL GROSS FLOOR AREA (EXCLUDING GARAGE CONCESSION)	173.42	m ²
SITE AREA	637.50	m ²
BUILDING FOOTPRINT (INCLUDING UNENCLOSED AREA)	234.78	m ²
DRIVEWAY & PATH	34.52	m ²
CROSSOVER	16.96	m ²
TOTAL FRONT AREA	83.64	m ²
FRONT LANDSCAPE AREA	58.73	%
TOTAL LANDSCAPE AREA	368.20	m ²
LANDSCAPE AREA (%)	57.76	%

SEPP 2017 REQUIREMENTS INLAND CDC		
SITE AREA	637.50	m ²
MAXIMUM GROSS FLOOR AREA	335.00	m ²
MINIMUM LANDSCAPED AREA	191.25	m ²
- GROSS FLOOR AREA MEANS THE SUM OF THE FLOOR AREA OF EACH FLOOR OF A BUILDING MEASURED FROM THE INTERNAL FACE OF EXTERNAL WALLS		
- LANDSCAPED AREA MUST HAVE A MINIMUM WIDTH AND LENGTH OF 1.5M		



NOTES:

PLEASE NOTE: DETAILS SHOWN ON THESE PLANS ARE INTENDED TO BE ACCURATE - HOWEVER INFORMATION WRITTEN INTO INDIVIDUAL CONTRACTS WILL TAKE PRECEDENCE OVER PLANS

- * ALL DIMENSIONS ARE IN MILLIMETRES
- * DO NOT SCALE - USE WRITTEN DIMENSIONS
- * ALL DIMENSIONS ARE TO STRUCTURAL FRAMES ONLY EXCLUDING FINISHED SURFACES

ThriveHomes
LEVEL 7, 5 RIDER BOULEVARD
RHODES NSW 2138
TELEPHONE 02 8758 4800
FAX 02 9300 5646

Builder's licence No. 301349C

CLIENT:
THRIVE HOMES

SITE ADDRESS:
**LOT 175 (DP 1304135)
NO. 17 KEIGHTLEY AVENUE
WINDRADYNE, NSW 2795**

- CDC TREE PLANTING REQUIREMENT:**
A) CLIENT TO PLANT TREE TO FRONT YARD THAT WILL REACH A HEIGHT OF 5M AT MATURITY
B) CLIENT TO PLANT TREE TO REAR YARD THAT WILL REAR A HEIGHT OF 8M AT MATURITY
- 960mm FALL ACROSS BUILDING ENVELOPE**
- GARAGE INTERNAL DIMENSION
5500mm (W) x 5500mm (D)

THIS DRAWING IS SUBJECT TO COPYRIGHT LAWS AND MAY NOT BE COPIED WITHOUT THE WRITTEN PERMISSION OF THRIVE HOMES PTY LTD-ACN 613 679 333



SITE NOTES:

BEFORE STARTING WORK ON SITE CHECK FOLLOWING:

- SERVICE LOCATIONS
- SEWER CONNECTION POSITION
- DRIVEWAY ALIGNMENT & LEVELS

N2 WIND CATEGORY

DP ○ INDICATES DOWNPIPE LOCATION

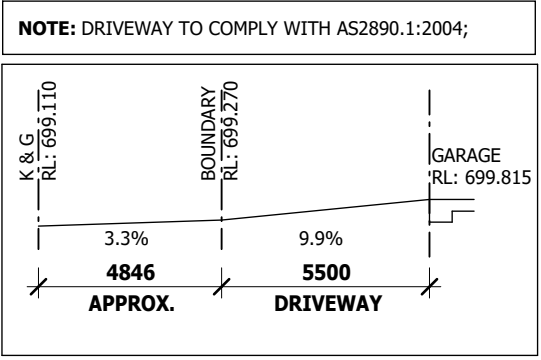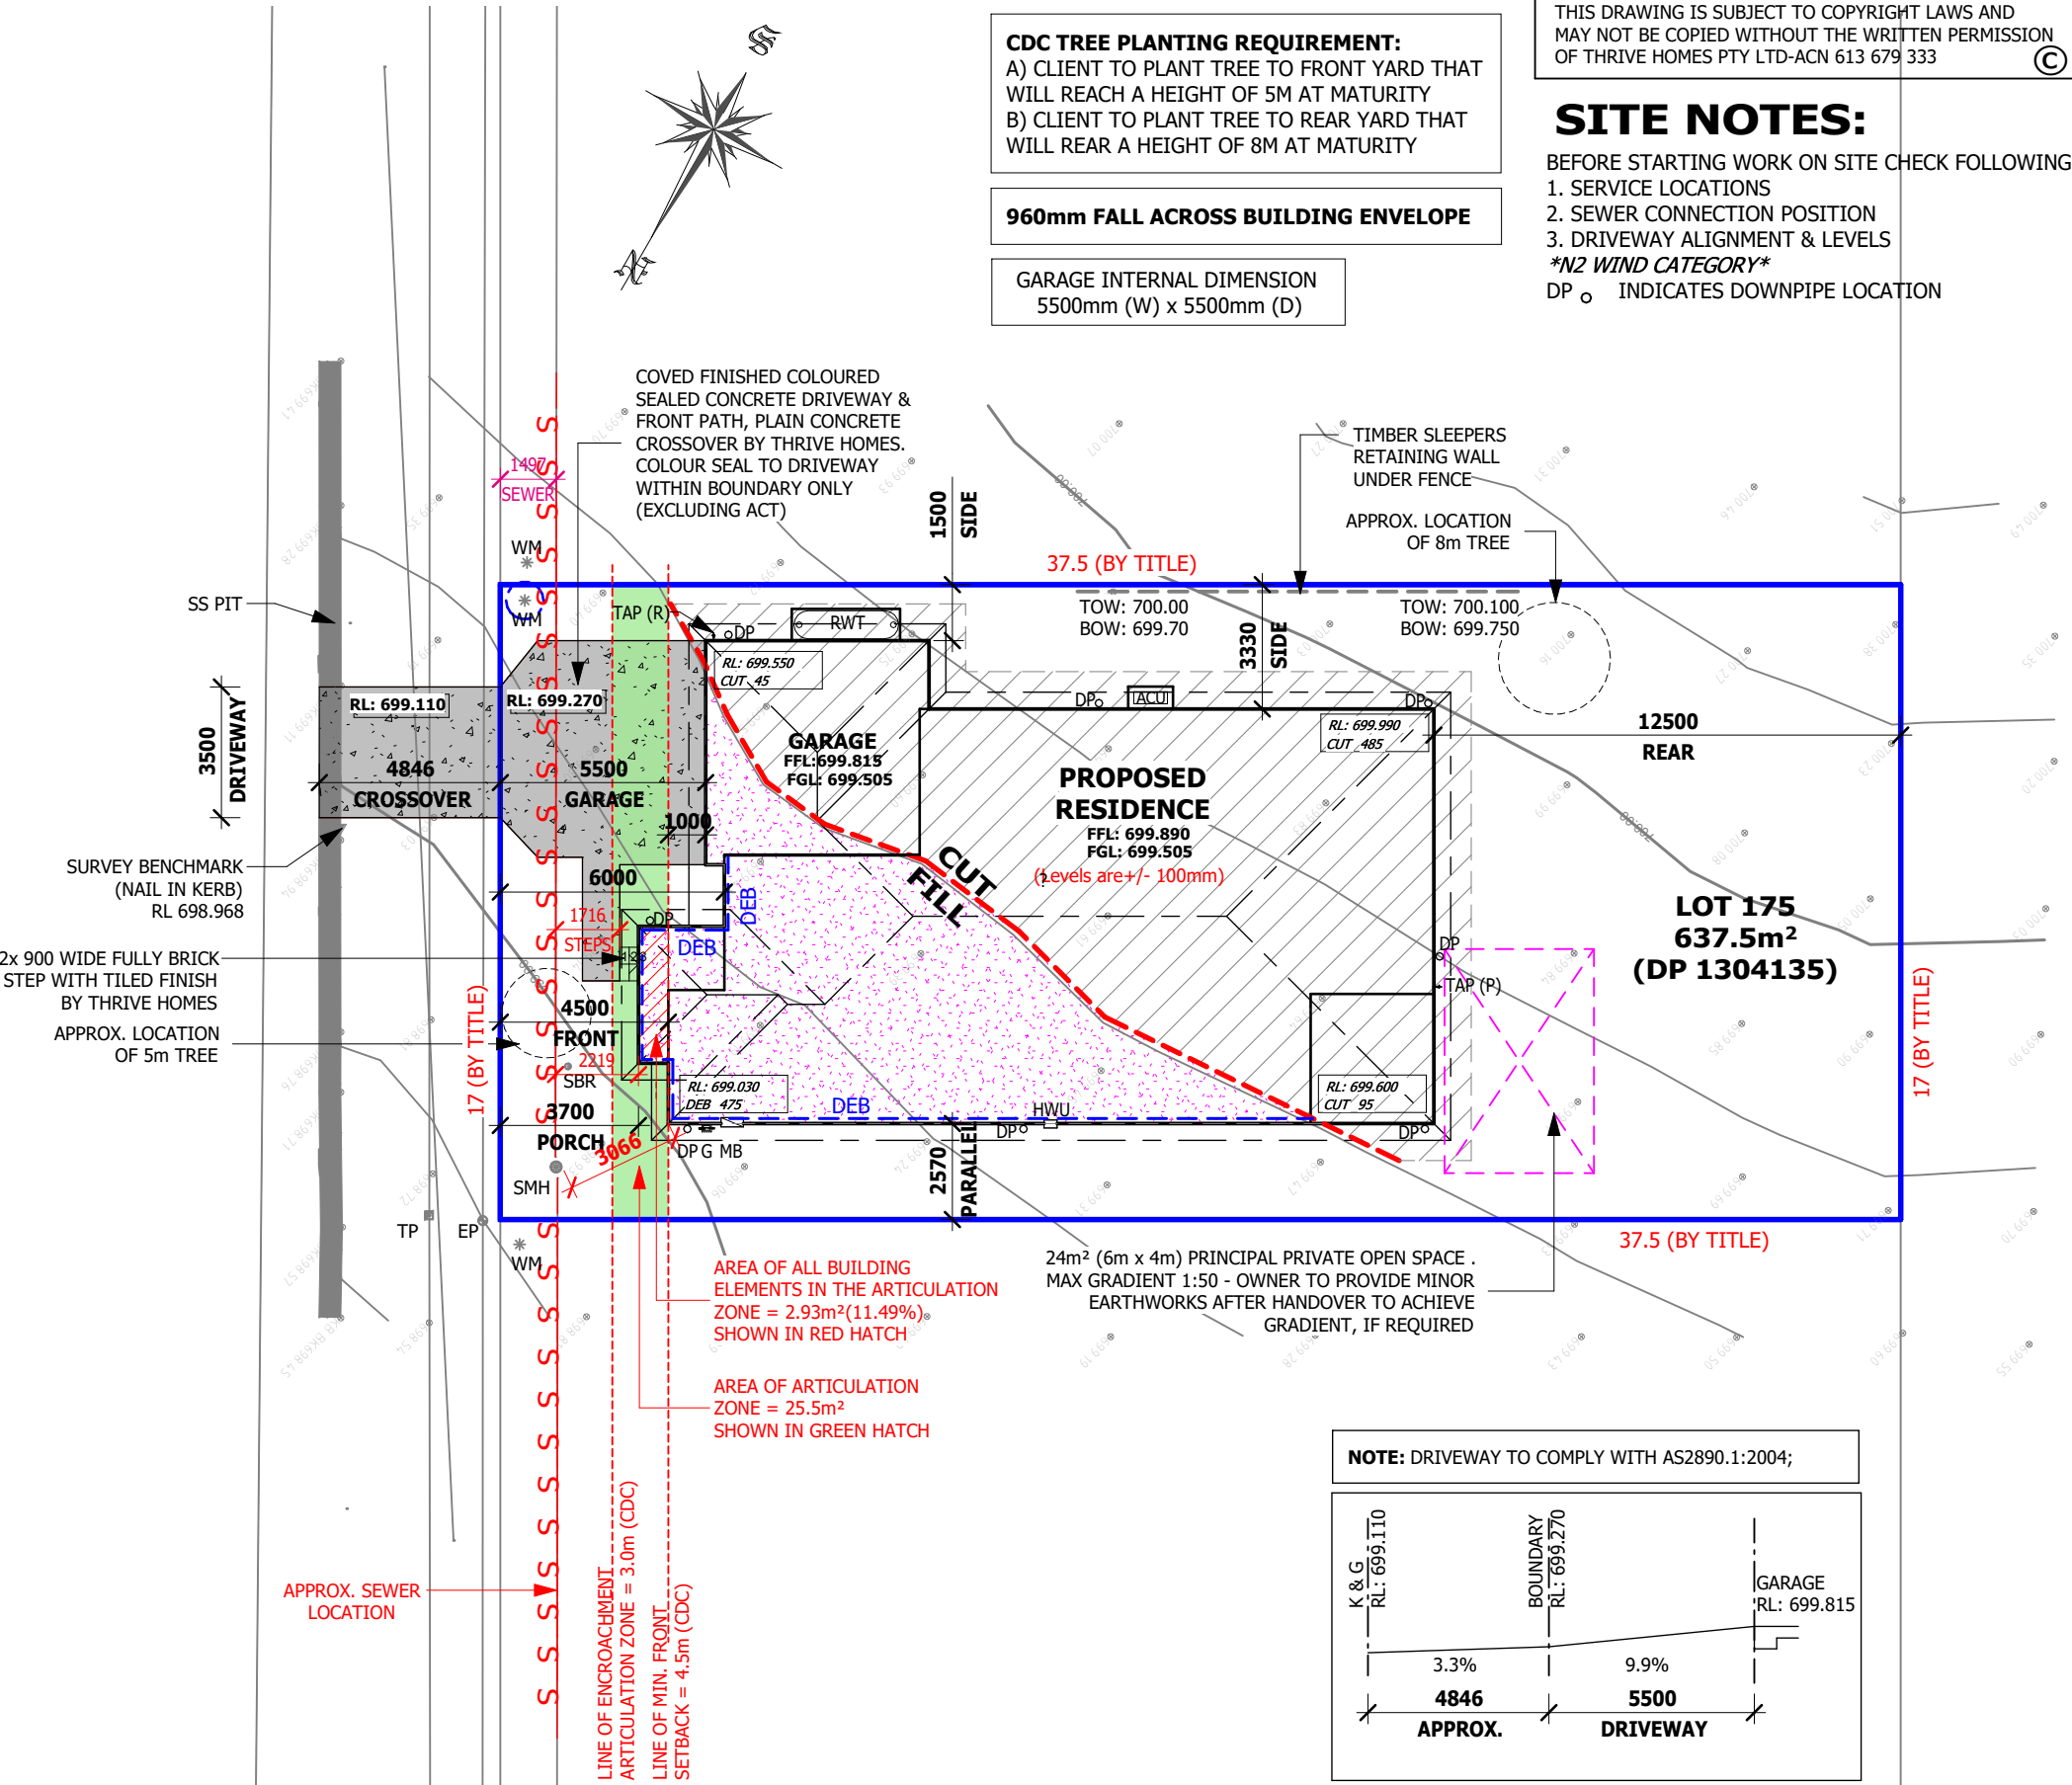


NOTES:

- ALL EXTERNAL DOORS TO BE FITTED WITH DRAFT EXCLUSION DEVICE
- WC DOORS TO BE FITTED WITH LIFT-OFF HINGES
- WINDOW OPENING SIZES TO BE CHECKED BEFORE FRAMES ARE CONSTRUCTED
- TIMBER TRUSSES TO SATISFY AS 1684 SAA TIMBER FRAMING CODE
- STEEL FRAMES TO SATISFY AS / NZS 4600
- ROOF SPACE TO BE VENTILATED BY EAVE VENTS
- 2040mm DOOR HEIGHTS THROUGHOUT INCLUDING ROBES AND LINEN.
- 2150mm HIGHT SQ.SET OPENINGS.

PROVIDE NATHERS COMPLIANT GLAZING TO ALL WINDOWS & EXTERNAL SLIDING DOOR


ALUMINIUM WINDOWS AND SLIDING DOORS IN MANUFACTURER'S STANDARD COLOUR RANGE, INCLUDING SECURITY-KEYED WINDOWS AND DOOR LOCKS WITH OBSCURE GLASS TO BATHROOMS, ENSUITE AND POWDER ROOM

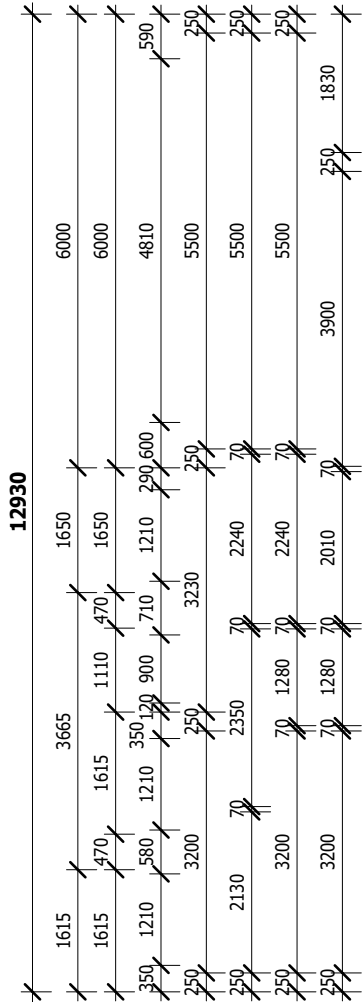

NOTE: LOCATION OF GAS AND ELECTRICAL METERS TO BE DETERMINED BY CONTRACTOR ON SITE TO NEAREST POINT OF CONNECTION

DWELLING TO BE BUILT IN ACCORDANCE WITH NCC 2022:

- SMOKE ALARMS TO PART 9.5.1 OF THE BCA
- MECHANICAL VENTILATION TO PART 10.6.2 (C) & 10.8.2 OF THE BCA TO ALL WET AREAS
- WATERPROOFING TO COMPLY WITH PART 10.2 OF THE BCA
- GLAZING TO BE IN ACCORDANCE WITH PART 8.2 OF THE BCA
- CONDENSATION MANAGEMENT TO COMPLY WITH PART 10.8 OF THE BCA

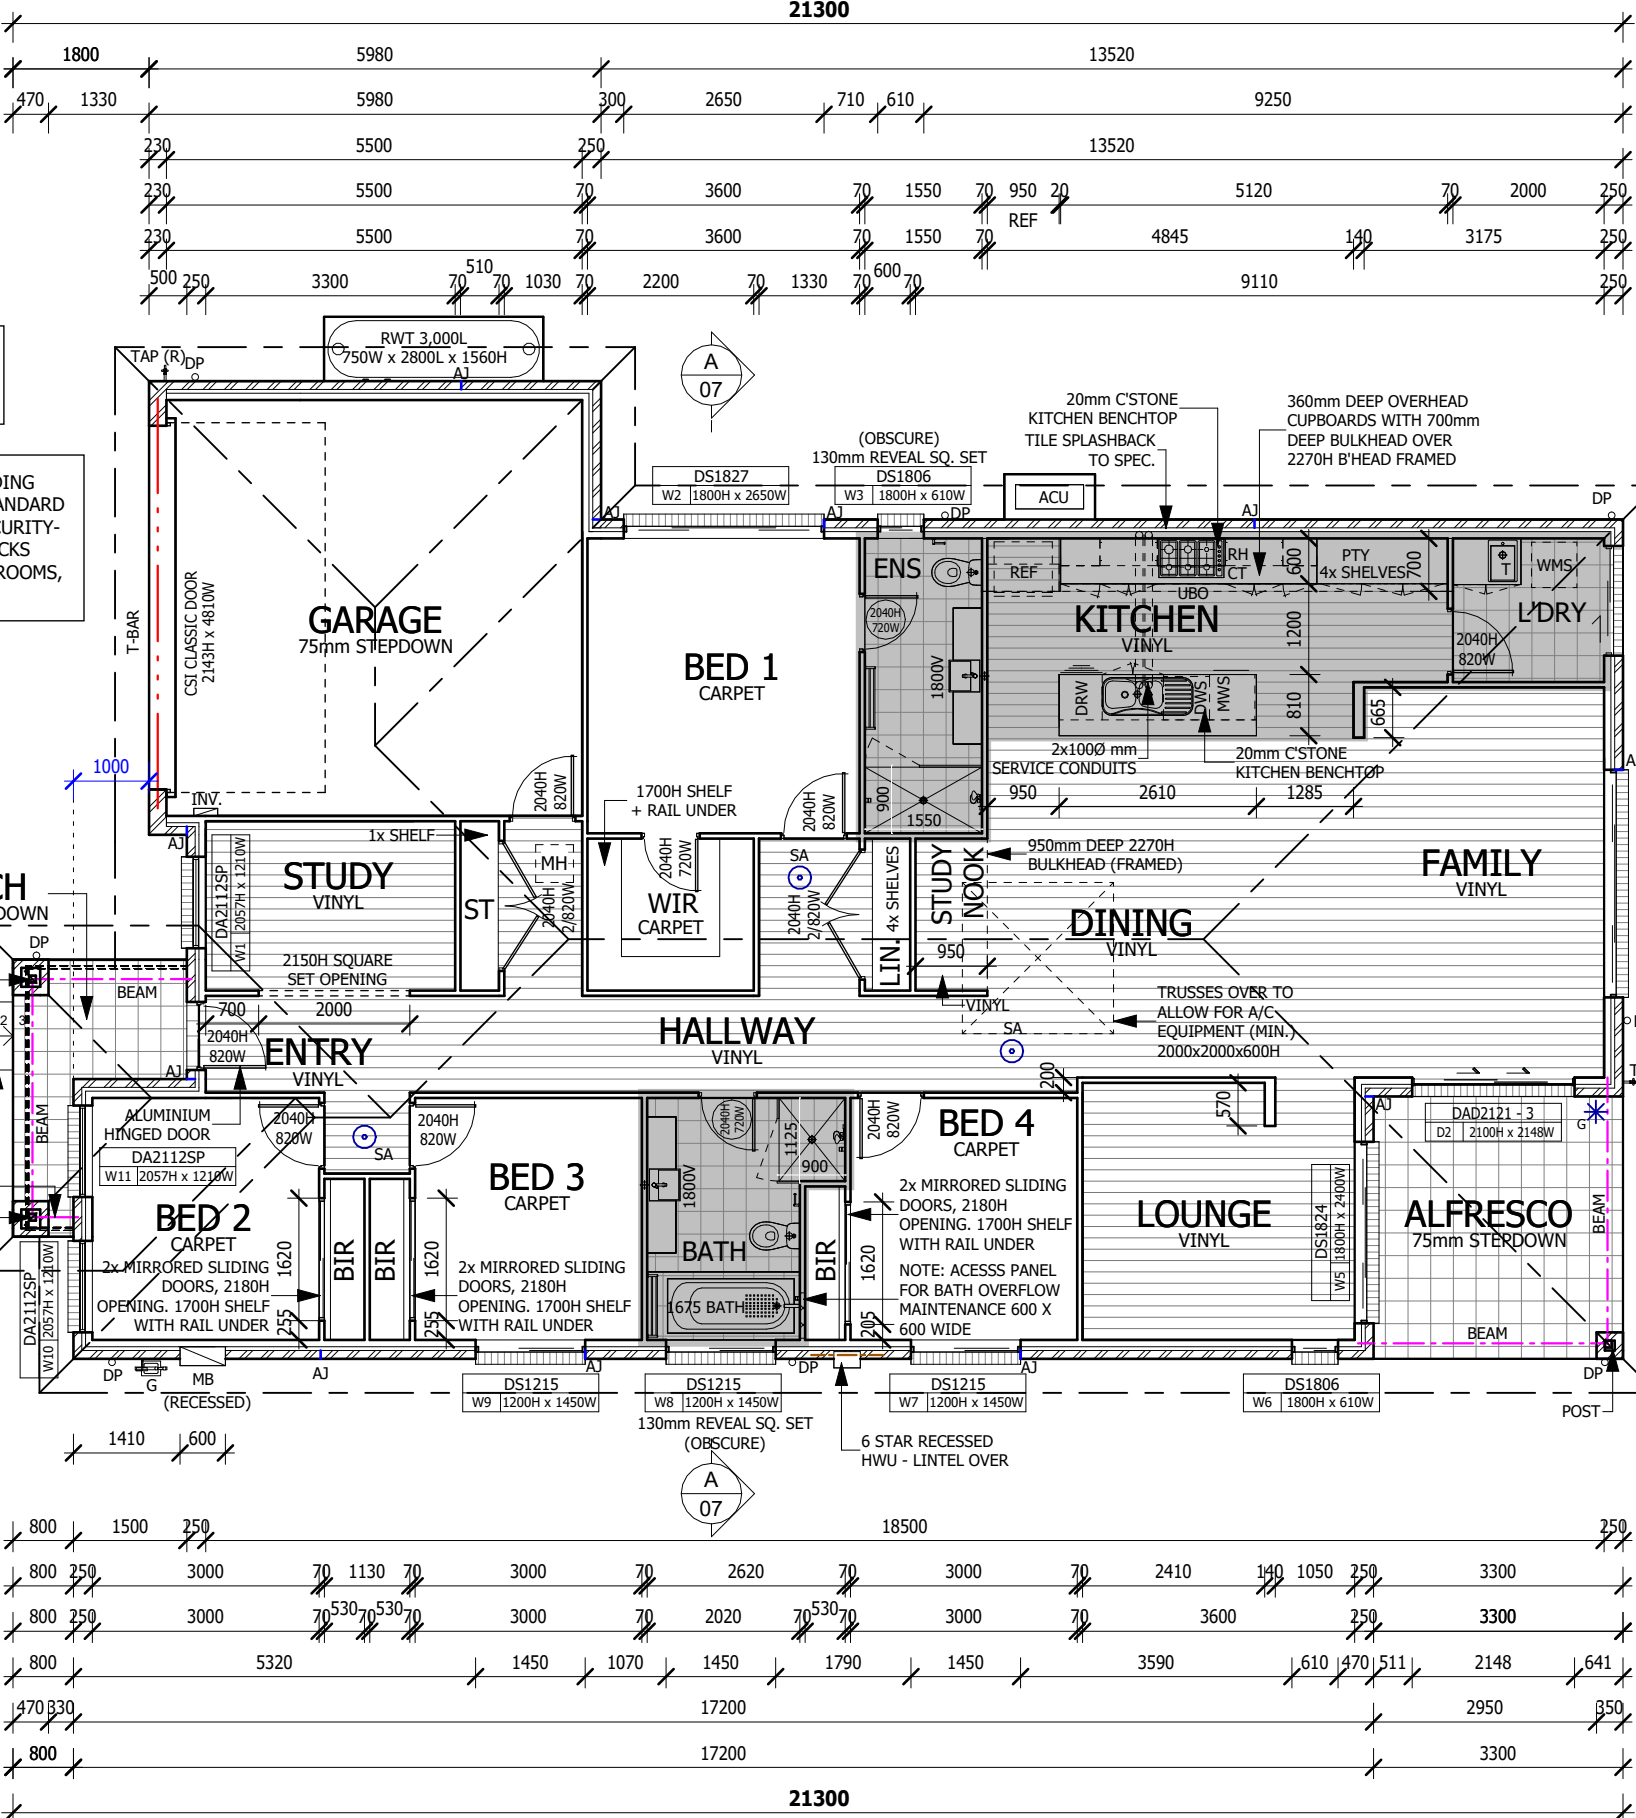

THIS DRAWING IS SUBJECT TO COPYRIGHT LAWS AND MAY NOT BE COPIED WITHOUT THE WRITTEN PERMISSION OF THRIVE HOMES PTY LTD-ACN 613 679 333


LEGEND:

70mm STEPDOWN TO WET AREAS

AC NOTE:

POSITIONS OF OUTLETS, RETURN AIR AND NUMBER OF DROPPERS IS DETERMINED AIR CONDITIONING CONTRACTOR.

ROOF AREA: 290.25 m²

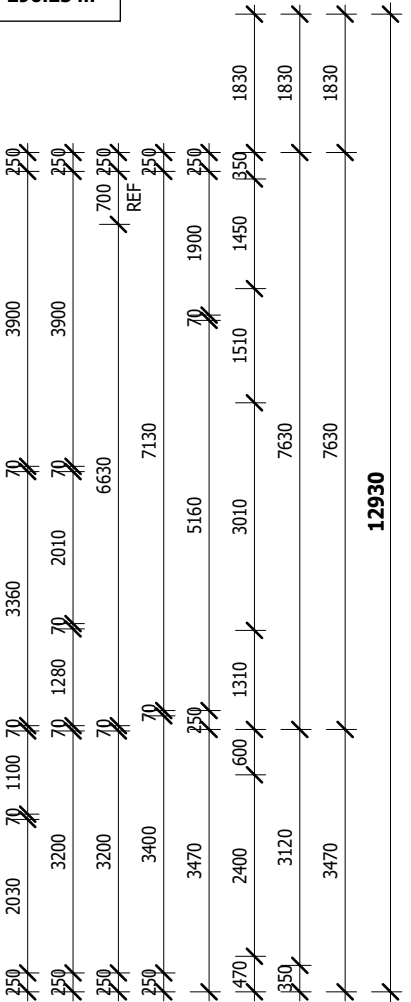

FLOOR AREAS

GROUND FLOOR	184.50 m²
GARAGE	33.53 m²
ALFRESCO	11.45 m²
PORCH	5.30 m²
TOTAL	234.78 m²

NOTES:

PLEASE NOTE: DETAILS SHOWN ON THESE PLANS ARE INTENDED TO BE ACCURATE - HOWEVER INFORMATION WRITTEN INTO INDIVIDUAL CONTRACTS WILL TAKE PRECEDENCE OVER PLANS


- ALL DIMENSIONS ARE IN MILLIMETRES
- DO NOT SCALE - USE WRITTEN DIMENSIONS
- ALL DIMENSIONS ARE TO STRUCTURAL FRAMES ONLY EXCLUDING FINISHED SURFACES

ThriveHomes
LEVEL 7, 5 RIDER BOULEVARD
RHODES NSW 2138
TELEPHONE 02 8758 4800
FAX 02 9300 5646
Builder's licence No. 301349C

CLIENT:
THRIVE HOMES
SITE ADDRESS:
LOT 175 (DP 1304135)
NO. 17 KEIGHTLEY AVENUE
WINDRADYNE, NSW 2795

HOUSE TYPE: ALLIRA 25
FACADE: VOGUE
TYPE: DOUBLE GARAGE
SPECIFICATION: STANDARD
DRAWING TITLE:
FLOOR PLAN

DRAWN BY: DH
DATE DRAWN: 04.03.26
SCALE: 1 : 100
COUNCIL AREA: BATHURST
JOB No: T001732
DRWG No: 03
ISSUE: C

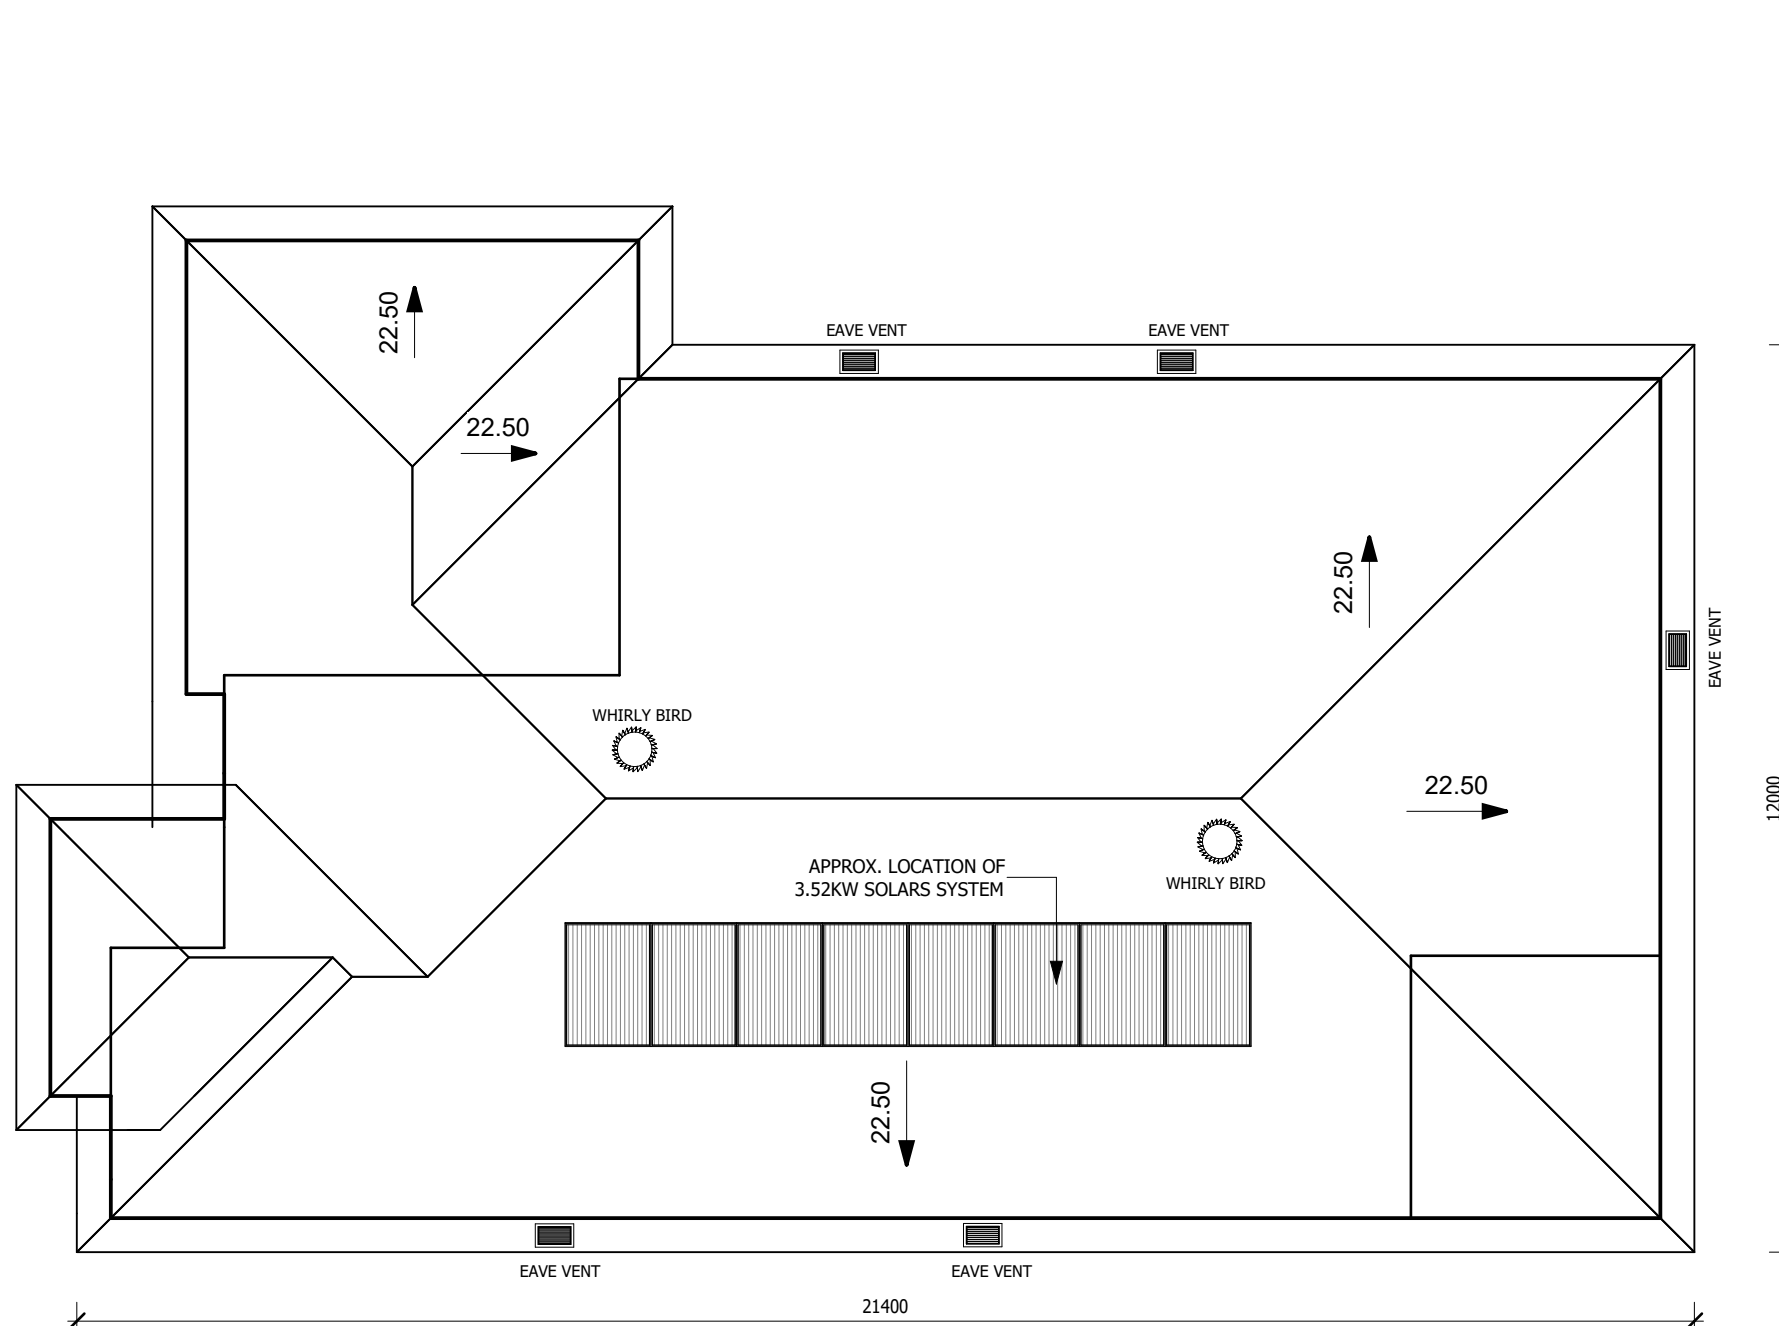

CONDENSATION CALCULATIONS				
*Whirlybirds must be placed not more 900mm below the ridge height or highest point of the roof space.				
	ROOF PITCH	ROOF LENGTH	WHIRLY BIRDS	EAVE VENTS
ROOF	22.5° PITCH	21.4(m)	2	5

NOTES:

PLEASE NOTE: DETAILS SHOWN ON THESE PLANS ARE INTENDED TO BE ACCURATE - HOWEVER INFORMATION WRITTEN INTO INDIVIDUAL CONTRACTS WILL TAKE PRECEDENCE OVER PLANS

- * ALL DIMENSIONS ARE IN MILLIMETRES
- * DO NOT SCALE - USE WRITTEN DIMENSIONS
- * ALL DIMENSIONS ARE TO STRUCTURAL FRAMES ONLY EXCLUDING FINISHED SURFACES

ThriveHomes
LEVEL 7, 5 RIDER BOULEVARD
RHODES NSW 2138
TELEPHONE 02 8758 4800
FAX 02 9300 5646

Builder's licence No. 301349C

CLIENT:
THRIVE HOMES

SITE ADDRESS:
LOT 175 (DP 1304135)
NO. 17 KEIGHTLEY AVENUE
WINDRADYNE, NSW 2795

HOUSE TYPE: ALLIRA 25
FACADE: VOGUE
TYPE: DOUBLE GARAGE
SPECIFICATION: STANDARD

DRAWING TITLE:
ROOF PLAN

DRAWN BY:
DH

DATE DRAWN:
04.03.26

SCALE:
1 : 100

COUNCIL AREA:
BATHURST

DRWG No:
04

JOB No:
T001732

ISSUE:
C

©

7

7

3

RS)

1



PLEASE NOTE: DETAILS SHOWN ON THESE PLANS ARE INTENDED TO BE ACCURATE - HOWEVER INFORMATION WRITTEN INTO INDIVIDUAL CONTRACTS WILL TAKE PRECEDENCE OVER PLANS

- * ALL DIMENSIONS ARE IN MILLIMETRES
- * DO NOT SCALE - USE WRITTEN DIMENSIONS
- * ALL DIMENSIONS ARE TO STRUCTURAL FRAMES ONLY EXCLUDING FINISHED SURFACES


ThriveHomes
LEVEL 7, 5 RIDER BOULEVARD
RHODES NSW 2138
TELEPHONE 02 8758 4800
FAX 02 9300 5646

Builder's licence No. 301349C


SITE ADDRESS:
LOT 175 (DP 1304135)
NO. 17 KEIGHTLEY AVENUE
WINDRADYNE, NSW 2795

HOUSE TYPE:	ALLIRA 25
FACADE:	VOGUE
TYPE:	DOUBLE GARAGE
SPECIFICATION:	STANDARD
DRAWING TITLE:	ELEVATIONS 1-2

DRAWN BY: DH	DATE DRAWN: 04.03.26	SCALE: 1 : 100
COUNCIL AREA: BATHURST		DRWG No: 05
JOB No: T001732		ISSUE: C

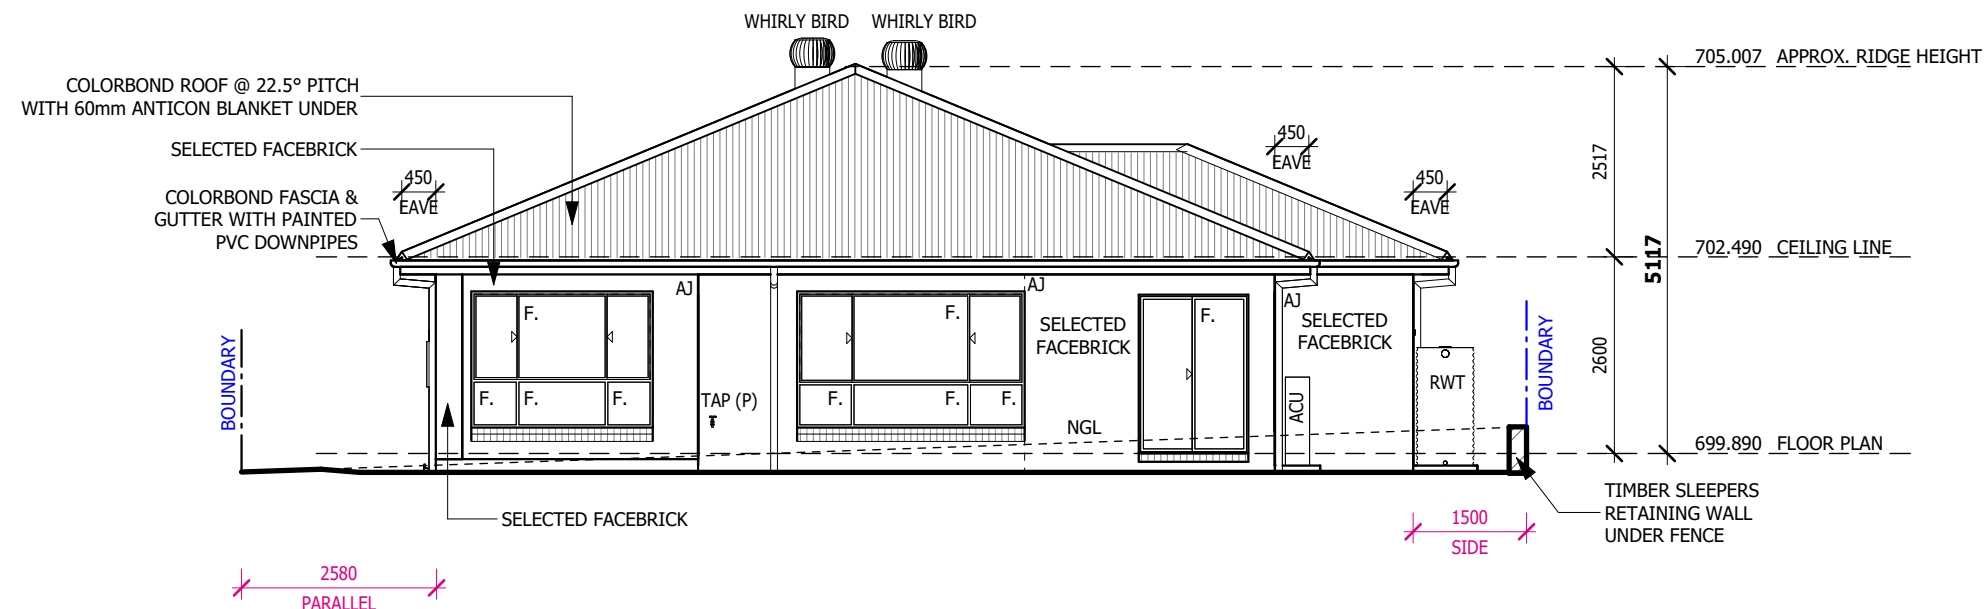

ELEVATION 3

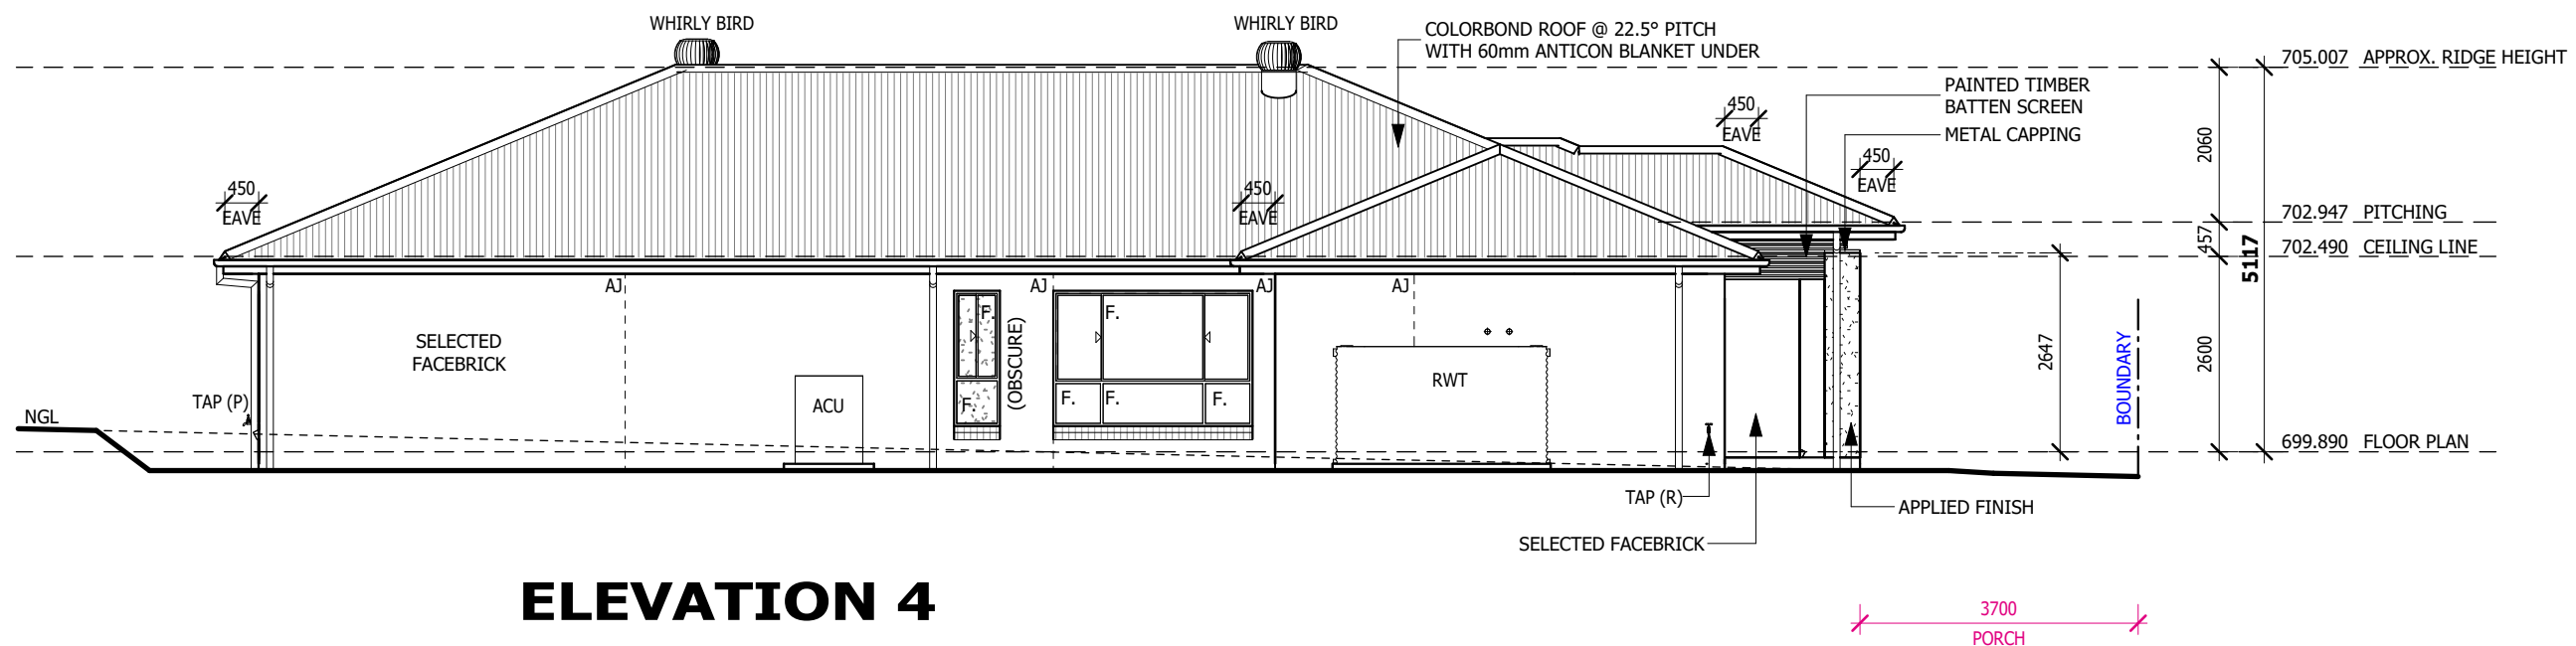

ELEVATION 4

- THIS DRAWING IS SUBJECT TO COPYRIGHT LAWS AND MAY NOT BE COPIED WITHOUT THE WRITTEN PERMISSION OF THRIVE HOMES PTY LTD-ACN 613 679 333 ©
- WINDOW HEAD HEIGHTS TO BE 2143H FROM FFL UNLESS STATED OTHERWISE.
- CEILING HEIGHT NOMINAL TO FRAME HEIGHT, SUBJECT TO SELECTED FLOOR FINISH.
- ARTICULATION JOINT REQUIRES ADDITIONAL STUD FOR BRICK TIES.
- NYLON MESH FLYSCREENS TO ALL OPENING WINDOWS, SLIDING AND STACKER DOORS (EXCLUDING HINGED DOORS)
- CSR WALL WRAP TO EXTERNAL WALLS

NOTES:

PLEASE NOTE: DETAILS SHOWN ON THESE PLANS ARE INTENDED TO BE ACCURATE - HOWEVER INFORMATION WRITTEN INTO INDIVIDUAL CONTRACTS WILL TAKE PRECEDENCE OVER PLANS

- * ALL DIMENSIONS ARE IN MILLIMETRES
- * DO NOT SCALE - USE WRITTEN DIMENSIONS
- * ALL DIMENSIONS ARE TO STRUCTURAL FRAMES ONLY EXCLUDING FINISHED SURFACES

ThriveHomes
LEVEL 7, 5 RIDER BOULEVARD
RHODES NSW 2138
TELEPHONE 02 8758 4800
FAX 02 9300 5646
Builder's licence No. 301349C

CLIENT:
THRIVE HOMES


SITE ADDRESS:
LOT 175 (DP 1304135)
NO. 17 KEIGHTLEY AVENUE
WINDRADYNE, NSW 2795

HOUSE TYPE: ALLIRA 25
FACADE: VOGUE
TYPE: DOUBLE GARAGE
SPECIFICATION: STANDARD
DRAWING TITLE:
ELEVATIONS 3-4



DRAWN BY: DH	DATE DRAWN: 04.03.26	SCALE: 1 : 100
COUNCIL AREA: BATHURST		DRWG No: 06
JOB No: T001732		ISSUE: C

©

SECTION A-A

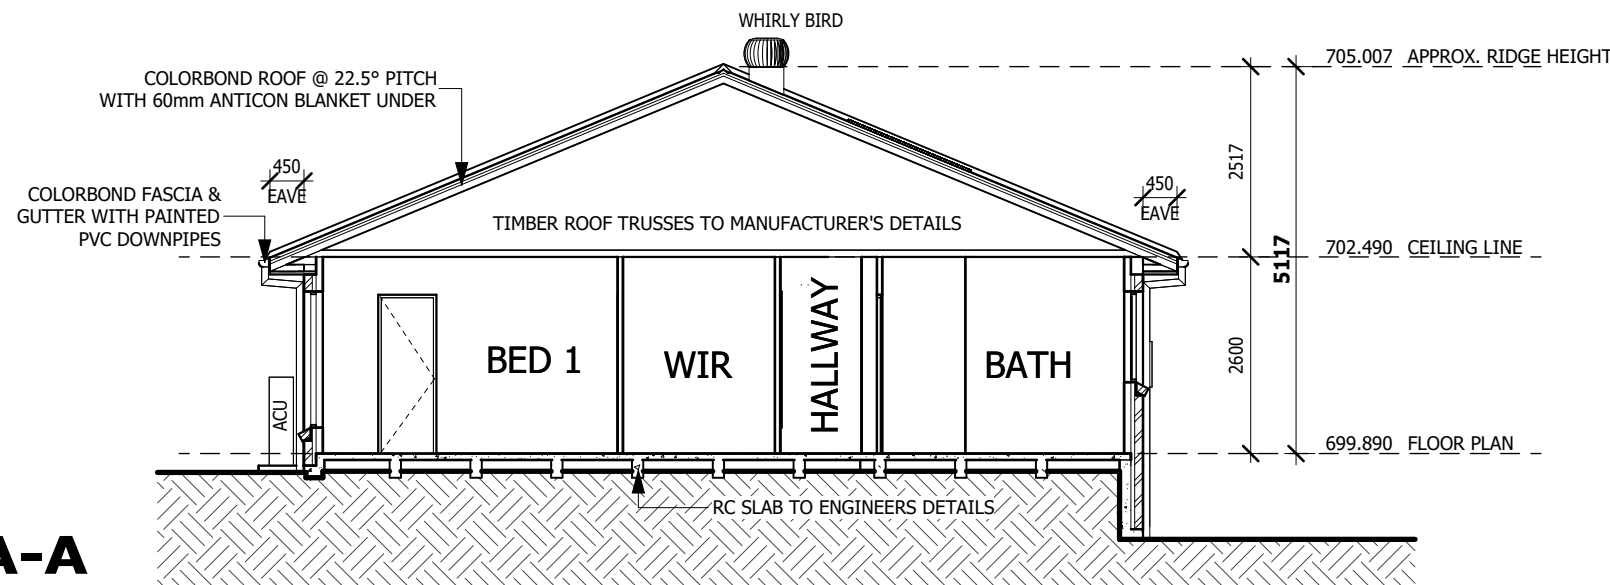

- INSULATION NOTE:**
- R6.0 THERMAL BATTS WITH R3.0 TO ROOF PERIMETER WHERE R6.0 WILL NOT FIT (EXCLUDING CEILINGS OVER GARAGE, PORCH & ALFRESCO)
 - R2.5 INSULATION TO EXTERNAL WALLS & R2.2 TO WALLS BETWEEN GARAGE AND HOUSE (EXCLUDING GARAGE EXTERNAL WALLS)
 - WALL WRAP TO EXTERNAL WALL THROUGHOUT

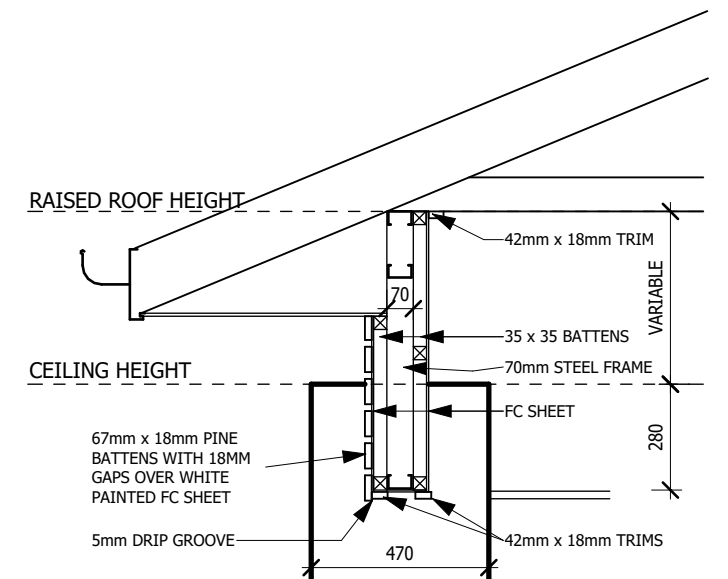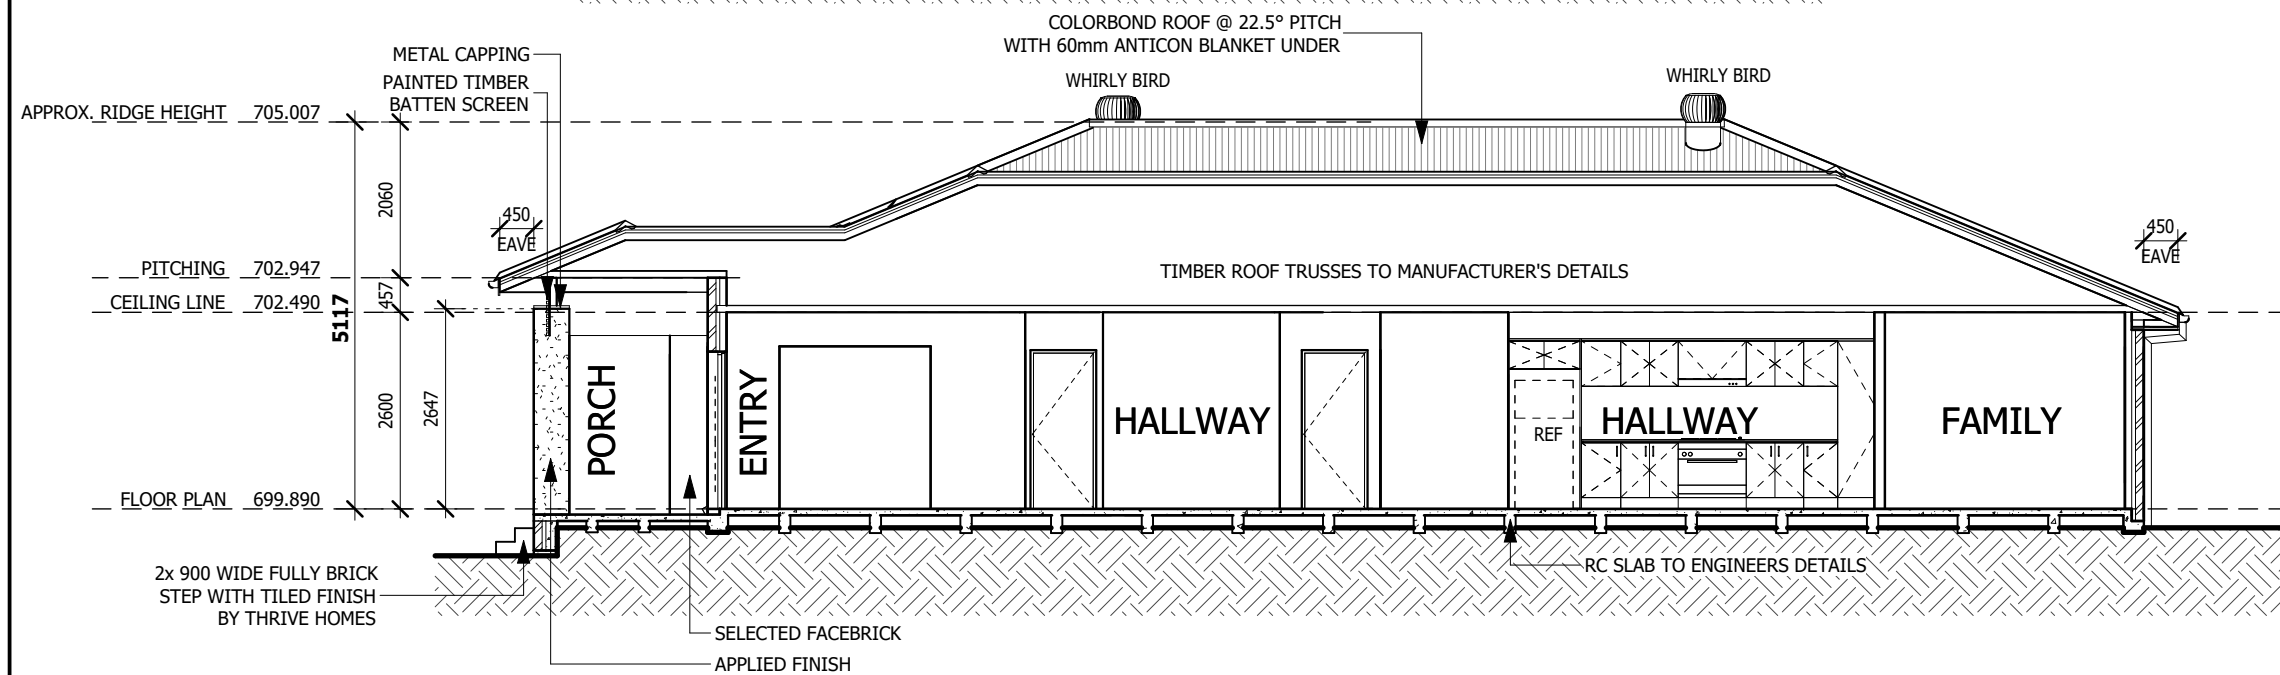

SECTION B-B

BASIX COMMITMENTS

PROJECT DETAILS			STORMWATER	ENERGY	NATURAL LIGHTING
Site area	638	m²	Rainwater tank to collect at least 174.0 m² of rain run off from roof area	ACTIVE COOLING/HEATING 1-phase	Applicant must provide a window for natural lighting to 2 bathrooms/toilets
Roof area	290.0	m²	Rainwater tank to be connected to all toilets with in the development	Cooling system with day/night zoning for bedrooms & living areas with an EER 3.0 STAR	
Number of bedrooms	4		Rainwater tank to be connected to cold water tap to supply water to the washing machine	Heating system with day/night zoning for bedrooms & living areas with an EER 3.5 STAR	
Total area of vegetation (garden & lawn)	369	m²	Rainwater to be connected to at least one outdoor tap for garden watering		COOKING (KITCHEN APPLIANCES)
ABSA Certificate Number (if applicable)	#HR-N7D9JM-02		Rainwater to have a capacity of at least 3000LTR		Install a gas cooktop and electric oven
Net conditioned floor area	160.7	m²		VENTILATION	
Net Unconditioned floor area	11.7	m²	WATER	At least 1 Bathroom: individual fan, ducted to façade or roof; Operation: please select	DESIGN ENHANCEMENT
Concession claimed (if applicable)	N/A		All showers with in the development are to have a minimum rating of 4 star showerheads	Kitchen: individual fan, ducted to façade or roof: manual switch on/off	Install a fixed outdoor clothes drying line
Cooling load (if applicable)	8	MJ/m²/pa	Each toilet is to have a flushing system of no less than a 4 star rating	Laundry: individual fan, ducted to façade or roof: manual switch on/off	
Heating load (if applicable)	146	MJ/m²/pa	All basin taps to have a minimum rating of 4 star rating	ARTIFICIAL LIGHTING	
			All taps in the kitchen are to have a minimum rating of 4 star	The applicant must ensure that a minimum of 80% of light fixtures are fitted with	
			HOT WATER	fluorescent, compact fluorescent, or light-emitting-diode (LED) lamps.	INSULATION
			Gas instantaneous hot water system with a performance of 6 stars		External wall [excluding garage]: R2.5
					Ceiling [excluding garage & alfresco]: R6.0

NOTES:

PLEASE NOTE: DETAILS SHOWN ON THESE PLANS ARE INTENDED TO BE ACCURATE - HOWEVER INFORMATION WRITTEN INTO INDIVIDUAL CONTRACTS WILL TAKE PRECEDENCE OVER PLANS

- * ALL DIMENSIONS ARE IN MILLIMETRES
- * DO NOT SCALE - USE WRITTEN DIMENSIONS
- * ALL DIMENSIONS ARE TO STRUCTURAL FRAMES ONLY EXCLUDING FINISHED SURFACES

ThriveHomes
LEVEL 7, 5 RIDER BOULEVARD
RHODES NSW 2138
TELEPHONE 02 8758 4800
FAX 02 9300 5646

Builder's licence No. 301349C

CLIENT:
THRIVE HOMES

SITE ADDRESS:
LOT 175 (DP 1304135)
NO. 17 KEIGHTLEY AVENUE
WINDRADYNE, NSW 2795

HOUSE TYPE:	ALLIRA 25
FACADE:	VOGUE
TYPE:	DOUBLE GARAGE
SPECIFICATION:	STANDARD

DRAWING TITLE:
SECTIONS & BASIX

DRAWN BY:	DH
-----------	----

DATE DRAWN:	04.03.26
-------------	----------

SCALE:
As indicated

COUNCIL AREA:
BATHURST

DRWG No: 07

JOB No:
T001732

ISSUE: C

LAUNDRY / WC


- PROVIDE SKIRTING TILE TO PERIMETER WALLS OF LAUNDRY & WC
- LAUNDRY SPLASH BACK - FOUR TILE HEIGHT OVER LAUNDRY TUB
- WM TAPS UNDER TUB

BATHROOM / ENSUITE


- PROVIDE FULL HEIGHT TILING TO MAIN BATH & BED-1 ENS.
- SEMI-FRAMELESS SHOWER SCREEN WITH PIVOT DOOR @ 2000 HIGH.
- APPROXIMATELY 900mm HIGH DIRECT FIX MIRROR TO WIDTH OF VANITY
- FULL HEIGHT VANITIES WITH KICKBOARD
- WALL MOUNTED TAPS & SPOUT TO BATH
- 70mm STEPDOWN TO WET AREAS
- BASIN MOUNTED TAPS TO VANITIES.
- 20mm C'STONE BENCHTOP TO VANITIES.

LEGEND:


70mm STEPDOWN TO WET AREAS

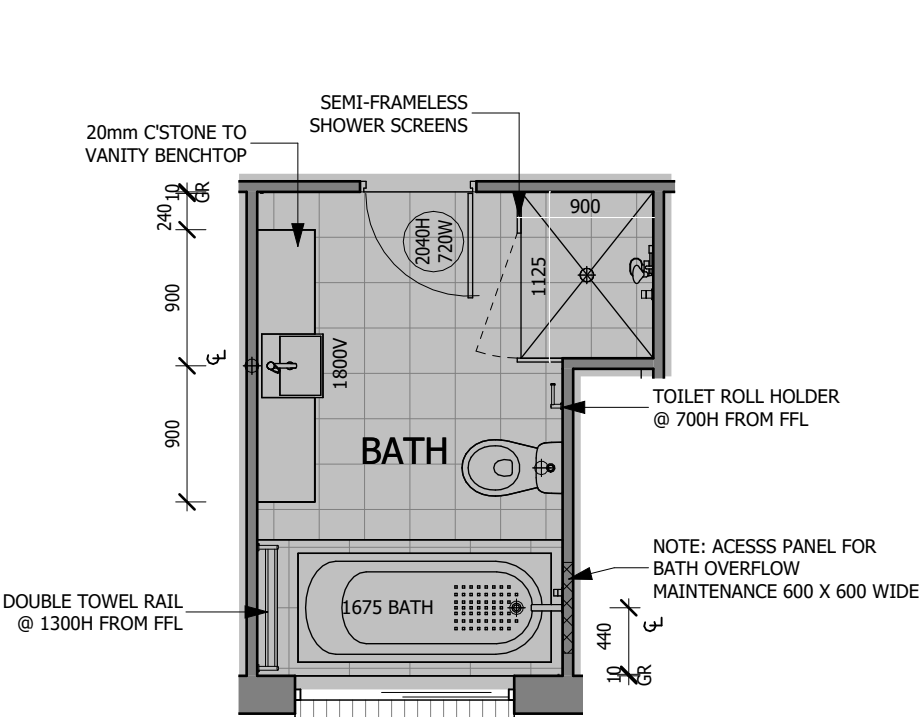

MAIN BATH

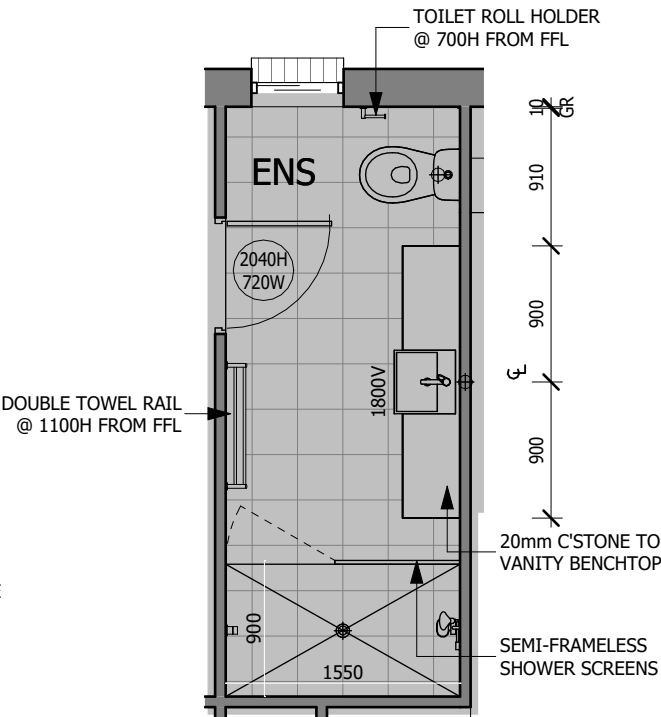

BED 1 ENSUITE

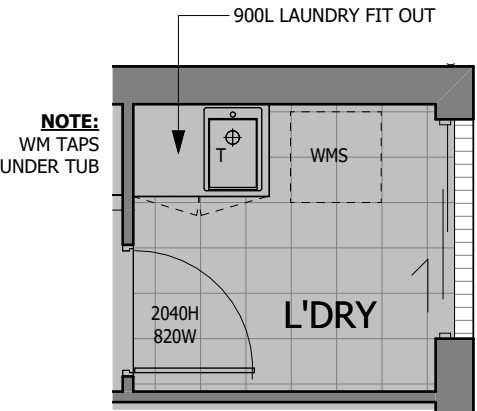

L'DRY

NOTES:

PLEASE NOTE: DETAILS SHOWN ON THESE PLANS ARE INTENDED TO BE ACCURATE - HOWEVER INFORMATION WRITTEN INTO INDIVIDUAL CONTRACTS WILL TAKE PRECEDENCE OVER PLANS

- * ALL DIMENSIONS ARE IN MILLIMETRES
- * DO NOT SCALE - USE WRITTEN DIMENSIONS
- * ALL DIMENSIONS ARE TO STRUCTURAL FRAMES ONLY EXCLUDING FINISHED SURFACES

ThriveHomes
LEVEL 7, 5 RIDER BOULEVARD
RHODES NSW 2138
TELEPHONE 02 8758 4800
FAX 02 9300 5646
Builder's licence No. 301349C

CLIENT:
THRIVE HOMES

SITE ADDRESS:
LOT 175 (DP 1304135)
NO. 17 KEIGHTLEY AVENUE
WINDRADYNE, NSW 2795

HOUSE TYPE: ALLIRA 25
FACADE: VOGUE
TYPE: DOUBLE GARAGE
SPECIFICATION: STANDARD

DRAWING TITLE:
WET AREA PLANS

DRAWN BY:
DH

DATE DRAWN:
04.03.26


SCALE:
1 : 50

COUNCIL AREA:
BATHURST

DRWG No:
08


JOB No:
T001732

ISSUE:
C

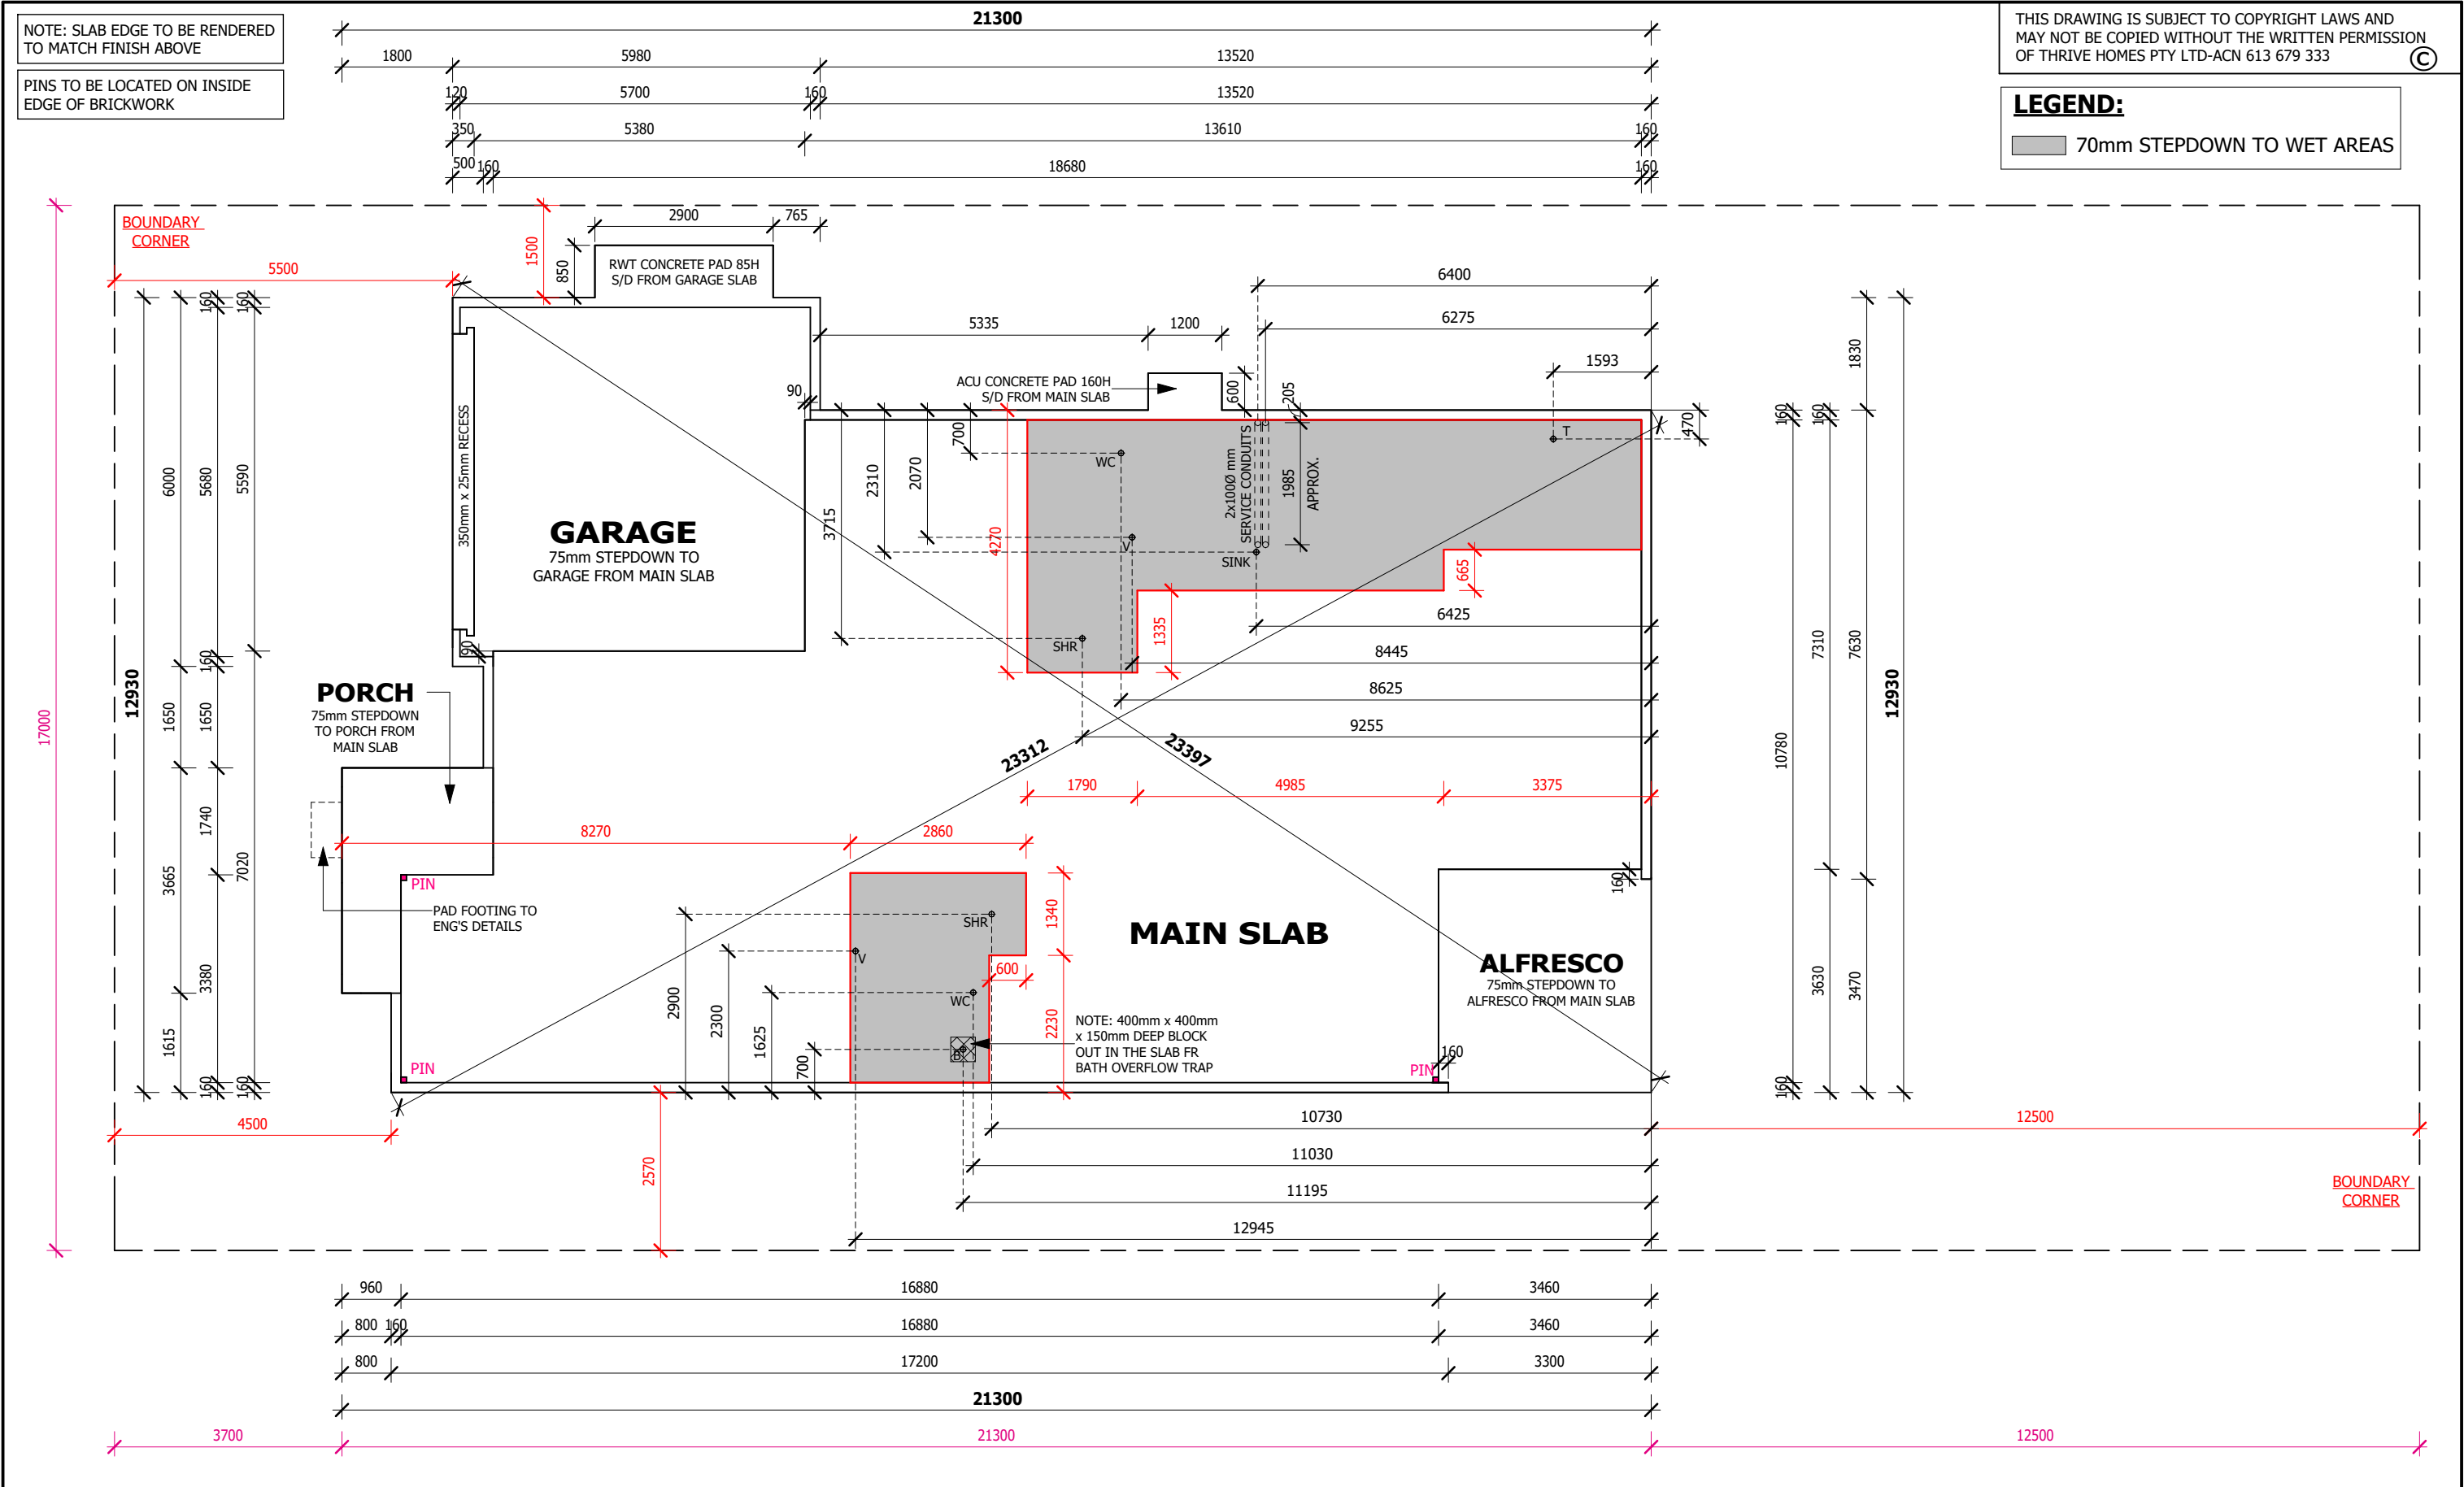

NOTES: PLEASE NOTE: DETAILS SHOWN ON THESE PLANS ARE INTENDED TO BE ACCURATE - HOWEVER INFORMATION WRITTEN INTO INDIVIDUAL CONTRACTS WILL TAKE PRECEDENCE OVER PLANS * ALL DIMENSIONS ARE IN MILLIMETRES * DO NOT SCALE - USE WRITTEN DIMENSIONS * ALL DIMENSIONS ARE TO STRUCTURAL FRAMES ONLY EXCLUDING FINISHED SURFACES	ThriveHomes LEVEL 7, 5 RIDER BOULEVARD RHODES NSW 2138 TELEPHONE 02 8758 4800 FAX 02 9300 5646 Builder's licence No. 301349C	CLIENT: THRIVE HOMES	HOUSE TYPE: ALLIRA 25	DRAWN BY: DH	DATE DRAWN: 04.03.26	SCALE: 1 : 100
		SITE ADDRESS: LOT 175 (DP 1304135) NO. 17 KEIGHTLEY AVENUE WINDRADYNE, NSW 2795	FACADE: VOGUE	COUNCIL AREA: BATHURST		DRWG No: 09
			TYPE: DOUBLE GARAGE			
			DRAWING TITLE: SLAB SETOUT PLAN	SPECIFICATION: STANDARD		JOB No: T001732

KEIGHTLEY AVENUE

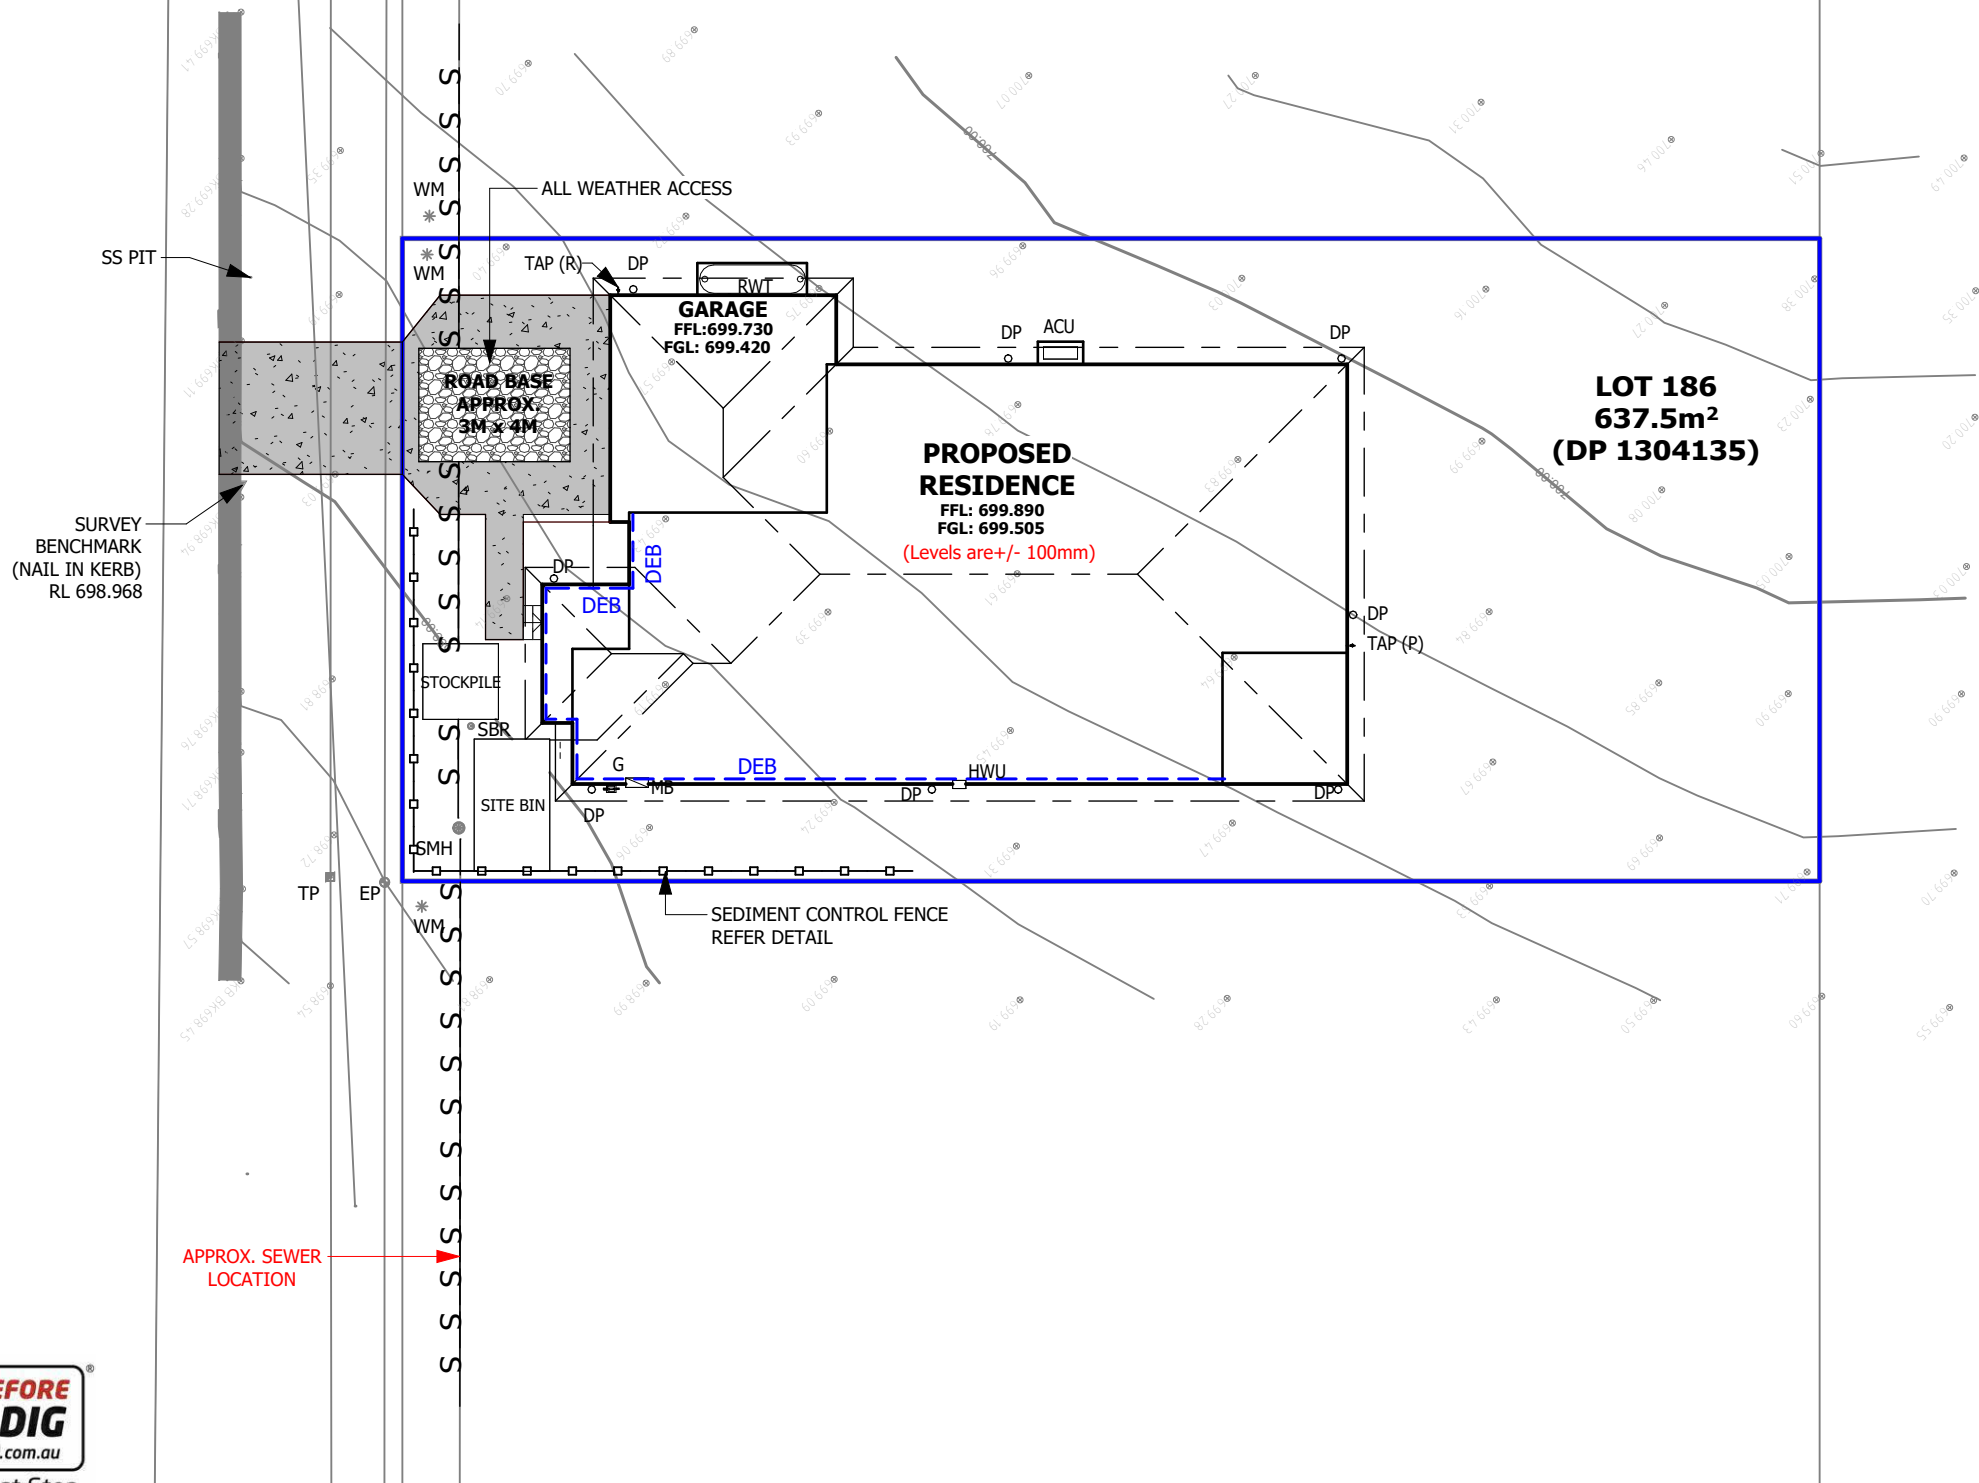


THIS DRAWING IS SUBJECT TO COPYRIGHT LAWS AND MAY NOT BE COPIED WITHOUT THE WRITTEN PERMISSION OF THRIVE HOMES PTY LTD-ACN 613 679 333

SEDIMENT CONTROL

INSTALL SEDIMENT CONTROL STRUCTURES IN LOCATIONS INDICATED ON THIS DRAWING AND AS OTHERWISE REQUIRED TO CONTROL SEDIMENT DURING ALL EXCAVATIONS AND WHILST AREAS OF THE SITE ARE EXPOSED TO EROSION. REVIEW CONTROL MEASURES AND MAINTAIN STRUCTURES DURING CONSTRUCTION.

IF ADDITIONAL MEASURES ARE REQUIRED FOR EROSION AND CONTROL OR BY COUNCIL REQUIREMENTS, REFER TO "URBAN EROSION AND SEDIMENT CONTROL" GUIDELINES PREPARED BY THE DEPARTMENT OF CONSERVATION AND LAND MANAGEMENT.

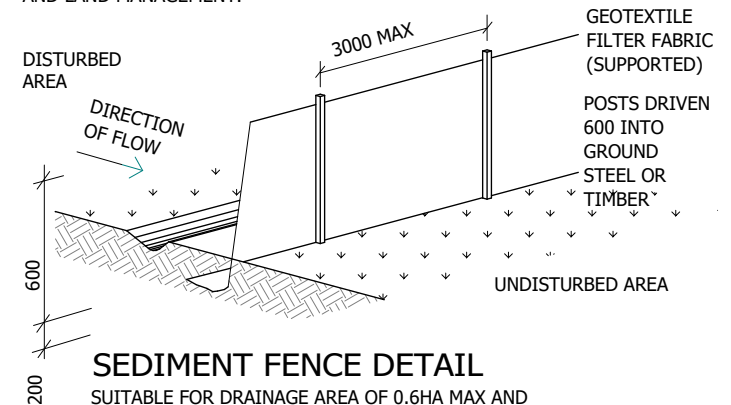

NOTES:

PLEASE NOTE: DETAILS SHOWN ON THESE PLANS ARE INTENDED TO BE ACCURATE - HOWEVER INFORMATION WRITTEN INTO INDIVIDUAL CONTRACTS WILL TAKE PRECEDENCE OVER PLANS

- * ALL DIMENSIONS ARE IN MILLIMETRES
- * DO NOT SCALE - USE WRITTEN DIMENSIONS
- * ALL DIMENSIONS ARE TO STRUCTURAL FRAMES ONLY EXCLUDING FINISHED SURFACES

ThriveHomes
LEVEL 7, 5 RIDER BOULEVARD
RHODES NSW 2138
TELEPHONE 02 8758 4800
FAX 02 9300 5646
Builder's licence No. 301349C

CLIENT:
THRIVE HOMES

SITE ADDRESS:
LOT 175 (DP 1304135)
NO. 17 KEIGHTLEY AVENUE
WINDRADYNE, NSW 2795

HOUSE TYPE: ALLIRA 25
FACADE: VOGUE
TYPE: DOUBLE GARAGE
SPECIFICATION: STANDARD

DRAWING TITLE:
SEDIMENT CONTROL PLAN

DRAWN BY: DH	DATE DRAWN: 04.03.26	SCALE: 1 : 200
COUNCIL AREA: BATHURST		DRWG No: 10
JOB No: T001732		ISSUE: C

©



PLEASE NOTE: DETAILS SHOWN ON THESE PLANS ARE INTENDED TO BE ACCURATE - HOWEVER INFORMATION WRITTEN INTO INDIVIDUAL CONTRACTS WILL TAKE PRECEDENCE OVER PLANS

- * ALL DIMENSIONS ARE IN MILLIMETRES
- * DO NOT SCALE - USE WRITTEN DIMENSIONS
- * ALL DIMENSIONS ARE TO STRUCTURAL FRAMES ONLY EXCLUDING FINISHED SURFACES

ThriveHomes

SITE ADDRESS:
LOT 175 (DP 1304135)
NO. 17 KEIGHTLEY AVENUE
WINDRADYNE, NSW 2795

HOUSE TYPE: ALLIRA 25

DRAWN BY:

DATE DRAWN:

SCALE:

1

04.03.26


1 : 200

COUNCIL AREA:
BATHURST


JOB No:
T001732

DRWG No:	11
----------	----


ISSUE:	C
--------	---

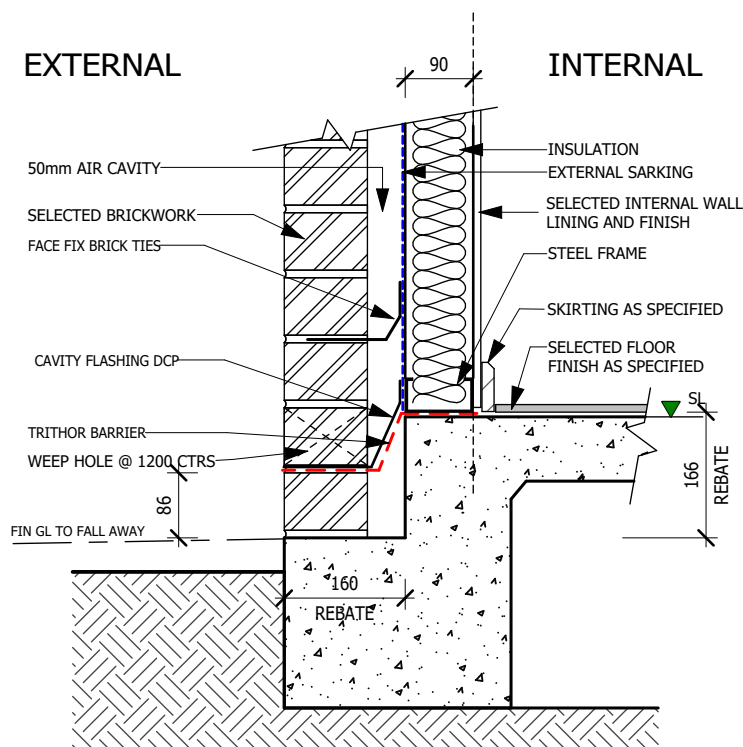


1 BRICK VENEER REBATE DETAIL
SCALE: 1 : 10

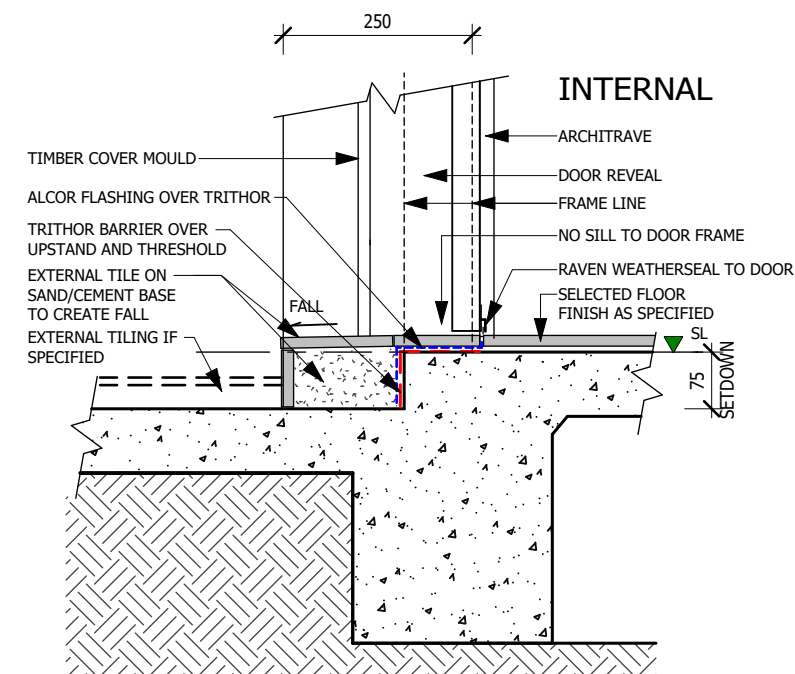

2 BRICK VENEER PORCH ENTRY DOOR
SCALE: 1 : 10

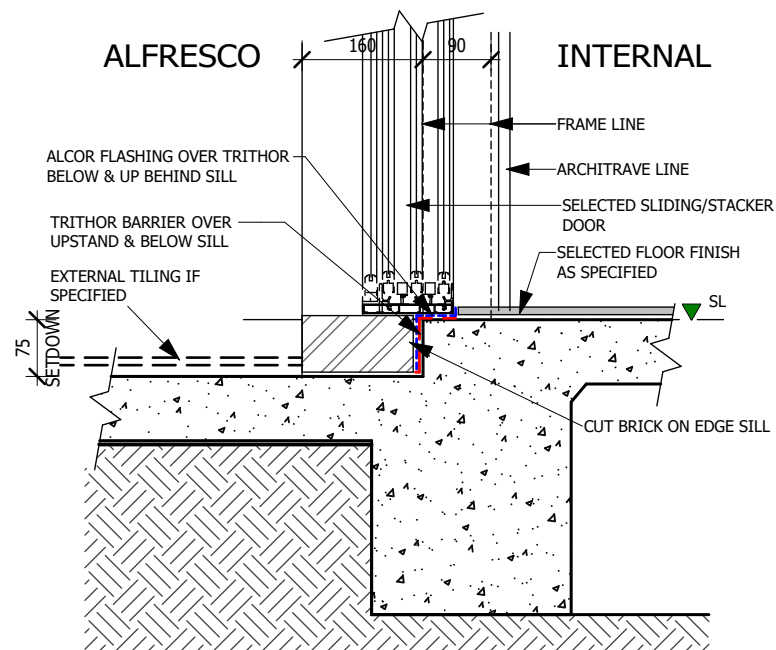

3 ALFRESCO DOOR - BRICK VENEER
SCALE: 1 : 10

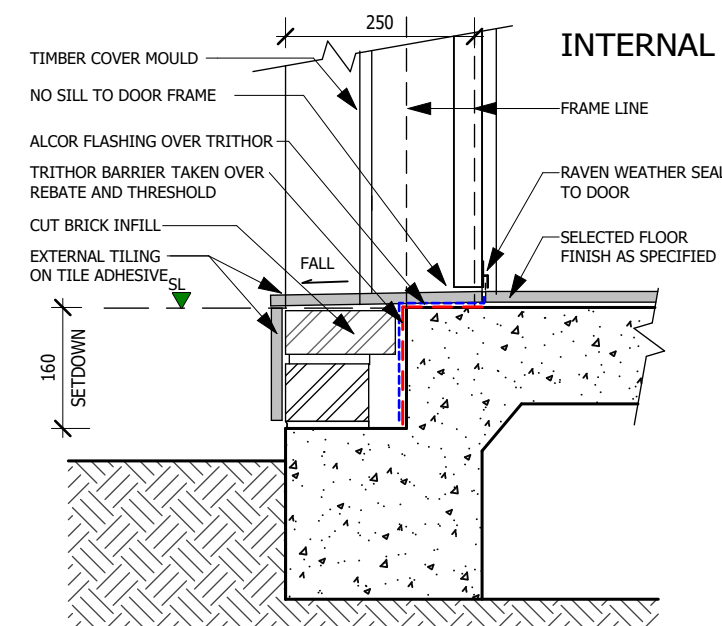

4 LAUNDRY TIMBER DOOR
SCALE: 1 : 10

NOTE: DETAILS ARE APPLICABLE TO ALL ARCHITECTURAL CONDITIONS NOT SPECIFICALLY DETAILED OR REFERENCED ON ARCHITECTURAL DRAWINGS.

NOTES:

PLEASE NOTE: DETAILS SHOWN ON THESE PLANS ARE INTENDED TO BE ACCURATE - HOWEVER INFORMATION WRITTEN INTO INDIVIDUAL CONTRACTS WILL TAKE PRECEDENCE OVER PLANS

- * ALL DIMENSIONS ARE IN MILLIMETRES
- * DO NOT SCALE - USE WRITTEN DIMENSIONS
- * ALL DIMENSIONS ARE TO STRUCTURAL FRAMES ONLY EXCLUDING FINISHED SURFACES

ThriveHomes

LEVEL 7, 5 RIDER BOULEVARD,
RHODES NSW 2138,
TELEPHONE 02 8758 4800,
FAX 02 9300 5646


Builder's licence No. 301349C

CLIENT:
THRIVE HOMES


SITE ADDRESS:
LOT 175 (DP 1304135)
NO. 17 KEIGHTLEY AVENUE
WINDRADYNE, NSW 2795

HOUSE TYPE: ALLIRA 25
FACADE: VOGUE
TYPE: DOUBLE GARAGE
SPECIFICATION: STANDARD
DRAWING TITLE:
SLAB DETAILS 1


DRAWN BY:	DATE DRAWN:	SCALE:
DH	04.03.26	1 : 10
COUNCIL AREA:	DRWG No:	
BATHURST	D1	
JOB No:	ISSUE:	
T001732	C	

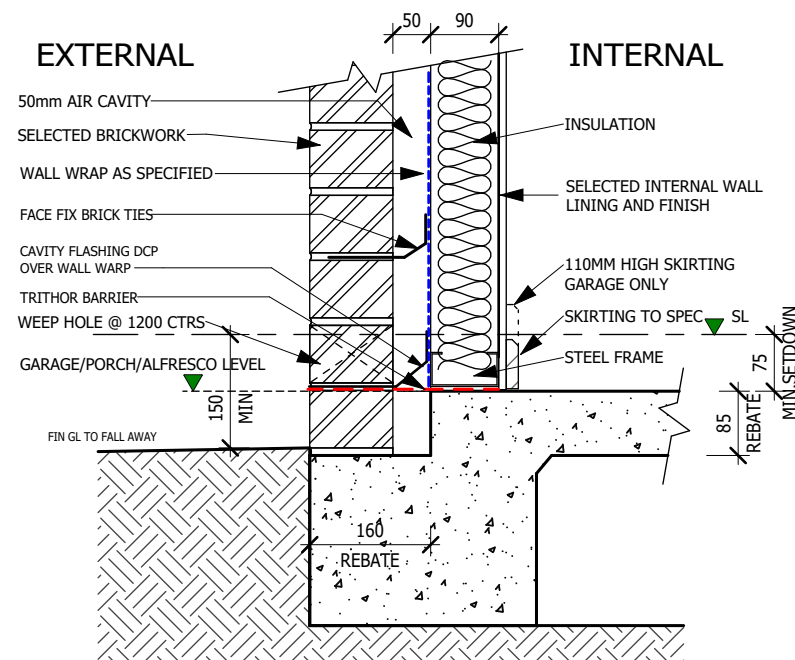


1 GARAGE REBATE (SIDE) & PORCH/ALFRESCO

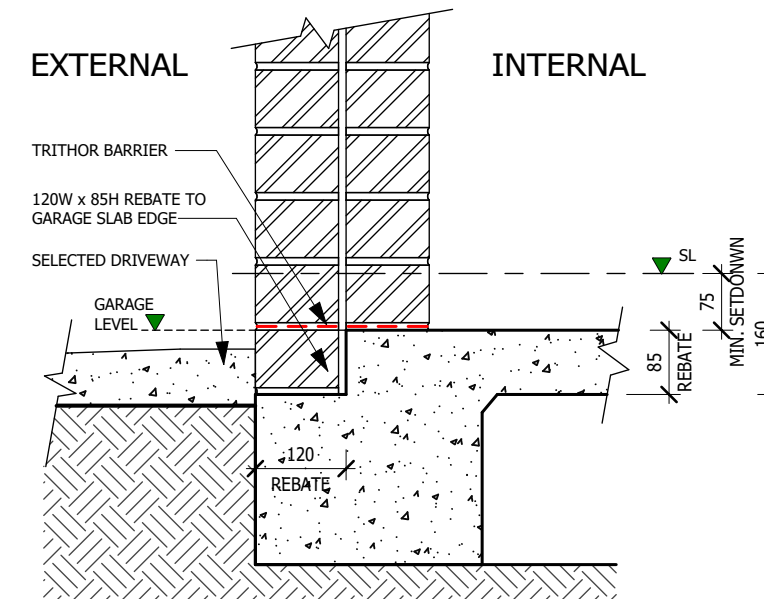

2 GARAGE REBATE (FRONT SIDE OF DOOR)

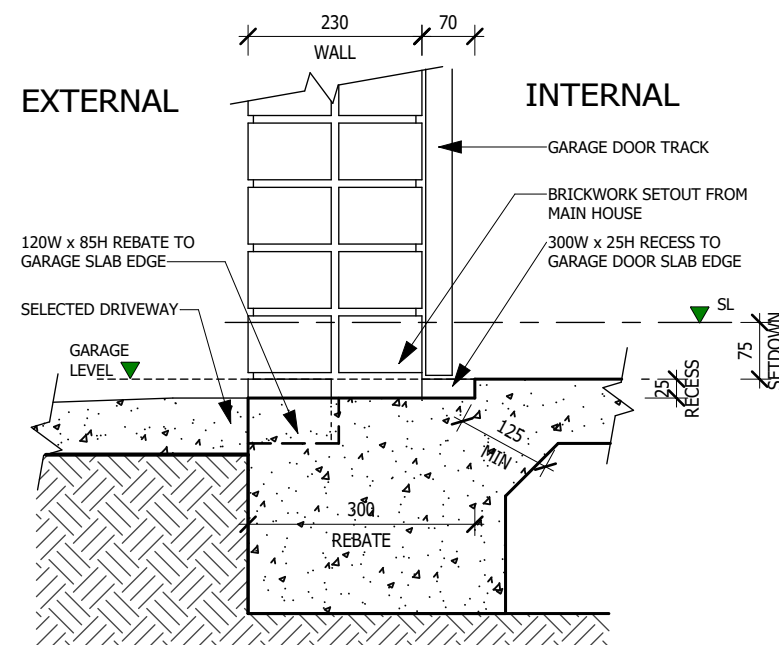

3 GARAGE RECESS (FRONT THROUGH RECESS)

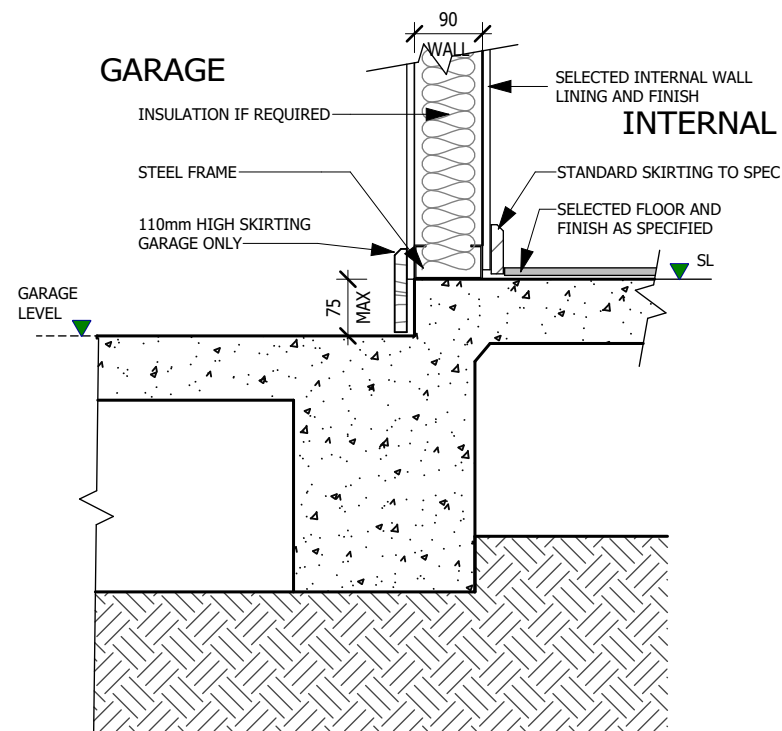

4 INTERNA GARAGE STEP - 75MM STEP ONLY
SCALE: 1 : 10

NOTES:

PLEASE NOTE: DETAILS SHOWN ON THESE PLANS ARE INTENDED TO BE ACCURATE - HOWEVER INFORMATION WRITTEN INTO INDIVIDUAL CONTRACTS WILL TAKE PRECEDENCE OVER PLANS

- * ALL DIMENSIONS ARE IN MILLIMETRES
- * DO NOT SCALE - USE WRITTEN DIMENSIONS
- * ALL DIMENSIONS ARE TO STRUCTURAL FRAMES ONLY EXCLUDING FINISHED SURFACES

ThriveHomes
LEVEL 7, 5 RIDER BOULEVARD,
RHODES NSW 2138,
TELEPHONE 02 8758 4800,
FAX 02 9300 5646


Builder's licence No. 301349C

CLIENT:
THRIVE HOMES


SITE ADDRESS:
LOT 175 (DP 1304135)
NO. 17 KEIGHTLEY AVENUE
WINDRADYNE, NSW 2795

HOUSE TYPE:	ALLIRA 25
FACADE:	VOGUE
TYPE:	DOUBLE GARAGE
SPECIFICATION:	STANDARD
DRAWING TITLE: SLAB DETAILS 2	


DRAWN BY: DH	DATE DRAWN: 04.03.26	SCALE: 1 : 10
COUNCIL AREA: BATHURST		DRWG No: D2
JOB No: T001732		ISSUE: C

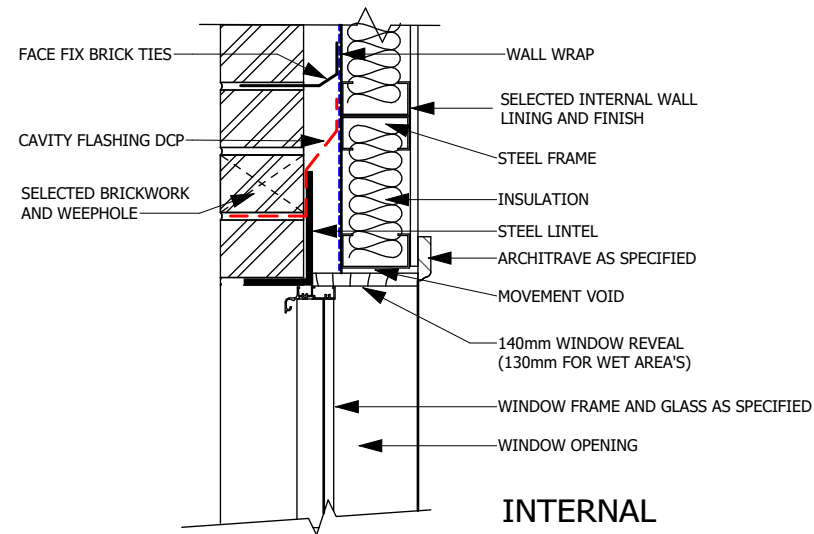


1 WINDOW HEAD - BRICK VENEER
SCALE: 1 : 10

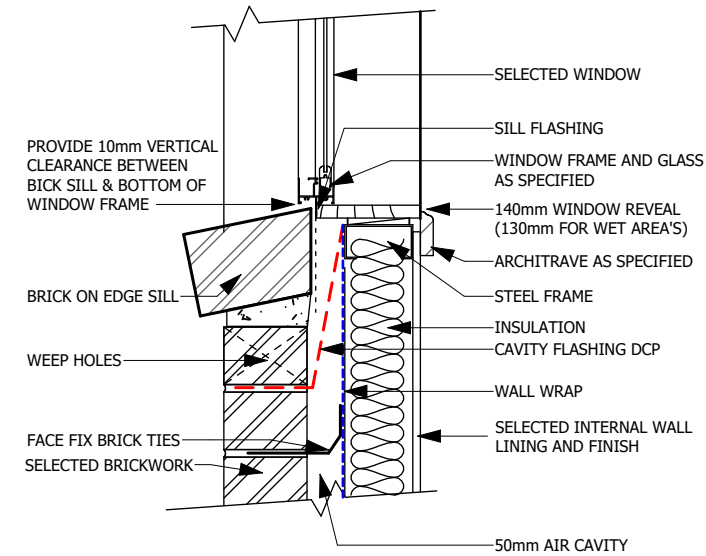

2 WINDOW SILL - BRICK VENEER
SCALE: 1 : 10

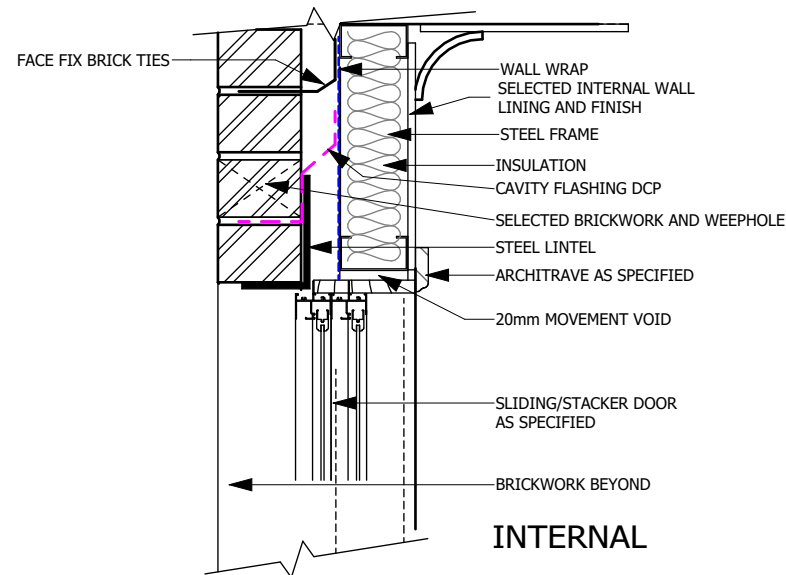

3 SLIDING DOOR HEAD - BV1
SCALE: 1 : 10

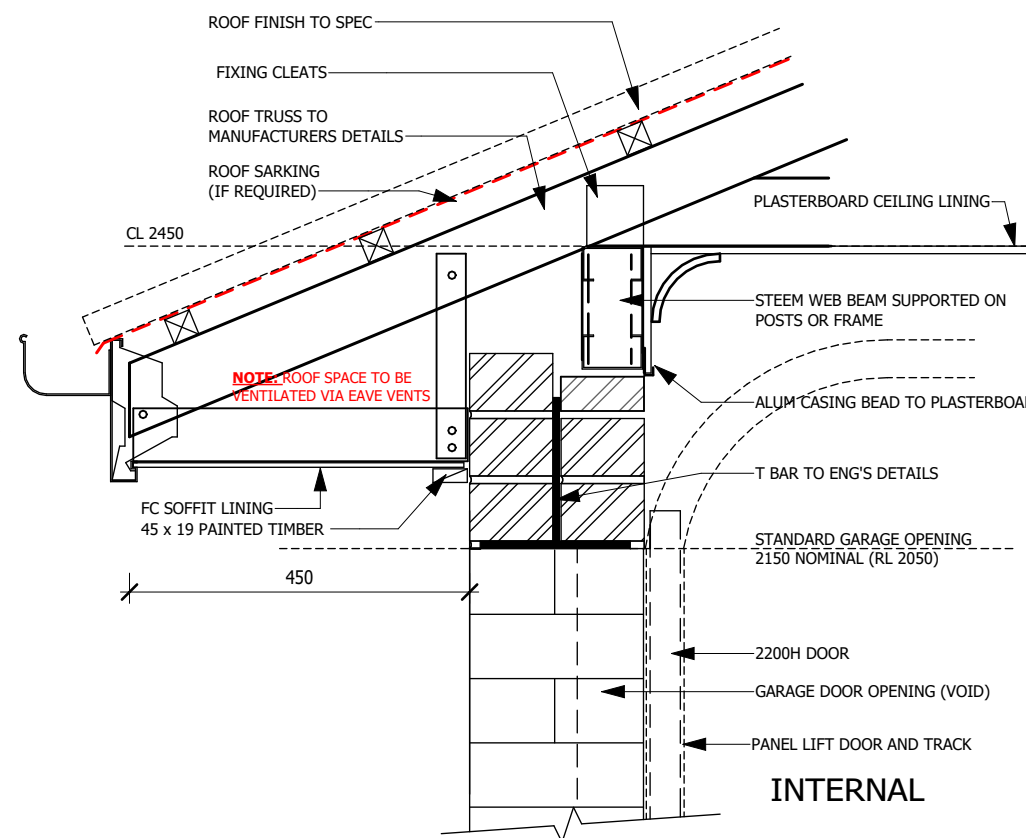

4 GARAGE DOOR HEAD DETAIL EAVES ABOVE
SCALE: 1 : 10

NOTES:

PLEASE NOTE: DETAILS SHOWN ON THESE PLANS ARE INTENDED TO BE ACCURATE - HOWEVER INFORMATION WRITTEN INTO INDIVIDUAL CONTRACTS WILL TAKE PRECEDENCE OVER PLANS
* ALL DIMENSIONS ARE IN MILLIMETRES
* DO NOT SCALE - USE WRITTEN DIMENSIONS
* ALL DIMENSIONS ARE TO STRUCTURAL FRAMES ONLY EXCLUDING FINISHED SURFACES

ThriveHomes

LEVEL 7, 5 RIDER BOULEVARD,
RHODES NSW 2138,
TELEPHONE 02 8758 4800,
FAX 02 9300 5646



Builder's licence No. 301349C

CLIENT:
THRIVE HOMES

SITE ADDRESS:
LOT 175 (DP 1304135)
NO. 17 KEIGHTLEY AVENUE
WINDRADYNE, NSW 2795

HOUSE TYPE: ALLIRA 25
FACADE: VOGUE
TYPE: DOUBLE GARAGE
SPECIFICATION: STANDARD
DRAWING TITLE:
WALL OPENINGS DETAILS

DRAWN BY: DH	DATE DRAWN: 04.03.26	SCALE: 1 : 10
COUNCIL AREA: BATHURST		DRWG No: D3
JOB No: T001732		ISSUE: C

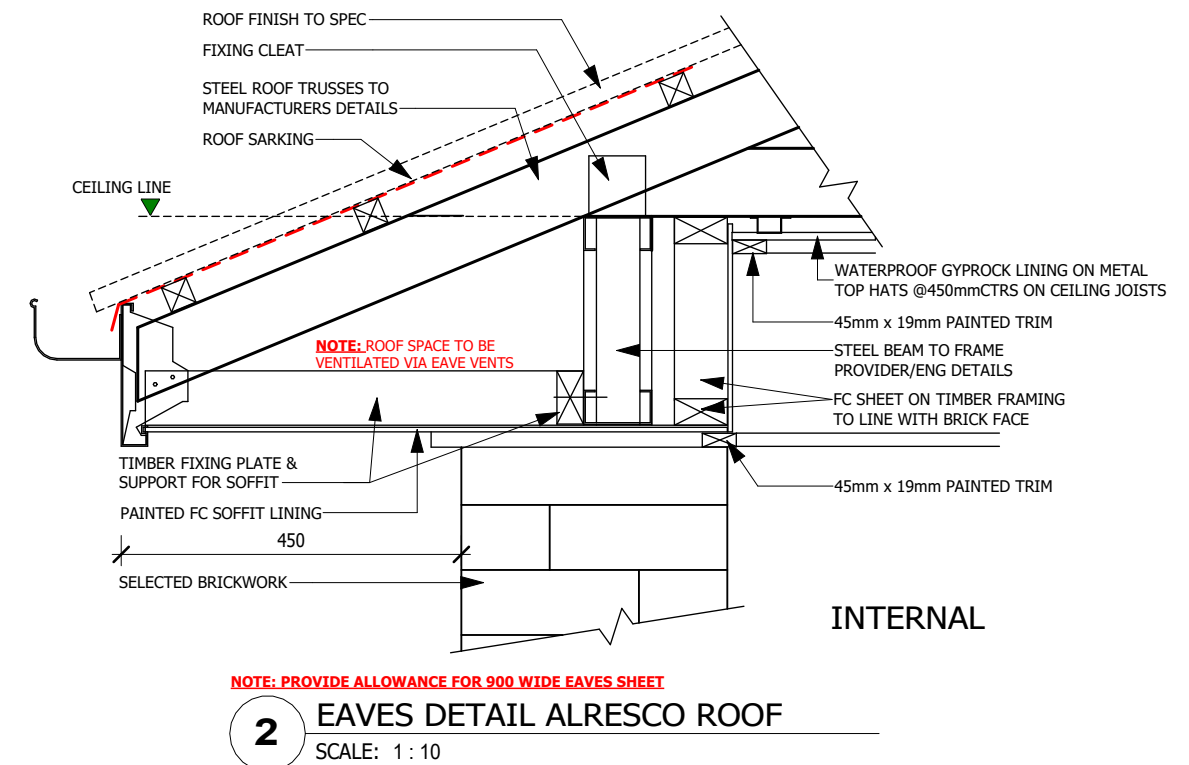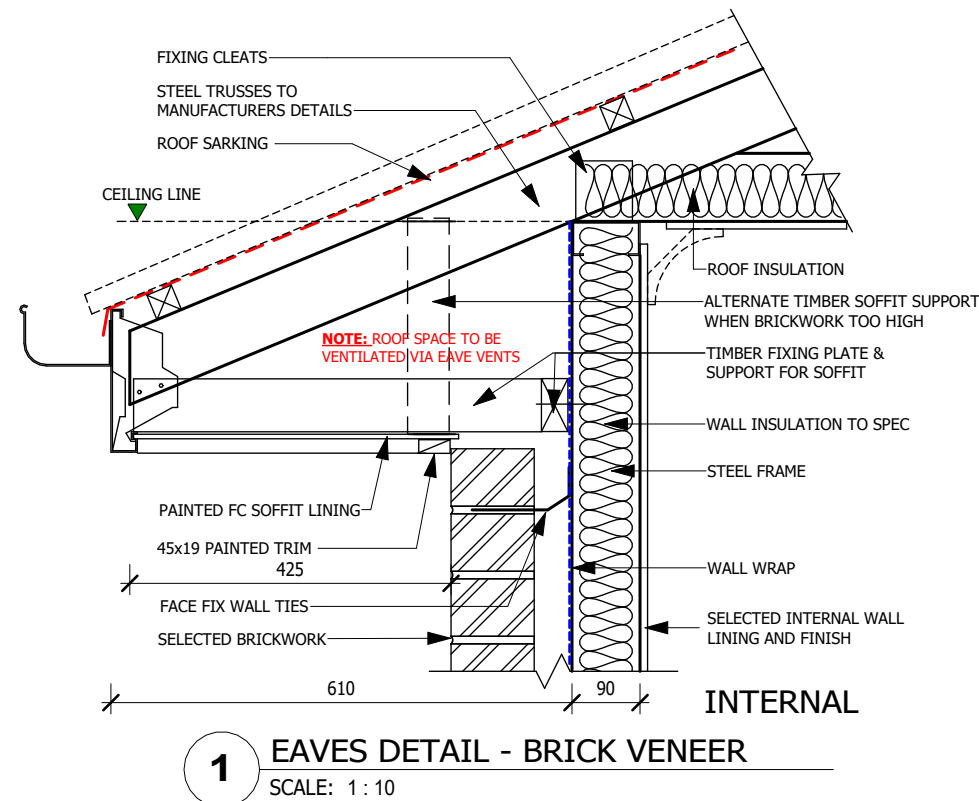

NOTES:

PLEASE NOTE: DETAILS SHOWN ON THESE PLANS ARE INTENDED TO BE ACCURATE - HOWEVER INFORMATION WRITTEN INTO INDIVIDUAL CONTRACTS WILL TAKE PRECEDENCE OVER PLANS

- * ALL DIMENSIONS ARE IN MILLIMETRES
- * DO NOT SCALE - USE WRITTEN DIMENSIONS
- * ALL DIMENSIONS ARE TO STRUCTURAL FRAMES ONLY EXCLUDING FINISHED SURFACES

ThriveHomes

LEVEL 7, 5 RIDER BOULEVARD,
RHODES NSW 2138,
TELEPHONE 02 8758 4800,
FAX 02 9300 5646

Builder's licence No. 301349C

CLIENT:
THRIVE HOMES


SITE ADDRESS:
LOT 175 (DP 1304135)
NO. 17 KEIGHTLEY AVENUE
WINDRADYNE, NSW 2795

HOUSE TYPE: ALLIRA 25
FACADE: VOGUE
TYPE: DOUBLE GARAGE
SPECIFICATION: STANDARD
DRAWING TITLE:
TYPICAL EAVES DETAILS


DRAWN BY: DH	DATE DRAWN: 04.03.26	SCALE: 1 : 10
COUNCIL AREA: BATHURST		DRWG No: D4
JOB No: T001732		ISSUE: C

THIS DRAWING IS SUBJECT TO COPYRIGHT LAWS AND
MAY NOT BE COPIED WITHOUT THE WRITTEN PERMISSION
OF THRIVE HOMES PTY LTD-ACN 613 679 333


THE KITCHEN LAYOUT SHOWN IS ONLY DIAGRAMATIC
ALL DETAILS AND DIMENSIONS TO BE CONFIRMED BY
THE MAKER PRIOR TO MANUFACTURE

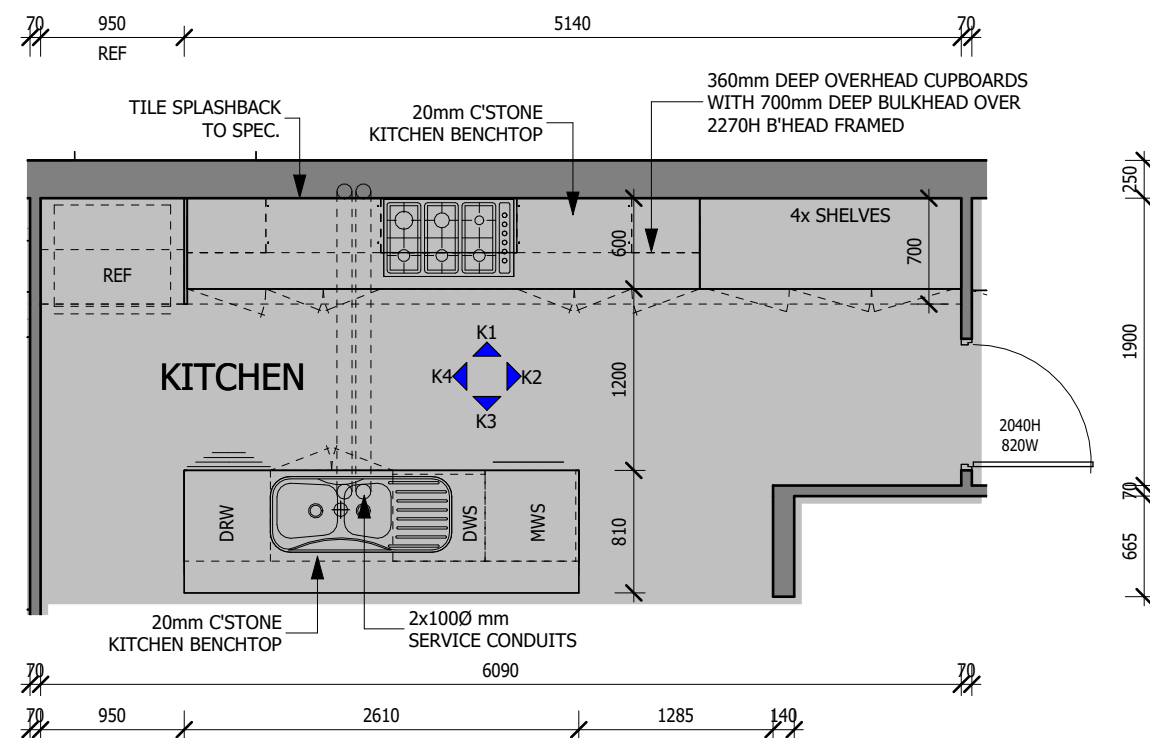


KITCHEN PLAN

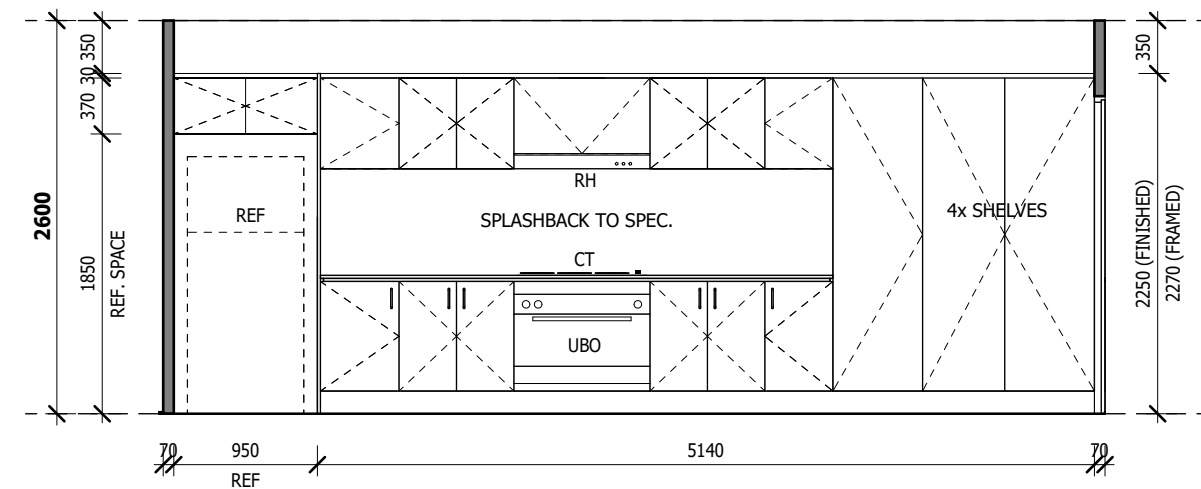


ELEVATION K1

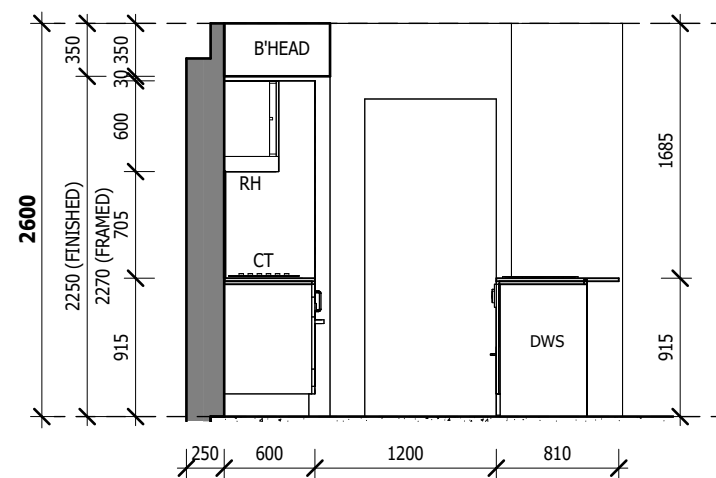

ELEVATION K2

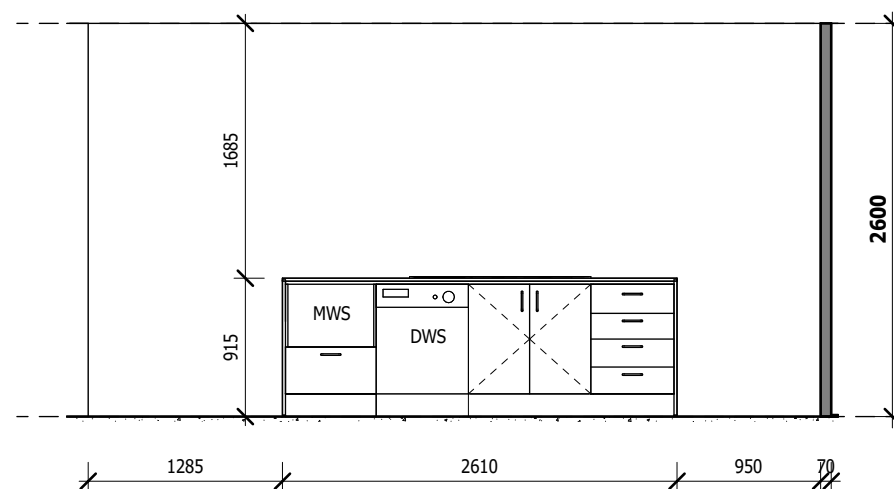

ELEVATION K3

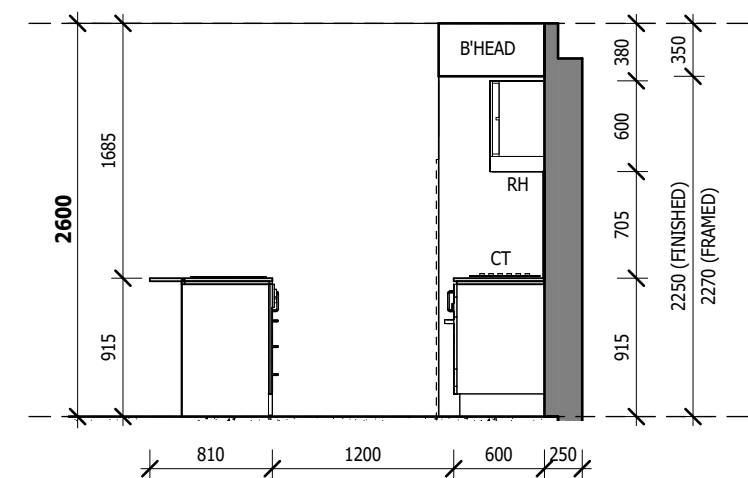

ELEVATION K4

NOTES: PLEASE NOTE: DETAILS SHOWN ON THESE PLANS ARE INTENDED TO BE ACCURATE - HOWEVER INFORMATION WRITTEN INTO INDIVIDUAL CONTRACTS WILL TAKE PRECEDENCE OVER PLANS * ALL DIMENSIONS ARE IN MILLIMETRES * DO NOT SCALE - USE WRITTEN DIMENSIONS * ALL DIMENSIONS ARE TO STRUCTURAL FRAMES ONLY EXCLUDING FINISHED SURFACES	ThriveHomes LEVEL 7, 5 RIDER BOULEVARD RHODES NSW 2138 TELEPHONE 02 8758 4800 FAX 02 9300 5646 Builder's licence No. 301349C	CLIENT: THRIVE HOMES	HOUSE TYPE: ALLIRA 25 FACADE: VOGUE	DRAWN BY: DH	DATE DRAWN: 04.03.26	SCALE: 1 : 50
		SITE ADDRESS: LOT 175 (DP 1304135) NO. 17 KEIGHTLEY AVENUE WINDRADYNE, NSW 2795	TYPE: DOUBLE GARAGE SPECIFICATION: STANDARD	COUNCIL AREA: BATHURST	DRWG No: KP	
			DRAWING TITLE: KITCHEN PLAN	JOB No: T001732	ISSUE: C	

NOTE: PERSPECTIVE IS FOR DIAGRAMATIC PURPOSES ONLY



NOTES:

PLEASE NOTE: DETAILS SHOWN ON THESE PLANS ARE INTENDED TO BE ACCURATE - HOWEVER INFORMATION WRITTEN INTO INDIVIDUAL CONTRACTS WILL TAKE PRECEDENCE OVER PLANS

- * ALL DIMENSIONS ARE IN MILLIMETRES
- * DO NOT SCALE - USE WRITTEN DIMENSIONS
- * ALL DIMENSIONS ARE TO STRUCTURAL FRAMES ONLY EXCLUDING FINISHED SURFACES

ThriveHomes
LEVEL 7, 5 RIDER BOULEVARD
RHODES NSW 2138
TELEPHONE 02 8758 4800
FAX 02 9300 5646

Builder's licence No. 301349C

CLIENT:
THRIVE HOMES

SITE ADDRESS:
LOT 175 (DP 1304135)
NO. 17 KEIGHTLEY AVENUE
WINDRADYNE, NSW 2795

HOUSE TYPE: ALLIRA 25
FACADE: VOGUE
TYPE: DOUBLE GARAGE
SPECIFICATION: STANDARD

DRAWING TITLE:
KITCHEN VIEWS

DRAWN BY:
DH

DATE DRAWN:
04.03.26

SCALE:

COUNCIL AREA:
BATHURST

DRWG No:
KV

JOB No:
T001732

ISSUE:
C