

AUSTRALIAN STANDARDS - REQUIREMENTS

ALL SITE PREPERATION & EARTH RETAINING STRUCTURES SHALL BE IN ACCORDANCE WITH **AS4678** & STRICTLY IN ACCORDANCE WITH ENGINEERS SPECIFICATIONS

CONCRETE SLAB & FOOTINGS TO BE DESIGNED & CONSTRUCTED IN ACCORDANCE WITH **AS2870** & STRICTLY IN ACCORDANCE WITH ENGINEERS SPECIFICATIONS

PILED FOOTINGS TO BE DESIGNED & CONSTRUCTED IN ACCORDANCE WITH **AS2159** & STRICTLY IN ACCORDANCE WITH ENGINEERS SPECIFICATIONS

ALL MASONRY TO BE DESIGNED & CONSTRUCTED IN ACCORDANCE WITH **AS3700**

THE STRUCTURAL DESIGN OF ALL BUILDING(S) TO BE DESIGNED & CONSTRUCTED IN ACCORDANCE WITH **AS/NZS1170** & STRICTLY IN ACCORDANCE WITH ENGINEERS SPECIFICATIONS

STEEL STRUCTURES TO BE DESIGNED & CONSTRUCTED IN ACCORDANCE WITH **AS4100** & STRICTLY IN ACCORDANCE WITH ENGINEERS SPECIFICATIONS

COLD-FORMED STEEL STRUCTURES TO BE DESIGNED & CONSTRUCTED IN ACCORDANCE WITH **AS/NZS4600** & STRICTLY IN ACCORDANCE WITH ENGINEERS SPECIFICATIONS

WINDOWS & DOORS SHALL BE MANUFACTURED & INSTALLED IN ACCORDANCE WITH **AS2047**

ROOF TRUSSES SHALL BE DESIGNED IN ACCORDANCE WITH **AS1720** & ERECTED, FXED & BRACED IN ACCORDANCE WITH MANUFACTURER'S INSTRUCTIONS

SHEET METAL ROOFING SHALL BE DESIGNED, MANUFACTURED & INSTALLED IN ACCORDANCE WITH **AS1562**

TERRACOTTA, FIBRE-CEMENT & TIMBER SLATES & SHINGLES SHALL BE DESIGNED, MANUFACTURED & INSTALLED IN ACCORDANCE WITH **AS4597**

ROOF TILES SHALL BE DESIGNED, MANUFACTURED & INSTALLED IN ACCORDANCE WITH **AS2050**

METAL WALL CLADDING SHALL BE DESIGNED, MANUFACTURED & INSTALLED IN ACCORDANCE WITH **AS1562**

AUTOCLAVED AERATED CONCRETE WALL CLADDING SHALL BE DESIGNED, MANUFACTURED & INSTALLED IN ACCORDANCE WITH **AS5146**

ALL WINDOWS & GLAZED DOORS SHALL BE DESIGNED, MANUFACTURED & INSTALLED IN ACCORDANCE WITH **AS2047** & STRICTLY IN ACCORDANCE WITH MANUFACTURERS SPECIFICATIONS

ALL GLAZING & GLAZED ASSEMBLIES SHALL BE DESIGNED, MANUFACTURED & INSTALLED IN ACCORDANCE WITH **AS1288** & STRICTLY IN ACCORDANCE WITH MANUFACTURERS SPECIFICATIONS

STRIP & SHEET FLOORING SHALL BE INSTALLED IN ACCORDANCE WITH **AS1684**

INSTALLATION OF PARTICLEBOARD FLOORING SHALL BE INSTALLED IN ACCORDANCE WITH **AS1860**

ALL TMBER DOORS & DOOR SETS SHALL BE MANUFACTURED IN ACCORDANCE WITH **AS2688** & **AS52689** UNLESS LISTED OTHERWISE IN SCHEDULE OF WORKS

TIMBER FRAMING IS TO BE DESIGNED & CONSTRUCTED IN ACCORDANCE WITH **AS1720** & RESIDENTIAL TIMBER-FRAMED CONSTRUCTION **AS1684** & STRICTLY IN ACCORDANCE WITH THE RESIDENTIAL TIMBER FRAMING CODE.

ALL PLUMBING SHALL COMPLY WITH THE REQUIREMENTS OF THE RELEVANT SUPPLY AUTHORITY & **AS3500**, & IN ACCORDANCE WITH THE AUSTRALIAN BUILDING CODES BOARD (ABCB), NCC VOLUME 3 'PLUMBING CODE OF AUSTRALIA'. ALL PLUMBING WORK MUST CARRIED OUT BY A LICENSED PLUMBER

SMOKE ALARMS MUST COMPLY WTIH **AS3786**

DRAINAGE SHALL BE DESIGNED & CONSTRUCTED IN ACCORDANCE WITH **AS3500**

WATERPROOFING OF DOMESTIC WET AREAS SHALL BE IN ACCORDANCE WITH **AS3740** & CERAMIC TILES MUST BE IN ACCORDANCE WITH **AS3958** & STRICTLY IN ACCORDANCE WITH MANUFACTURERS SPECIFICATIONS

INTERIOR & ARTIFICIAL LIGHTING SHALL BE DESIGNED & INSTALLED IN ACCORDANCE WITH **AS/NZS1680**

SWIMMING POOLS, INCLUDING POOL DEPTHS, SAFETY BARRIERS & WATER RETICULATION SYSTEMS MUST BE INSTALLED IN ACCORDANCE WITH **AS1926** & STRICTLY IN ACCORDANCE WITH MANUFACTURERS SPECIFICATIONS

DOMESTIC COLID-FUEL BURNING APPLIANCES MUST BE INSTALLED IN ACCORDANCE WITH **AS/NZS2918** & STRICTLY IN ACCORDANCE WITH MANUFACTURERS SPECIFICATIONS

BUILDINGS LOCATED IN BUSHFIRE PRONE AREAS MUST COMPLY WITH **AS3959** & STRICTLY IN ACCORDANCE WITH THE CONSTRUCTION REQUIREMENTS PRESCRIBED WITHIN THE RELEVANT BAL RATING, ASSESSED WITHIN **AS3959**.

ENGAGED PIERS IN SINGLE LEAF MASONRY WALLS SHALL BE CONSTRUCTED IN ACCORDANCE WITH TABLE 9.2 PIER SPACINGS FOR ONE WAY SPANNING WALLS, OF AUSTRALIAN ST&ARD **AS4773.1-2010** MASONRY IN SMALL BUILDINGS. REFER TO THE TABLE EXTRACT FOR DETAILS

TERMITE PROTECTION WILL BE IN ACCORDANCE WITH PART 3.4 OF THE ABCB HOUSING PROVISIONS AND **AS3660.1**

LIFT OFF HINGES (LOH) WILL BE INSTALLED TO FULLY ENSLOED SANITARY COMPARTMENTS IN ORDER TO ENSURE COMPLIANCE WITH ABCB HOUSING PROVISIONS PART 10.4

G.J. Gardner. HOMES

DRAWING LIST

DRAWING No.	DRAWING TITLE	DATE DRAWN	REVISION
01	TITLE PAGE	02/12/2025	B
02	NCC REQUIREMENTS	02/12/2025	B
03	SITE PLAN	02/12/2025	B
04	GROUND FLOOR PLAN	02/12/2025	B
05	ROOF PLAN	02/12/2025	B
06	CONCRETE SETOUT PLAN	02/12/2025	B
07	ELECTRICAL PLAN	02/12/2025	B
08	BUILDING ELEVATIONS	02/12/2025	B
09	BUILDING ELEVATIONS	02/12/2025	B
10	BUILDING SECTIONS	02/12/2025	B
11	WET AREA ELEVATIONS	02/12/2025	B
12	WET AREA ELEVATIONS	02/12/2025	B
13	BUILDING DETAILS - SHEET 1	02/12/2025	B
14	BUILDING DETAILS - SHEET 2	02/12/2025	B
15	DRIVEWAY PROFILE	02/12/2025	B

SIGNATURES

OWNER	DATE
OWNER	DATE
BUILDER	DATE

LEGEND

CJ	CONSTRUCTION JOINT
DP	DOWNPIPE
FP	FIRE PLACE
FW	FLOOR WASTE
HWS	HOT WATER SYSTEM
AC	AIR CONDITIONING
PS	PLUMBING STACK/DUCT
SP	STEEL POST
TBC	TO BE CONFIRMED
RL	RELATIVE LEVEL
AHD	AUSTRALIAN HEIGHT DATUM
CSD	CAVITY SLIDING DOOR
OHC	OVER HEAD CUPBOARD
FG	FIXED GLASS
FSR	FLOOR SPACE RATIO
LB	LOAD BEARING
NGL	NATURAL GROUND LINE
UBO	UNDER BENCH OVEN
WO	WALL OVEN
DW	DISHWASHER
MW	MICROWAVE
WM	WASHING MACHINE
WIR	WALK-IN ROBE
SD	SLIDING GLASS DOOR
AAW	ALUMINIUM AWNING WINDOW
ADH	ALUMINIUM DOUBLE HUNG WINDOW
AAW	ALUMINIUM AWNING WINDOW
ALW	ALUMINIUM LOUVRE WINDOW
BCA	BUILDING CODE OF AUSTRALIA
AS	AUSTRALIAN ST&ARDS



© COPYRIGHT-THIS DRAWING REMAINS THE PROPERTY OF G.J GARDNER HOMES & IS PROVIDED FOR THE USE AS DESCRIBED & MAY NOT BE USED OR REPRODUCED IN WHOLE OR IN PART WITH OUT THE WRITTEN PERMISSION. ANY L&SCAPING (WHEN SHOWN) ARE FOR ILLUSTRATIVE PURPOSES ONLY & DO NOT FORM PART OF ANY CONTRACT

G.J. Gardner. HOMES G.J. GARDNER ORANGE Construct Homes Orange Pty Ltd A.B.N: 19 622 460 119 License: 317706C PO Box 8015, Orange East, NSW, 2800 P: (02) 6360 3988 W: www.gjgardner.com.au E: orange@gjgardner.com.au	ROBINA 125 CLASSIC © COPYRIGHT EXCLUSIVE TO G.J.GARDNER HOMES	TONY JAMES DESIGN PTY LTD A.B.N: 96 486 946 536 Q.B.C.C License: 10632`7 V.B.A License: DP-AD-44789 M: 0412 832 646 P: (07) 5665 9230 E: anthony@tonyjames.com.au W: www.tonyjames.com.au	CLIENT: SARAH KENNEDY DRAWING TITLE: TITLE PAGE	PROJECT: PROPOSED NEW RESIDENCE LOT 217 DP 1305914 47 HAWKE LANE ORANGE NSW 2800	PAGES: 01 OF 15	SHEET SIZE: A3	FLOOR AREAS: GROUND FLOOR 90.74 m² GARAGE 22.54 m² ALFRESCO 9.43 m² PORCH 2.45 m² 125.16 m²	REV: 1 2 A B	DETAILS: PRELIMINARY ISSUE 1 PRELIMINARY ISSUE CONSTRUCTION ISSUE CONSTRUCTION ISSUE	DATE: 02/12/2025 16/12/2025 03/03/2026 06/03/2026
					JOB NO: 40283					
					DRAWN: TJ					
					DATE: 02/12/2025					

GENERAL REQUIREMENTS

DRAWINGS PREPARED FROM INFORMATION SUPPLIED BY THE OWNER &/OR BUILDER
ALL DIMENSIONS ARE IN MILLMETRES & SHALL BE VERIFIED ON SITE

DO NOT SCALE FROM DRAWNG

ALL DIMENSIONS & ALL FLOOR LEVELS PROVIDED ARE TO BE CONFIRMED PRIOR TO CONSTRUCTION

IT IS THE RESPONSIBLITY OF THE BUILDER TO VERIFY DOCUMENTS AS TO THEIR ACCURACY & SUITABILITY

THESE PLANS ARE TO BE READ IN CONJUNCTION WITH ENGINEER'S DETAILS

ALL STRUCTURAL ELEMENTS ARE TO BE DESIGNED BY A PRACTICING STRUCTURAL ENGINEER

ALL METAL FITTINGS USED IN STRUCTURAL TIMBER JOINTS & BRACING MUST HAVE CORROSION PROTECTION.

AUTOCLAVED AERATED CONCRETE PRODUCTS SHALL BE INSTALLED IN ACCORDANCE WITH MANUFACTURER'S PRODUCT SPECIFICATION

NCC REFERS TO THE NATIONAL CONSTRUCTION CODE OF AUSTRALIA - VOLUME 2 (NCC 2022)

ABCB REFERS TO AUSTRALIAN BUILDING CODES BOARD, (ABCB)

ALL CONSTRUCTION WORK MUST BE COMPLETED STRICTLY IN ACCORDANCE WITH THE NATIONAL CONSTRUCTION CODE (NCC 2022) VOLUME 2, NCC VOLUME 3 'PLUMBING CODE OF AUSTRALIA' & THE AUSTRALIAN BUILDING CODES BOARD (ABCB) HOUSING PROVISIONS ST&ARD.

STATUTORY REQUIREMENTS

ALL WORK TO BE CARRIED OUT IN ACCORDANCE WITH THE NCC, CONDITIONS IMPOSED BY THE LOCAL AUTHORITY & THE COMMITMENTS OUTLINED IN THE RELEVANTBASIX CERTIFICATE &/OR NATHER'S ASSESSMENT.

THE BUILDER IS TO COMPLY WITH THE REQUIREMENTS OF ALL LEGALLY CONSTITUTED AUTORITIES HAVING JURISDICTION OVER THE BUILDING WORKS & THE PROVISIONS OF THE HOME BULDING ACT

PRIOR TO THE COMMENCEMENT OF BUILDING WORK, THE BUILDER SHALL PROVIDE TEMPORARY TOILET FACILITIES FOR THE USE OF SUBCONTRACTORS. WHERE THE LOCAL AUTHORITY REQUIRES THE TEMPORARY TOILET TO BE CONNECTED TO THE SEWER MAINS, THE ADDITIONAL COST SHALL BE BORNE BY THE OWNER. ON COMPLETION, THE BULDER SHALL REMOVE THE AMENITY

NCC REQUIREMENTS - SECTION H CLASS 1 & 10 BUILDINGS.

PART H1 STRUCTURE:

A CLASS 1 OR 10 BUILDING'S STRUCTURAL RELIABILITY & RESISTANCE SHALL COMPLY WITHH1P1 OF NCCA CLASS 1 OR CLASS 10 BUILDING MUST BE CONSTRUCTED IN ACCORDANCE WITH SECTION 2 (PARTS 2.1 & 2.2)

OF THE AUSTRALIAN BUILDING CODES BOARD (ABCB) HOUSING PROVISIONS, OR THE RELEVANT PROVSIONS OF H1D2, H1D3-H1D12 OF NCC FOR STRUCTURAL PROVISIONS OR ANY COMBINATION THEREOF ALL SITE PREPERATION & EARTHWORKS SHALL BE IN ACCORDANCE WITH THE ENGINEER'S DETAILS & H1D3 OF NCC & SECTION 3 (PARTS 3.1-3.4) & SECTION 4 (PART 4.2.2) OF THE AUSTRALIAN BUILDING CODES BOARD (ABCB) HOUSING PROVISIONS.

TERMITE RISK MANAGEMENT IN ACCORDANCE WITH NCC H1D3 & ABCB HOUSING PART 3.4

ALL FOOTINGS & SLABS, EXCAVATIONS & UNDERFLOOR FILL SHALL BE IN ACCORDANCE WITH THE ENGINEER'S DETAILS & H1D4 & NSW H1D4(1) & H2D3 OF NCC & SECTION 4 (PARTS 4.1-4.2) OF THE AUSTRALIAN BUILDING CODES BOARD (ABCB) HOUSING PROVISIONS.

ALL MASONRY SHALL COMPLY WITH H1D5 & H2D4 OF NCC & SECTION 5 (PARTS 5.1-5.7) OF THE AUSTRALIAN BUILDING CODES BOARD (ABCB) HOUSING PROVISIONS. APPROPRIATE TIES SHALL BE PROVIDED TO ARTCULATED MASONRY JOINTS

TIMBER FRAMEWORK SHALL COMPLY WTH H1D6 OF NCC, AS1684 & SECTION 6 (PARTS 6.1-6.3) OF THE AUSTRALIAN BUILDING CODES BOARD (ABCB) HOUSING PROVISIONS

STEEL FRAMING SHALL BE IN ACCORDANCE WITH MANUFACTURER'S RECOMMENDATION & H1D6 OF NCC & SECTION 6 (PARTS 6.16.3) OF THE AUSTRALIAN BUILDING CODES BOARD (ABCB) HOUSING PROVISIONS

ALL ROOF CLADDING & WALL CLADDING SHALL COMPLY WITH H1D7 & H2D6 OF NCC & SECTION 7 (PARTS 7.1-7.5) OF THE AUSTRALIAN BUILDING CODES BOARD (ABCB) HOUSING PROVISIONS. & BE INSTALLED IN ACCORDANCE WITH MANUFACTURER'S RECOMMENDATIONS

ALL GLAZING SHALL COMPLY WITH H1D8 & H2D7. OF NCC & SECTION 8 (PARTS 8.1-8.4) OF THE AUSTRALIAN BUILDING CODES BOARD (ABCB) HOUSING PROVISIONS

A CLASS 1 BUILDING CONSTRUCTED IN A FLOOD HAZARD AREA SHALL COMPLY WITHH1P2 & H1D10 OF NCC & CONSTRUCTED IN ACCORDANCE WITH THE AUSTRALIAN BUILDING CODES BOARD (ABCB) ST&ARD FOR CONSTRUCTION OF BUILDINGS IN FLOOD HAZARD AREAS

ATTACHMENT OF FRAMED DECKS & BALCONIES TO EXTERNAL WALLS OF BUILDINGS USING A WALING PLATE SHALL BE IN ACCORDANCE WITH H1D11 OF NCC & SECTION 12 (PART 12.3) OF THE AUSTRALIAN BUILDING CODES BOARD (ABCB) HOUSING PROVISIONS

PILED FOOTINGS TO BE IN ACCORDANCE WITH H1D12 OF NCC & IN ACCORDANCE WITH ENGINEERS SPECIFICATIONS.

PART H2 DAMP & WEATHERPROOFING:

RAINWATER MANAGEMENT, INCL. SURFACE WATER SHALL COMPLY WITH PART H2P1 OF NCC

WEATHERPROOFING OF A BUILDING SHALL COMPLY WITH PART H2P2 OF NCC

RIISING DAMP SHALL COMPLY WITH PART H2P3 OF NCC & PART NSW H2P3(1) & (2).

DRAINAGE FOR SWIMMING POOLS SHALL COMPLY WITH PART H2P4 OF NCC

DRAINAGE SHALL BE DESIGNED & CONSTRUCTED IN ACCORDANCE WTH PART H2D2 OF NCC & SECTION 3 (PART 3.3) OF THE AUSTRALIAN BUILDING CODES BOARD (ABCB) HOUSING PROVISIONS

SUBFLOOR VENTILATION TO BE IN ACCORDANCE WITH H2D5 & H2P3 OF NCC & SECTION 5 (PART 5.7) & SECTION 6 (PART 6.2) OF THE AUSTRALIAN BUILDING CODES BOARD (ABCB) HOUSING PROVISIONS. EXTERNAL WATERPROOFING FOR ROOFING SYSTEMS ON FLAT ROOFS, ROOF TERRACES, BALCONIES & TERRACES & OTHER SIMILAR HORIZONTAL SURFACES LOCATED ABOVE INTERNAL SPACES OF A BUILDING SHALL COMPLY WITH H2D8 OF NCC

PART H3 FIRE SAFETY:

A CLASS 1 BUILDING MUST BE PROTECTED FROM THE SPREAD OF FIRE IN ACCORDANCE WITHH3P1 OF NCC

ALL OCCUPANTS OF A CLASS 1 BUILDING MUST BE PROVIDED WITH AUTOMATIC WARNING ON THE DETECTION OF SMOKE IN ACCORDANCE WITH H3P2.

CLASS 1 & 10 BUILDINGS WITHIN THE BUSHFIRE ZONE MUST BE CONSTRUCTED WITH MATERIALS CONTAINING FIRE HAZARD PROPERTIES & NON-COMBUSTIBLE ELEMENTS IN ACCORDANCE WITH H3D2 OF NCC

FIRE SEPARATION OF EXTERNAL WALLS MUST COMPLY WITH H3D3 OF NCC & PART 9.2 OF THE AUSTRALIAN BUILDING CODES BOARD (ABCB) HOUSING PROVISIONS.

FIRE PROTECTION OF SEPARATING WALLS & FLOORS MUST COMPLY WITH H3D4 OF NCC & PART 9.3 OF THE AUSTRALIAN BUILDING CODES BOARD (ABCB) HOUSING PROVISIONS. FIRE SEPARATION OF GARAGE-TOP DWELLINGS MUST COMPLY WITH H3D5 & NSWH3D5 OF NCC & SECTION 9 (PARTS 9.3 & 9.4) OF THE AUSTRALIAN BUILDING CODES BOARD (ABCB) HOUSING PROVISIONS.

SMOKE ALARMS & EVACUATION LIGHTING TO BE INSTALLED IN ACCORDANCE WITHH3D6 OF NCC & SECTION 9 (PART 9.5) OF THE AUSTRALIAN BUILDING CODES BOARD (ABCB) HOUSING PROVISIONS.

PART H4 HEALTH & AMENITY:

WET AREAS TO BE CONSTRUCTED & WEATHERPROOFED IN ACCORDANCE WITH H4D2, H2P1 & H2D8 OF NCC & SECTION 10 (PART 10.2) OF THE AUSTRALIAN BUILDING CODES BOARD (ABCB) HOUSING PROVISIONS.

MATERIALS & INSTALLATION OF WET AREA COMPONENTS & SYSTEMS MUST COMPLY WITH H4D3 OF NCC & SECTION 10 (PART 10.2) OF THE AUSTRALIAN BUILDING CODES BOARD (ABCB) HOUSING PROVISIONS.

ROOM HEIGHTS ARE TO BE CONSTRUCTED IN ACCORDANCE WITH H4D4 & H4P2 OF NCC & SECTION 10 (PART 10.3) OF THE AUSTRALIAN BUILDING CODES BOARD (ABCB) HOUSING PROVISIONS.

HEALTH & AMENITY FACILITIES ARE TO BE CONSTRUCTED IN ACCORDANCE WITHH4D5 & H4P3 OF NCC & SECTION 10 (PART 10.4) OF THE AUSTRALIAN BUILDING CODES BOARD (ABCB) HOUSING PROVISIONS.

LIGHT SHALL COMPLY WITH H4D6 & H4P4 OF NCC & SECTION 10 (PART 10.5) OF THE AUSTRALIAN BUILDING CODES BOARD (ABCB) HOUSING PROVISIONS.

ARTIFICIAL LIGHTING IS TO BE INSTALLED IN ACCORDANCE WITHH4D6 OF NCC & SECTION 10 PART 10.5.2 TO ANY SANITARY COMPARTMENT, BATHROOM, SHOWER ROOM, AIRLOCK & LAUNDRIES IF NATURAL LIGHTING IN ACCORDANCE WITH THE RELEVANT PROVISIONS OF PART 10.5.1 IS NOT AVAILABLE

VENTILATION IS TO BE INSTALLED IN ACCORDANCE WITH H4D7 & H4P5 OF NCC & SECTION 10 (PART 10.6) OF THE AUSTRALIAN BUILDING CODES BOARD (ABCB) HOUSING PROVISIONS. & INSTALLED TO MANUFACTURERS SPECIFICATIONS

SOUND INSULATION IS TO BE INSTALLED IN ACCORDANCE WITH H4D8 & H4P6 OF NCC & SECTION 10 (PART 10.7) OF THE AUSTRALIAN BUILDING CODES BOARD (ABCB) HOUSING PROVISIONS. & INSTALLED TO MANUFACTURERS SPECIFICATIONS

CONDENSATION & WATER VAPOUR MANAGEMENT SHALL COMPLY WITH H4D9 & H4P7 OF NCC & SECTION 10 (PART 10.8) OF THE AUSTRALIAN BUILDING CODES BOARD (ABCB) HOUSING PROVISIONS.

PART H5 SAFE MOVEMENT & ACCESS:

CLASS 1 & 10 BUILDINGS MUST BE CONSTRUCTED IN ACCORDANCE WITHH5P1 OF NCC

STAIRWAYS & RAMPS MUST BE CONSTRUCTED IN ACCORDANCE WITH H5D2 OF NCC & SECTION 11 (PART 11.2) OF THE AUSTRALIAN BUILDING CODES BOARD (ABCB) HOUSING PROVISIONS.

BARRIERS & H&RAILS MUST BE INSTALLED IN ACCORDANCE WITH H5D3 & H5P2 OF NCC & SECTION 11 (PART 11.3) OF THE AUSTRALIAN BUILDING CODES BOARD (ABCB) HOUSING PROVISIONS.

PART H6 ENERGY EFFICIENCY

THERMAL PERFORMANCE OF A CLASS 1 & 10 BUILDING SHALL COMPLY WITH H6D2 & H6P1 OF NCC & SECTION 13 (PARTS 13.213.5) OF THE AUSTRALIAN BUILDING CODES BOARD (ABCB) HOUSING PROVISIONS.

THE ENERGY VALUE &/OR USAGE OF A BUILDING'S DOMESTIC SERVICES MUST COMPLY WITH H6D2 & H6P2 OF NCC & SECTION

13 (PARTS 13.6-13.7) OF THE AUSTRALIAN BUILDING CODES BOARD (ABCB) HOUSING PROVISIONS.

PART H7 ANCILLARY PROVISIONS & ADDITIONAL CONSTRUCTION REQUIREMENTS

SWIMMING POOLS, INCLUDING POOL DEPTHS, SAFETY BARRIERS & WATER RETICULATION SYSTEMS MUST BE INSTALLED IN ACCORDANCE WITH H7D2 & NSWH7D2(1) & H7P1. & H7P2 OF NCC. SWIMMING POOL DRAINAGE IS TO COMPLY WITH H2P4 OF NCC

ALL CLASS 1 & 10 BUILDINGS LOCATED IN ALPINE AREAS MUST COMPLY WITHH7D3 & H7P4 OF NCC & SECTION 12 (PART 12.2) OF THE AUSTRALIAN BUILDING CODES BOARD (ABCB) HOUSING PROVISIONS.

ALL CLASS 1 & 10 BUILDINGS LOCATED IN BUSHFIRE PRONE AREAS MUST COMPLY WITHH7D4 & NSWH7D4 & H7P5

A PRIVATE BUSHFIRE SHELTER IS TO BE CONSTRUCTED IN ACCORDANCE WITH H7P6 OF NCC FOR CLASS 10C BUILDINGS LOCATED IN A BUSHFIRE PRONE AREA ONLY

HEATING APPLIANCES, FIREPLACES, CHIMNEYS & FLUES ARE TO BE INSTALLED IN ACCORDANCE WITH H7D5 & H7P3 & SECTION 12 (PART 12.4) OF THE AUSTRALIAN BUILDING CODES BOARD (ABCB HOUSING PROVISIONS.

GENERAL

TERMITE PROTECTION WILL BE IN ACCORDANCE WITH PART 3.4 OF THE ABCB HOUSING PROVISIONS AND AS3660.1

DRIVEWAY WILL COMPLY WITH AS2890.1:2004

PART 10.8 CONDENSATION REQUIREMENTS

LOCATION	VENTILATION REQUIREMENT (mm²)	PROPOSED METHOD
RIDGE LINE	89,2000mm² (17.84 X 5,000mm²/m	RIDGE VENTILATION
EAVE	124,880mm² (17.84 X 7,000mm²/m	AIR FLOW FASCIA
KITCHEN EXHAUST FAN	MINIMUM FLOW 40 L/S	DUCTED OUTSIDE
BATHROOM/WC EXHAUST FAN	MINIMUM FLOW 25 L/S	DUCTED OUTSIDE
PLIABLE MEMBRANE OR SARKING	VAPOUR PERMEANCE 1.14 ug/N.s (CLIMATE ZONE 6,7,8)	

SIGNATURES

	/	/
OWNER	DATE	
	/	/
OWNER	DATE	
	/	/
BUILDER	DATE	

© COPYRIGHT-THIS DRAWING REMAINS THE PROPERTY OF G.J GARDNER HOMES & IS PROVIDED FOR THE USE AS DESCRIBED & MAY NOT BE USED OR REPRODUCED IN WHOLE OR IN PART WITH OUT THE WRITTEN PERMISSION. ANY L&SCAPING (WHEN SHOWN) ARE FOR ILLUSTRATIVE PURPOSES ONLY & DO NOT FORM PART OF ANY CONTRACT

G.J. Gardner. HOMES G.J. GARDNER ORANGE Construct Homes Orange Pty Ltd A.B.N: 19 622 460 119 License: 317706C PO Box 8015, Orange East, NSW, 2800 P: (02) 6360 3988 W: www.gjgardner.com.au E: orange@gjgardner.com.au	ROBINA 125 CLASSIC © COPYRIGHT EXCLUSIVE TO G.J.GARDNER HOMES	TONY JAMES DESIGN PTY LTD A.B.N: 96 486 946 536 Q.B.C.C License: 10632`7 V.B.A License: DP-AD-44789 M: 0412 832 646 P: (07) 5665 9230 E: anthony@tonyjames.com.au W: www.tonyjames.com.au	CLIENT: SARAH KENNEDY DRAWING TITLE: NCC REQUIREMENTS	PROJECT: PROPOSED NEW RESIDENCE LOT 217 DP 1305914 47 HAWKE LANE ORANGE NSW 2800	PAGES: 02 OF 15	SHEET SIZE: A3	FLOOR AREAS:	REV: 1	DETAILS: PRELIMINARY ISSUE 1	DATE: 02/12/2025
								2	PRELIMINARY ISSUE	16/12/2025
					JOB NO: 40283			A	CONSTRUCTION ISSUE	03/03/2026
					DRAWN: TJ			B	CONSTRUCTION ISSUE	06/03/2026
					DATE: 02/12/2025					

A PRELIMINARY SURVEY HAS BEEN MADE OF THE BOUNDARIES AND MAY BE SUBJECT TO FURTHER INVESTIGATION

NOTES:

- BOUNDARY DIMENSIONS AND BEARINGS BASED ON CURRENT TITLE INFORMATION.
- SITE AREA CALCULATED FROM CURRENT TITLE DIMENSIONS.
- LOT BOUNDARIES HAVE BEEN RE-ESTABLISHED FOR PLOTTING PURPOSES ONLY. NO PHYSICAL MARKING OF THE BOUNDARIES HAS BEEN UNDERTAKEN.
- ONLY VISIBLE SERVICES HAVE BEEN LOCATED. NO INVESTIGATION OF UNDERGROUND SERVICES HAS BEEN MADE. RELEVANT AUTHORITIES ARE TO BE NOTIFIED PRIOR TO ANY DEVELOPMENT.
- CONTOURS ARE INDICATIVE OF GROUND FORM ONLY. ONLY SPOT LEVELS SHOULD BE USED FOR CALCULATIONS OF QUANTITIES WITH CAUTION.
- CONTOUR INTERVAL 0.2m MINOR 1.0m MAJOR.
- ORIGIN OF LEVELS: SSM 202244 RL 927.31 AHD (SCIMS SKETCH 15/09/2023).



LEGEND


BM - BENCH MARK
EBOX - ELECTRICITY BOX
HYD - HYDRANT
LP - LIGHT POLE
NBN - NATIONAL BROADBAND NETWORK
SJ - SEWER JUNCTION
WS - WATER SERVICE

(SI) EASEMENT TO DRAIN SEWAGE 3 WIDE (DP1305914)
(DF) EASEMENT TO DRAIN WATER 3 WIDE (DP1305914)

SEE DEED AND DP1305914 FOR RESTRICTIONS ON THE

HAWKE LANE

SUNDOWNER STREET

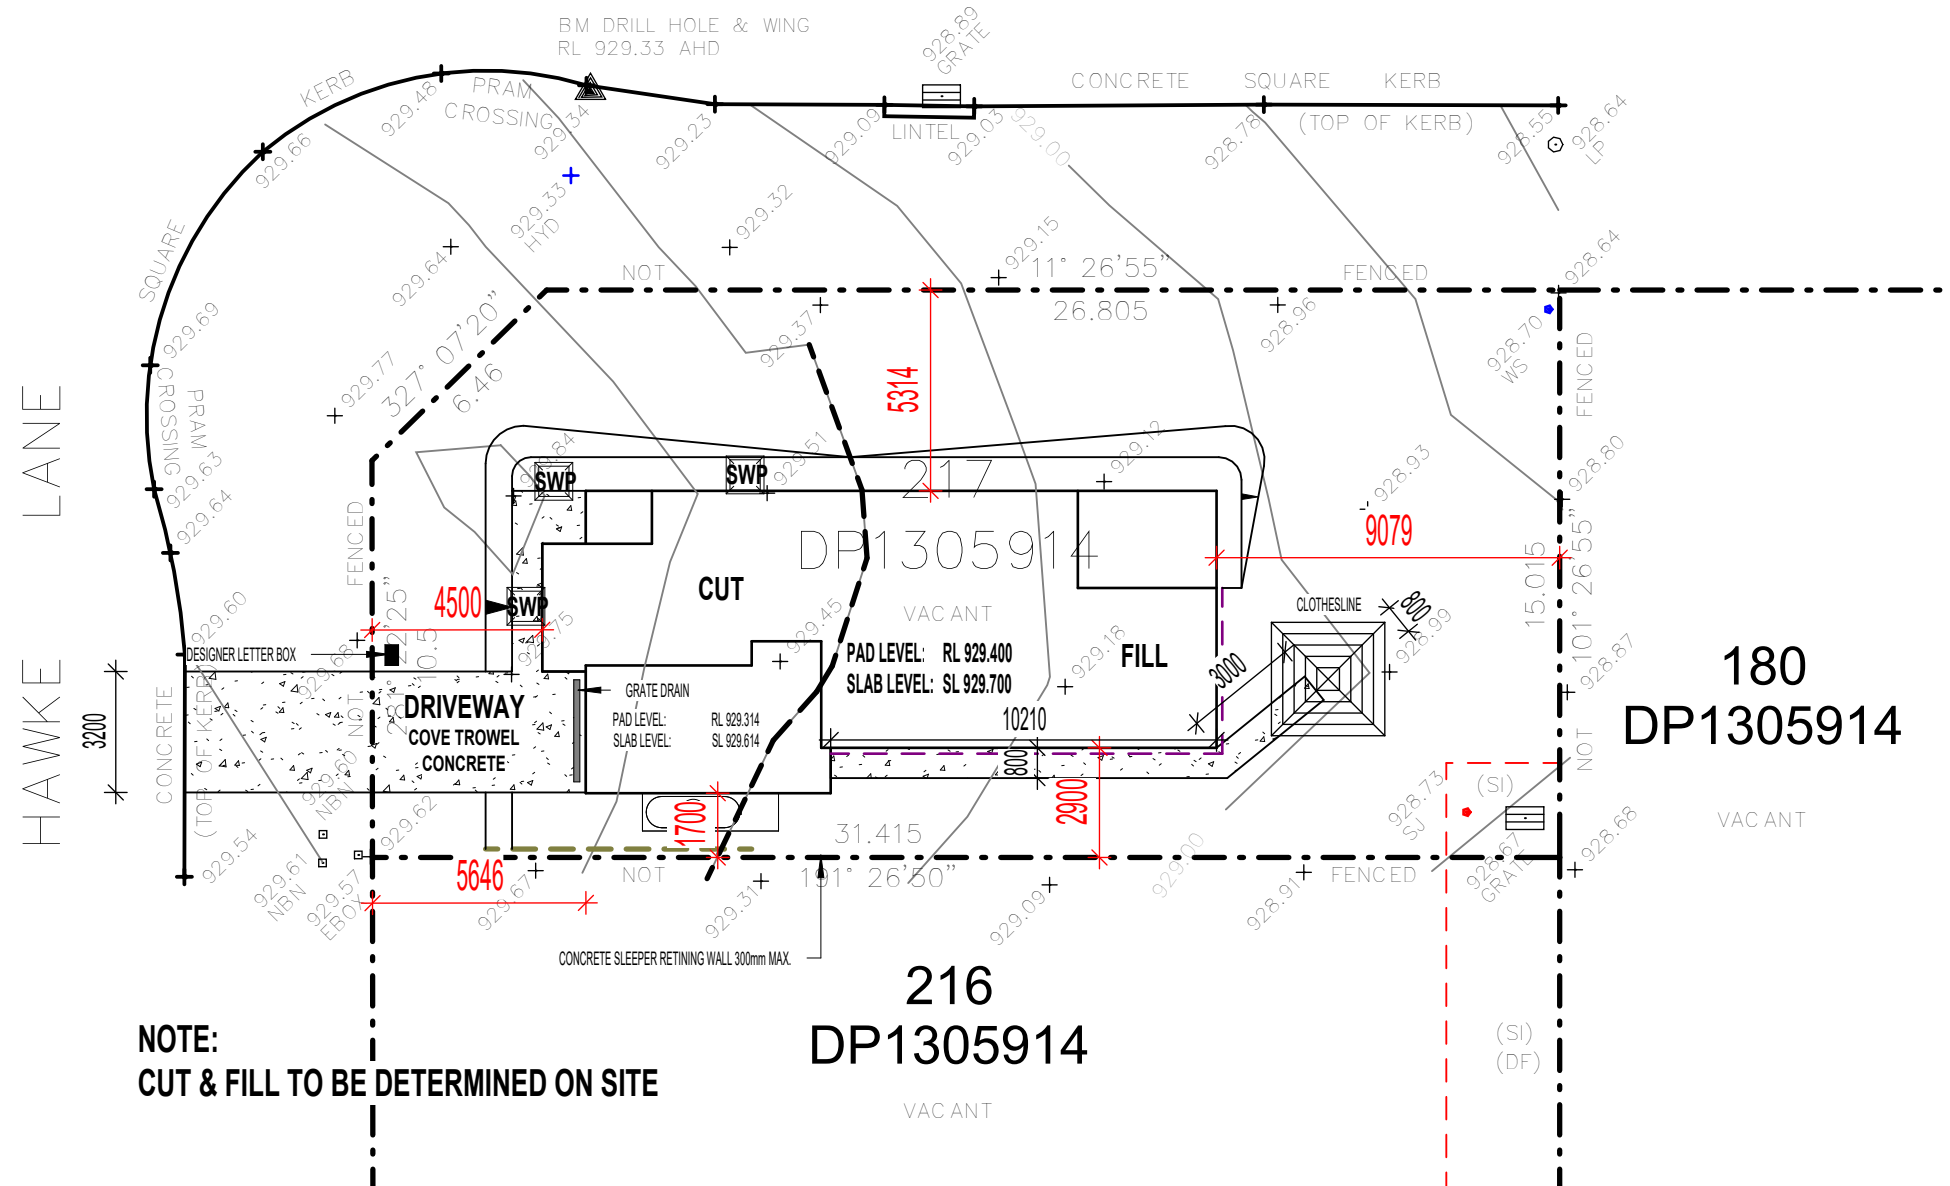

SITE PLAN
1 : 200


SITE INFORMATION

LOT - 217
DP - 1305914
SITE AREA - 461.4m²
SITE COVER - 27.31%

SIGNATURES

OWNER	DATE
OWNER	DATE
BUILDER	DATE

NOTE:
MONUMENT ROOF OR DARKER SA.0.73

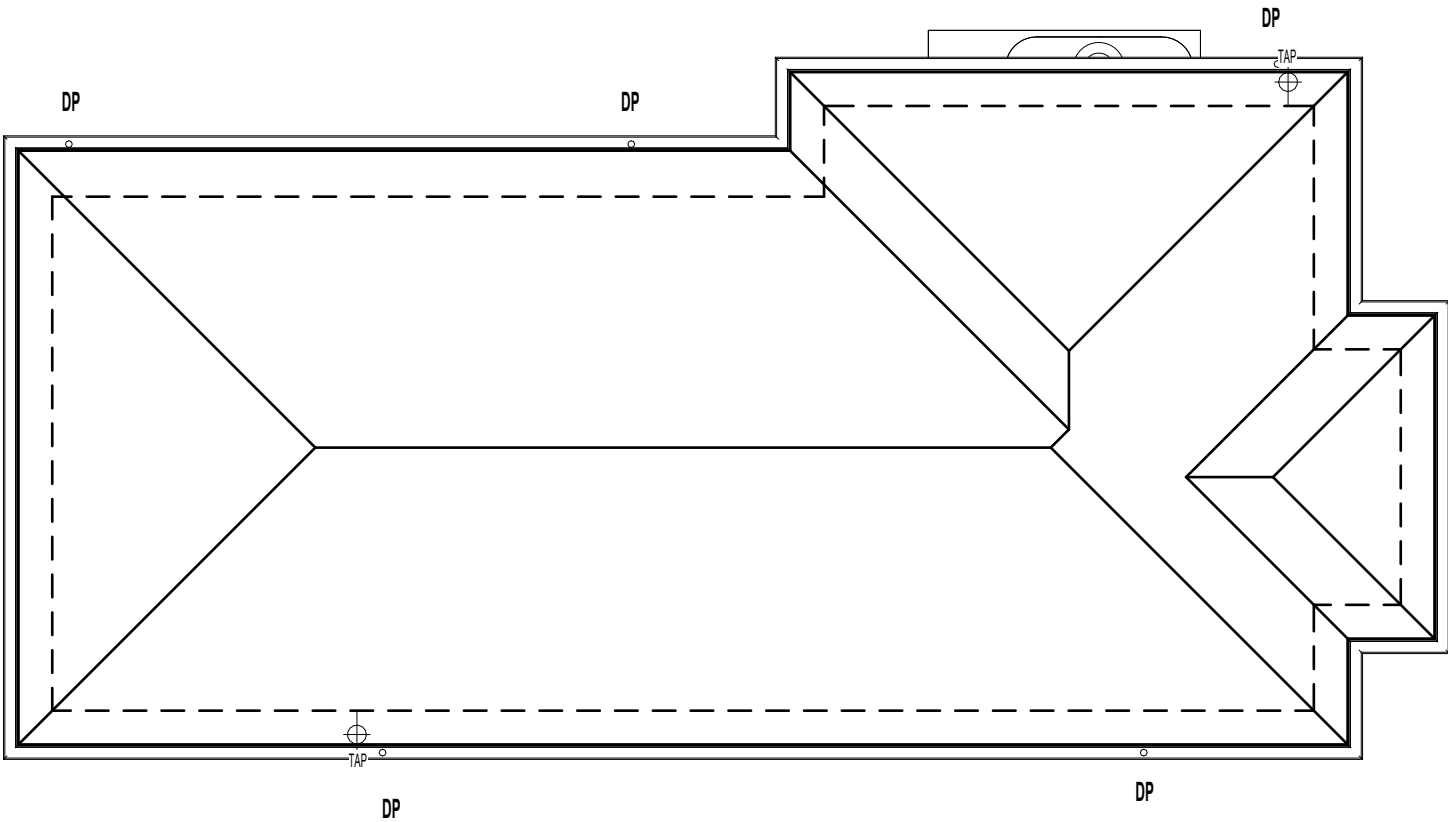

ROOF PLAN
1 : 100

SIGNATURES


		/	/
OWNER		DATE	
		/	/
OWNER		DATE	
		/	/
BUILDER		DATE	

© COPYRIGHT-THIS DRAWING REMAINS THE PROPERTY OF G.J GARDNER HOMES & IS PROVIDED FOR THE USE AS DESCRIBED & MAY NOT BE USED OR REPRODUCED IN WHOLE OR IN PART WITH OUT THE WRITTEN PERMISSION. ANY LANDSCAPING (WHEN SHOWN) ARE FOR ILLUSTRATIVE PURPOSES ONLY AND DO NOT FORM PART OF ANY CONTRACT

G.J. Gardner. HOMES G.J. GÄRDNER ORANGE Construct Homes Orange Pty Ltd A.B.N: 19 622 460 119 License: 317706C PO Box 8015, Orange East, NSW, 2800 P: (02) 6360 3988 W: www.gjgardner.com.au E: orange@gjgardner.com.au	ROBINA 125 CLASSIC © COPYRIGHT EXCLUSIVE TO G.J.GARDNER HOMES	TONY JAMES DESIGN PTY LTD A.B.N: 96 486 946 536 Q.B.C.C License: 106327 V.B.A License: DP-AD-44789 M: 0412 832 646 P: (07) 5665 9230 E: anthony@tonyjames.com.au W: www.tonyjames.com.au	CLIENT: SARAH KENNEDY DRAWING TITLE: ROOF PLAN	PROJECT: PROPOSED NEW RESIDENCE LOT 217 DP 1305914 47 HAWKE LANE ORANGE NSW 2800	PAGES: 05 OF 15	SHEET SIZE: A3	FLOOR AREAS:	REV: 1 2 A B	DETAILS: PRELIMINARY ISSUE 1 PRELIMINARY ISSUE CONSTRUCTION ISSUE CONSTRUCTION ISSUE	DATE: 02/12/2025 16/12/2025 03/03/2026 06/03/2026
					JOB NO: 40283					
					DRAWN: TJ					
					DATE: 02/12/2025					

CONCRETE SETOUT PLAN

1 : 100

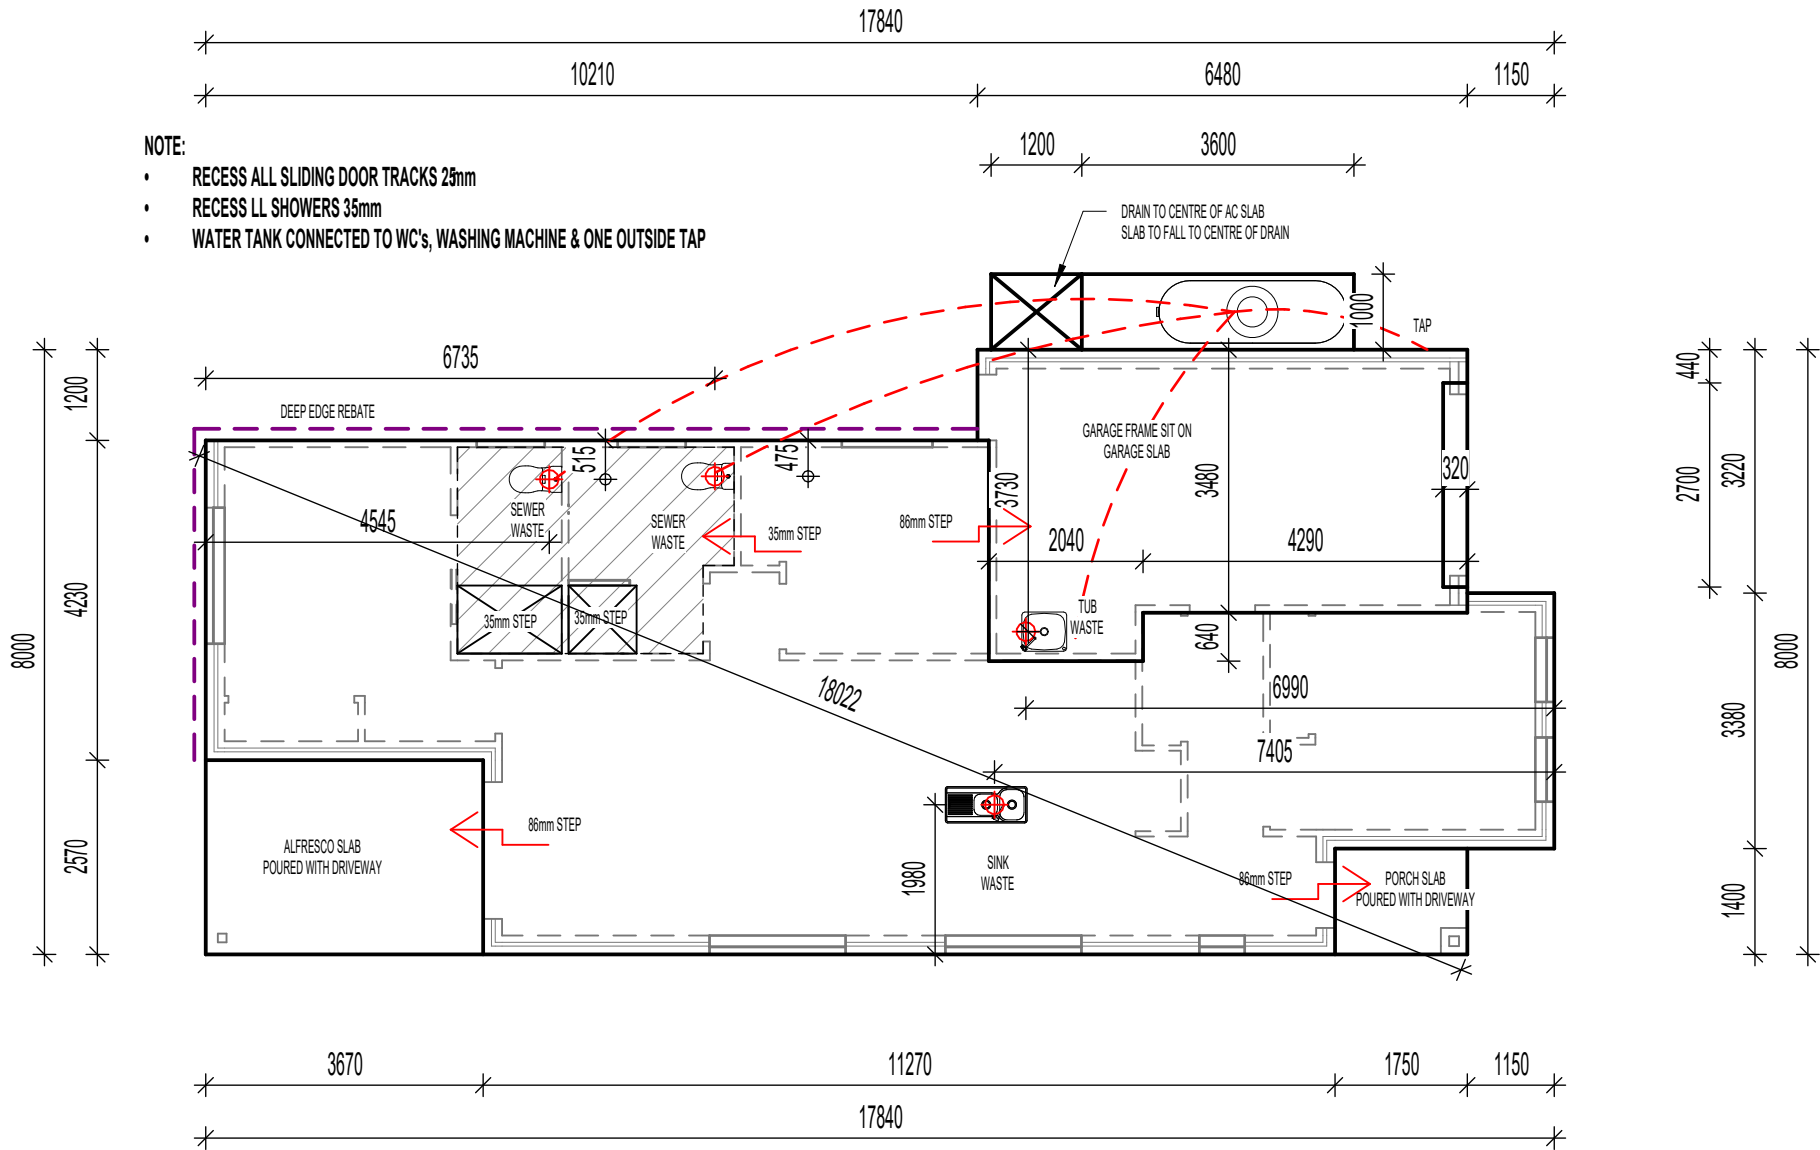

SIGNATURES

		/	/
OWNER		DATE	
		/	/
OWNER		DATE	
		/	/
BUILDER		DATE	

© COPYRIGHT-THIS DRAWING REMAINS THE PROPERTY OF G.J GARDNER HOMES & IS PROVIDED FOR THE USE AS DESCRIBED & MAY NOT BE USED OR REPRODUCED IN WHOLE OR IN PART WITH OUT THE WRITTEN PERMISSION. ANY LANDSCAPING (WHEN SHOWN) ARE FOR ILLUSTRATIVE PURPOSES ONLY AND DO NOT FORM PART OF ANY CONTRACT

G.J. Gardner.

HOMES

G.J. GARDNER ORANGE

Construct Homes Orange Pty Ltd

A.B.N: 19 622 460 119 License: 317706C

PO Box 8015, Orange East, NSW, 2800

P: (02) 6360 3988 W: www.gjgardner.com.au

E: orange@gjgardner.com.au

ROBINA 125

CLASSIC

© COPYRIGHT EXCLUSIVE
TO G.J.GARDNER HOMES

TONY JAMES DESIGN PTY LTD

A.B.N: 96 486 946 536

Q.B.C.C License: 106327

V.B.A License: DP-AD-44789

M: 0412 832 646

P: (07) 5665 9230

E: anthony@tonyjames.com.au

W: www.tonyjames.com.au

CLIENT:

SARAH KENNEDY

DRAWING TITLE:

CONCRETE SETOUT PLAN

PROJECT: PROPOSED NEW RESIDENCE

LOT 217 DP 1305914

47 HAWKE LANE

ORANGE NSW 2800

PAGES: 06 OF 15

SHEET SIZE: A3

JOB NO: 40283

DRAWN: TJ

DATE: 02/12/2025

FLOOR AREAS:

GROUND FLOOR 90.74 m²

GARAGE 22.54 m²

ALFRESCO 9.43 m²

PORCH 2.45 m²

125.16 m²

REV:	DETAILS:	DATE:
1	PRELIMINARY ISSUE 1	02/12/2025
2	PRELIMINARY ISSUE	16/12/2025
A	CONSTRUCTION ISSUE	03/03/2026
B	CONSTRUCTION ISSUE	06/03/2026

ELECTRICAL LEGEND

- 

DOUBLE GPO - 18
- WP



WATER PROOF DOUBLE GPO - 1
- P



CEILING MOUNTED PENDANT LIGHT - 0
- 


CEILING MOUNTED LIGHT - 0
- 

SINGLE GPO - 5
- WP



WATERPROOF SINGLE GPO - 1
- 

LED LIGHTS - 15
- 

 EXTRACTION FAN - DUCTED TO EAVE - 0
- 

DOUBLE TUBE-FLURO LIGHT - 1
- 

HARD WIRED SMOKE ALARM - 3
- 

TELEVISION POINT - 2
- PAY



PAY TV POINT - 1
- 

TELEPHONE POINT - 0
- 

HEAT / LIGHT / FAN - 2 DUCTED TO EAVE
- 

DATA POINT - 1
- B



EXTERNAL UP / DOWN LIGHTS - 1
- 

SPOT LIGHT - 2
- AC




AC OUTLET - 7
- 

1200mm CEILING FAN - 1
- 

1200mm CEILING FAN WITH LIGHT - 3
- 

NBN PROVISION & DOUBLE GPO - 1
- 2 WAY SWITCHES - 2
- 3 WAY SWITCHES - 0

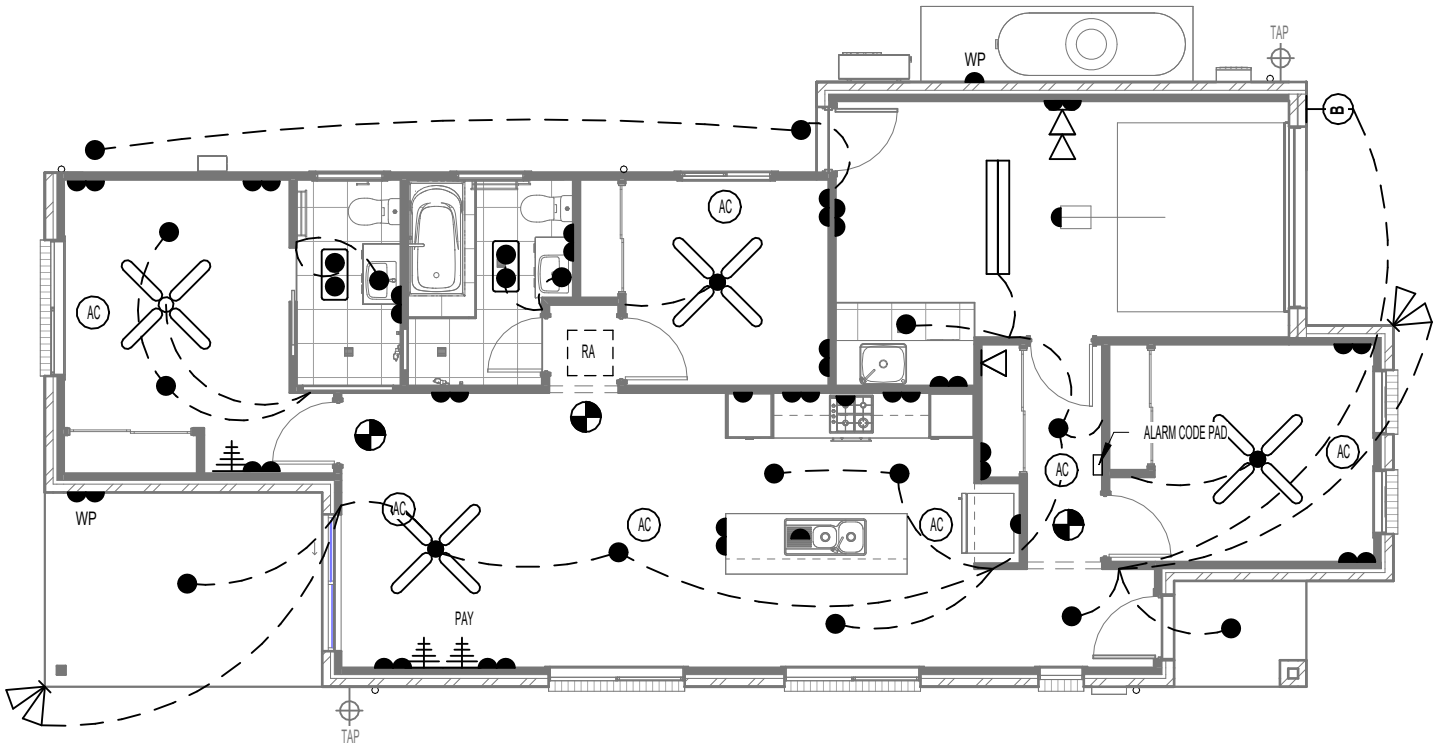

DUCTED AC SYSTEM

1 X ZONED DAIKIN FDYAN100AV1 10.0 / 12.5KW SINGLE PHASE (EER 3.23C/3.57H)
STANDARD INVERTER SYSTEM IN A DAY 6.0KW / NIGHT 4.7KW OPERATING SITUATION. THE SYSTEM TO BE DUCTED USING R1.0 FLEXIBLE POLYMER DUCTWORK UP TO 7 X CEILING OUTLET GRILLES WITH THE ADDITION OF 1 X RETURN AIR GRILLE IN THE HALLWAY CEILING OUTSIDE THE BATHROOM. THE DUCTED SYSTEM TO HAVE 1 X AIRTOUCH2+ WIFI COMPATIBLE WALL CONTROLLER AND TO BE ZONED USING CLOSABLE ZONE MOTORS & BARRELS AS FOLLOWS:-
ZONE 1 CLOSABLE:- KITCHEN/DINING/LIVING (6.0KW)
ZONE 2 CLOSABLE:- BEDROOM 1 (1.9KW)
ZONE 3 CLOSABLE:- BEDROOM 2 (1.6KW)
ZONE 4 CLOSABLE:- BEDROOM 3 (1.2KW)
THE ABOVE MENTIONED DUCTED SYSTEM TO THE ROBINA 125 HOUSE PLAN WITH A TOTAL AREA OF 124.8M2 REQUIRES 10.7KW OF AIR CONDITIONING IF ALL THE AREAS ARE BEING OPERATED AT ONCE, THIS SYSTEM IS DESIGNED TO HAVE 100% OF THE ZONES OPERATIONAL AT ONCE

NOTE:
LIGHT TO ROOF SPACE

ELECTRICAL PLAN

1 : 100


SIGNATURES

		/ /
OWNER	DATE	/ /
		/ /
OWNER	DATE	/ /
		/ /
BUILDER	DATE	

© COPYRIGHT-THIS DRAWING REMAINS THE PROPERTY OF G.J GARDNER HOMES & IS PROVIDED FOR THE USE AS DESCRIBED & MAY NOT BE USED OR REPRODUCED IN WHOLE OR IN PART WITH OUT THE WRITTEN PERMISSION. ANY LANDSCAPING (WHEN SHOWN) ARE FOR ILLUSTRATIVE PURPOSES ONLY AND DO NOT FORM PART OF ANY CONTRACT

G.J. Gardner. HOMES G.J. GÄRDNER ORANGE Construct Homes Orange Pty Ltd A.B.N: 19 622 460 119 License: 317706C PO Box 8015, Orange East, NSW, 2800 P: (02) 6360 3988 W: www.gjgardner.com.au E: orange@gjgardner.com.au	ROBINA 125 CLASSIC © COPYRIGHT EXCLUSIVE TO G.J.GARDNER HOMES	TONY JAMES DESIGN PTY LTD	CLIENT:	PROJECT: PROPOSED NEW RESIDENCE	PAGES: 07 OF 15	SHEET SIZE: A3	FLOOR AREAS:		REV:	DETAILS:	DATE:
		A.B.N: 96 486 946 536	SARAH KENNEDY	LOT 217 DP 1305914 47 HAWKE LANE ORANGE NSW 2800	GROUND FLOOR 90.74 m² GARAGE 22.54 m² ALFRESCO 9.43 m² PORCH 2.45 m² 125.16 m²	JOB NO: 40283	1	PRELIMINARY ISSUE 1	02/12/2025		
		Q.B.C.C License: 106327	DRAWING TITLE:								
		V.B.A License: DP-AD-44789	ELECTRICAL PLAN								
		M: 0412 832 646									
P: (07) 5665 9230											
E: anthony@tonyjames.com.au											
W: www.tonyjames.com.au											

G.J. Gardner. HOMES G.J. GÄRDNER ORANGE Construct Homes Orange Pty Ltd A.B.N: 19 622 460 119 License: 317706C PO Box 8015, Orange East, NSW, 2800 P: (02) 6360 3988 W: www.gjgardner.com.au E: orange@gjgardner.com.au	ROBINA 125 CLASSIC © COPYRIGHT EXCLUSIVE TO G.J.GARDNER HOMES	TONY JAMES DESIGN PTY LTD	CLIENT:	PROJECT: PROPOSED NEW RESIDENCE	PAGES: 07 OF 15	SHEET SIZE: A3	FLOOR AREAS:		REV:	DETAILS:	DATE:
		A.B.N: 96 486 946 536	SARAH KENNEDY	LOT 217 DP 1305914 47 HAWKE LANE ORANGE NSW 2800	GROUND FLOOR 90.74 m² GARAGE 22.54 m² ALFRESCO 9.43 m² PORCH 2.45 m² 125.16 m²	JOB NO: 40283	1	PRELIMINARY ISSUE 1	02/12/2025		
		Q.B.C.C License: 106327	DRAWING TITLE:								
		V.B.A License: DP-AD-44789	ELECTRICAL PLAN								
		M: 0412 832 646									
P: (07) 5665 9230											
E: anthony@tonyjames.com.au											
W: www.tonyjames.com.au											

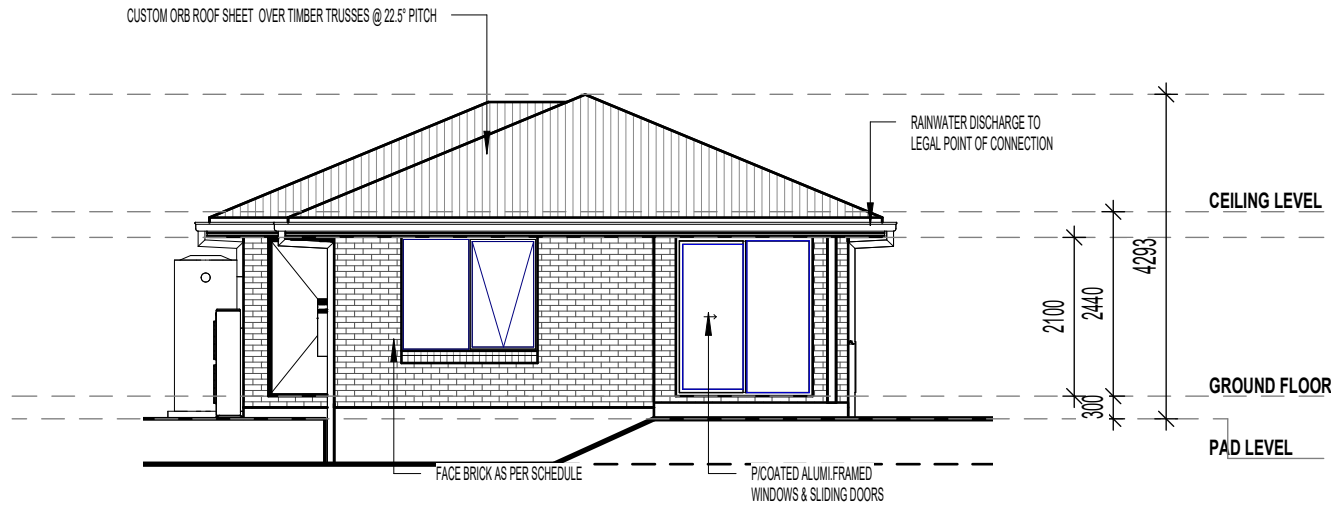

NORTHERN ELEVATION
1 : 100




EASTERN ELEVATION
1 : 100

SIGNATURES


OWNER	DATE
OWNER	DATE
BUILDER	DATE

© COPYRIGHT-THESE DRAWINGS REMAINS THE PROPERTY OF G.J. GARDNER HOMES & IS PROVIDED FOR THE USE AS DESCRIBED & MAY NOT BE USED OR REPRODUCED IN WHOLE OR IN PART WITHOUT THE WRITTEN PERMISSION. ANY LANDSCAPING (WHEN SHOWN) ARE FOR ILLUSTRATIVE PURPOSES ONLY AND DO NOT FORM PART OF ANY CONTRACT

G.J. Gardner. HOMES G.J. GARDNER ORANGE Construct Homes Orange Pty Ltd A.B.N: 19 622 460 119 License: 317706C PO Box 8015, Orange East, NSW, 2800 P: (02) 6360 3988 W: www.gjgardner.com.au E: orange@gjgardner.com.au	ROBINA 125 CLASSIC © COPYRIGHT EXCLUSIVE TO G.J.GARDNER HOMES	TONY JAMES DESIGN PTY LTD A.B.N: 96 486 946 536 Q.B.C.C License: 106327 V.B.A License: DP-AD-44789 M: 0412 832 646 P: (07) 5665 9230 E: anthony@tonyjames.com.au W: www.tonyjames.com.au	CLIENT: SARAH KENNEDY DRAWING TITLE: BUILDING ELEVATIONS	PROJECT: PROPOSED NEW RESIDENCE LOT 217 DP 1305914 47 HAWKE LANE ORANGE NSW 2800	PAGES: 08 OF 15	SHEET SIZE: A3	FLOOR AREAS: GROUND FLOOR 90.74 m ² GARAGE 22.54 m ² ALFRESCO 9.43 m ² PORCH 2.45 m ² 125.16 m²	REV: 1	DETAILS: PRELIMINARY ISSUE 1	DATE: 02/12/2025
					JOB NO: 40283			2	PRELIMINARY ISSUE	16/12/2025
					DRAWN: TJ			A	CONSTRUCTION ISSUE	03/03/2026
					DATE: 02/12/2025			B	CONSTRUCTION ISSUE	06/03/2026

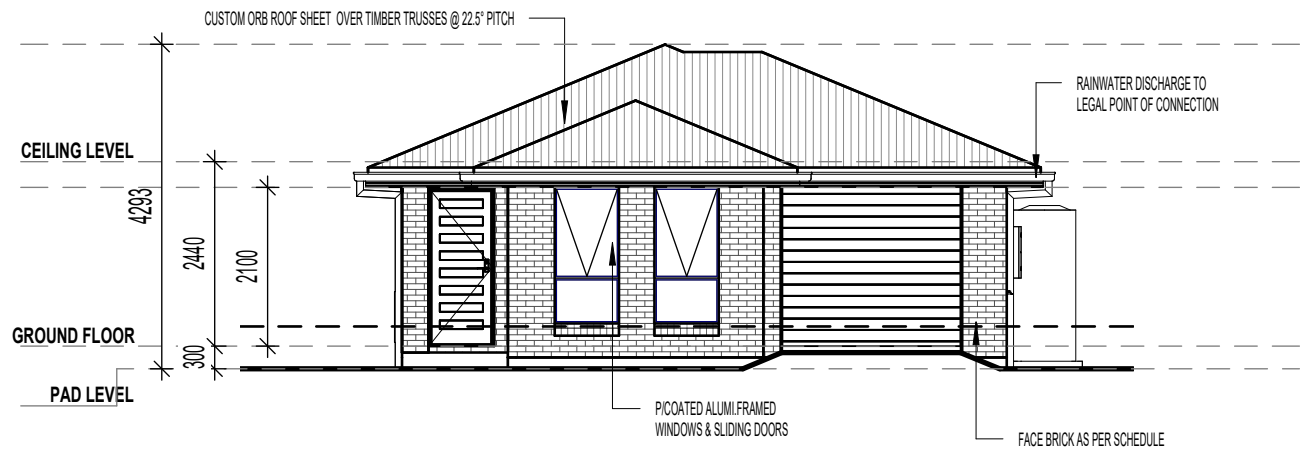

SOUTHERN ELEVATION
1 : 100

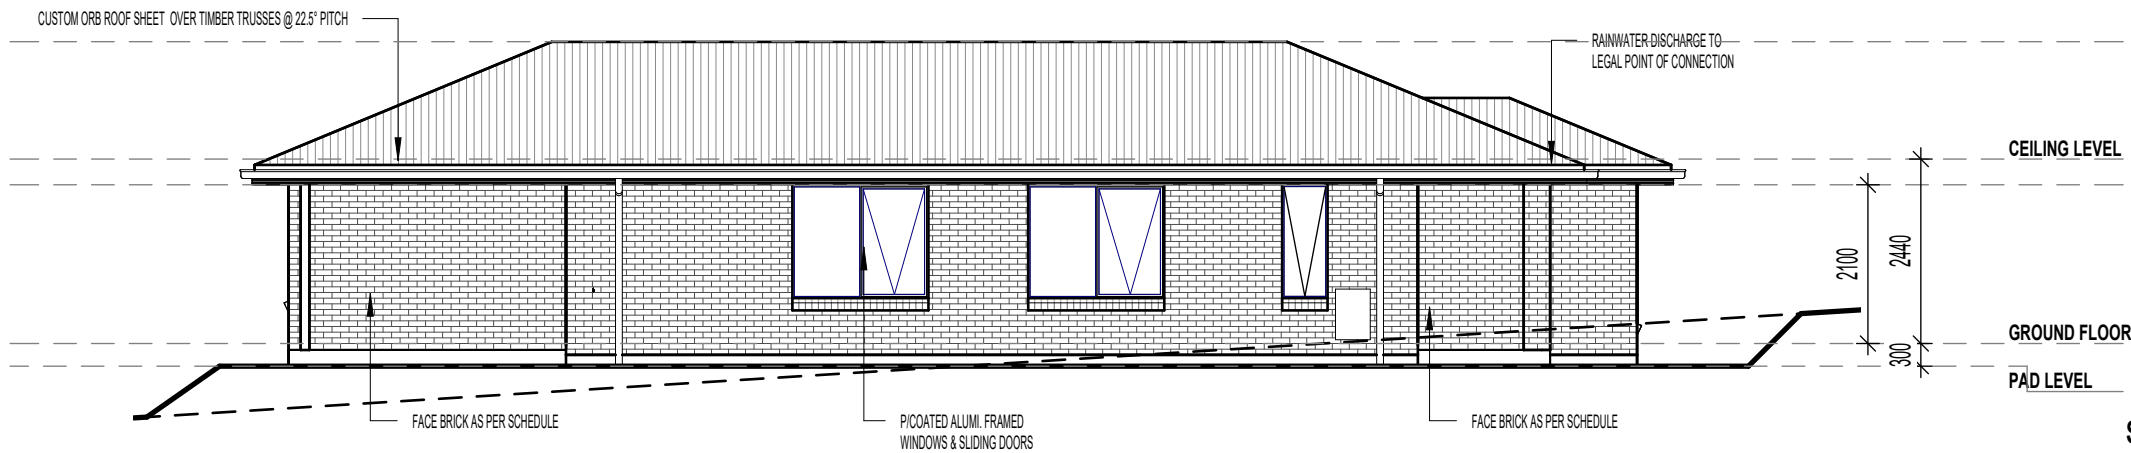

WESTERN ELEVATION
1 : 100

SIGNATURES

		/	/
OWNER		DATE	
		/	/
OWNER		DATE	
		/	/
BUILDER		DATE	

© COPYRIGHT-THESE DRAWINGS REMAINS THE PROPERTY OF G.J. GARDNER HOMES & IS PROVIDED FOR THE USE AS DESCRIBED & MAY NOT BE USED OR REPRODUCED IN WHOLE OR IN PART WITHOUT THE WRITTEN PERMISSION. ANY LANDSCAPING (WHEN SHOWN) ARE FOR ILLUSTRATIVE PURPOSES ONLY AND DO NOT FORM PART OF ANY CONTRACT

G.J. Gardner.

HOMES

G.J. GARDNER ORANGE

Construct Homes Orange Pty Ltd

A.B.N: 19 622 460 119 License: 317706C

PO Box 8015, Orange East, NSW, 2800

P: (02) 6360 3988 W: www.gjgardner.com.au

E: orange@gjgardner.com.au

ROBINA 125

CLASSIC

© COPYRIGHT EXCLUSIVE
TO G.J.GARDNER HOMES

TONY JAMES DESIGN PTY LTD

A.B.N: 96 486 946 536

Q.B.C.C License: 106327

V.B.A License: DP-AD-44789

M: 0412 832 646

P: (07) 5665 9230

E: anthony@tonyjames.com.au

W: www.tonyjames.com.au

CLIENT:

SARAH KENNEDY

DRAWING TITLE:

BUILDING ELEVATIONS

PROJECT: PROPOSED NEW RESIDENCE

LOT 217 DP 1305914

47 HAWKE LANE

ORANGE NSW 2800

PAGES: 09 OF 15

SHEET SIZE: A3

JOB NO: 40283

DRAWN: TJ

DATE: 02/12/2025

FLOOR AREAS:

GROUND FLOOR 90.74 m²


GARAGE 22.54 m²

ALFRESCO 9.43 m²

PORCH 2.45 m²

125.16 m²

REV:	DETAILS:	DATE:
1	PRELIMINARY ISSUE 1	02/12/2025
2	PRELIMINARY ISSUE	16/12/2025
A	CONSTRUCTION ISSUE	03/03/2026
B	CONSTRUCTION ISSUE	06/03/2026

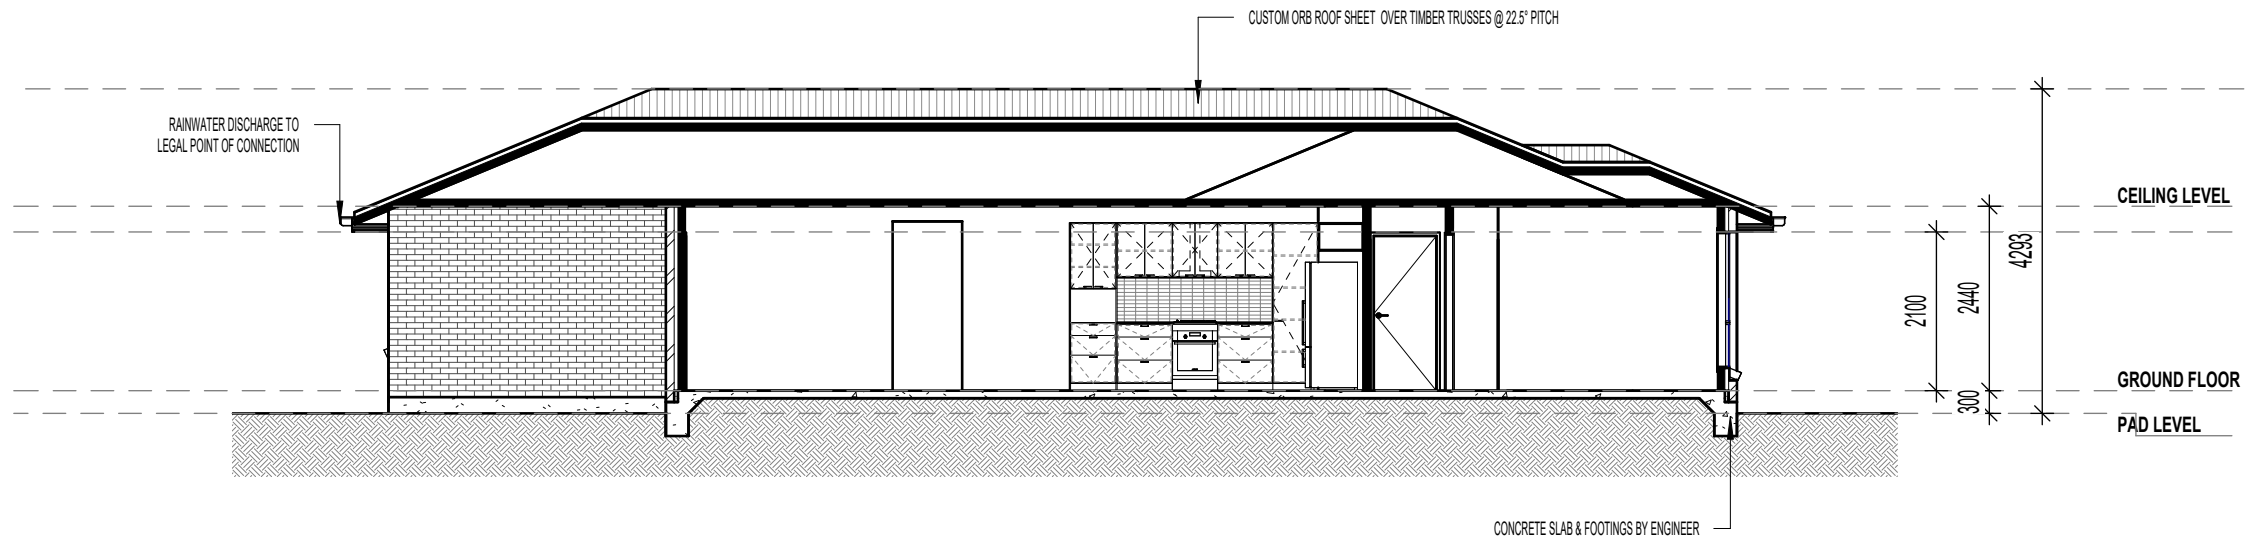

SECTION S1
1 : 100




SECTION S2
1 : 100

SIGNATURES


		/ /
OWNER	DATE	/ /
		/ /
OWNER	DATE	/ /
		/ /
BUILDER	DATE	

© COPYRIGHT-THIS DRAWING REMAINS THE PROPERTY OF G.J GARDNER HOMES & IS PROVIDED FOR THE USE AS DESCRIBED & MAY NOT BE USED OR REPRODUCED IN WHOLE OR IN PART WITH OUT THE WRITTEN PERMISSION. ANY LANDSCAPING (WHEN SHOWN) ARE FOR ILLUSTRATIVE PURPOSES ONLY AND DO NOT FORM PART OF ANY CONTRACT


G.J. Gardner. HOMES G.J. GARDNER ORANGE Construct Homes Orange Pty Ltd A.B.N: 19 622 460 119 License: 317706C PO Box 8015, Orange East, NSW, 2800 P: (02) 6360 3988 W: www.gjgardner.com.au E: orange@gjgardner.com.au	ROBINA 125 CLASSIC © COPYRIGHT EXCLUSIVE TO G.J.GARDNER HOMES	TONY JAMES DESIGN PTY LTD A.B.N: 96 486 946 536 Q.B.C.C License: 106327 V.B.A License: DP-AD-44789 M: 0412 832 646 P: (07) 5665 9230 E: anthony@tonyjames.com.au W: www.tonyjames.com.au	CLIENT: SARAH KENNEDY DRAWING TITLE: BUILDING SECTIONS	PROJECT: PROPOSED NEW RESIDENCE LOT 217 DP 1305914 47 HAWKE LANE ORANGE NSW 2800	PAGES: 10 OF 15	SHEET SIZE: A3	FLOOR AREAS: GROUND FLOOR 90.74 m ² GARAGE 22.54 m ² ALFRESCO 9.43 m ² PORCH 2.45 m ² 125.16 m²	REV: 1	DETAILS: PRELIMINARY ISSUE 1	DATE: 02/12/2025
					JOB NO: 40283			2	PRELIMINARY ISSUE	16/12/2025
					DRAWN: TJ			A	CONSTRUCTION ISSUE	03/03/2026
					DATE: 02/12/2025			B	CONSTRUCTION ISSUE	06/03/2026

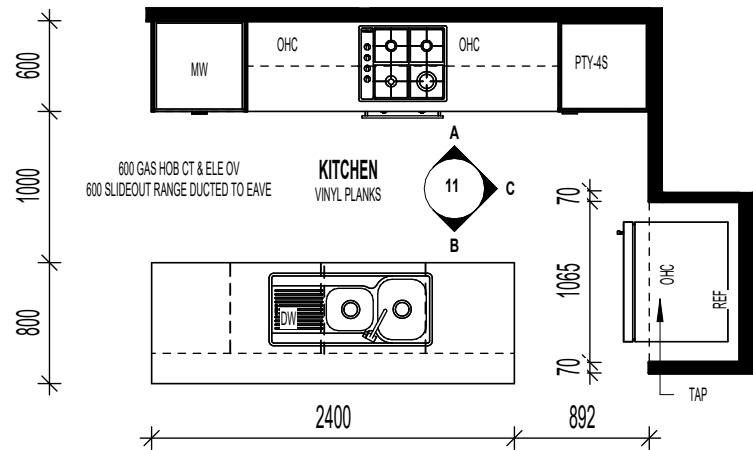


KITCHEN FLOOR PLAN
1 : 50

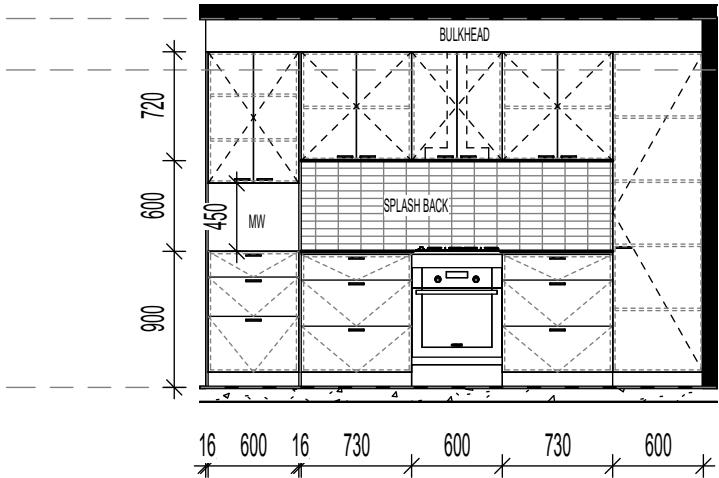


A
1 : 50

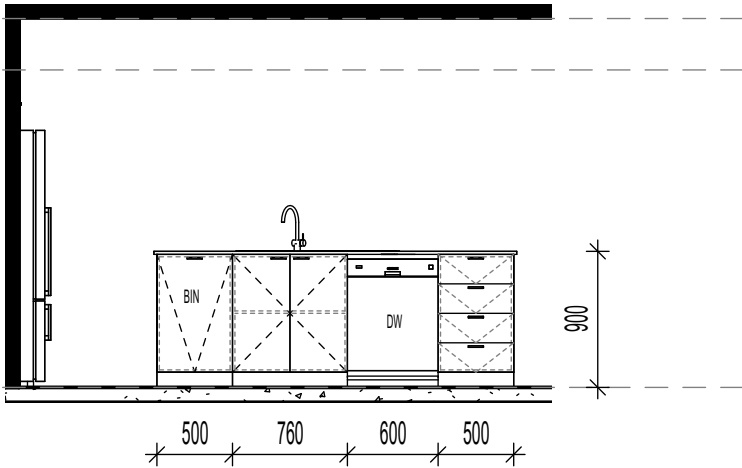

B
1 : 50

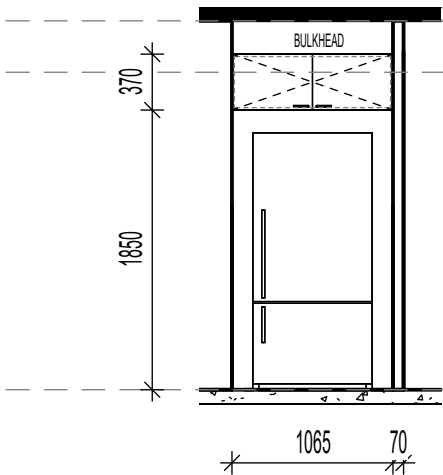

C
1 : 50

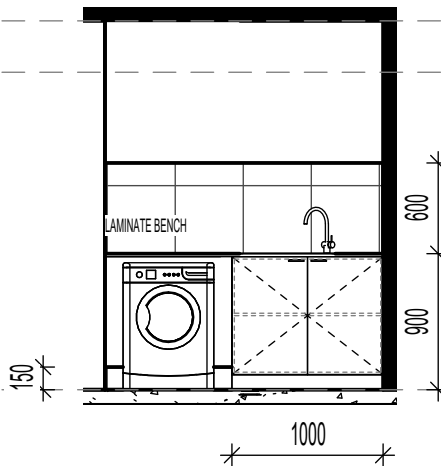

LAUNDRY
1 : 50

SIGNATURES

OWNER	/ /	DATE
OWNER	/ /	DATE
BUILDER	/ /	DATE

© COPYRIGHT-THIS DRAWING REMAINS THE PROPERTY OF G.J GARDNER HOMES & IS PROVIDED FOR THE USE AS DESCRIBED & MAY NOT BE USED OR REPRODUCED IN WHOLE OR IN PART WITH OUT THE WRITTEN PERMISSION. ANY LANDSCAPING (WHEN SHOWN) ARE FOR ILLUSTRATIVE PURPOSES ONLY AND DO NOT FORM PART OF ANY CONTRACT

G.J. Gardner.
G.J. GARDNER ORANGE
Construct Homes Orange Pty Ltd
A.B.N: 19 622 460 119 License: 317706C
PO Box 8015, Orange East, NSW, 2800
P: (02) 6360 3988 W: www.gjgardner.com.au
E: orange@gjgardner.com.au

HOMES

ROBINA 125
CLASSIC
© COPYRIGHT EXCLUSIVE
TO G.J.GARDNER HOMES

TONY JAMES DESIGN PTY LTD
A.B.N: 96 486 946 536
Q.B.C.C License: 106327
V.B.A License: DP-AD-44789
M: 0412 832 646
P: (07) 5665 9230
E: anthony@tonyjames.com.au
W: www.tonyjames.com.au


CLIENT:
SARAH KENNEDY
DRAWING TITLE:
WET AREA ELEVATIONS

PROJECT: PROPOSED NEW RESIDENCE
**LOT 217 DP 1305914
47 HAWKE LANE
ORANGE NSW 2800**







PAGES:
11 OF 15
SHEET SIZE:
A3
JOB NO: 40283
DRAWN: TJ
DATE: 02/12/2025

FLOOR AREAS:
GROUND FLOOR 90.74 m²
GARAGE 22.54 m²
ALFRESCO 9.43 m²
PORCH 2.45 m²
125.16 m²

REV:	DETAILS:	DATE:
1	PRELIMINARY ISSUE 1	02/12/2025
2	PRELIMINARY ISSUE	16/12/2025
A	CONSTRUCTION ISSUE	03/03/2026
B	CONSTRUCTION ISSUE	06/03/2026

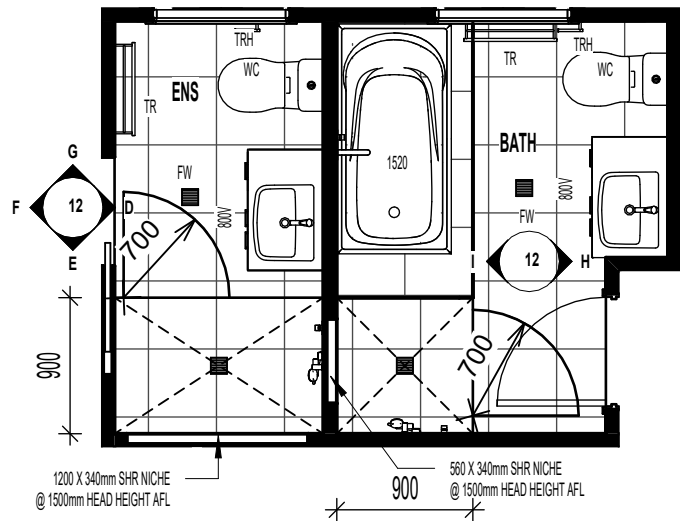


ENSUITE & BATHROOM FLOOR PLAN
1 : 50

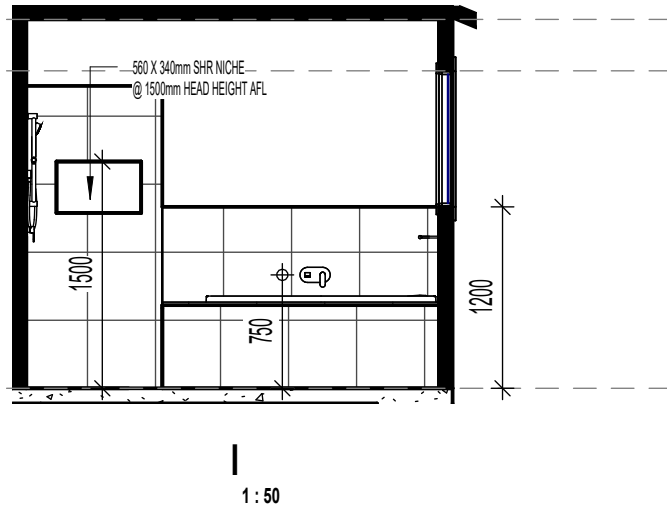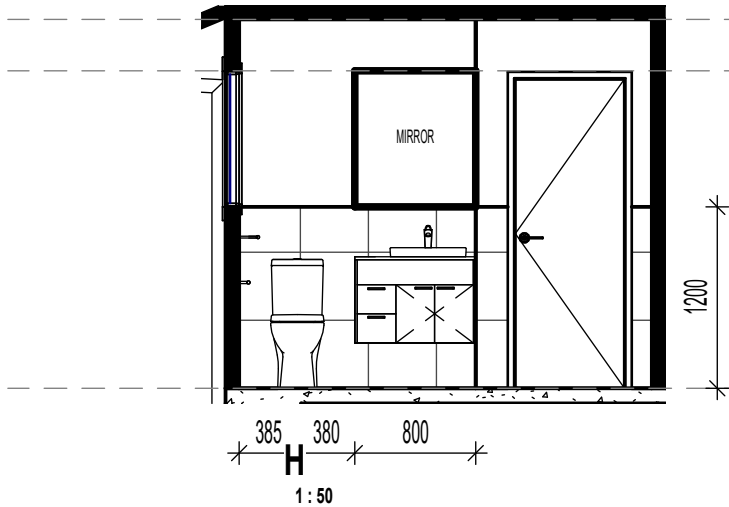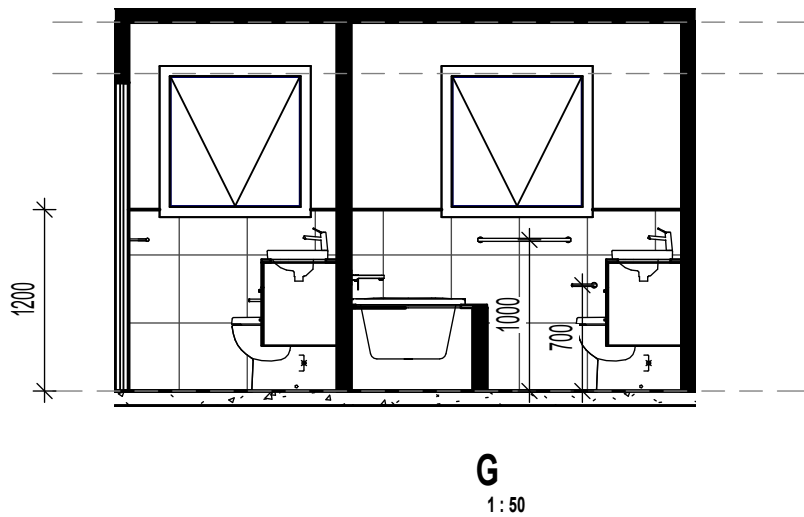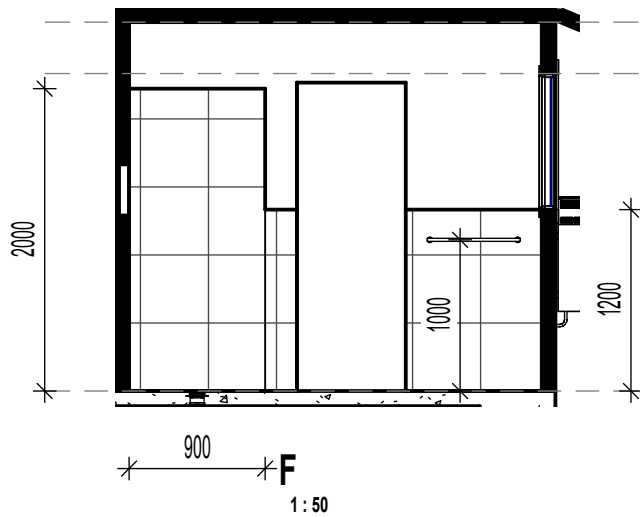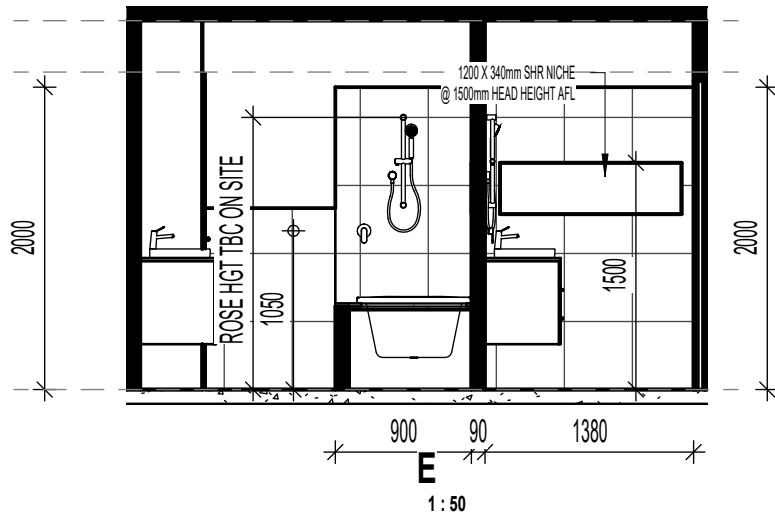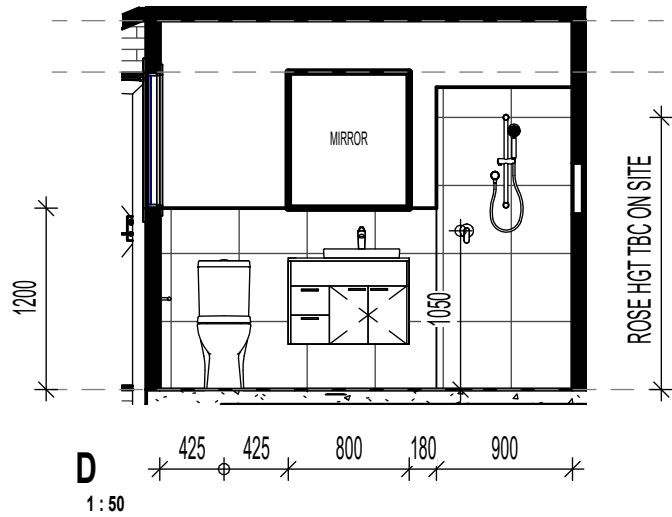


SIGNATURES


OWNER	DATE
OWNER	DATE
BUILDER	DATE

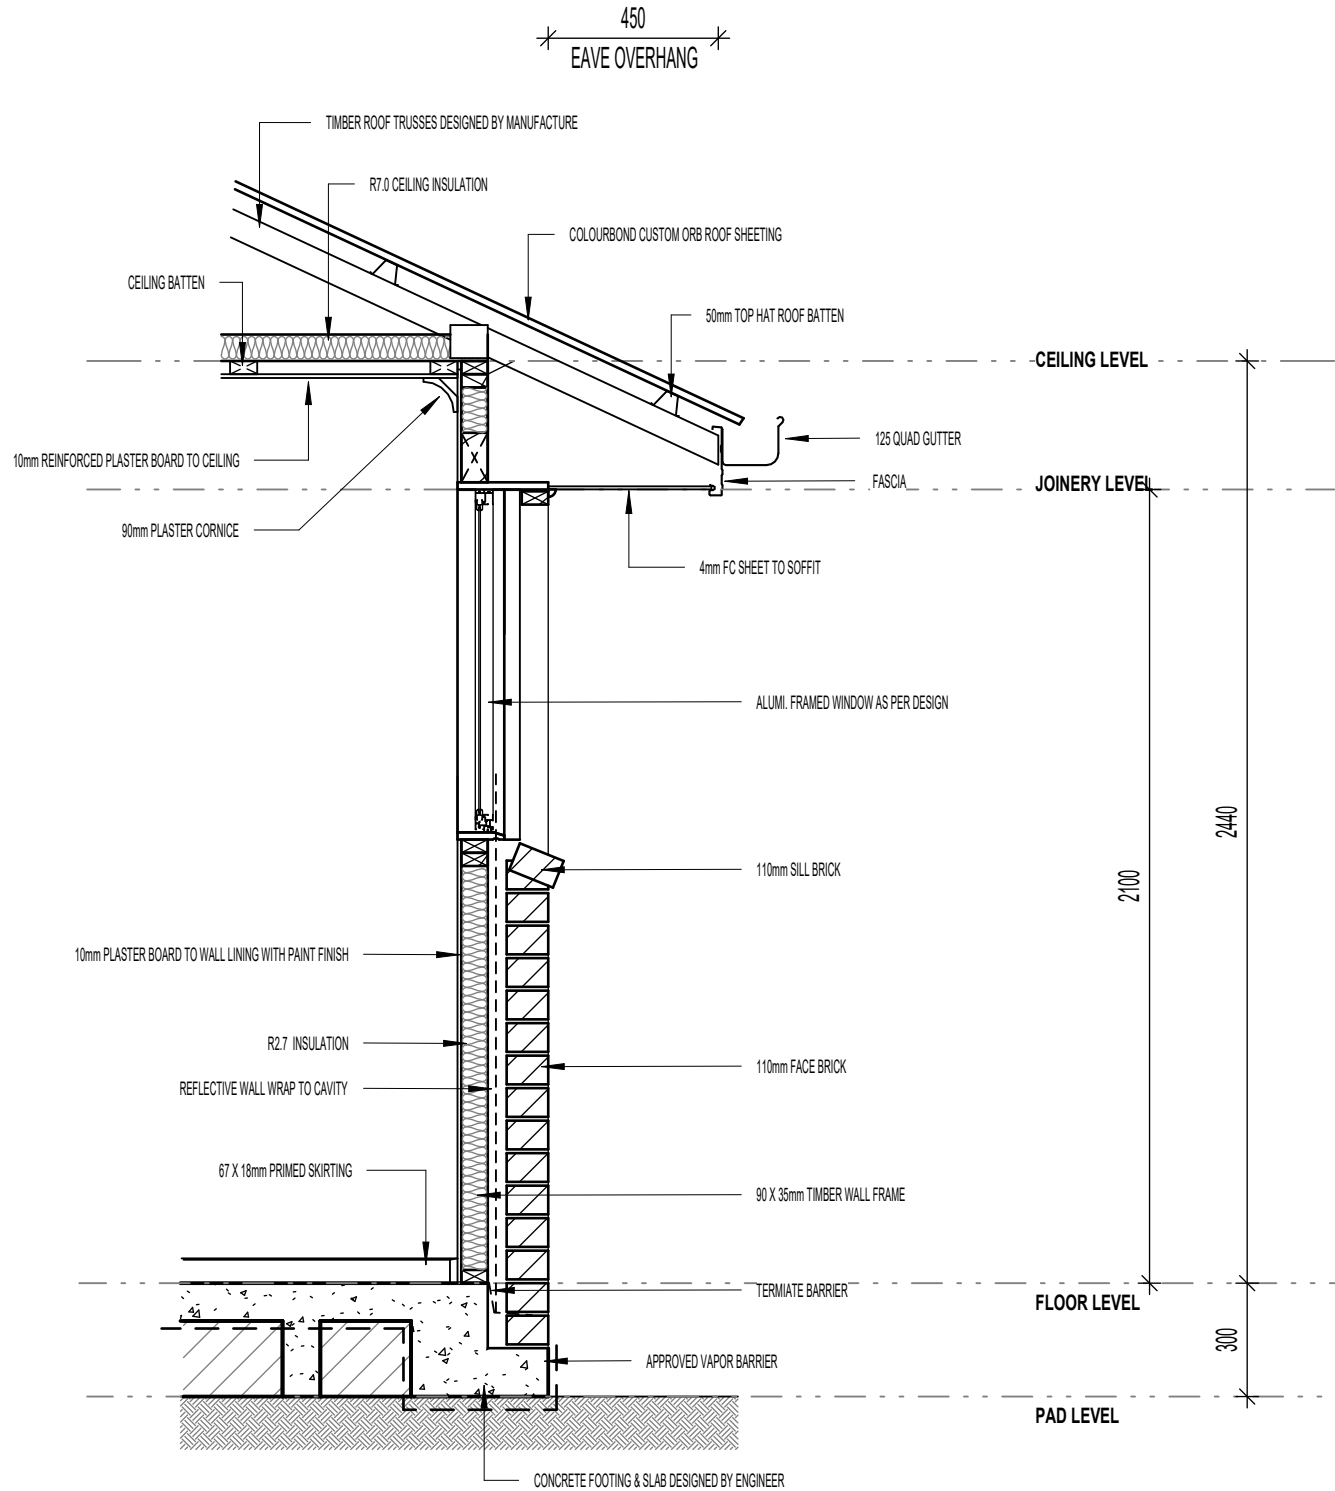

TYP. BRICK VENEER WALL DETAIL - CB ROOF
1 : 20

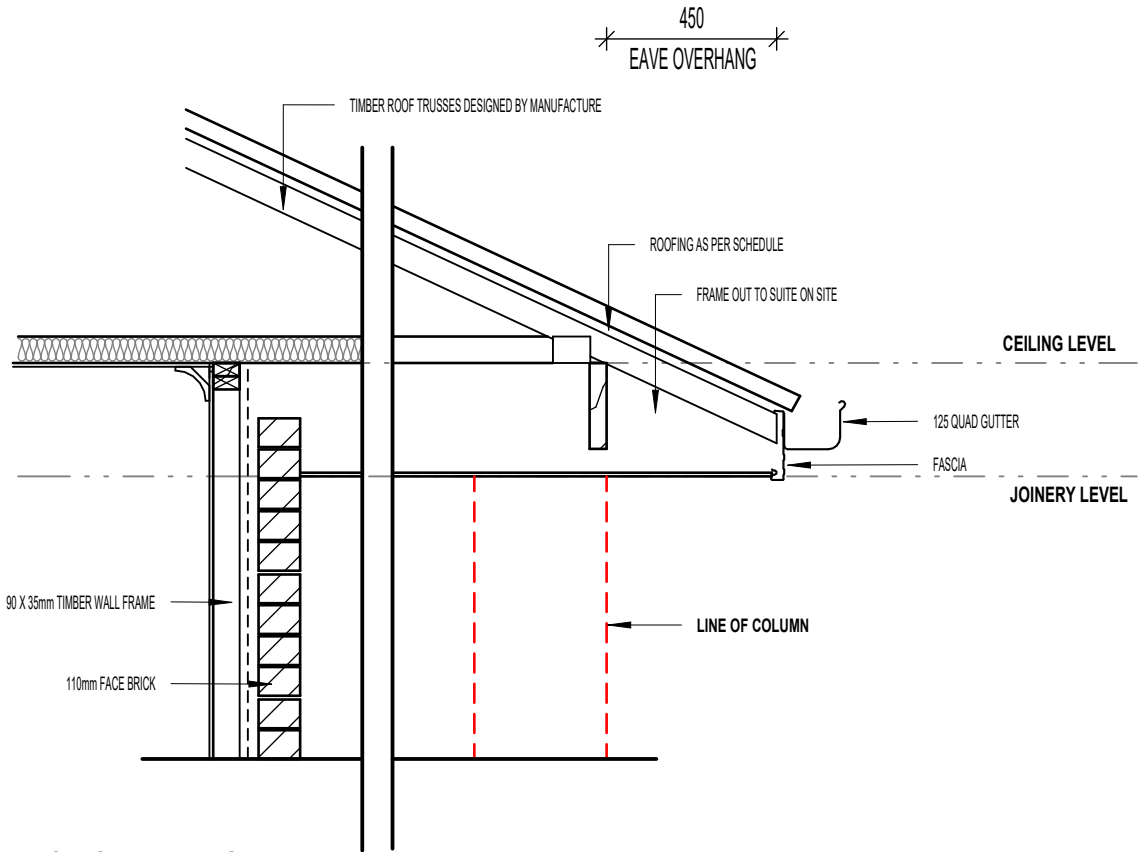

TYP. PORCH EAVES DETAIL
1 : 20

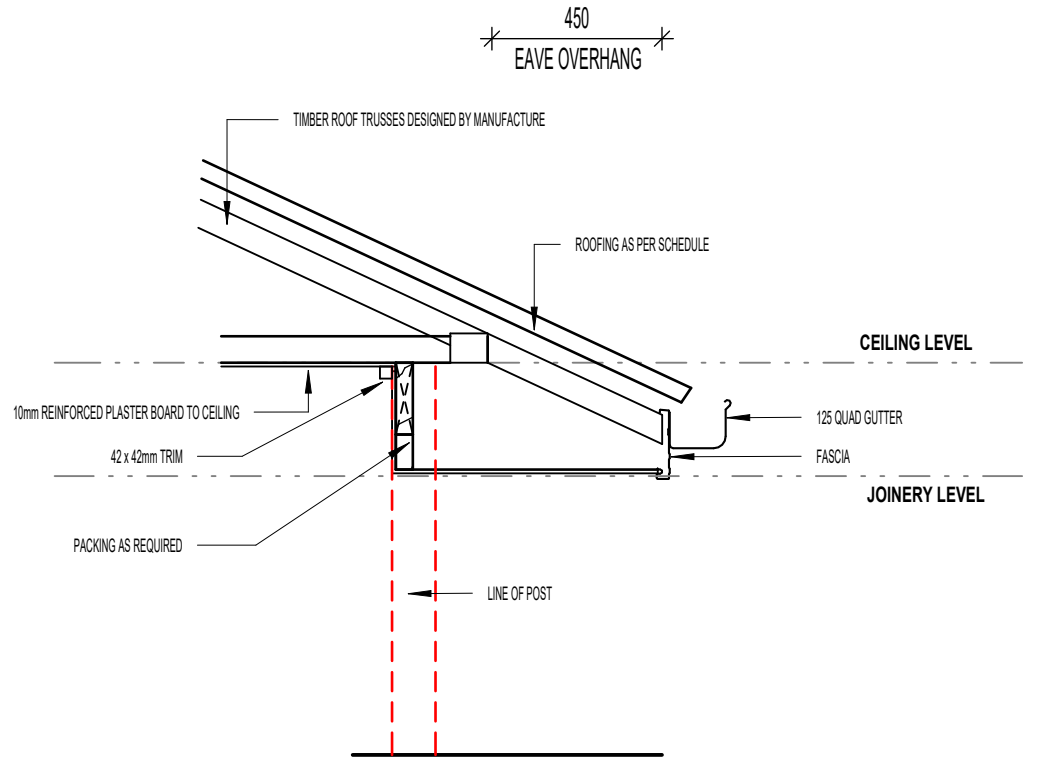

TYP. ALFRESCO EAVE DETAIL
1 : 20

SIGNATURES

OWNER	DATE
OWNER	DATE
BUILDER	DATE

© COPYRIGHT-THESE DRAWINGS REMAIN THE PROPERTY OF G.J GARDNER HOMES & IS PROVIDED FOR THE USE AS DESCRIBED & MAY NOT BE USED OR REPRODUCED IN WHOLE OR IN PART WITHOUT THE WRITTEN PERMISSION. ANY LANDSCAPING (WHEN SHOWN) ARE FOR ILLUSTRATIVE PURPOSES ONLY AND DO NOT FORM PART OF ANY CONTRACT

G.J. Gardner.
G.J. GARDNER ORANGE
Construct Homes Orange Pty Ltd
A.B.N: 19 622 460 119 License: 317706C
PO Box 8015, Orange East, NSW, 2800
P: (02) 6360 3988 W: www.gjgardner.com.au
E: orange@gjgardner.com.au

HOMES

ROBINA 125
CLASSIC
© COPYRIGHT EXCLUSIVE
TO G.J.GARDNER HOMES

TONY JAMES DESIGN PTY LTD
A.B.N: 96 486 946 536
Q.B.C.C License: 106327
V.B.A License: DP-AD-44789
M: 0412 832 646
P: (07) 5665 9230
E: anthony@tonyjames.com.au
W: www.tonyjames.com.au

CLIENT:
SARAH KENNEDY



DRAWING TITLE:
BUILDING DETAILS - SHEET 1

PROJECT: PROPOSED NEW RESIDENCE
**LOT 217 DP 1305914
47 HAWKE LANE
ORANGE NSW 2800**

PAGES:
13 OF 15
SHEET SIZE:
A3
JOB NO: 40283
DRAWN: TJ
DATE: 02/12/2025



FLOOR AREAS:
GROUND FLOOR 90.74 m²
GARAGE 22.54 m²
ALFRESCO 9.43 m²
PORCH 2.45 m²
125.16 m²

REV:	DETAILS:	DATE:
1	PRELIMINARY ISSUE 1	02/12/2025
2	PRELIMINARY ISSUE	16/12/2025
A	CONSTRUCTION ISSUE	03/03/2026
B	CONSTRUCTION ISSUE	06/03/2026

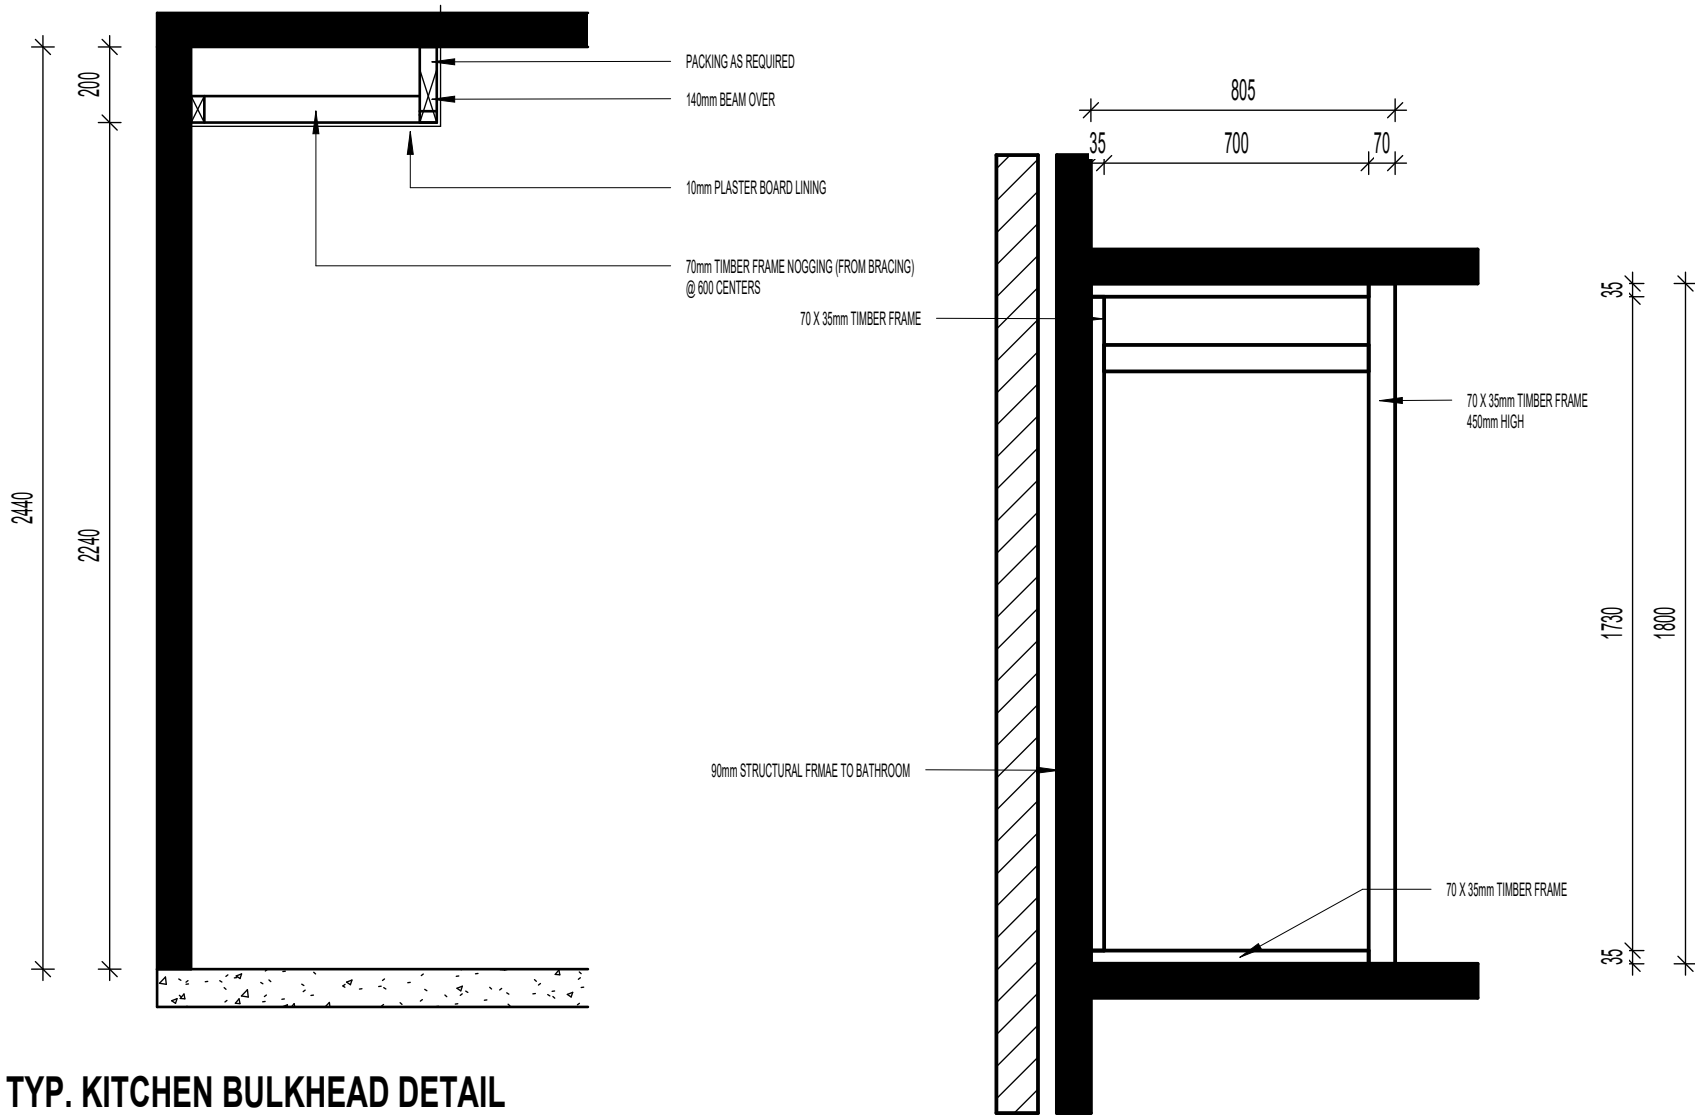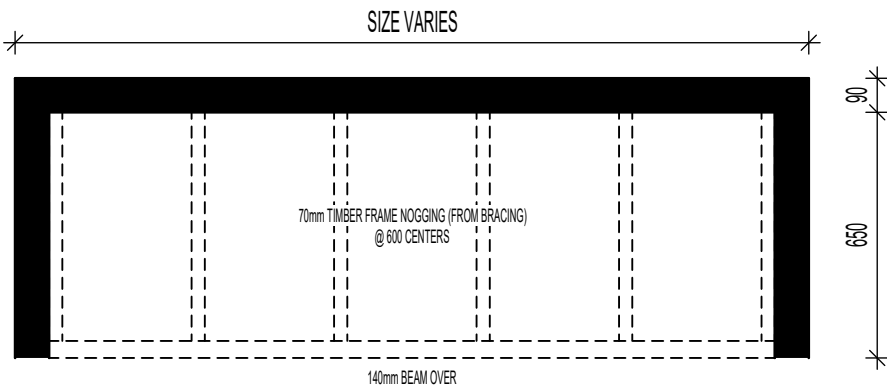

TYP. KITCHEN BULKHEAD DETAIL
1 : 20

TYP. 1675 BATH DETAIL
1 : 20

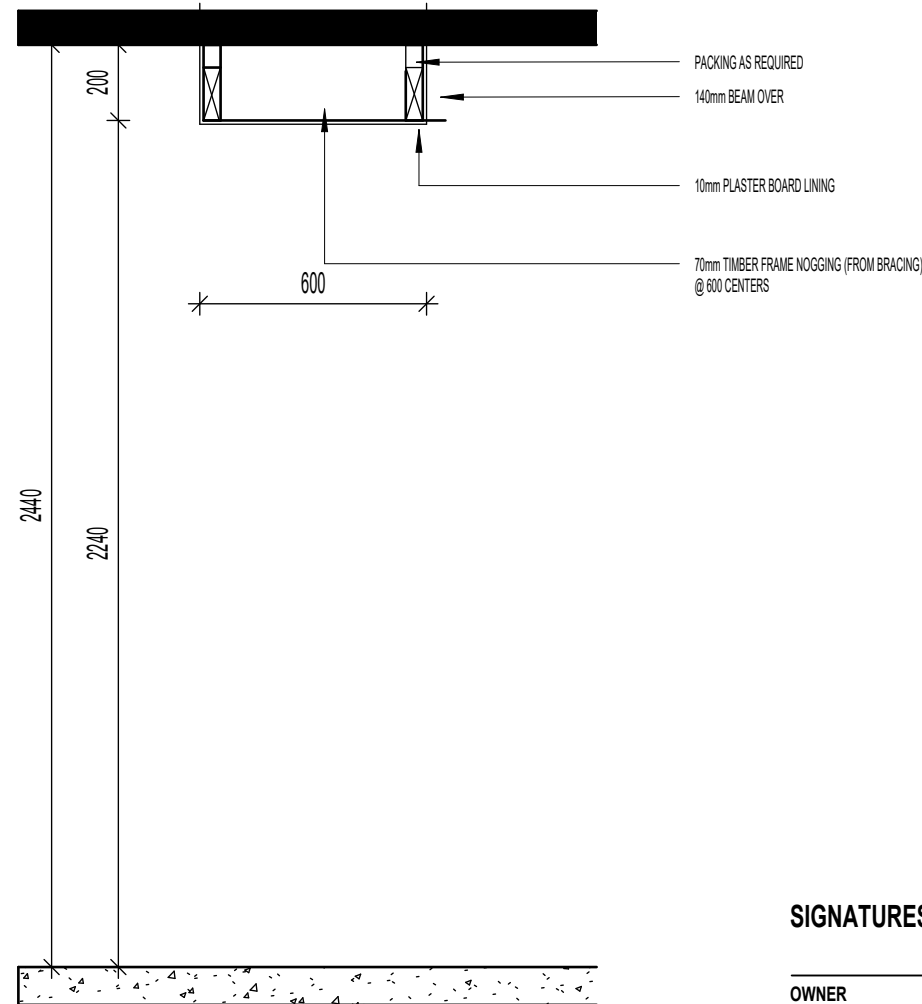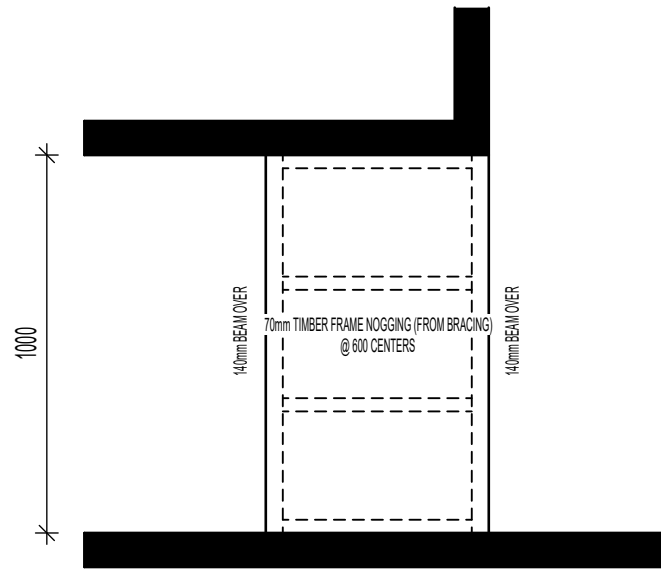

TYP. HALLWAY DETAIL
1 : 20

SIGNATURES


OWNER	DATE
OWNER	DATE
BUILDER	DATE

© COPYRIGHT-THIS DRAWING REMAINS THE PROPERTY OF G.J GARDNER HOMES & IS PROVIDED FOR THE USE AS DESCRIBED & MAY NOT BE USED OR REPRODUCED IN WHOLE OR IN PART WITH OUT THE WRITTEN PERMISSION. ANY LANDSCAPING (WHEN SHOWN) ARE FOR ILLUSTRATIVE PURPOSES ONLY AND DO NOT FORM PART OF ANY CONTRACT

G.J. Gardner. HOMES G.J. GARDNER ORANGE Construct Homes Orange Pty Ltd A.B.N: 19 622 460 119 License: 317706C PO Box 8015, Orange East, NSW, 2800 P: (02) 6360 3988 W: www.gjgardner.com.au E: orange@gjgardner.com.au	ROBINA 125 CLASSIC © COPYRIGHT EXCLUSIVE TO G.J.GARDNER HOMES	TONY JAMES DESIGN PTY LTD A.B.N: 96 486 946 536 Q.B.C.C License: 106327 V.B.A License: DP-AD-44789 M: 0412 832 646 P: (07) 5665 9230 E: anthony@tonyjames.com.au W: www.tonyjames.com.au	CLIENT: SARAH KENNEDY DRAWING TITLE: BUILDING DETAILS - SHEET 2	PROJECT: PROPOSED NEW RESIDENCE LOT 217 DP 1305914 47 HAWKE LANE ORANGE NSW 2800	PAGES: 14 OF 15	SHEET SIZE: A3	FLOOR AREAS: GROUND FLOOR90.74 m² GARAGE22.54 m² ALFRESCO9.43 m² PORCH2.45 m² 125.16 m²	REV: 1 2 A B	DETAILS: PRELIMINARY ISSUE 1 PRELIMINARY ISSUE CONSTRUCTION ISSUE CONSTRUCTION ISSUE	DATE: 02/12/2025 16/12/2025 03/03/2026 06/03/2026
			JOB NO: 40283							
			DRAWN: TJ							
			DATE: 02/12/2025							

DRIVEWAY PROFILE

1 : 75

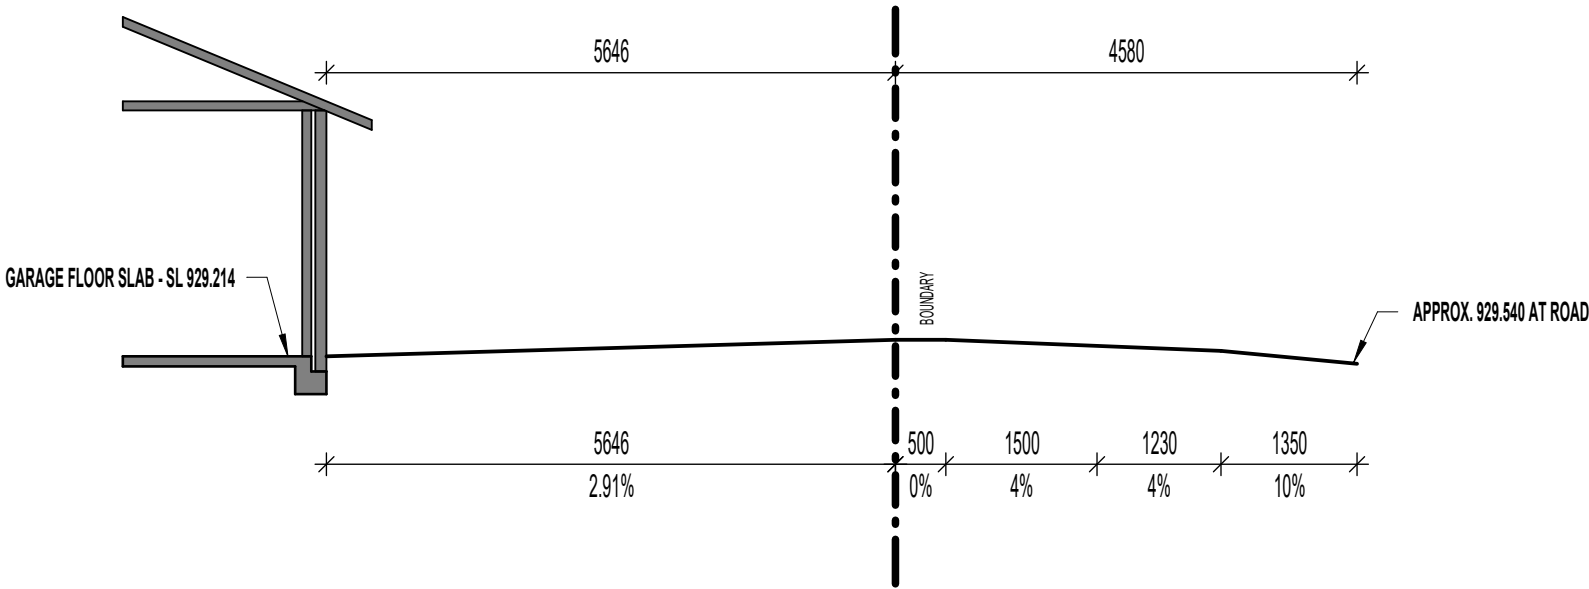

SIGNATURES

	/	/
OWNER	DATE	
	/	/
OWNER	DATE	
	/	/
BUILDER	DATE	

© COPYRIGHT-THIS DRAWING REMAINS THE PROPERTY OF G.J GARDNER HOMES & IS PROVIDED FOR THE USE AS DESCRIBED & MAY NOT BE USED OR REPRODUCED IN WHOLE OR IN PART WITH OUT THE WRITTEN PERMISSION. ANY LANDSCAPING (WHEN SHOWN) ARE FOR ILLUSTRATIVE PURPOSES ONLY AND DO NOT FORM PART OF ANY CONTRACT

G.J. Gardner. HOMES G.J. GARDNER ORANGE Construct Homes Orange Pty Ltd A.B.N: 19 622 460 119 License: 317706C PO Box 8015, Orange East, NSW, 2800 P: (02) 6360 3988 W: www.gjgardner.com.au E: orange@gjgardner.com.au	ROBINA 125 CLASSIC © COPYRIGHT EXCLUSIVE TO G.J.GARDNER HOMES	TONY JAMES DESIGN PTY LTD A.B.N: 96 486 946 536 Q.B.C.C License: 106327 V.B.A License: DP-AD-44789 M: 0412 832 646 P: (07) 5665 9230 E: anthony@tonyjames.com.au W: www.tonyjames.com.au	CLIENT: SARAH KENNEDY DRAWING TITLE: DRIVEWAY PROFILE	PROJECT: PROPOSED NEW RESIDENCE LOT 217 DP 1305914 47 HAWKE LANE ORANGE NSW 2800	PAGES: 15 OF 15	SHEET SIZE: A3	FLOOR AREAS: GROUND FLOOR90.74 m² GARAGE22.54 m² ALFRESCO9.43 m² PORCH2.45 m² 125.16 m²	REV: 1 2 A B	DETAILS: PRELIMINARY ISSUE 1 PRELIMINARY ISSUE CONSTRUCTION ISSUE CONSTRUCTION ISSUE	DATE: 02/12/2025 16/12/2025 03/03/2026 06/03/2026	
				JOB NO: 40283							
				DRAWN: TJ							
						DATE: 02/12/2025					