

PROPOSED NEW DWELLING
LOT 1808 ZILLIE CLOSE DUBBO
NSW 2830 FOR:



Part 10.8 Condensation Requirements			
Climate Zone	Location	Requirement	Proposed Method
ALL	Kitchen / Laundry	Installed exhaust system requires minimum flow rate of 40L/s, ducted externally.	Ducted Fan (Flow > 40L/s)
ALL	Bathroom / WC	Installed exhaust system requires minimum flow rate of 25L/s, ducted externally.	Ducted Fan (Flow > 25L/s)
4 & 5	External Wall	Pliable membrane or sarking material to have a minimum vapour permeance of 0.143 µg/N.s.	Vapawrap (1.14 µg/N.s)
6, 7 & 8	External Wall	Pliable membrane or sarking material to have a vapour permeance of 1.14 µg/N.s.	Vapawrap (1.14 µg/N.s)
6, 7 & 8	Ridge	Ventilation of 5000mm2/m at the ridge.	Gap at Ridge, Cut Back Anticon
6, 7 & 8	Eaves	Roof Pitch ≥ 10° and < 15° requires ventilation of 25,000mm2/m at the eaves.	1 x Vent (200x400) Per 3.2m
		Roof Pitch ≥ 15° and < 75° requires ventilation of 7,000mm2/m at the eaves.	1 x Vent (200x400) Per 11.4m

NOTE: Ventilation requirement (mm2/m) is the minimum free open area per meter length of the **longest horizontal dimension** of the roof.

BASIX REQUIREMENTS


- 3-STARS SHOWERHEADS.
- 4-STARS WC, 4-STARS TAPS.
- 3000L SLIMLINE FOR EACH DWELLING MUST COLLECT WATER FROM 250m² OF ROOF AREA.
- SISAL TUFF WALL WRAP TO EXTERNAL WALLS.
- R2.0 HIGH DENSITY INSULATION BATTS TO INTERNAL WALLS JOINING TO GARAGE ONLY
- R2.0 INSULATION BATTS W/ NR WRAP TO ALL EXTERNAL WALLS INCLUDING GARAGE
- R6.0 INSULATION BATTS TO ENTIRE CEILING INCLUDING GARAGE / R3.0 EDGE BATTS INCLUDED
- R1.3 ANTICON BLANKET TO ENTIRE CEILING INCLUDING GARAGE
- ROOF - SHALE GREY, EXTERNAL WALLS - CLAD WATTYL - EARTHCHILD
- GLAZING: SINGLE CLEAR / COMFORT PLUS (W5, SD4) / DOUBLE GLAZED (W6, W9)
- 6-STARS GAS INSTANTANEOUS HOT WATER SYSTEM TO DWELLING. NATURAL
- EXHAUST FANS TO BATHROOM, ENSUITE AND KITCHEN RANGEHOOD.
- 12.5kW PANASONIC DUCTED REVERSE CYCLE AIR CONDITIONING UNIT, DAY/NIGHT ZONED WITH UPTO 11 OUTLETS.
- OVEN - ELECTRIC: OMEGA OBOP6016AM
- COOKTOP - NATURAL: Gas Cooktop OMEGA OCGG604WB
- RANGEHOOD: OMEGA ORU52MB
- DISHWASHER: OMEGA ODWF6015BXCOM
- SOLAR PHOTOVOLTAIC SYSTEM - 2kW 5 solar panels with 2kW invertor (NORTH FACING)

CONSTRUCTION NOTES

- ALL DIMENSIONS ARE IN MILLIMETRES AND SHOULD BE USED IN PREFERENCE TO SCALED MEASUREMENTS.
- ALL LEVELS ARE TO BE VERIFIED ON THE SITE BY THE BUILDER PRIOR TO WORK COMMENCING.
- ALL WET AREAS ARE TO BE SUITABLY GRADED AND DRAINED.
- FLOOR SLAB TO BE DESIGNED BY AN APPROVED STRUCTURAL ENGINEER.
- ALL TIMBER SPACING, SPANS AND SIZES SHALL COMPLY WITH TIMBER FRAMING CODE AS 1684.
- ENSURE STRICT COMPLIANCE WITH THE REQUIREMENTS OF BUILDING CODE OF AUS IN RELATION TO SIDE BOUNDARY CLEARANCE.
- ALL SEWER AND STORMWATER DRAINAGE TO BE IN STRICT ACCORDANCE WITH THE REQUIREMENTS OF THE LOCAL GOVERNMENT AUTHORITY.
- WET AREAS ARE TO BE SEALED AT THE INTERSECTION OF THE FLOOR AND WALL AND 1800 HIGH IN THE SHOWER RECESS CORNERS WITH AN APPROVED WET AREA SEAL.
- POWDER COATED ALUMINIUM WINDOWS AND DOORS TO BE USED THROUGHOUT. COLOUR SELECTION BY BUILDER.
- ALL FIXINGS, TIE DOWNS AND CONSTRUCTION METHODS ARE TO BE IN STRICT ACCORDANCE WITH AS1684 AND THE BCA.
- TERMITE PROTECTION TO BE IN ACCORDANCE WITH AS3660-1

GENERAL NOTES:


- LOCATE EXISTING SERVICES PRIOR TO CONSTRUCTION.
- EROSION / SEDIMENT CONTROL IN STRICT ACCORDANCE WITH COUNCIL REQUIREMENTS (REFER BUILDER).
- PROVIDE HARDBASE ALL WEATHER ACCESS, DURING CONSTRUCTION.
- CUT AND FILL TO BUILDER'S DISCRETION.
- NOMINATED WATER TO TANK. OVERFLOW TO STREET.
- BUILDER TO CONFIRM ALL FINISHED FLOOR LEVELS ON SITE.
- WIND - N2
- SITE - H1
- SOIL - H1

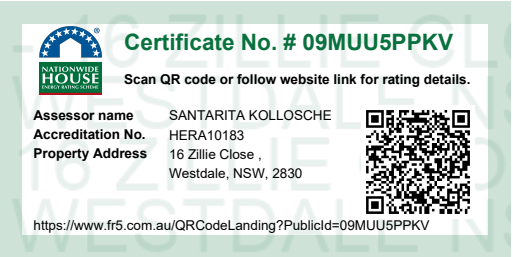

DRAWING SCHEDULE:

SHEET	DESCRIPTION/TITLE
01	COVER SHEET
02	SITE PLAN
03	SERVICES PLAN
04	LANDSCAPE PLAN
05	FLOOR PLAN
06	ELEVATIONS1-3
07	ELEVATION 4 & SECTION
08	SLAB PLAN
09	ELECTRICAL PLAN
10	BATH/WC/ENSUITE
11	LAUNDRY / KITCHEN
12	WET AREA - STEP DOWNS
13	ROBE/LINEN/CABINETRY
14	ADJUSTABLE POST
15	ALFRESCO BULKHEADS
16	GARAGE DOOR /CORNER/TERMITE PROTECTION
17	FLOOR DETAILS
18	ARTICULATION VERTICAL JOINT

Window	Type	Specification	U-Value	SHGC	SG AREA	DG AREA
W1	Fixed Window SG	WID-012-01 A Aluminium Awning Window SG 5mmClr	6.32	0.63	0.54	
SD3,	Sliding Door SG	WID-005-01 A Al Residential Internal Sliding Door SG 4mm Clear	6.25	0.72	3.15	
W2, W3, W4	Sliding Window SG	WID-006-01 A Al Residential Sliding Window SG 3mm Clear	6.42	0.76	6.21	
SD4	Sliding Door SG Comfort Plus	WID-005-04 A Al Residential Internal Sliding Door SG 638mm Comfort Plus	4.42	0.44	5.04	
W5,	Sliding Window SG Comfort Plus	WID-006-04 A Al Residential Sliding Window SG 638mm Comfort Plus	4.53	0.46	2.25	
W6, W9	Sliding Window DG Double Glazed	WID-006-09 A Al Residential Sliding Window DG 3mm Clear / 6mm Air Gap / 4mm Energy Advanta	3.99	0.56		5.04
W7, W8, W10	Obscure Window SG	WID-028-09 A BSW Ascend Sliding Window SG 5mmClr	6.55	0.62	2.70	
W11, W12	D/Hung Window SG	WID-003-01 A Al Residential Double Hung Window SG 3Clr	6.24	0.74	3.24	
TOTALS (28.17)					23.13m2	5.04m2

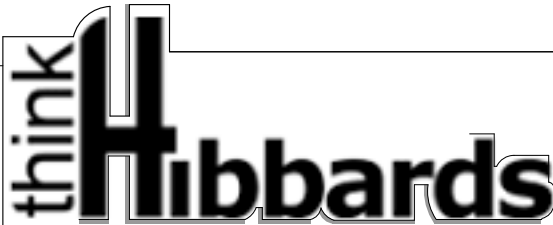

Address:
130 West High Street
Coffs Harbour NSW 2450

Hibbards P/L ABN 22 057 895 020
E:coffs@hibbards.com.au
P:(02) 6650 3300
F:(02) 6651 7044
W: https://hibbardhomes.com.au/

COPYRIGHT & NOTES

figured dimensions to be used in reference to scaling - all dimensions to be checked on site .Copying of this plan is strictly prohibited without written permission of Hibbard Homes . All boundaries and contours subject to survey


DESIGN
KIATO 225 SG22 W02 RHG

JOB ADDRESS


LOT 1808 ZILLIE CLOSE
DUBBO NSW 2830

PROPOSAL NEW DWELLING DP: 1318131


drawing title		COVER SHEET						
date	issue	description			JOB No.	11439	revision	
09/01/26	1	ISSUED FOR CC APPROVAL			SCALE	NTS	1	
					DRAWN	ML		PAGE
					DATE	13/01/2026	1	
					WIND	'N2'		SITE

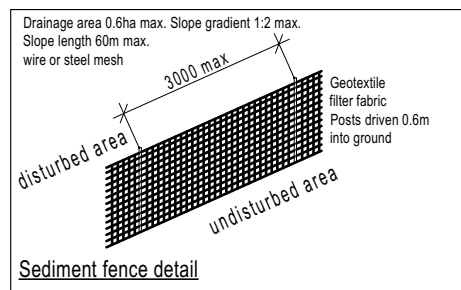

APPROX. LEVELS
PAD RL : 314.10
SLAB RL : 314.50
GARAGE PAD RL : 314.014
GARAGE RL : 314.414

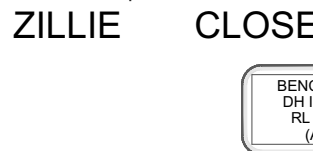

Driveway to be constructed in accordance with AS2890.1
Parking facilities, off street carpark

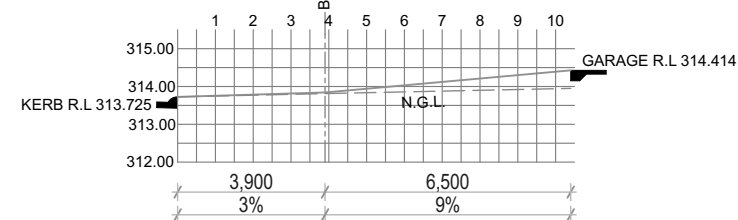

Driveway Section

SCALE 1:200




SEWER INFORMATION NOT AVAILABLE VIA BYDA AT THE TIME OF SURVEY

(Q) - EASEMENT TO DRAIN SEWAGE VARIABLE WIDTH

(T) - EASEMENT TO DRAIN WATER 5 WIDE

(V) - EASEMENT FOR SERVICE 5 WIDE

(Z) - RIGHT OF CARRIAGEWAY 5 WIDE

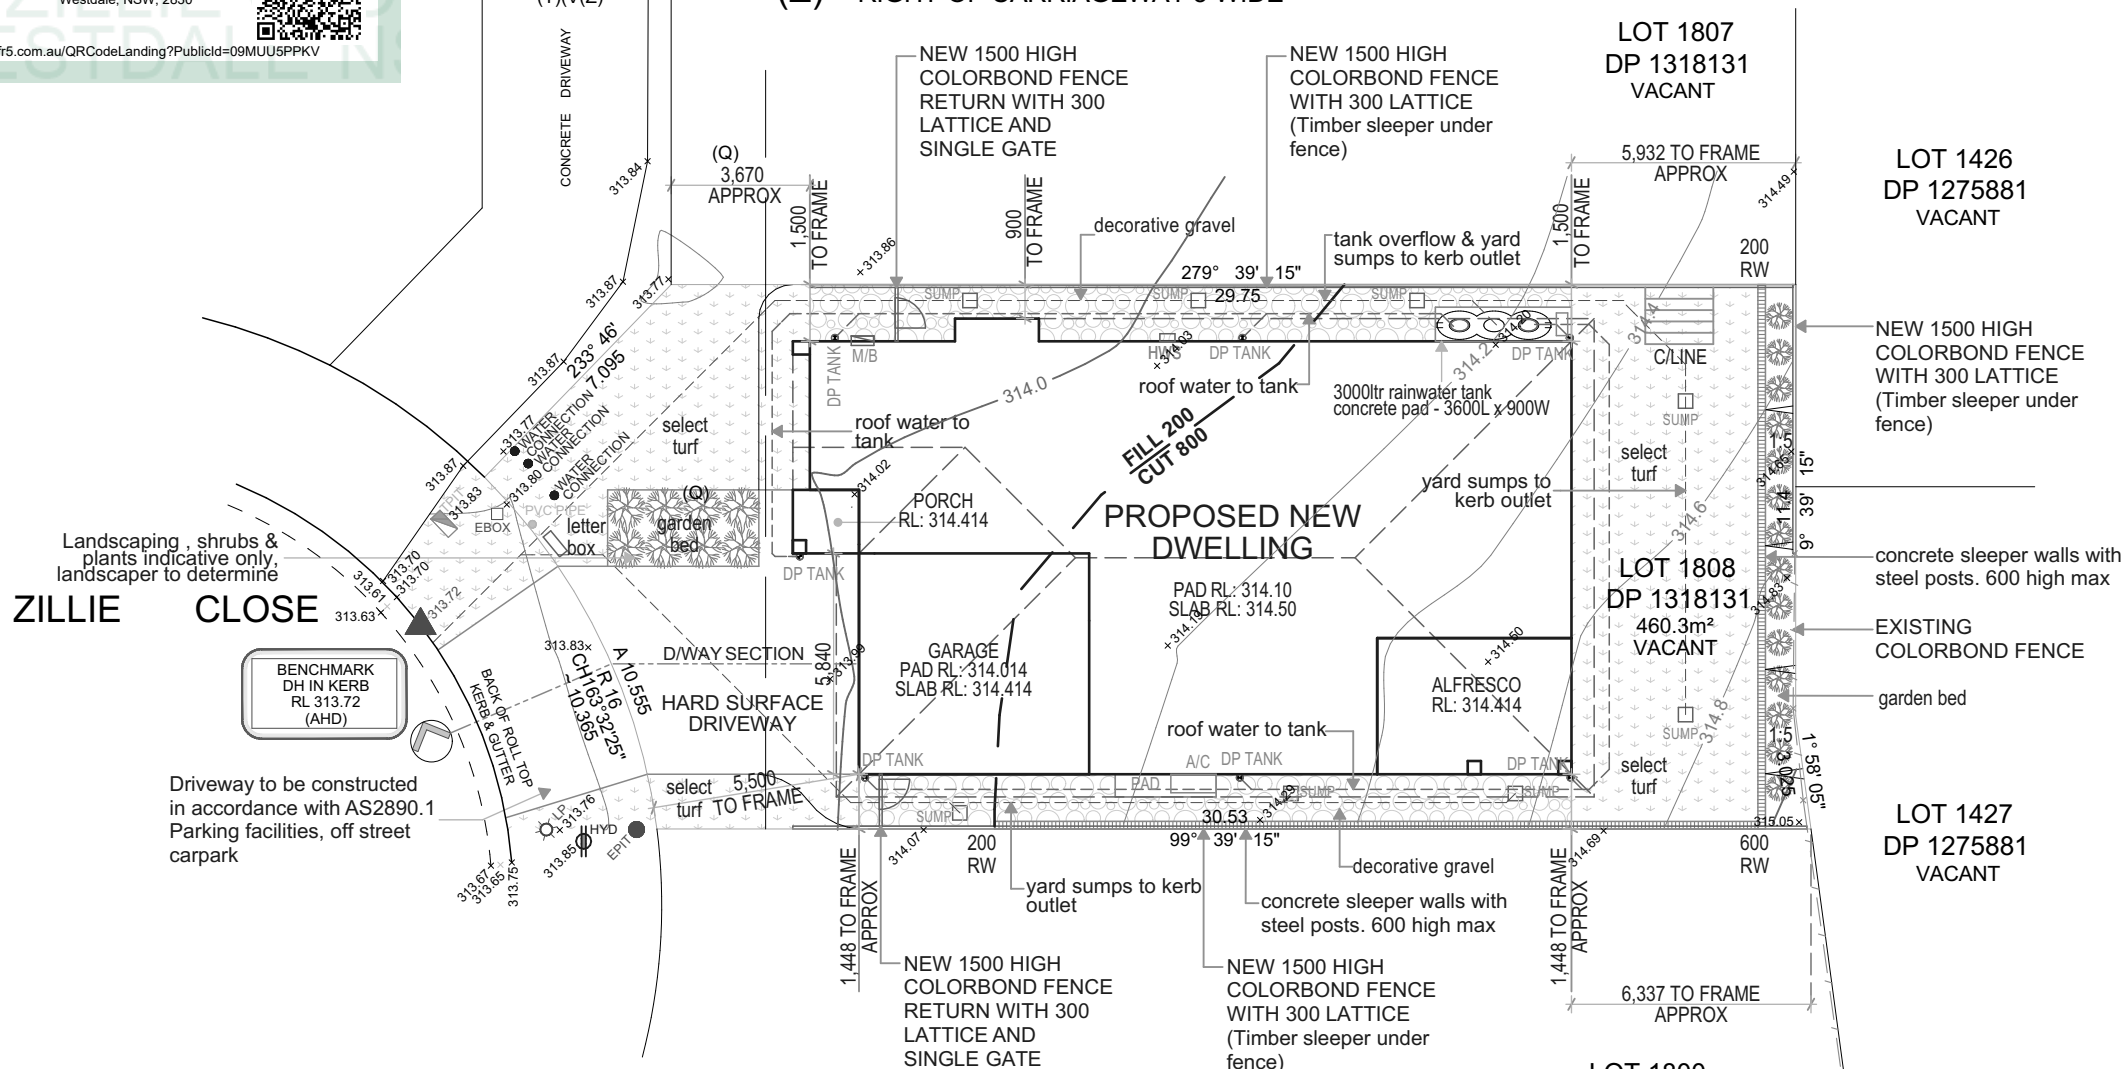

Site Plan

SCALE 1:200

Address:
130 West High Street
Coffs Harbour NSW 2450


Hibbards P/L ABN 22 057 895 020


E: coffs@hibbards.com.au
P: (02) 6650 3300
F: (02) 6651 7044
W: <https://hibbardhomes.com.au/>

COPYRIGHT & NOTES	
figured dimensions to be used in reference to scaling - all dimensions to be checked on site . Copying of this plan is strictly prohibited without written permission of Hibbard Homes . All boundaries and contours subject to survey	
DESIGN	KIATO 225 SG22 W02 RHG

JOB ADDRESS			
LOT 1808 ZILLIE CLOSE DUBBO NSW 2830			
PROPOSAL	NEW DWELLING	DP:	1318131

drawing title		SITE PLAN										
date	issue	description						JOB No.		11439		revision
09/01/26	1	ISSUED FOR CC APPROVAL						SCALE		1:200 printed to A3 size		1
								DRAWN		ML		
								DATE		13/01/2026		PAGE 2
								WIND	'N2'	SITE		

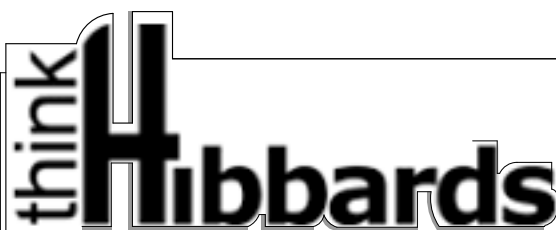

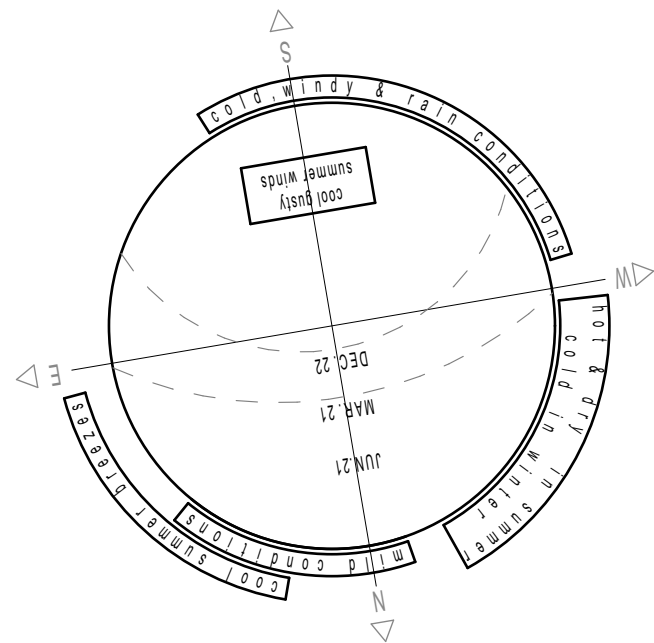


Solar & Wind Chart



ZILLIE

CLOSE

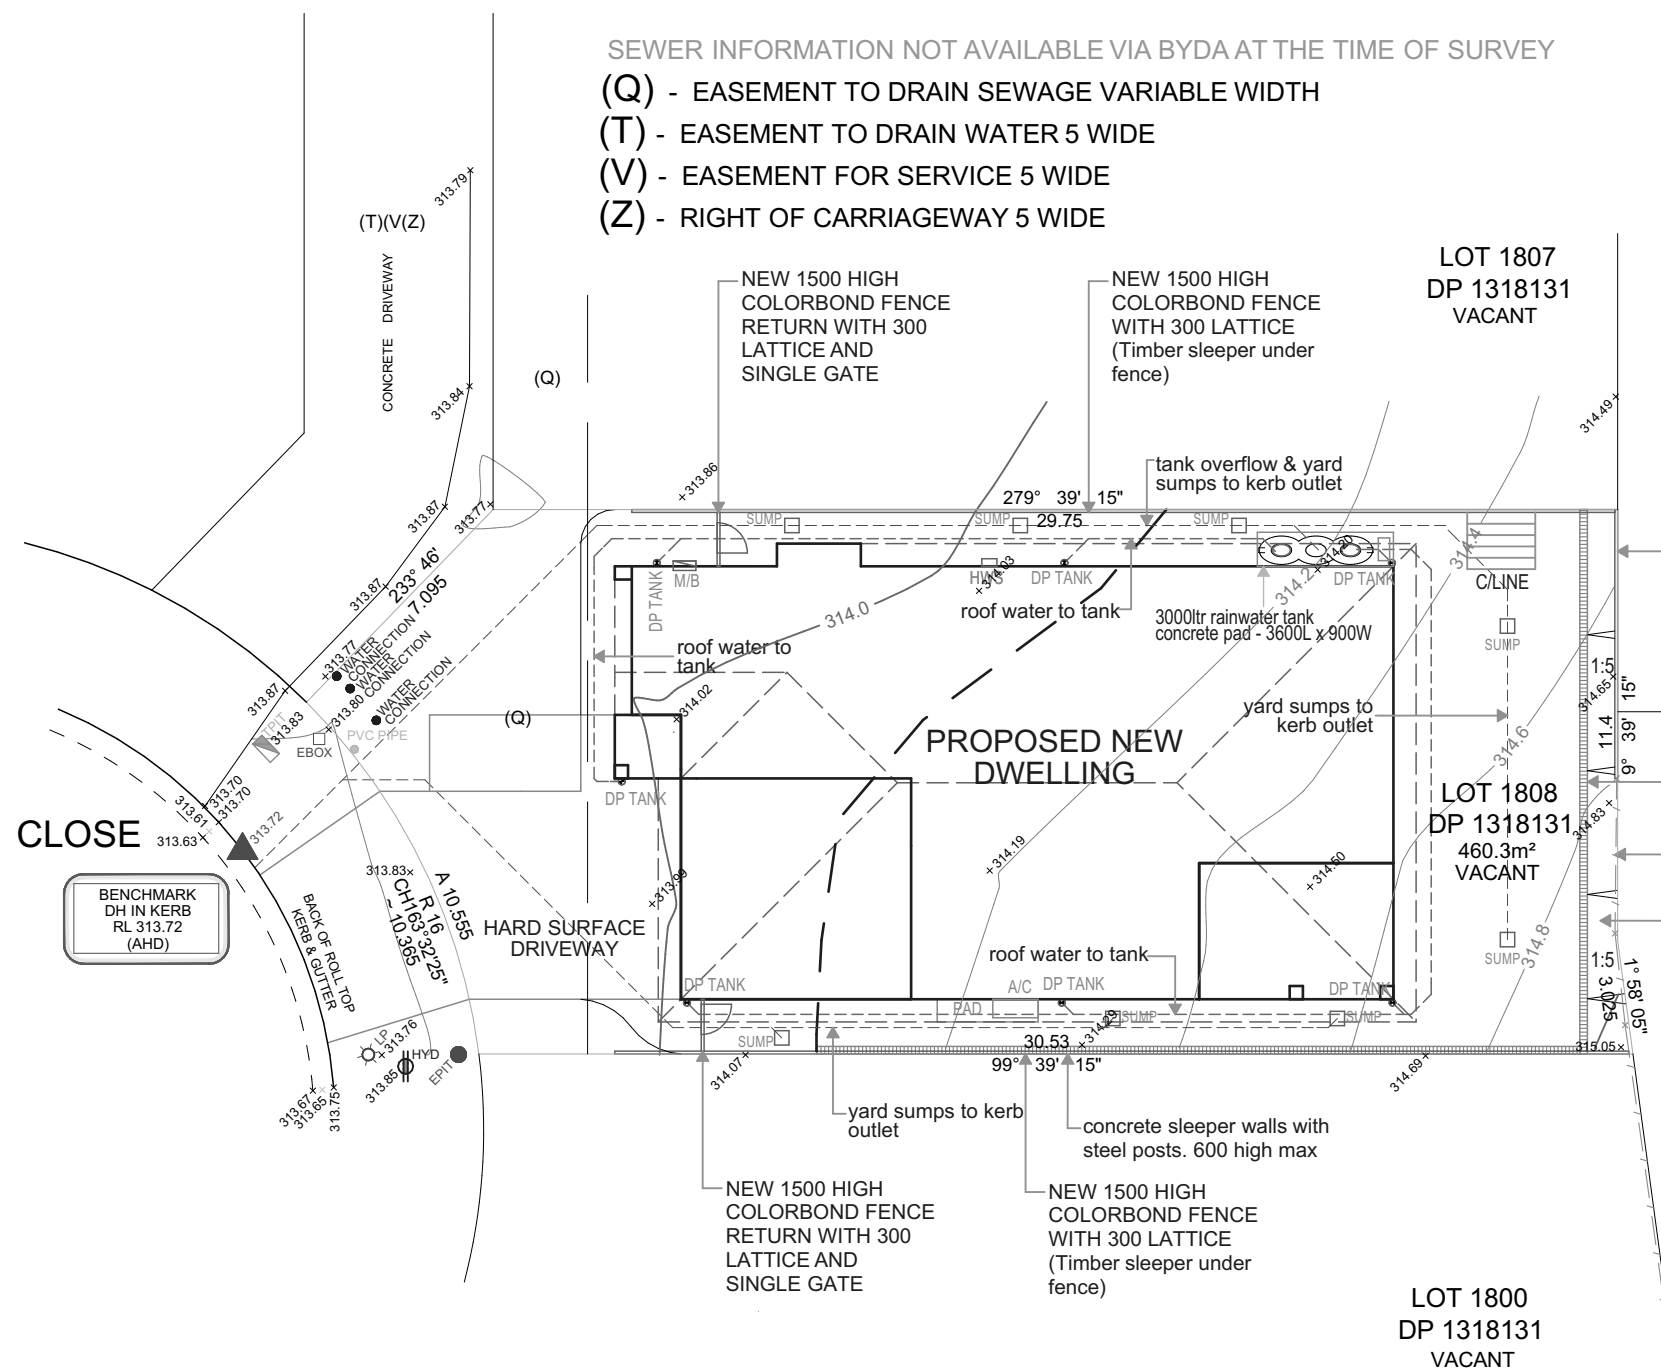


Services Plan
SCALE 1:200

Certificate No. # 09MUU5PPKV
Scan QR code or follow website link for rating details.

Assessor name: SANTARITA KOLLOSCHKE
Accreditation No.: HERA10183
Property Address: 16 Zillie Close, Westdale, NSW, 2830

<https://www.fr5.com.au/QRCodeLanding?PublicId=09MUU5PPKV>

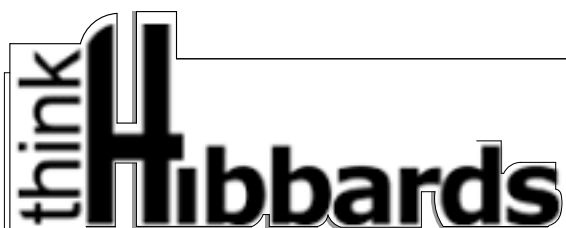

Address:
130 West High Street
Coffs Harbour NSW 2450

Hibbards P/L ABN 22 057 895 020
E: coffs@hibbards.com.au
P: (02) 6650 3300
F: (02) 6651 7044
W: <https://hibbardhomes.com.au/>

COPYRIGHT & NOTES

figured dimensions to be used in reference to scaling - all dimensions to be checked on site. Copying of this plan is strictly prohibited without written permission of Hibbard Homes. All boundaries and contours subject to survey


DESIGN: KIATO 225 SG22 W02 RHG

JOB ADDRESS

LOT 1808 ZILLIE CLOSE
DUBBO NSW 2830

PROPOSAL: NEW DWELLING DP: 1318131


drawing title		SERVICES PLAN			
date	issue	description		JOB No.	11439
09/01/26	1	ISSUED FOR CC APPROVAL		SCALE	1:200
				DRAWN	ML
				DATE	13/01/2026
				WIND	'N2'
				SITE	
				revision	1
				PAGE	3

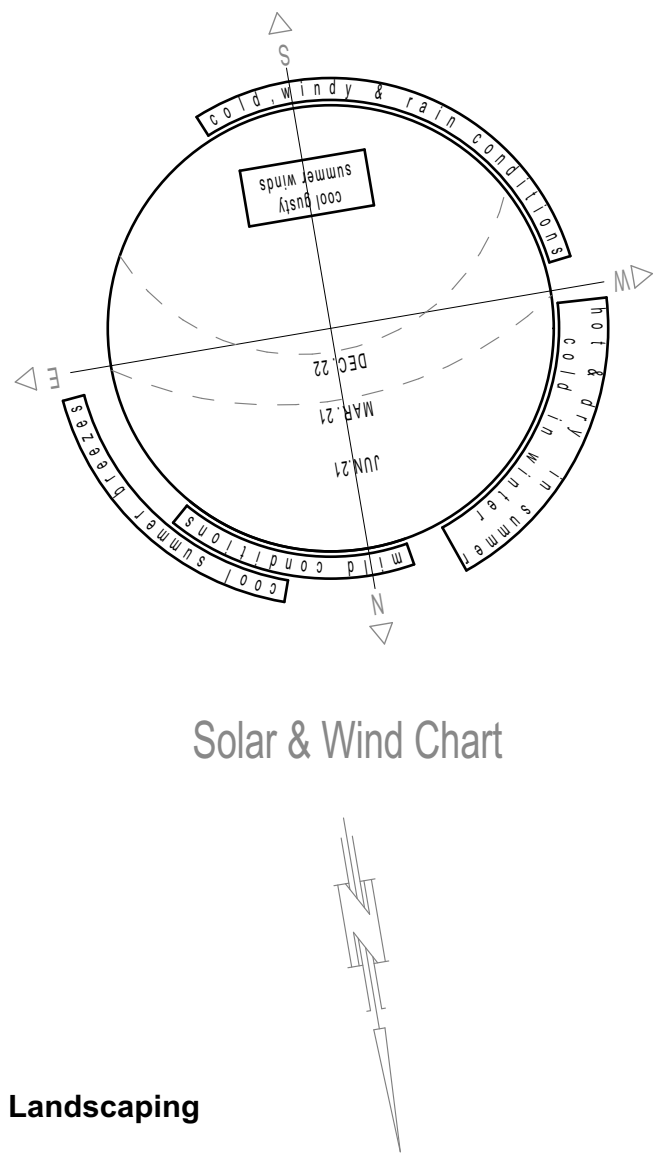

Landscaping

Note : Plant types will be selected from the following range by the nominated landscaper .Specific types have not been nominated due to availability of plants

- gardenia florida
- viburnum tinus
- virburnum odartissium
- oriental pearl
- callistamen
- nandina moon bay
- westringa
- diosma
- port wine magnolia
- photinia super red
- purple fountain grass
- mixed gardens of shrubs grasses & ground covers

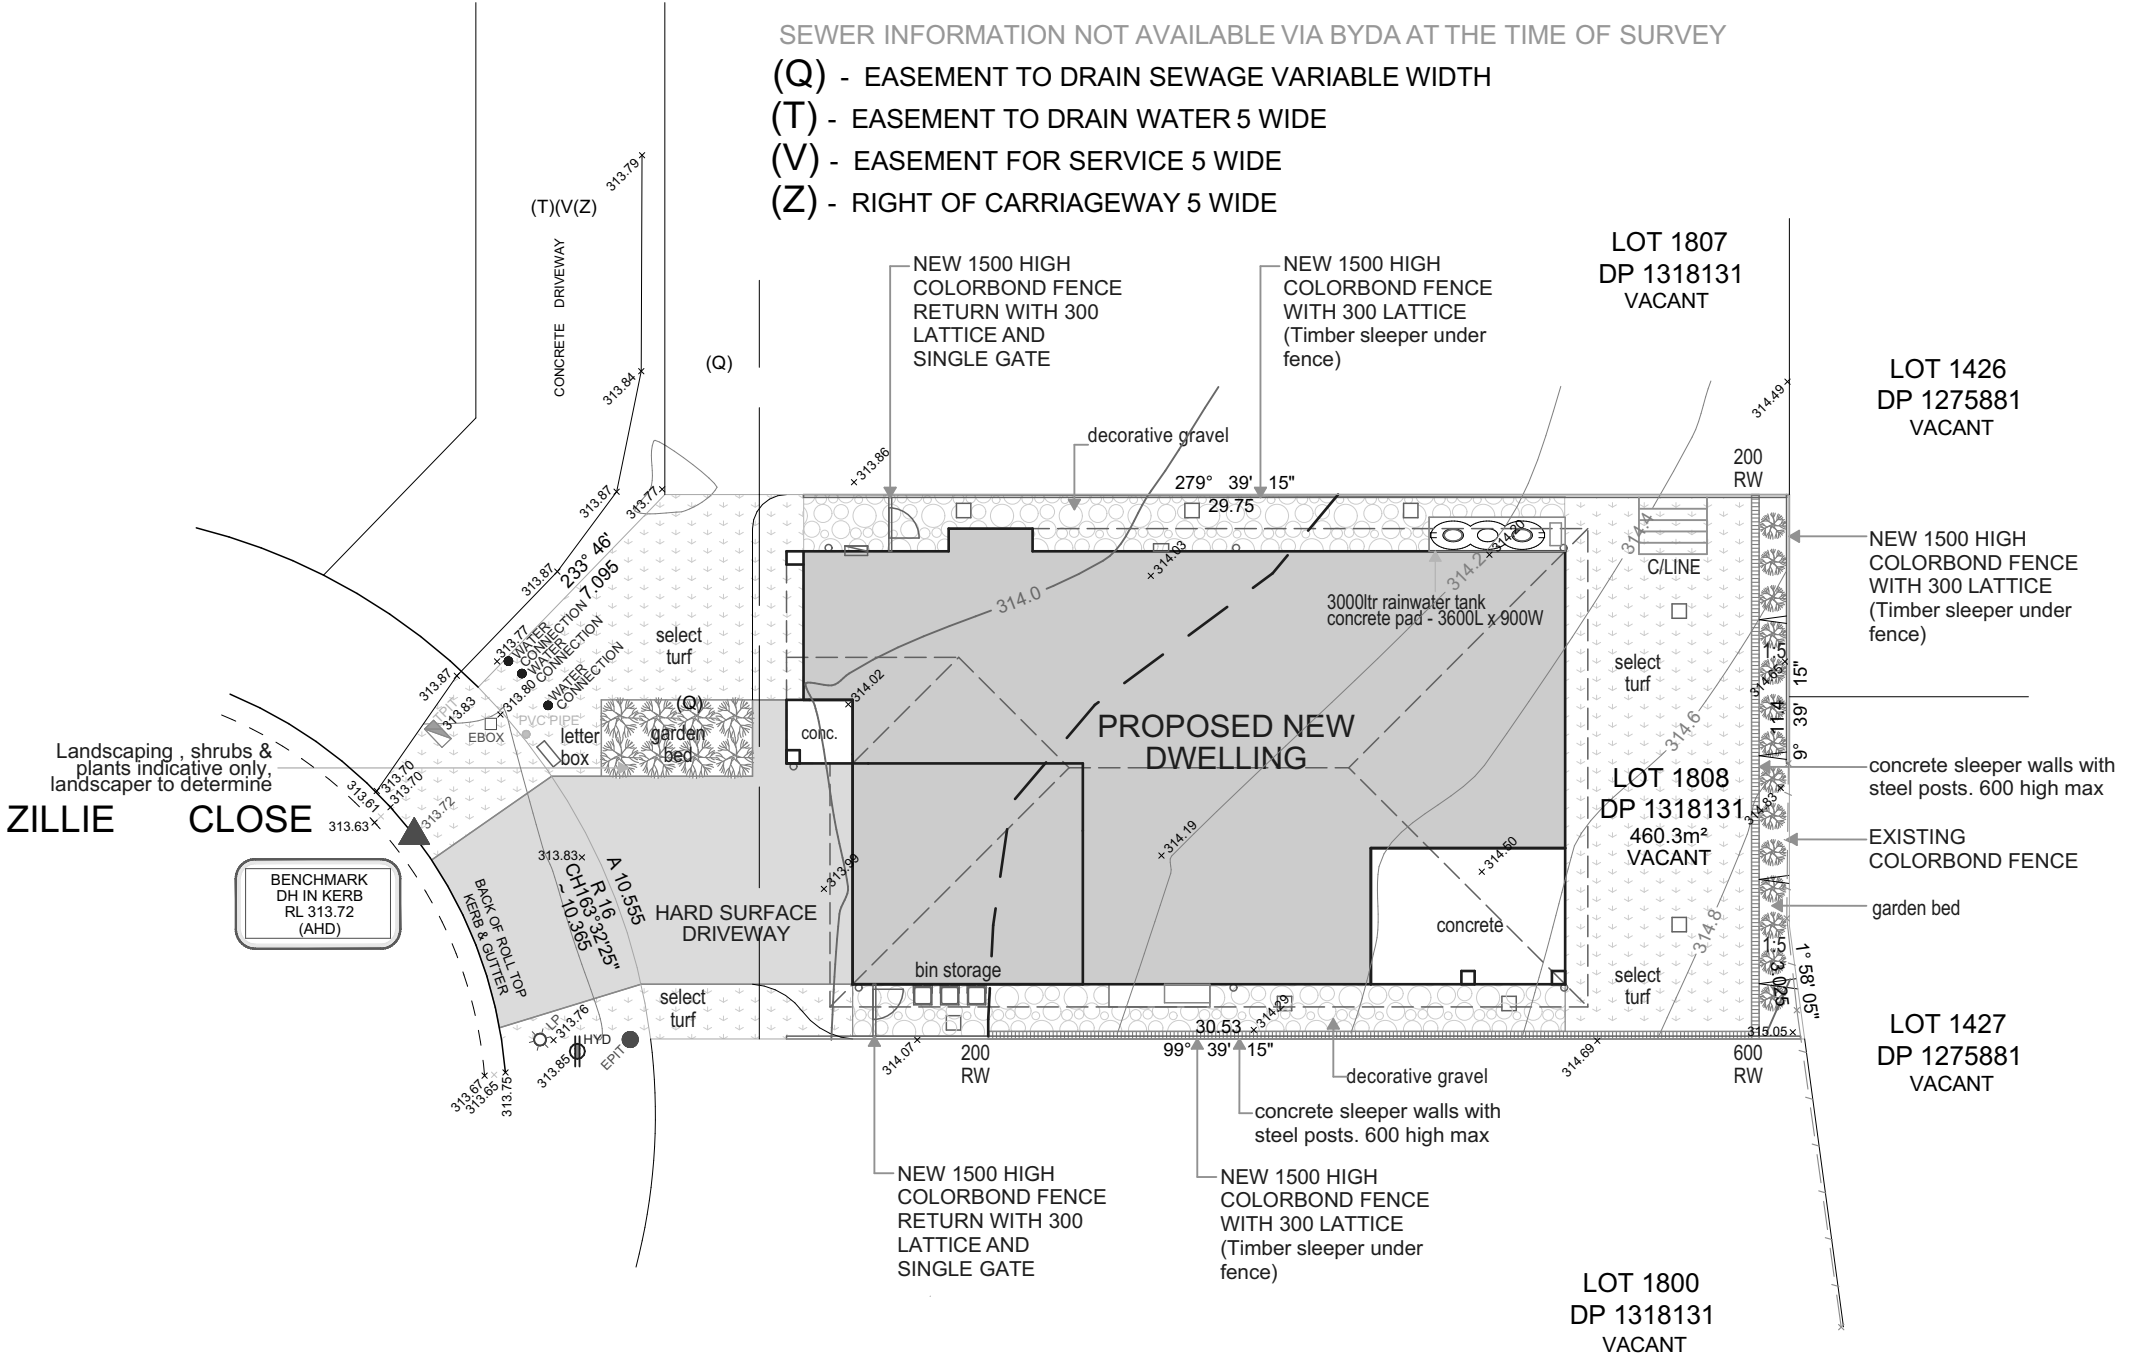


Landscape Plan
SCALE 1:200

Certificate No. # 09MUU5PPKV

Scan QR code or follow website link for rating details.

Assessor name	SANTARITA KOLLOSCHKE
Accreditation No.	HERA10183
Property Address	16 Zillie Close , Westdale, NSW, 2830

<https://www.fr5.com.au/QRCodeLanding?PublicId=09MUU5PPKV>

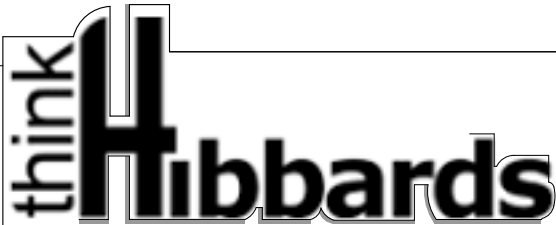

Address:
130 West High Street
Coffs Harbour NSW 2450
Hibbards P/L ABN 22 057 895 020
E:coffs@hibbards.com.au
P:(02) 6650 3300
F:(02) 6651 7044
W: <https://hibbardhomes.com.au/>

COPYRIGHT & NOTES

figured dimensions to be used in reference to scaling - all dimensions to be checked on site .Copying of this plan is strictly prohibited without written permission of Hibbard Homes . All boundaries and contours subject to survey

DESIGN
KIATO 225 SG22 W02 RHG



JOB ADDRESS

LOT 1808 ZILLIE CLOSE
DUBBO NSW 2830

PROPOSAL **NEW DWELLING** **DP:** **1318131**


drawing title		LANDSCAPE PLAN			
date	issue	description		JOB No.	11439
09/01/26	1	ISSUED FOR CC APPROVAL		SCALE	1:200 printed to A3 size
				DRAWN	ML
				DATE	13/01/2026
				WIND	'N2'
				SITE	
				revision	1
				PAGE	4

Note: refer to slab layout sheet for slab setout

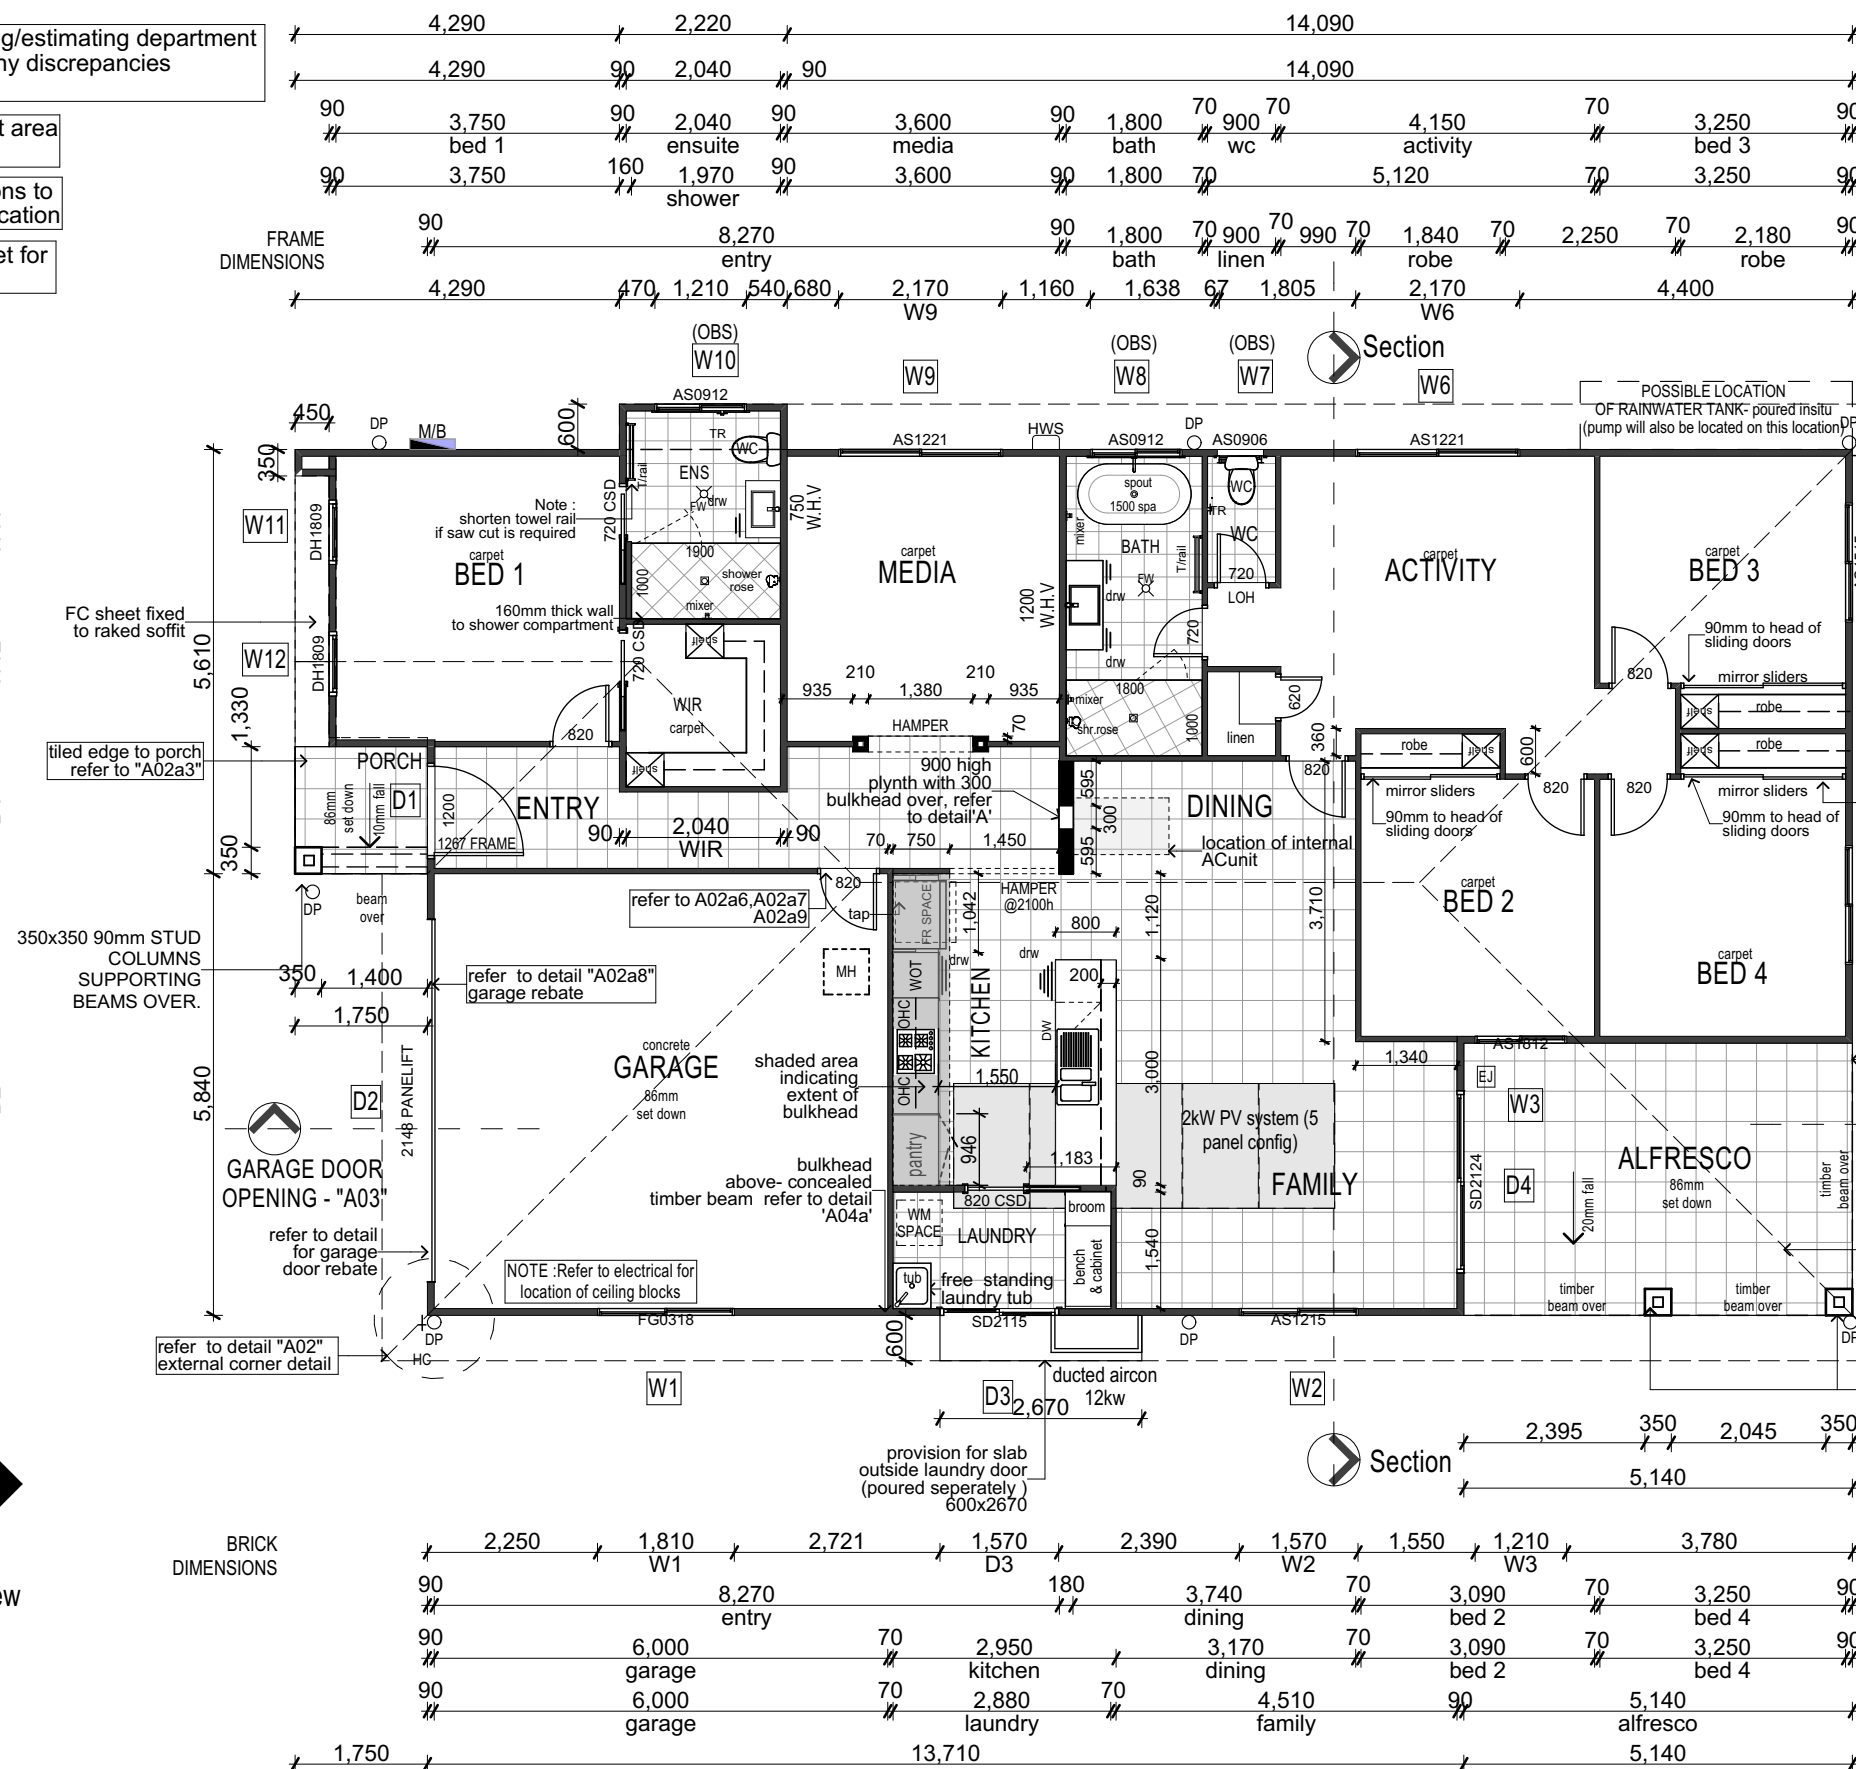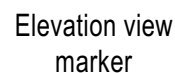

Areas	
Living	168.38 m ²
Garage	35.56 m ²
Alfresco	18.50 m ²
Porch	3.20 m ²
Total :	225.93 m²
Perimeter:	64.70 Lm




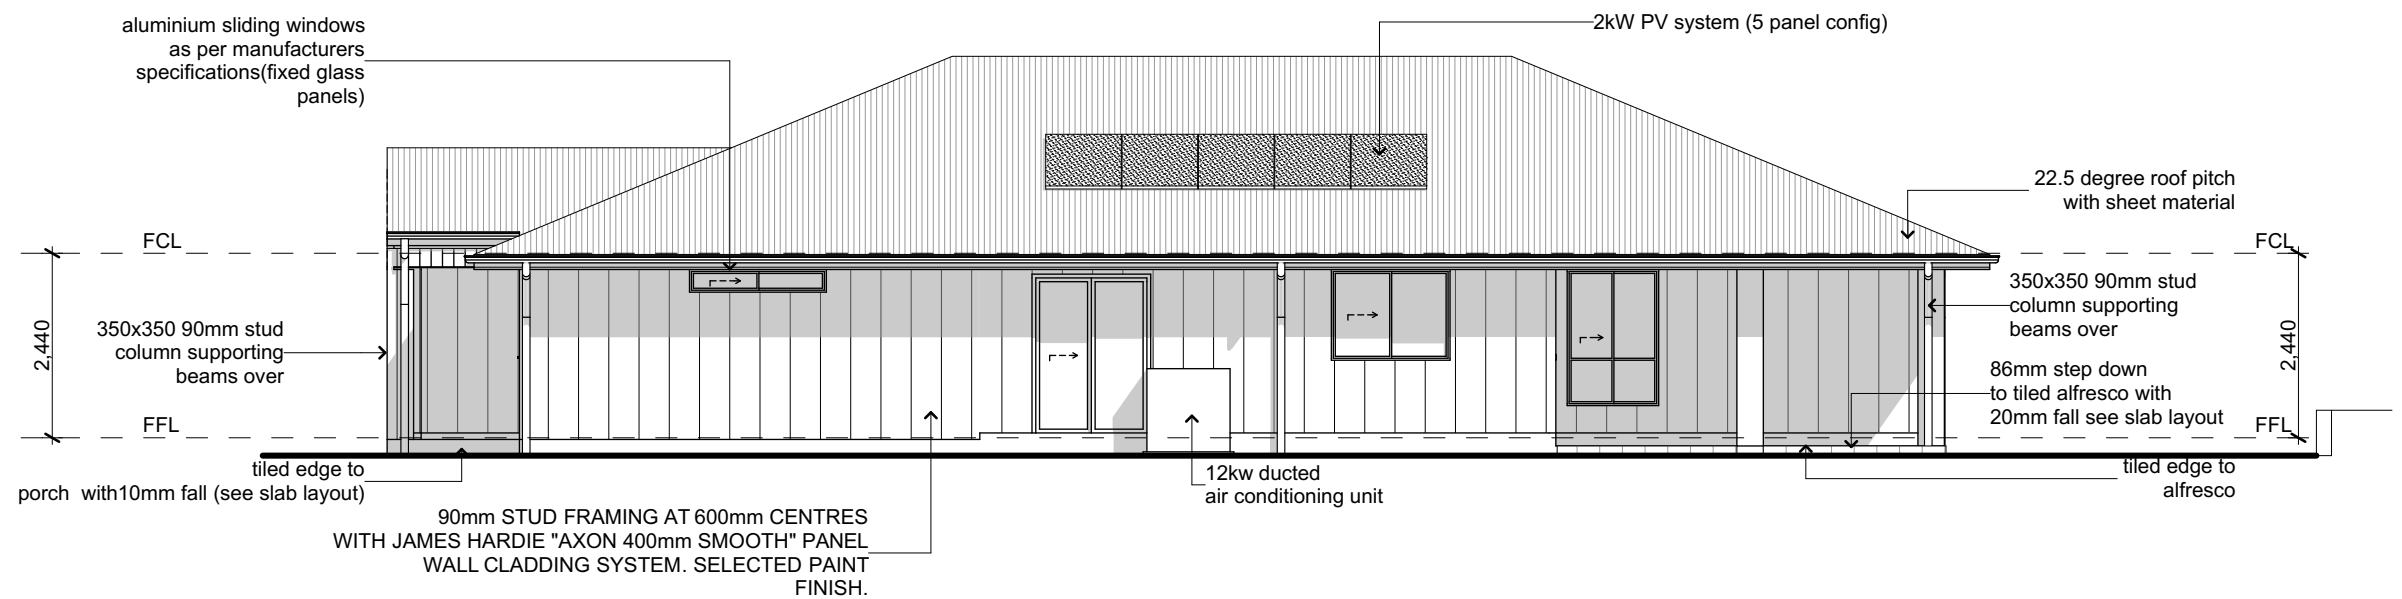

ELEVATION 1


NORTH

RIDGE HEIGHT RL: 319.48

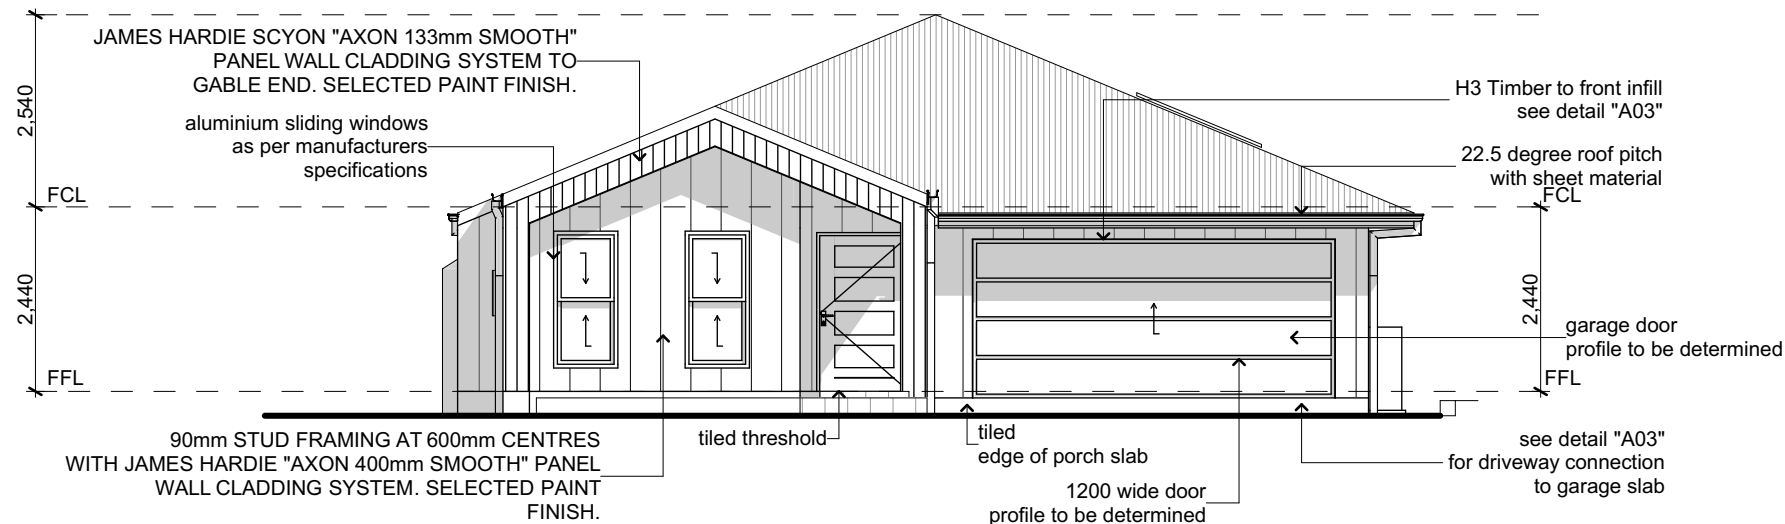

ELEVATION 2

EAST

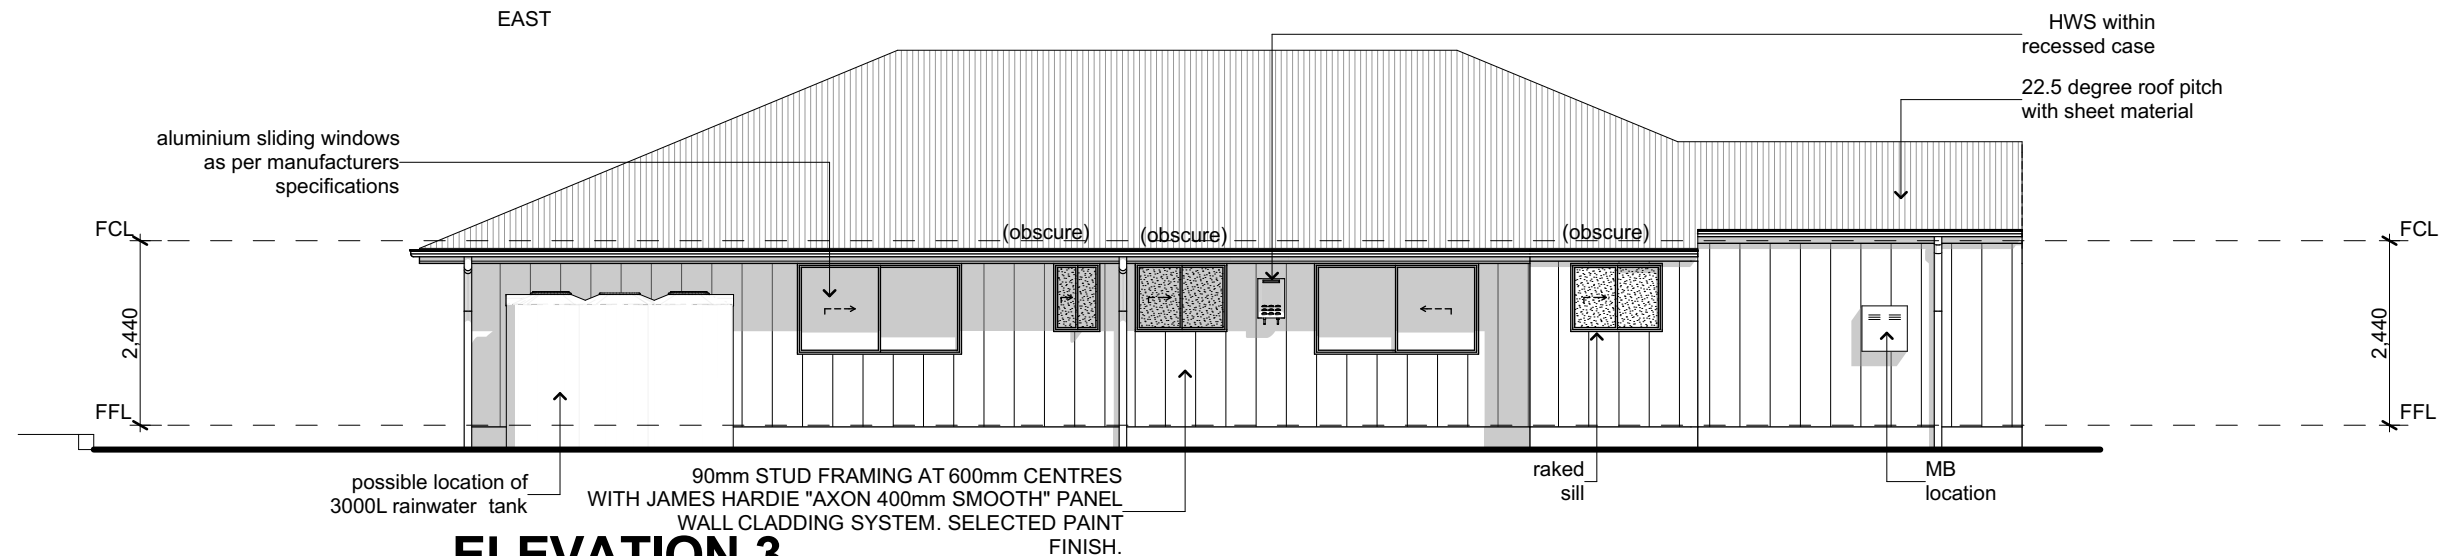

ELEVATION 3

SOUTH

Address:
130 West High Street
Coffs Harbour NSW 2450
Hibbards P/L ABN 22 057 895 020
E:coffs@hibbards.com.au
P:(02) 6650 3300
F:(02) 6651 7044
W: https://hibbardhomes.com.au/

COPYRIGHT & NOTES

figured dimensions to be used in reference to scaling - all dimensions to be checked on site. Copying of this plan is strictly prohibited without written permission of Hibbard Homes. All boundaries and contours subject to survey

DESIGN

KIATO 225 SG22 W02 RHG

JOB ADDRESS

LOT 1808 ZILLIE CLOSE
DUBBO NSW 2830


PROPOSAL

NEW DWELLING

DP:

1318131

drawing title			ELEVATIONS1-3			
date	issue	description		JOB No.	11439	revision
09/01/26	1	ISSUED FOR CC APPROVAL		SCALE	1:100	1
				DRAWN	ML	PAGE
				DATE	13/01/2026	6
				WIND	'N2'	SITE

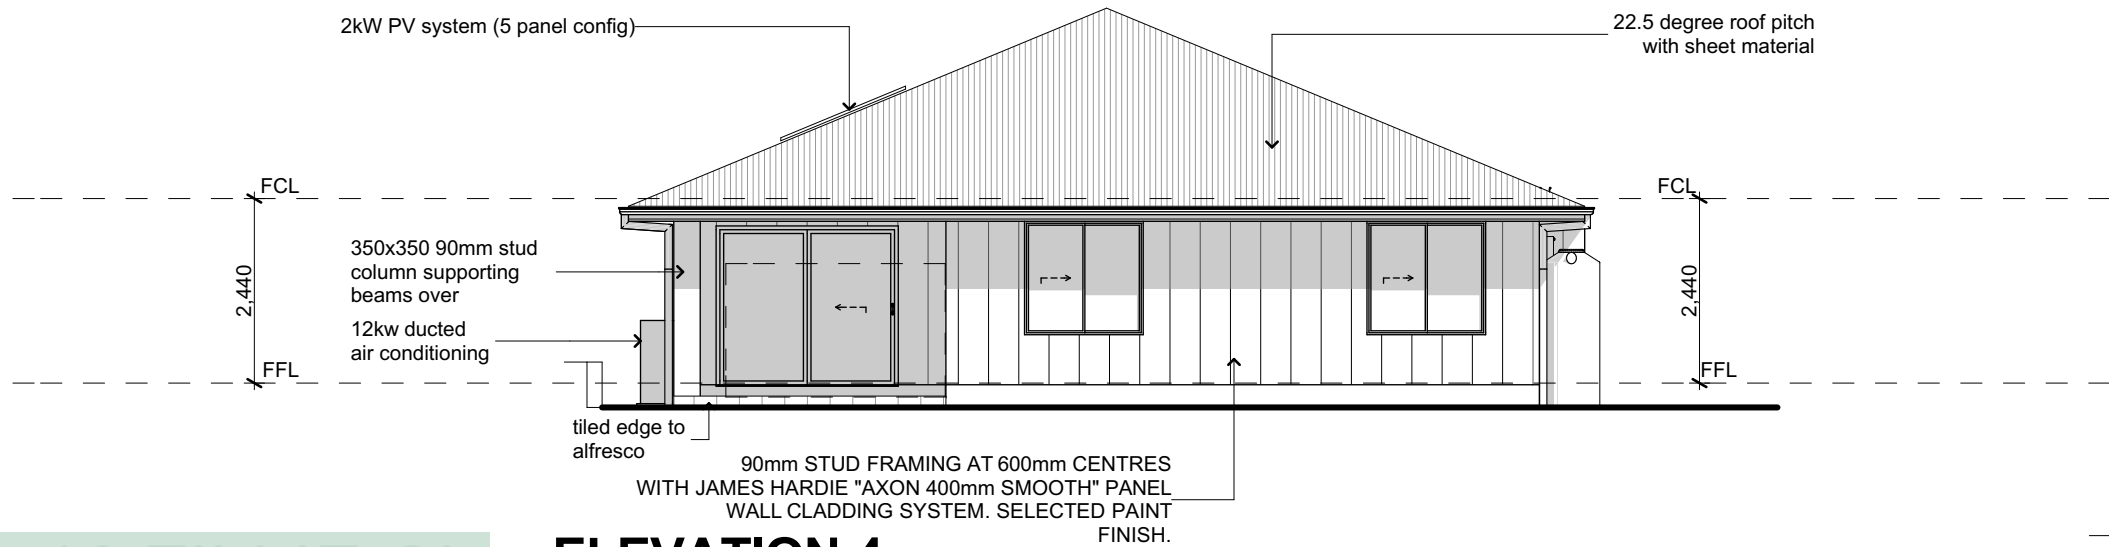

ELEVATION 4
WEST




Certificate No. # 09MUU5PPKV

Scan QR code or follow website link for rating details.

Assessor name: SANTARITA KOLLOSCHKE
Accreditation No. HERA10183
Property Address: 16 Zillie Close, Westdale, NSW, 2830



<https://www.fr5.com.au/QRCodeLanding?PublicId=09MUU5PPKV>

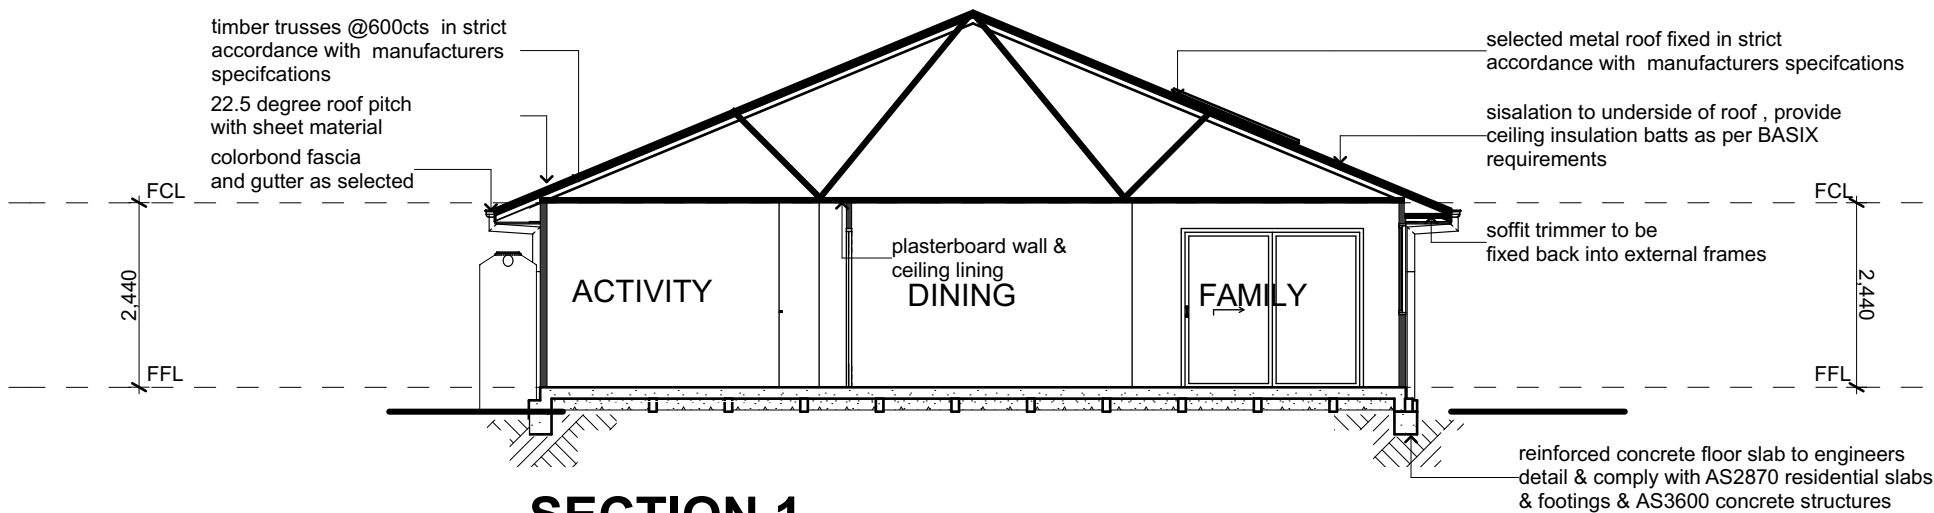


SECTION 1


Note : The wind classification of N2 is in accordance with AS1684-2010 , the tie down and bracing details are to be provided to the PCA prior to the relevant inspection

Note : Termite Protection
Termite protection is to be in accordance with AS3660-1 and installed in accordance with manufacturers specifications


Note : Cabintery
Please refer to internal elevations for cabinietry designs

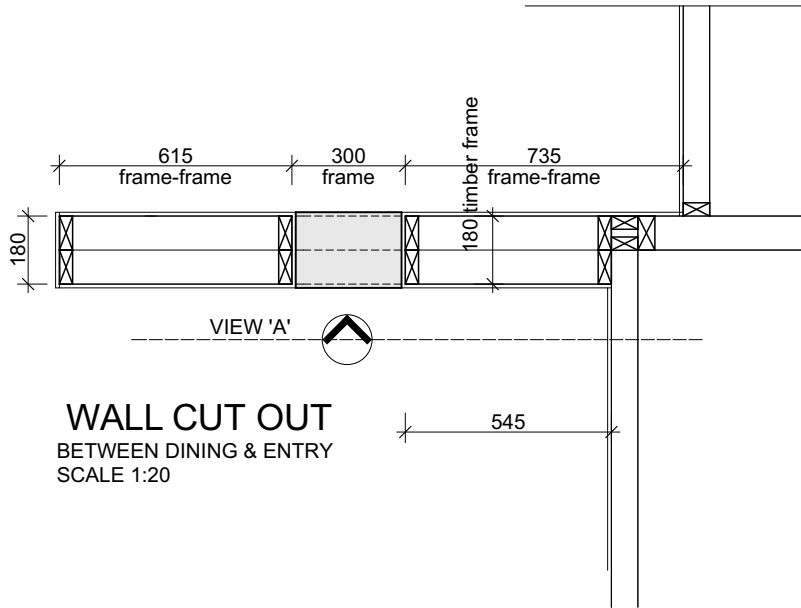

WALL CUT OUT
BETWEEN DINING & ENTRY
SCALE 1:20

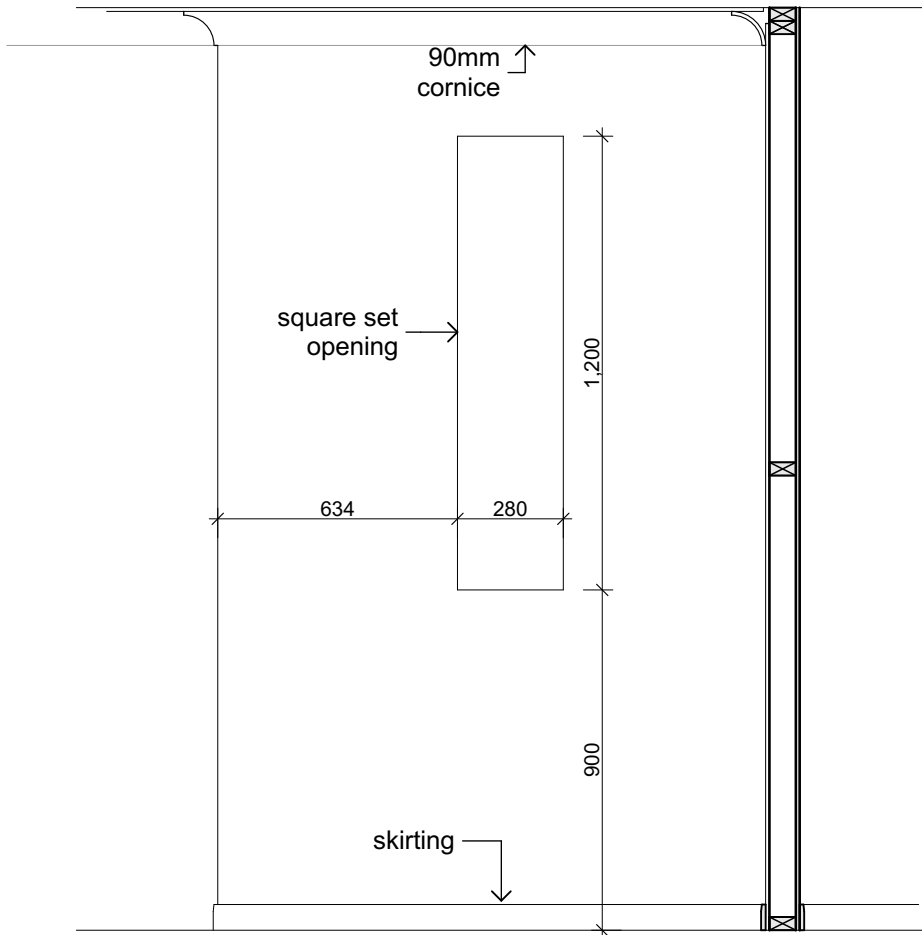

VIEW 'A'
as viewed from Dining Room
BETWEEN DINING & ENTRY
SCALE 1:20

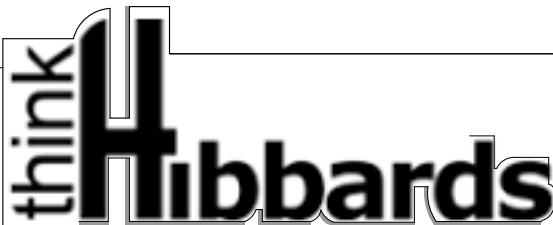

Address:
130 West High Street
Coffs Harbour NSW 2450
Hibbards P/L ABN 22 057 895 020
E:coffs@hibbards.com.au
P:(02) 6650 3300
F:(02) 6651 7044
W: <https://hibbardhomes.com.au/>

COPYRIGHT & NOTES

figured dimensions to be used in reference to scaling - all dimensions to be checked on site .Copying of this plan is strictly prohibited without written permission of Hibbard Homes . All boundaries and contours subject to survey

DESIGN
KIATO 225 SG22 W02 RHG

JOB ADDRESS

**LOT 1808 ZILLIE CLOSE
DUBBO NSW 2830**

PROPOSAL NEW DWELLING DP: 1318131

drawing title			ELEVATION 4 & SECTION				
date	issue	description		JOB No.	11439	revision	
09/01/26	1	ISSUED FOR CC APPROVAL		SCALE	1:100	1	
				DRAWN	ML	PAGE	
				DATE	13/01/2026	7	
				WIND	'N2'	SITE	

Note :Wall hung basin waste pipe is to be centre line of wall stud framing .
Laundry Tub waste pipe is nominally offset from wall 125mm to centre of pipe

Note :dimensions to penetrations is using a running dimension method from external edge of slab to centre of hole

Note :Please notify the drafting department at Hibbards head office for any discrepancies in details and dimensions

Note : Plumbing penetrations are located from external edge of brickwork - dimensioned as a running dimension



Certificate No. # 09MUU5PPKV

Scan QR code or follow website link for rating details.

Assessor name

Accreditation No.

Property Address



SANTARITA KOLLOSCHKE

HERA10183

16 Zillie Close ,
Westdale, NSW, 2830



https://www.fr5.com.au/QRCodeLanding?PublicId=09MUU5PPKV

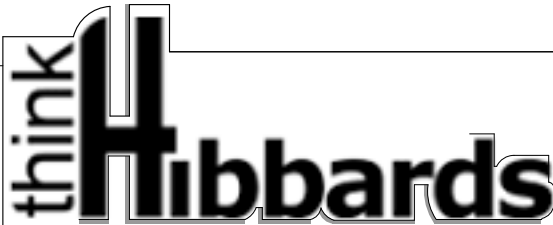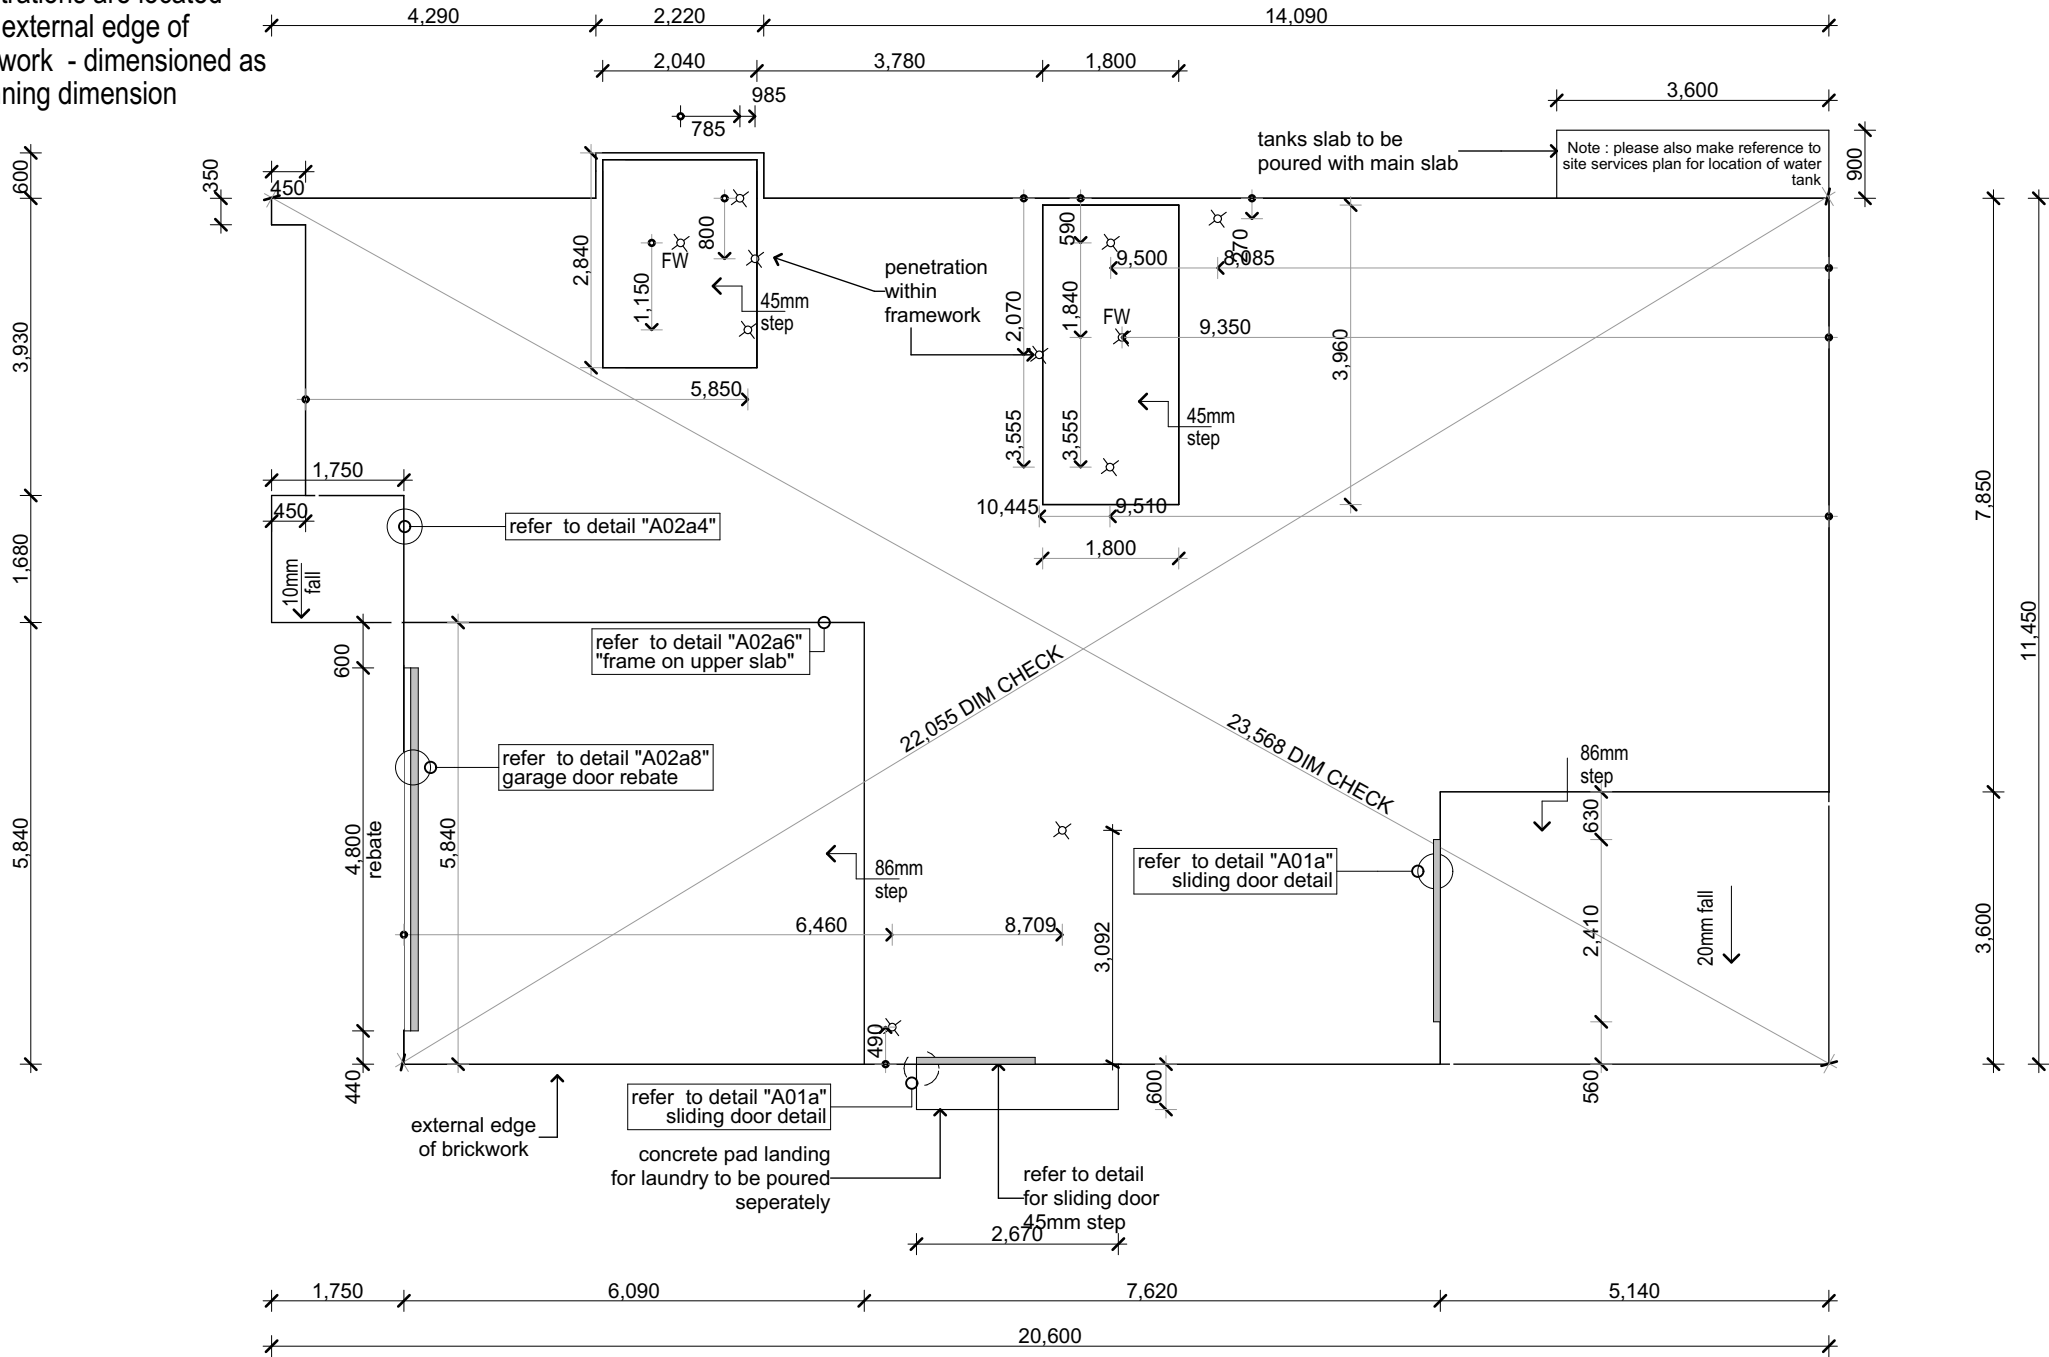

Address:
130 West High Street
Coffs Harbour NSW 2450
Hibbards P/L ABN 22 057 895 020
E:coffs@hibbards.com.au
P:(02) 6650 3300
F:(02) 6651 7044
W: https://hibbardhomes.com.au/

COPYRIGHT & NOTES
figured dimensions to be used in reference to scaling - all dimensions to be checked on site .Copying of this plan is strictly prohibited without written permission of Hibbard Homes . All boundaries and contours subject to survey
DESIGN
KIATO 225 SG22 W02 RHG

JOB ADDRESS
LOT 1808 ZILLIE CLOSE
DUBBO NSW 2830
PROPOSAL **NEW DWELLING** **DP:** **1318131**

drawing title			SLAB PLAN			
date	issue	description		JOB No.	11439	revision
09/01/26	1	ISSUED FOR CC APPROVAL		SCALE	1:100	1
				DRAWN	ML	PAGE
				DATE	13/01/2026	8
				WIND	'N2'	SITE



Certificate No. # 09MUU5PPKV

Scan QR code or follow website link for rating details.

Assessor name

SANTARITA KOLLOSCHKE

Accreditation No.


HERA10183

Property Address

16 Zillie Close ,
Westdale, NSW, 2830



<https://www.fr5.com.au/QRCodeLanding?PublicId=09MUU5PPKV>

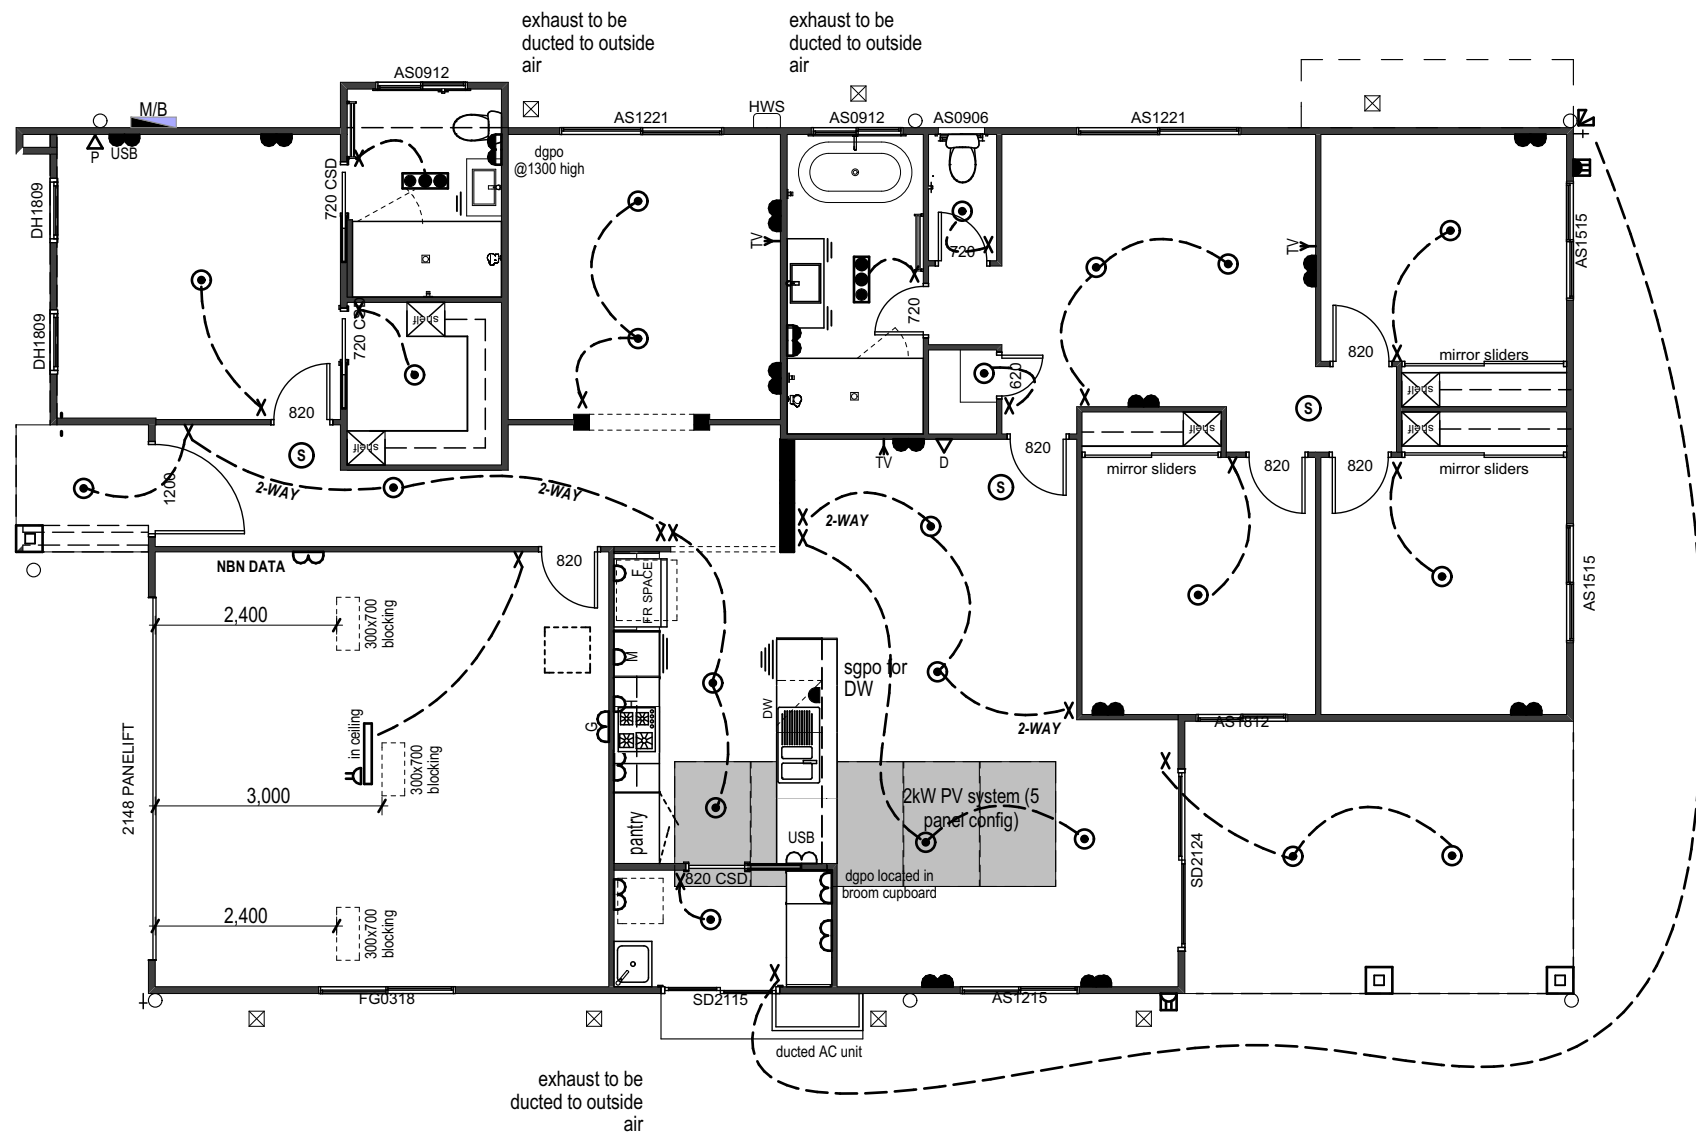


NOTE:
ALL EXTERNAL LIGHTS WILL BE SHIELDED TO
PREVENT LIGHT ABOVE HORIZONTAL

LIGHTING LEGEND

- SINGLE @ 300
- DOUBLE @ 300 - USB
- DOUBLE @ 300
- SINGLE @ 1050
- DOUBLE @ 1050 - USB
- DOUBLE @ 1050
- APPLIANCE SHELF DOUBLE @ 1600
- VANITY @ 1100
- GARAGE @ 1350
- FRIDGE @ 1650
- MICROWAVE @ 1650
- RANGEHOOD @1650
- LIGHT SWITCH
- DOWNLIGHT
- TV
- PHONE
- DUCTED EXHAUST FAN
- PANELIFT GPO
- FLUORO LIGHT
- 2-WAY 2 WAY CIRCUIT
- DOUBLE WATERPROOF GPO @ 1050
- SINGLE WATERPROOF GPO @ 1050
- SMOKE ALARMS BY ELECTRICIAN TO AS3786
- DATA POINT
- GAS POINT (DUBBO, TAMWORTH & MUDGEE)
- NBN DATA NBN DATA POINT @ 1050
- DOUBLE SPOT
- BUNKER LIGHT
- DUCTED EXHAUST
- DUCTED GRILL
- 2 IN 1 DUCTED EXHAUST FAN/LIGHT
- 2 IN 1 NON-DUCTED EXHAUST FAN/LIGHT
- 3 IN 1 FAN / LIGHT / HEAT
- EVAPORATIVE COOLER POINT (DUBBO, TAMWORTH & MUDGEE)

NOTE:
THIS IS A GENERIC ELECTRICAL PLAN ONLY.
THE LAYOUT, LOCATION OF POINTS, LIGHTS
AND OUTLETS SHOWN MAY ALTER WITHOUT
NOTIFICATION, DUE TO COUCIL
REQUIREMENTS, BUILDING LOCATION AND/OR
OTHER UNFORSEEN CIRCUMSTANCES

ALL PRODUCTS AND
FINISHES AS PER BUILDERS
SPECIFICATIONS

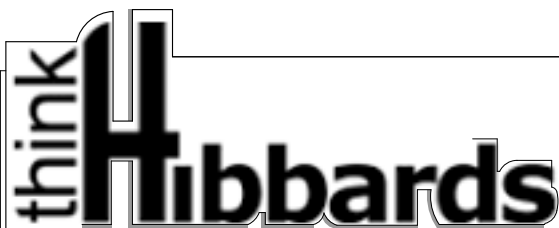


Address:
130 West High Street
Coffs Harbour NSW 2450
Hibbards P/L ABN 22 057 895 020
E:coffs@hibbards.com.au
P:(02) 6650 3300
F:(02) 6651 7044
W: <https://hibbardhomes.com.au/>

COPYRIGHT & NOTES
figured dimensions to be used in reference to scaling - all
dimensions to be checked on site .Copying of this plan is
strictly prohibited without written permission of Hibbard
Homes . All boundaries and contours subject to survey
DESIGN
KIATO 225 SG22 W02 RHG

JOB ADDRESS
**LOT 1808 ZILLIE CLOSE
DUBBO NSW 2830**
PROPOSAL **NEW DWELLING** **DP:** **1318131**

drawing title			ELECTRICAL PLAN				
date	issue	description			JOB No.	11439	revision
09/01/26	1	ISSUED FOR CC APPROVAL			SCALE	1:100	1
					DRAWN	ML	PAGE
					DATE	13/01/2026	9
					WIND	'N2'	SITE

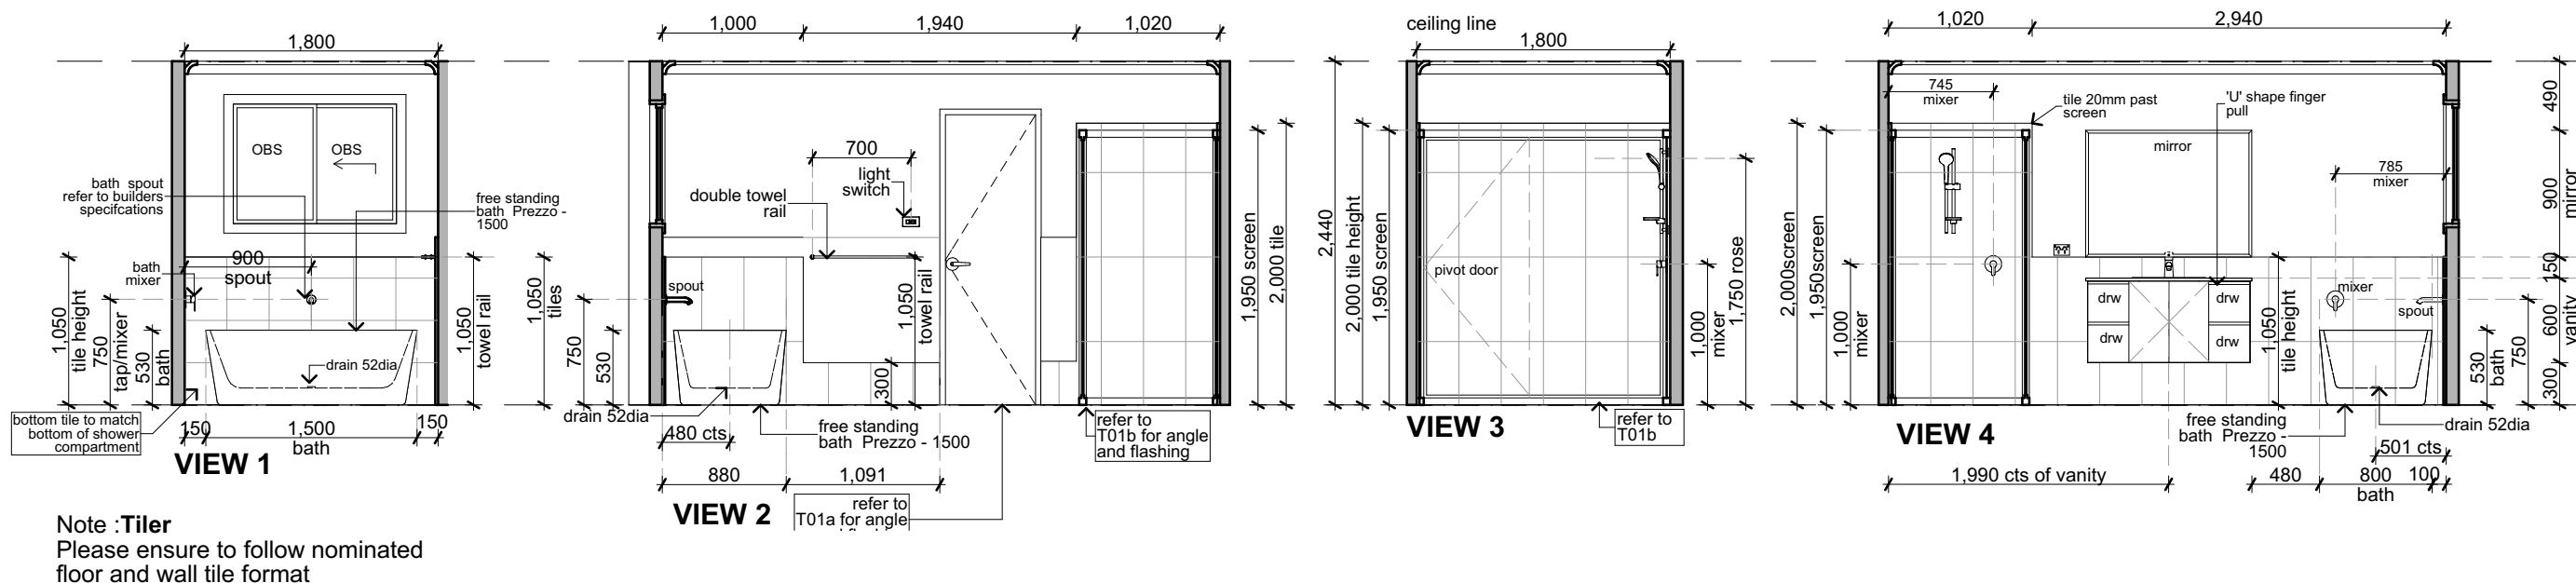

TR

720° switch

VIEW 1

700 toilet roll

450

1,050

OBS OBS

VIEW 2

260

light switch

1,300

300

VIEW 3

2,440

referto T01a for angle

VIEW 4


700 toilet roll


300

700


toilet roll

Note :Tiler
Please ensure to follow nominated floor and wall tile format

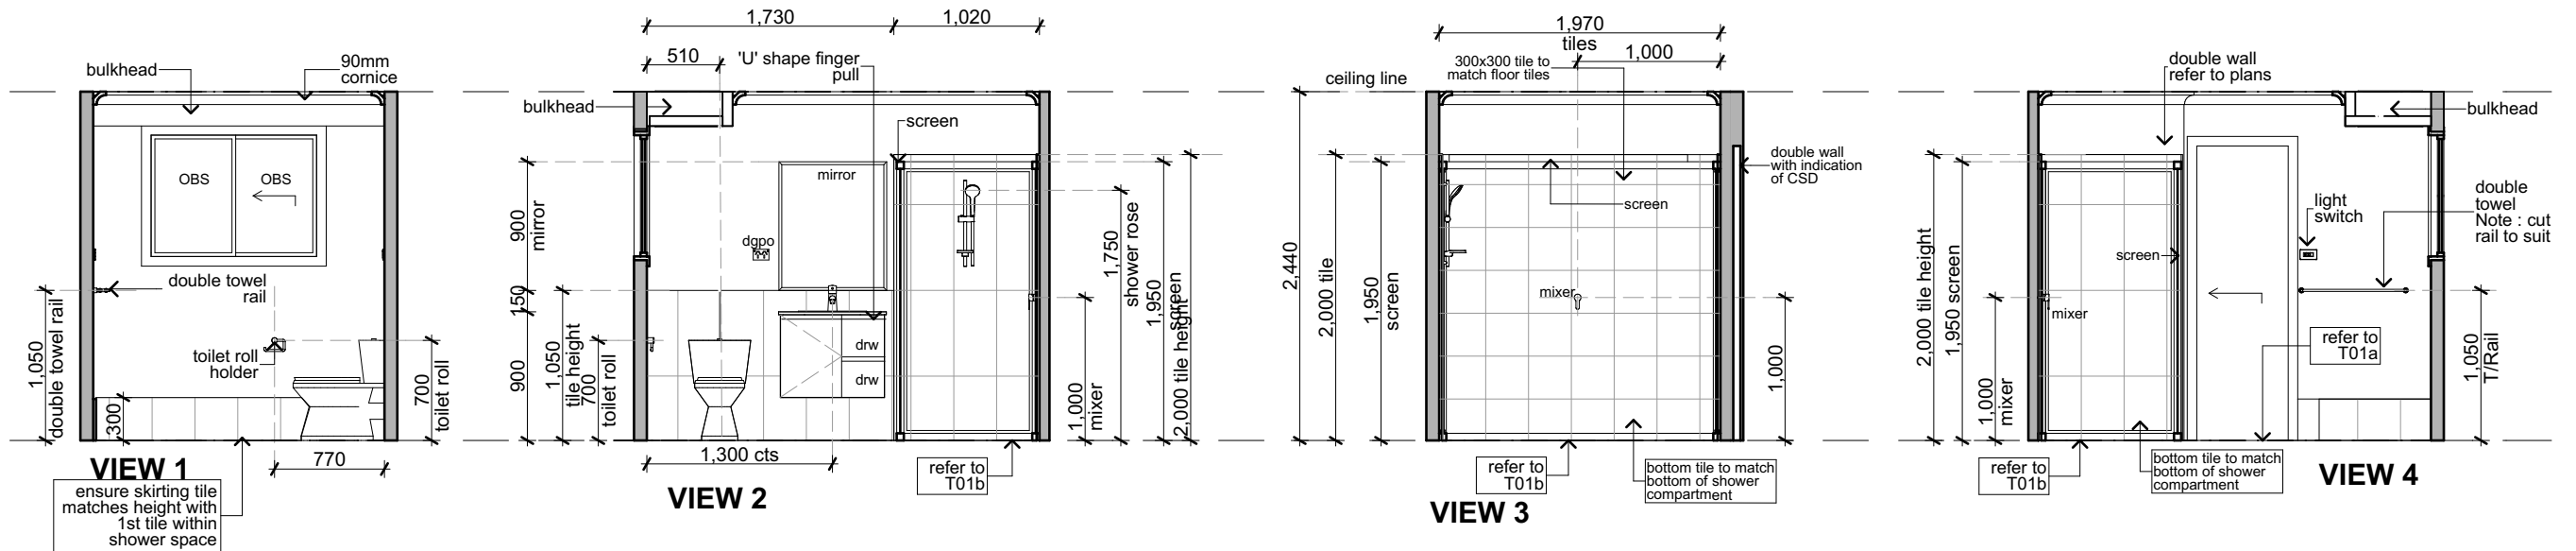

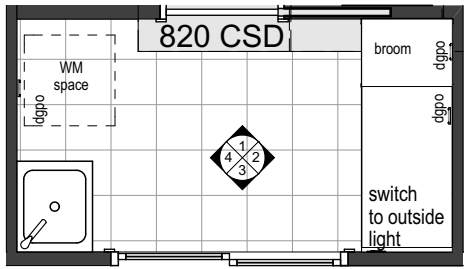


LAUNDRY LAYOUT

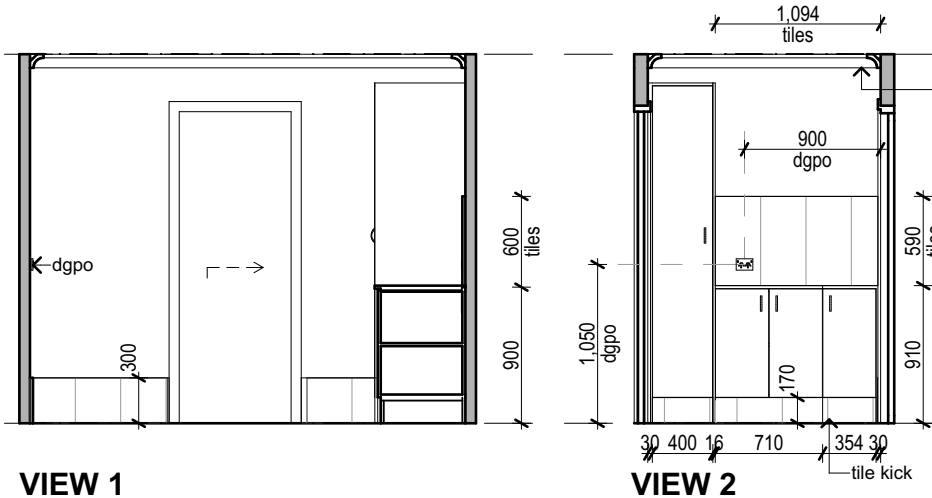


VIEW 1

VIEW 2


Note :Tiler
Please ensure to follow nominated
floor and wall tile format

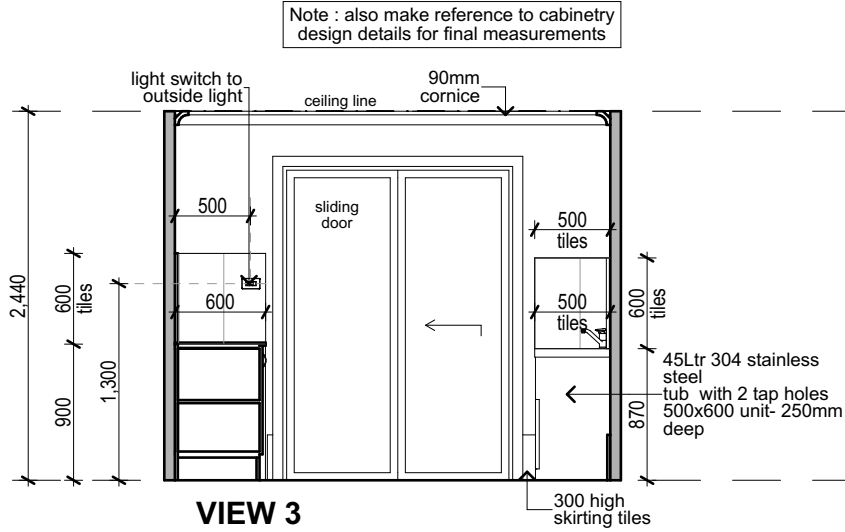


VIEW 3

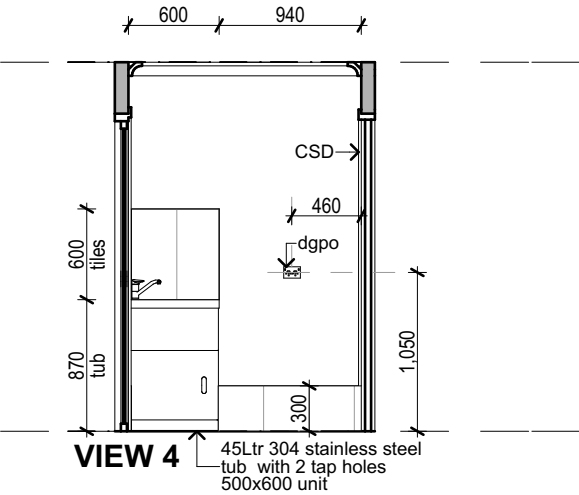


VIEW 4

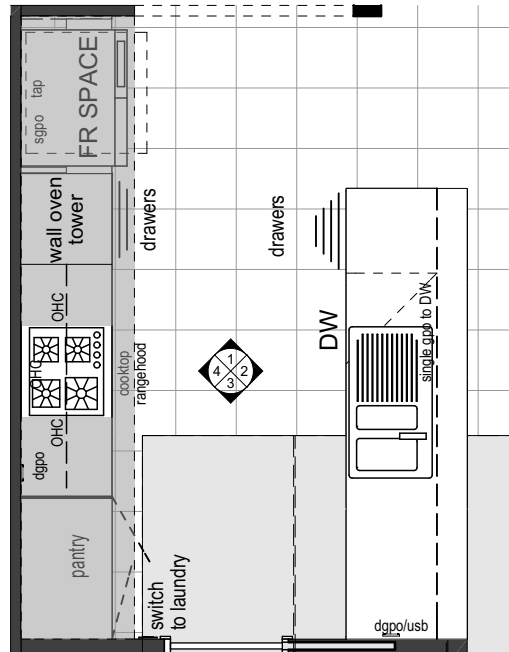


KITCHEN LAYOUT

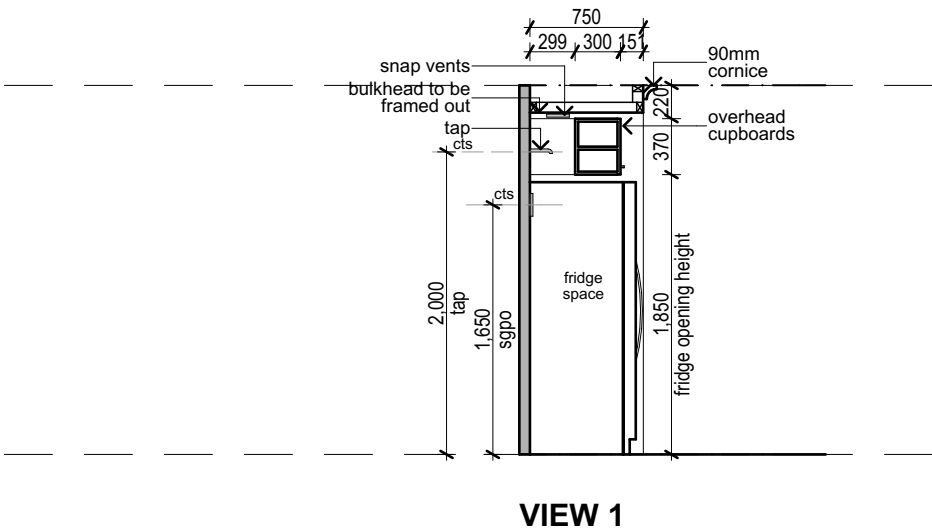

VIEW 1

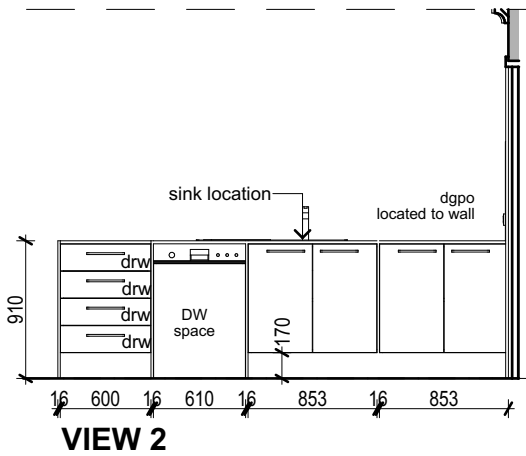


VIEW 2

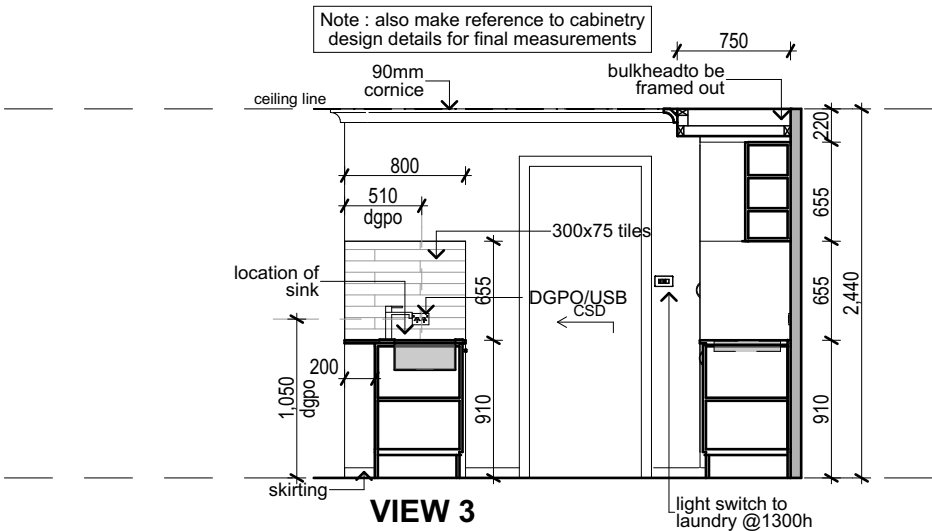


VIEW 3

light switch to
laundry @1300h

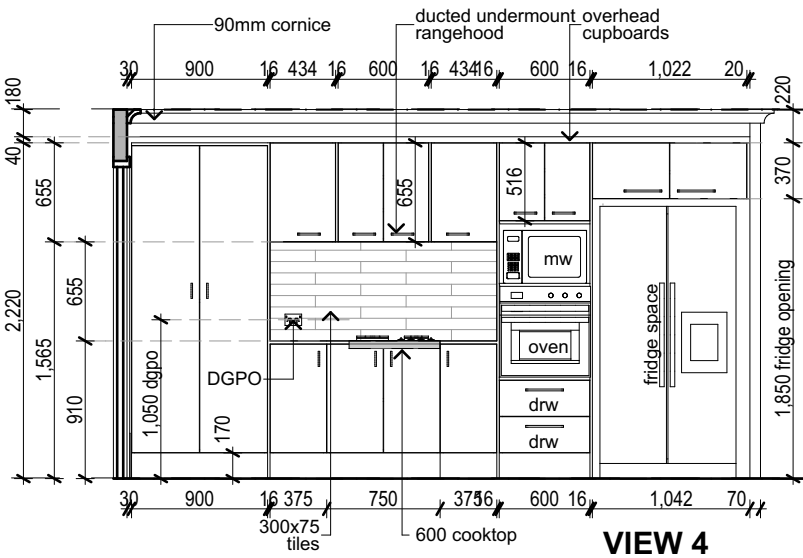

VIEW 4

Note :Tiler
Please ensure to follow nominated
floor and wall tile format

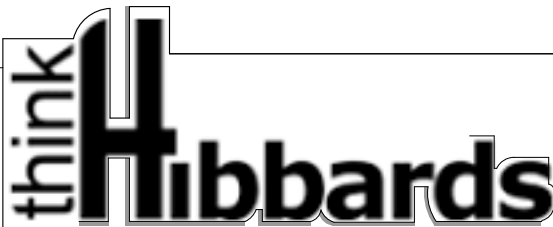


Address:
130 West High Street
Coffs Harbour NSW 2450
Hibbards P/L ABN 22 057 895 020
E:coffs@hibbards.com.au
P:(02) 6650 3300
F:(02) 6651 7044
W: https://hibbardhomes.com.au/

COPYRIGHT & NOTES
figured dimensions to be used in reference to scaling - all
dimensions to be checked on site .Copying of this plan is
strictly prohibited without written permission of Hibbard
Homes . All boundaries and contours subject to survey
DESIGN
KIATO 225 SG22 W02 RHG


JOB ADDRESS
LOT 1808 ZILLIE CLOSE
DUBBO NSW 2830
PROPOSAL NEW DWELLING DP: 1318131

drawing title			LAUNDRY / KITCHEN			
date	issue	description		JOB No.	11439	revision
09/01/26	1	ISSUED FOR CC APPROVAL		SCALE	1:50	1
				DRAWN	ML	PAGE
				DATE	13/01/2026	11
				WIND	'N2'	SITE

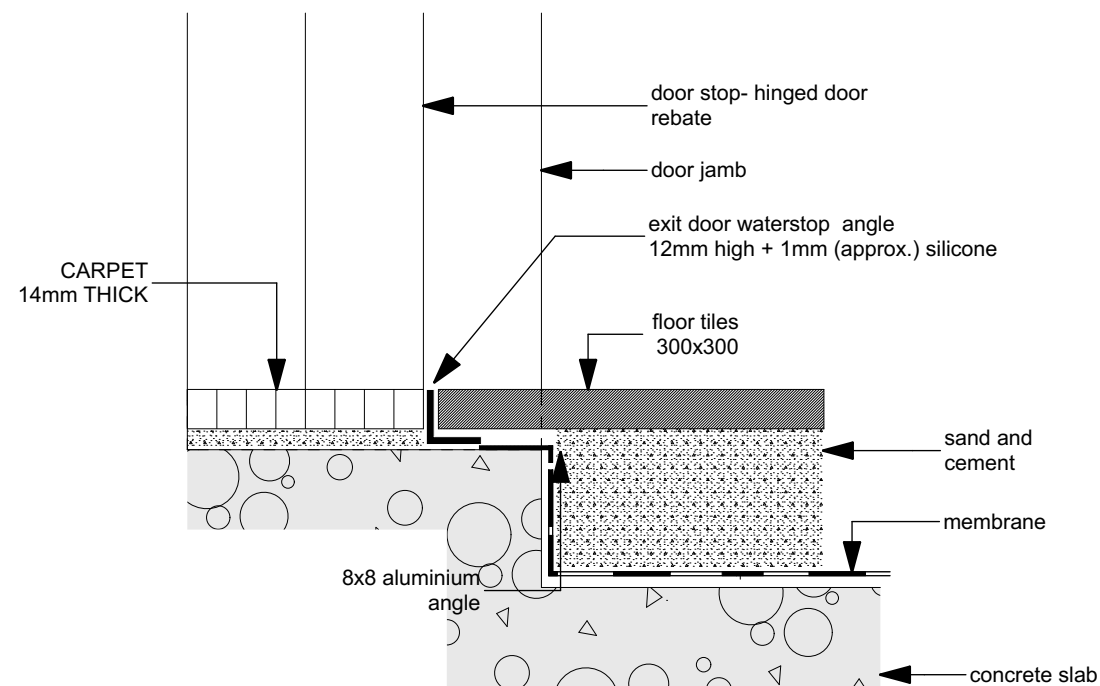


DETAIL 2

T01a

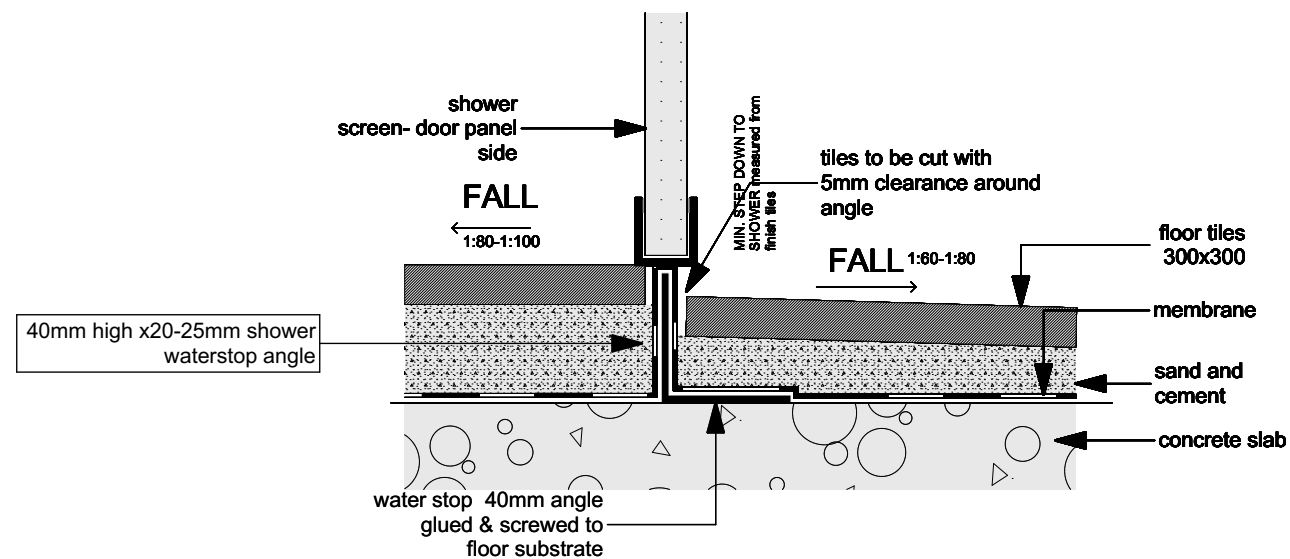


T01b




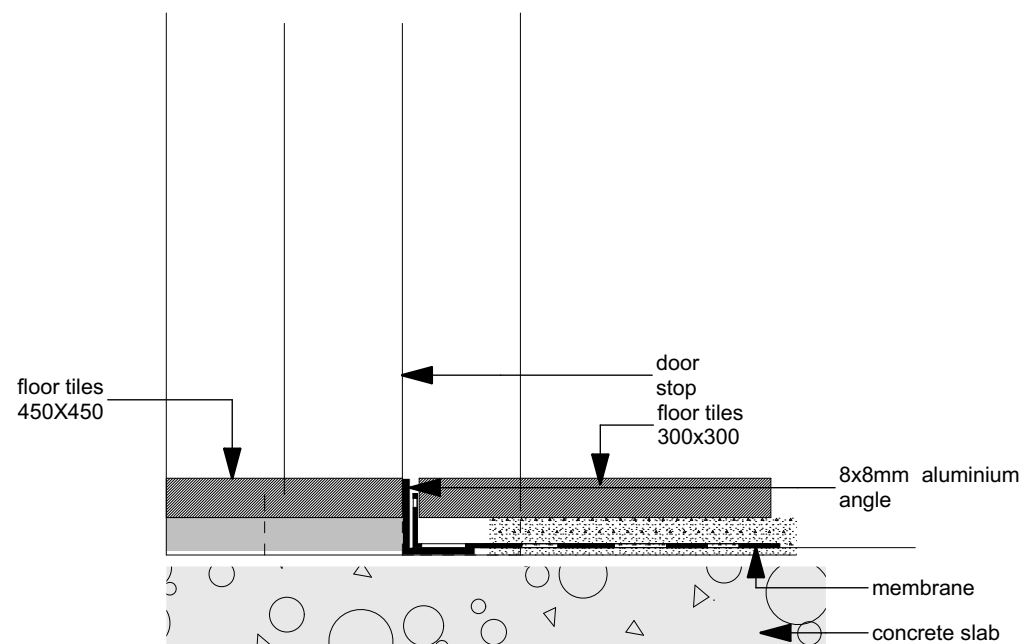


DETAIL 1

T01c




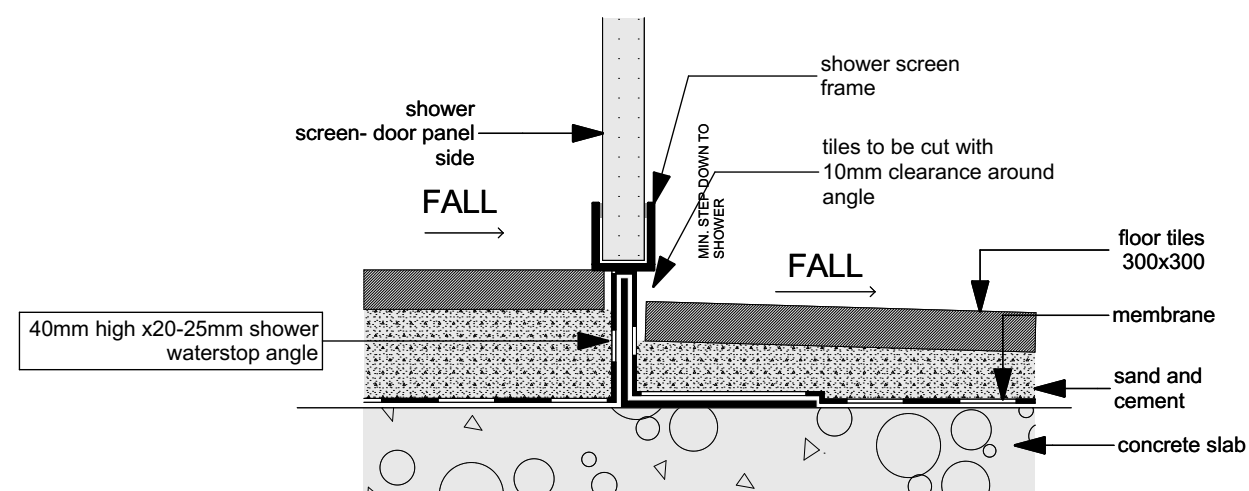


T01d

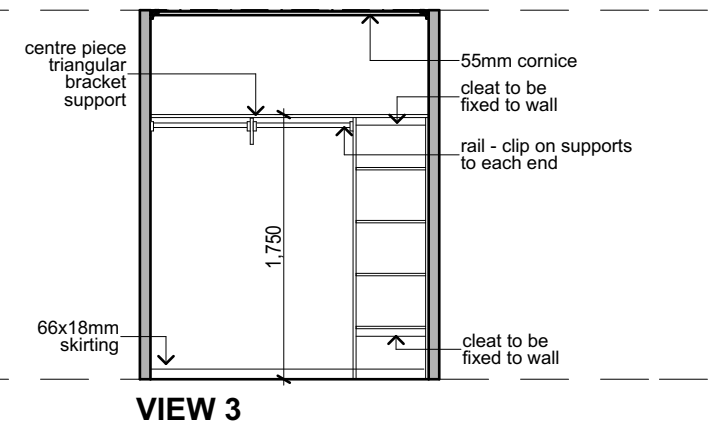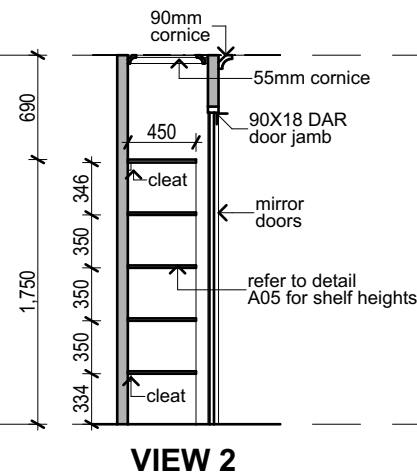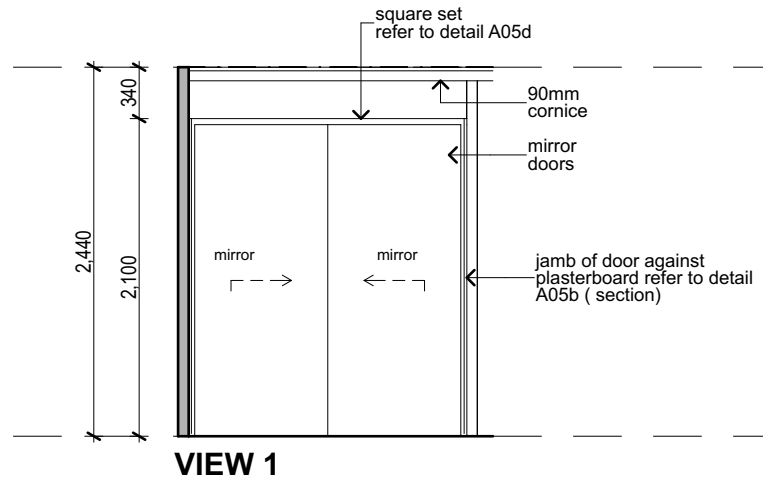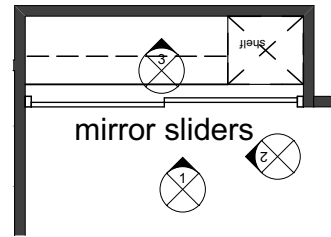


NOTE : HANGING RAIL TO HAVE MAXIMUM LENGTH OF 900mm UNTIL A TRIANGULAR BRACE SUPPORT IS REQUIRED

NOTE : HANGING RAIL TO HAVE MAXIMUM LENGTH OF 2600mm UNTIL A FULL BLADE FROM SHELF TO FLOOR SUPPORT IS REQUIRED

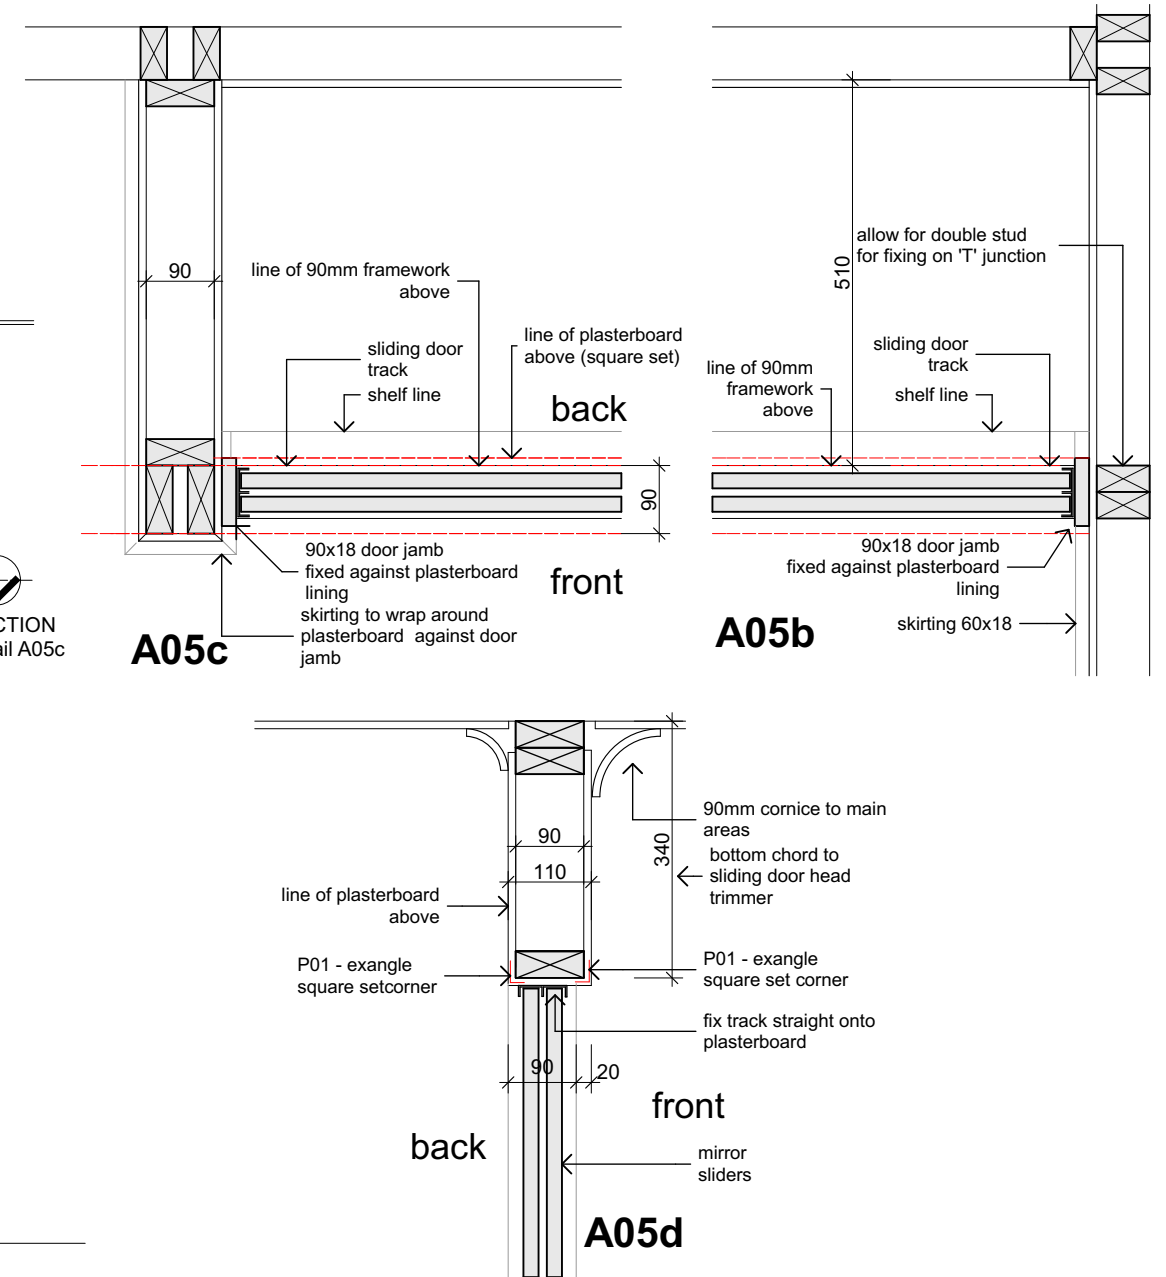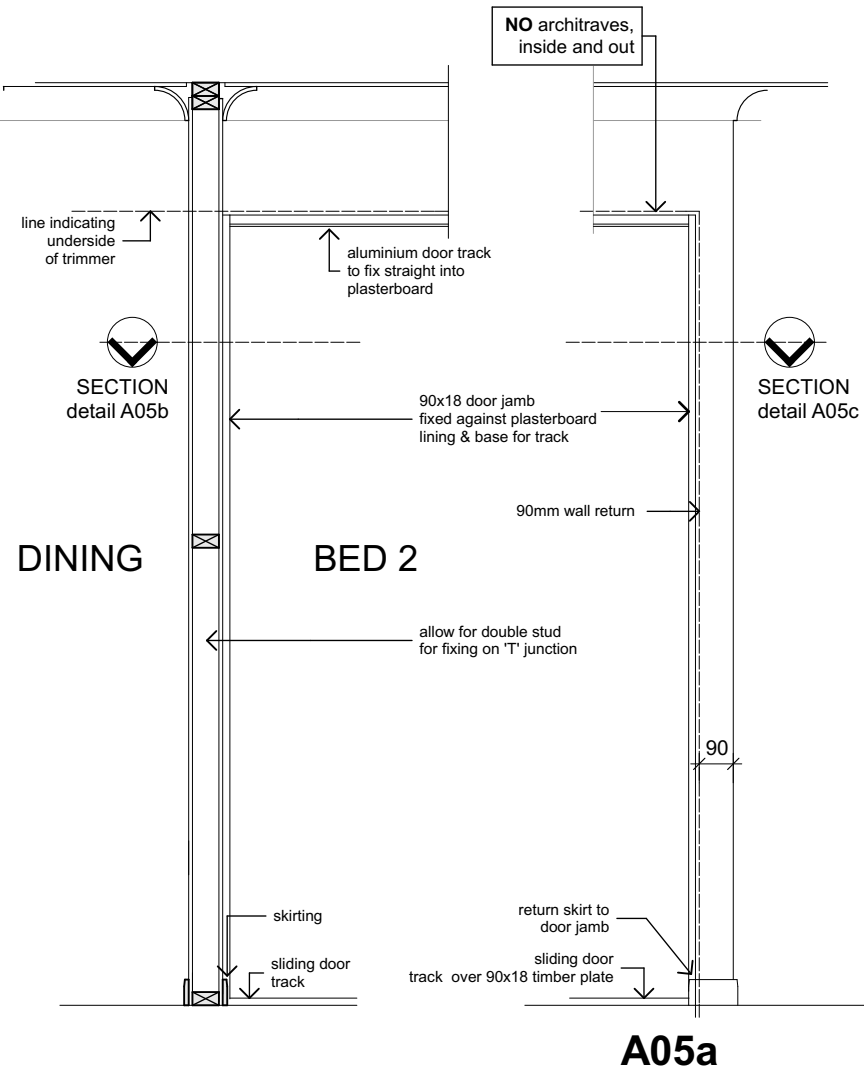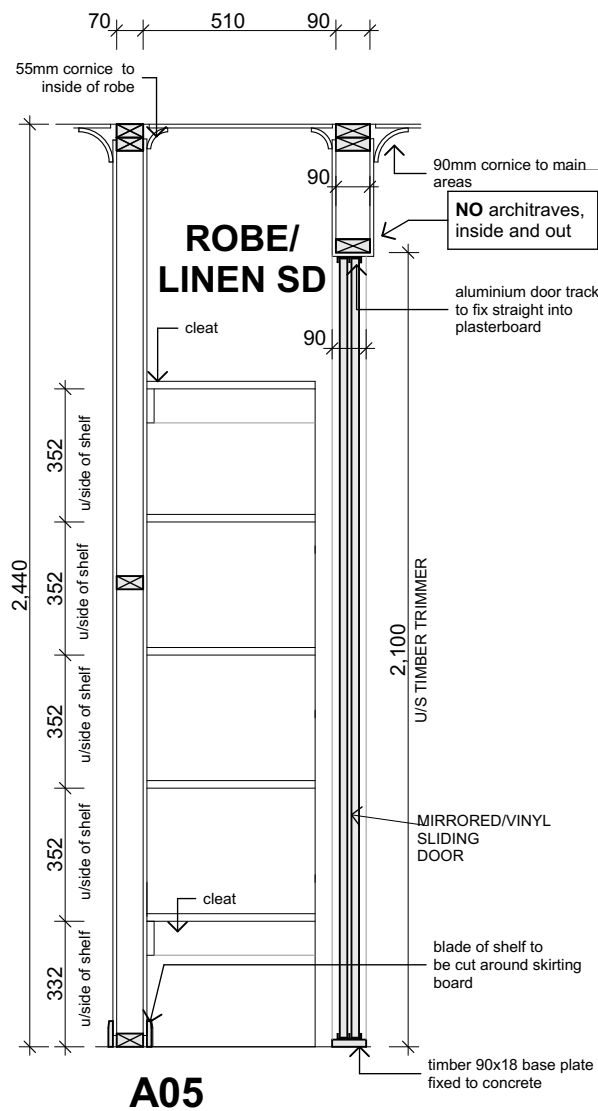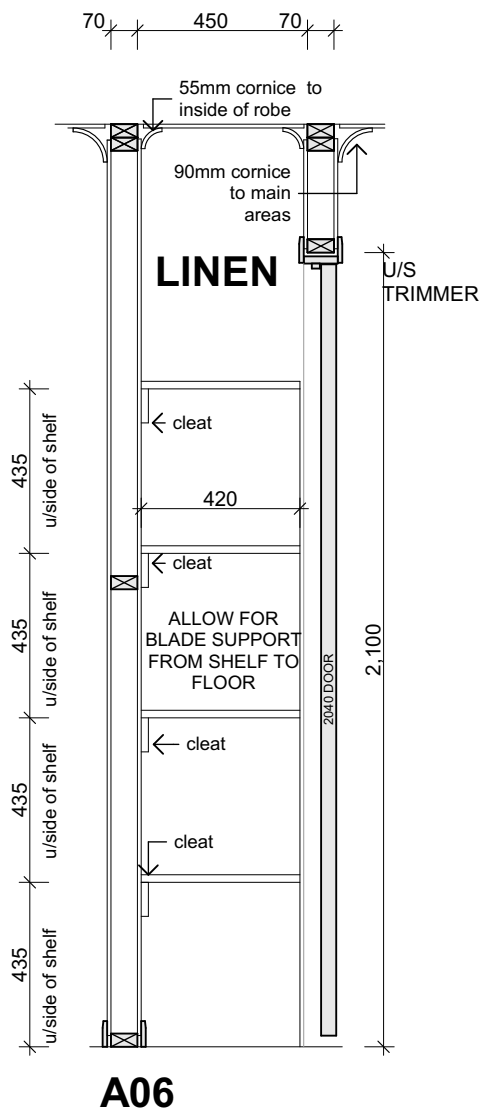

NOTE : AS VIEWED FROM FRONT FACE
VIEW 1

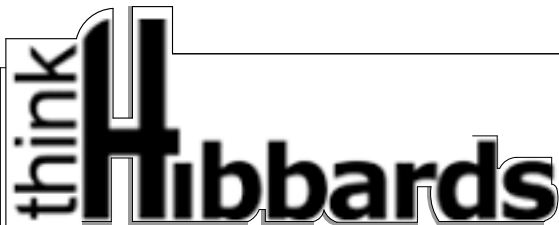


Address:
130 West High Street
Coffs Harbour NSW 2450
Hibbards P/L ABN 22 057 895 020
E:coffs@hibbards.com.au
P:(02) 6650 3300
F:(02) 6651 7044
W: https://hibbardhomes.com.au/


COPYRIGHT & NOTES
figured dimensions to be used in reference to scaling - all dimensions to be checked on site .Copying of this plan is strictly prohibited without written permission of Hibbard Homes . All boundaries and contours subject to survey
DESIGN
KIATO 225 SG22 W02 RHG

JOB ADDRESS
LOT 1808 ZILLIE CLOSE
DUBBO NSW 2830
PROPOSAL
NEW DWELLING
DP: 1318131

drawing title			ROBE/LINEN/CABINETRY			
date	issue	description		JOB No.	11439	revision
09/01/26	1	ISSUED FOR CC APPROVAL		SCALE	1:50,20,10	1
				DRAWN	ML	PAGE
				DATE	13/01/2026	13
				WIND	'N2'	SITE

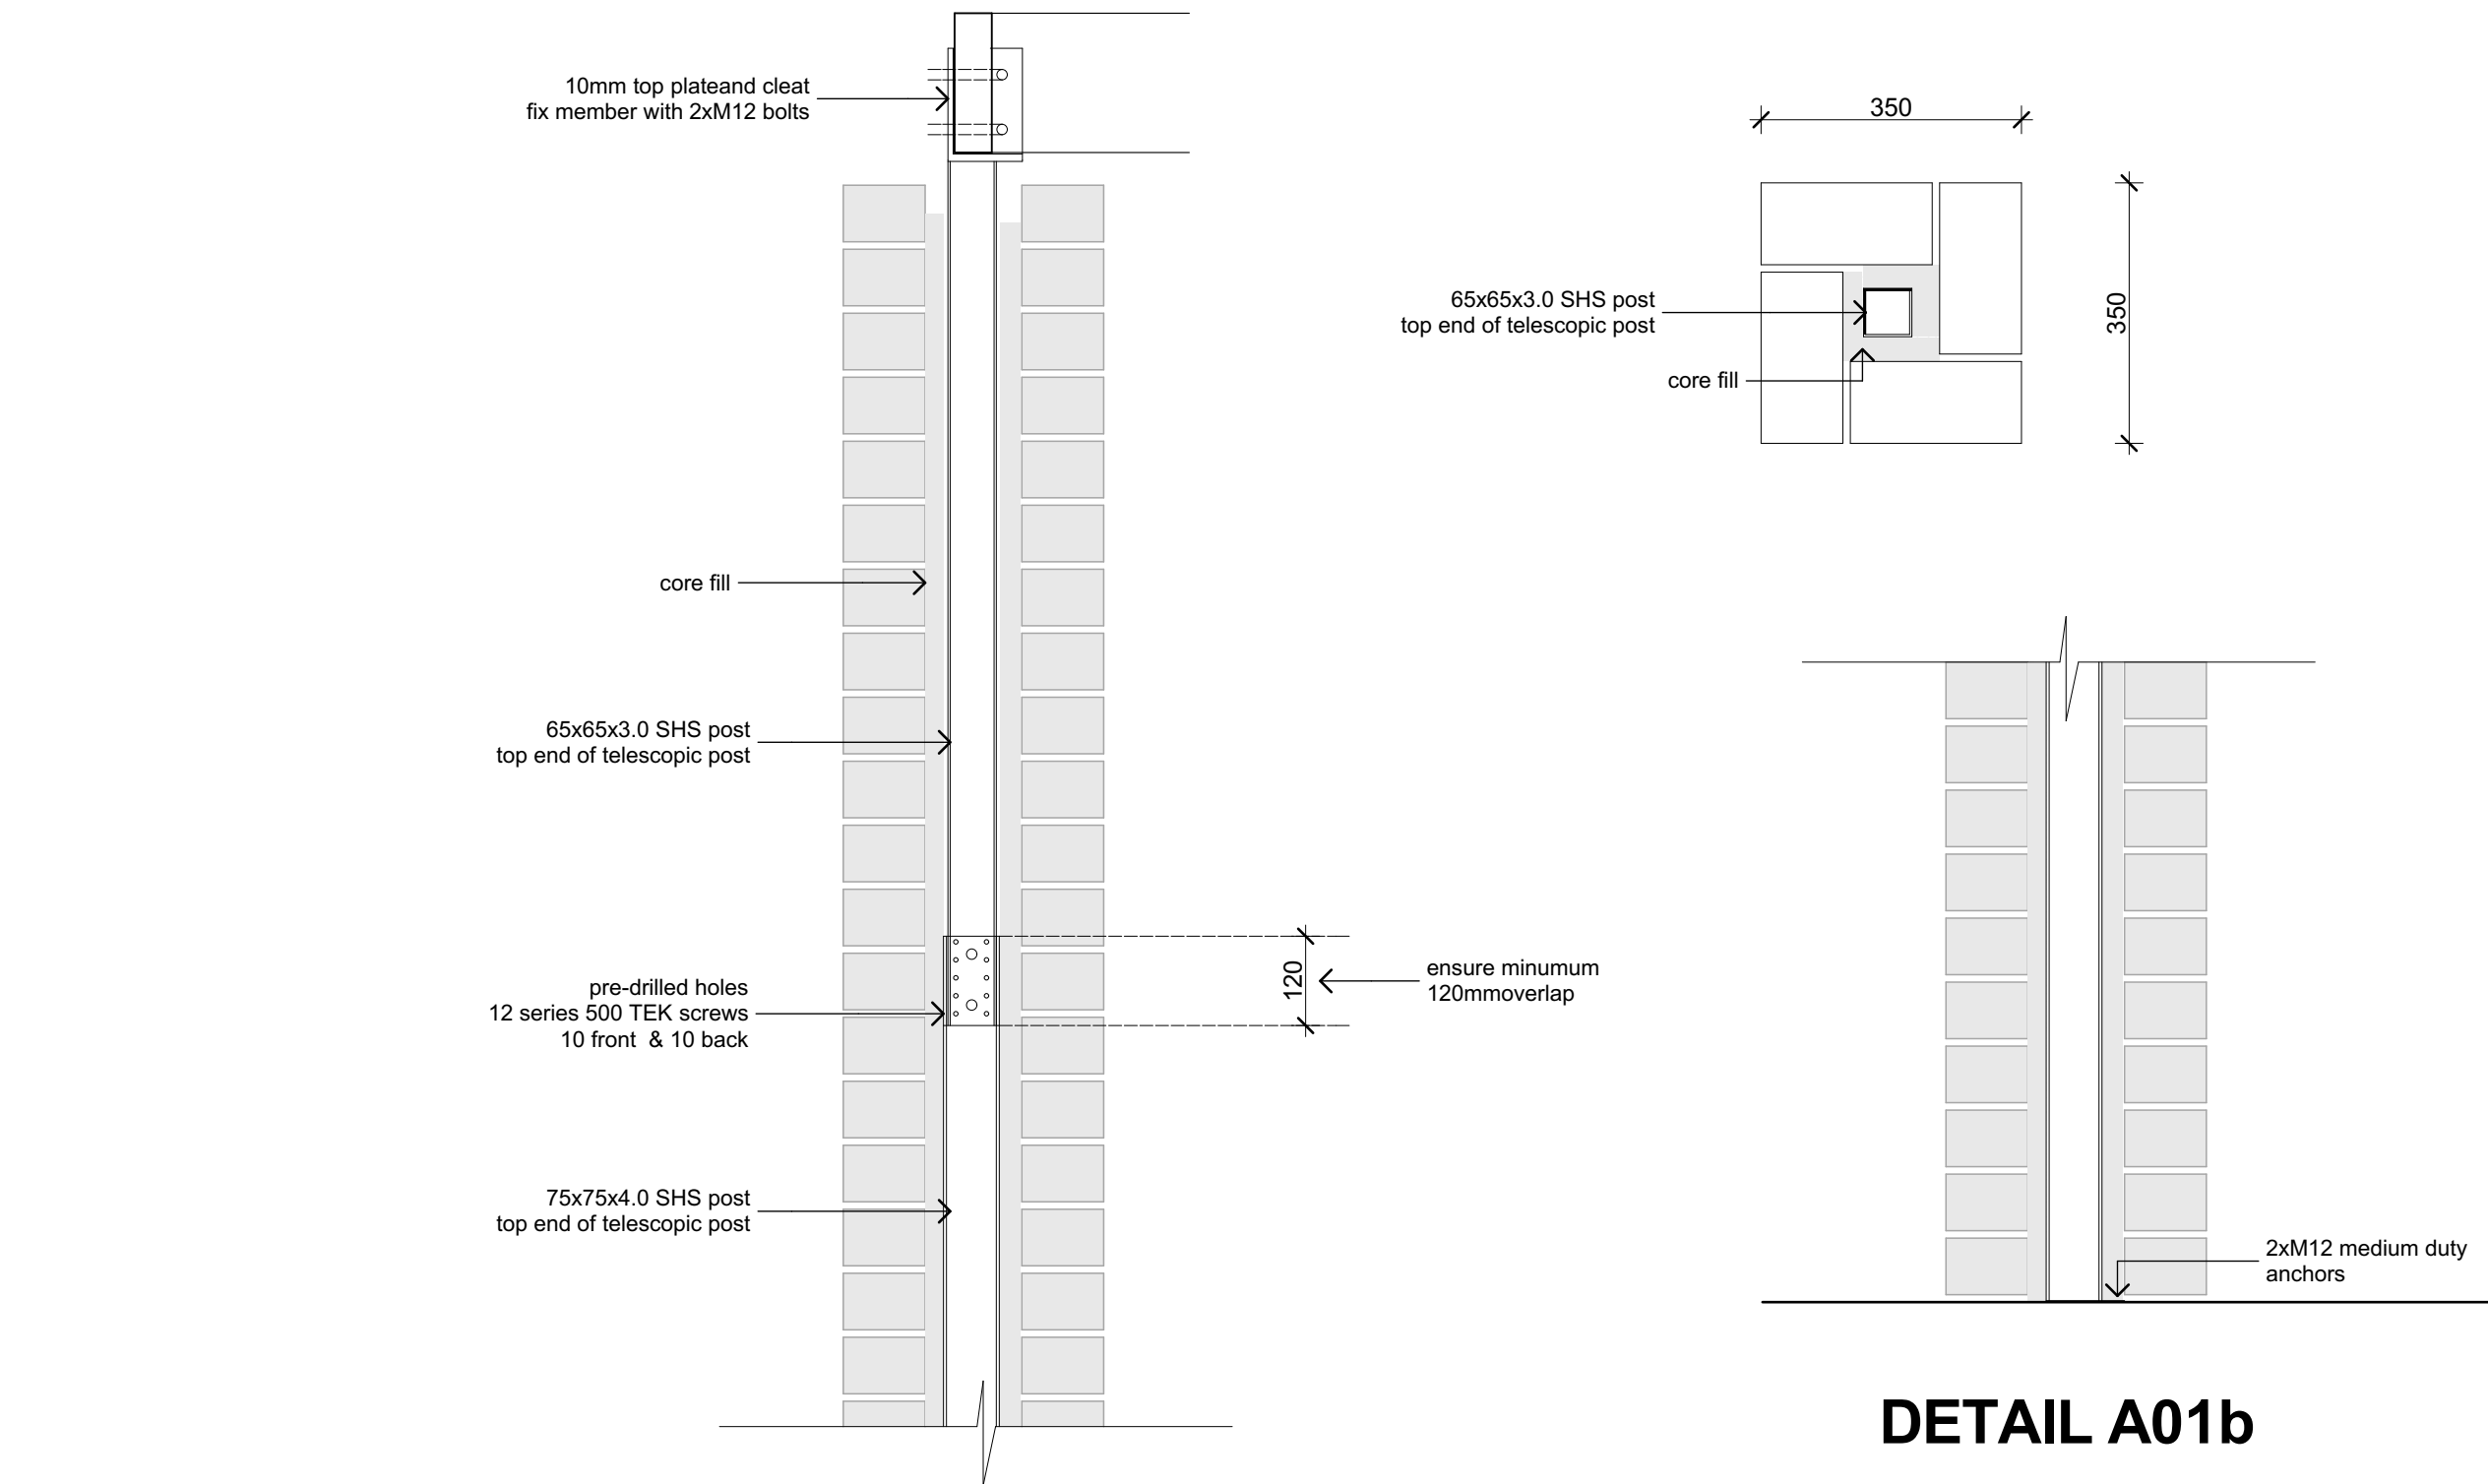

DETAIL A01b

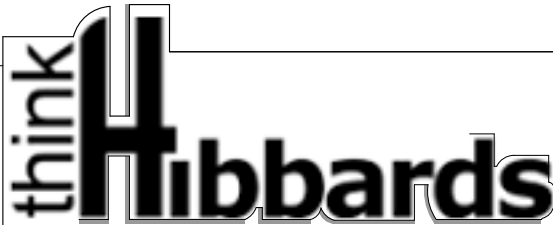


Address:
130 West High Street
Coffs Harbour NSW 2450

Hibbards P/L ABN 22 057 895 020
E:coffs@hibbards.com.au
P:(02) 6650 3300
F:(02) 6651 7044
W: https://hibbardhomes.com.au/

COPYRIGHT & NOTES	
figured dimensions to be used in reference to scaling - all dimensions to be checked on site .Copying of this plan is strictly prohibited without written permission of Hibbard Homes . All boundaries and contours subject to survey	
DESIGN	KIATO 225 SG22 W02 RHG


JOB ADDRESS			
LOT 1808 ZILLIE CLOSE DUBBO NSW 2830			
PROPOSAL	NEW DWELLING	DP:	1318131

drawing title		ADJUSTABLE POST			
date	issue	description		JOB No.	revision
09/01/26	1	ISSUED FOR CC APPROVAL		11439	1
				SCALE	1:10 printed to A3 size
				DRAWN	ML
				DATE	13/01/2026
				WIND	'N2'
				SITE	
					PAGE
					14

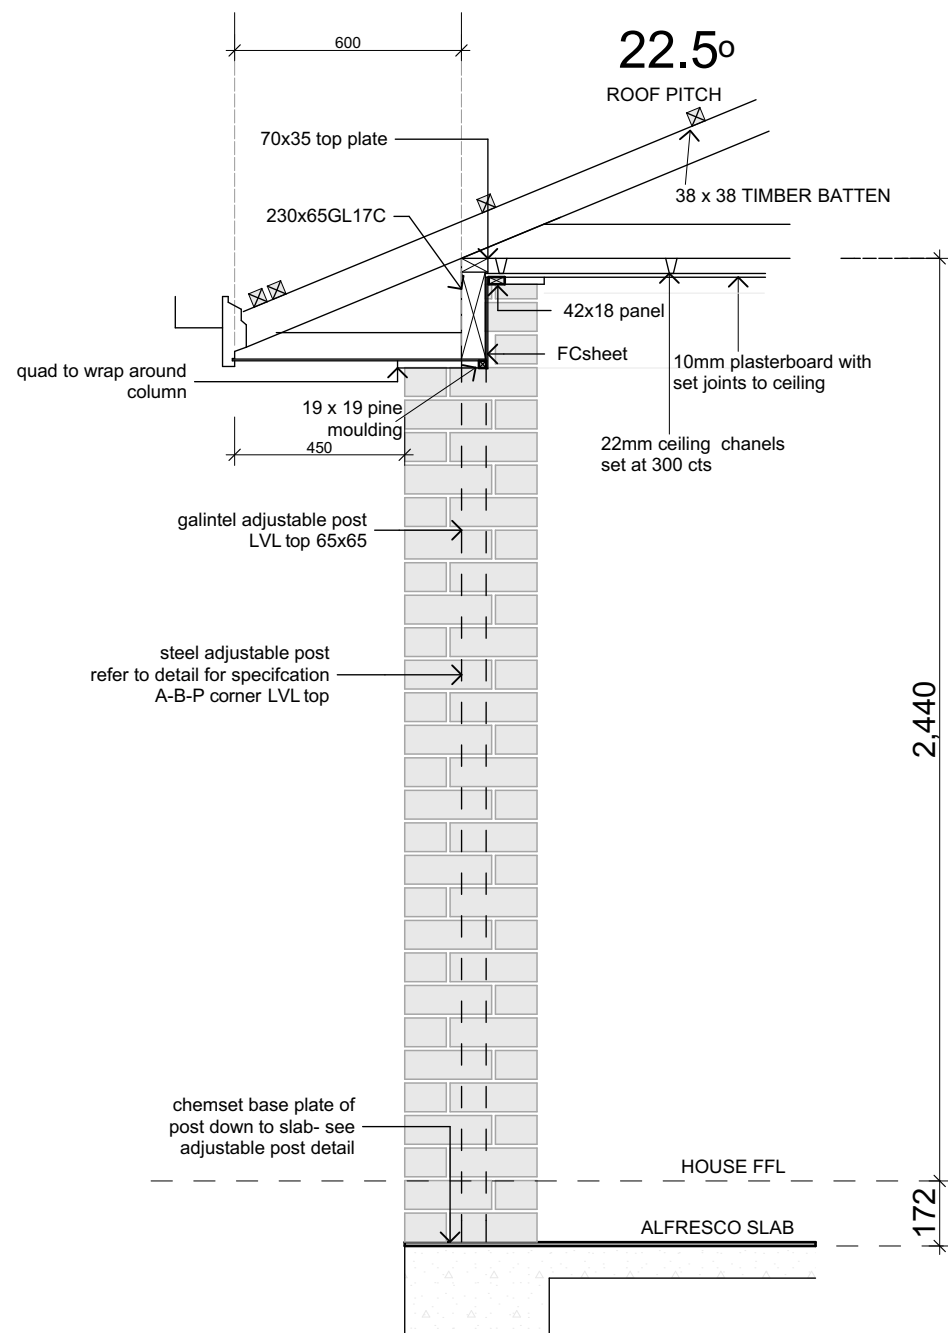


COLUMN SECTION
Detail A01

SCALE 1:20

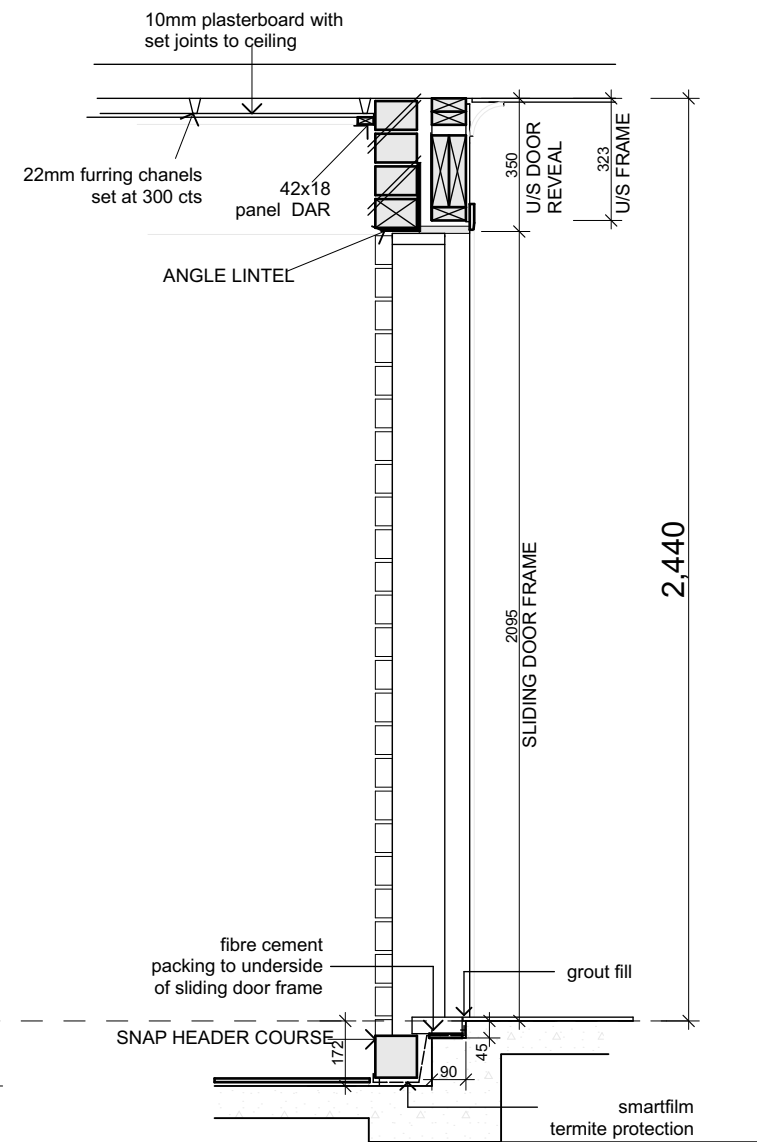


SLIDING DOOR SECTION
Detail A01a

SCALE 1:20

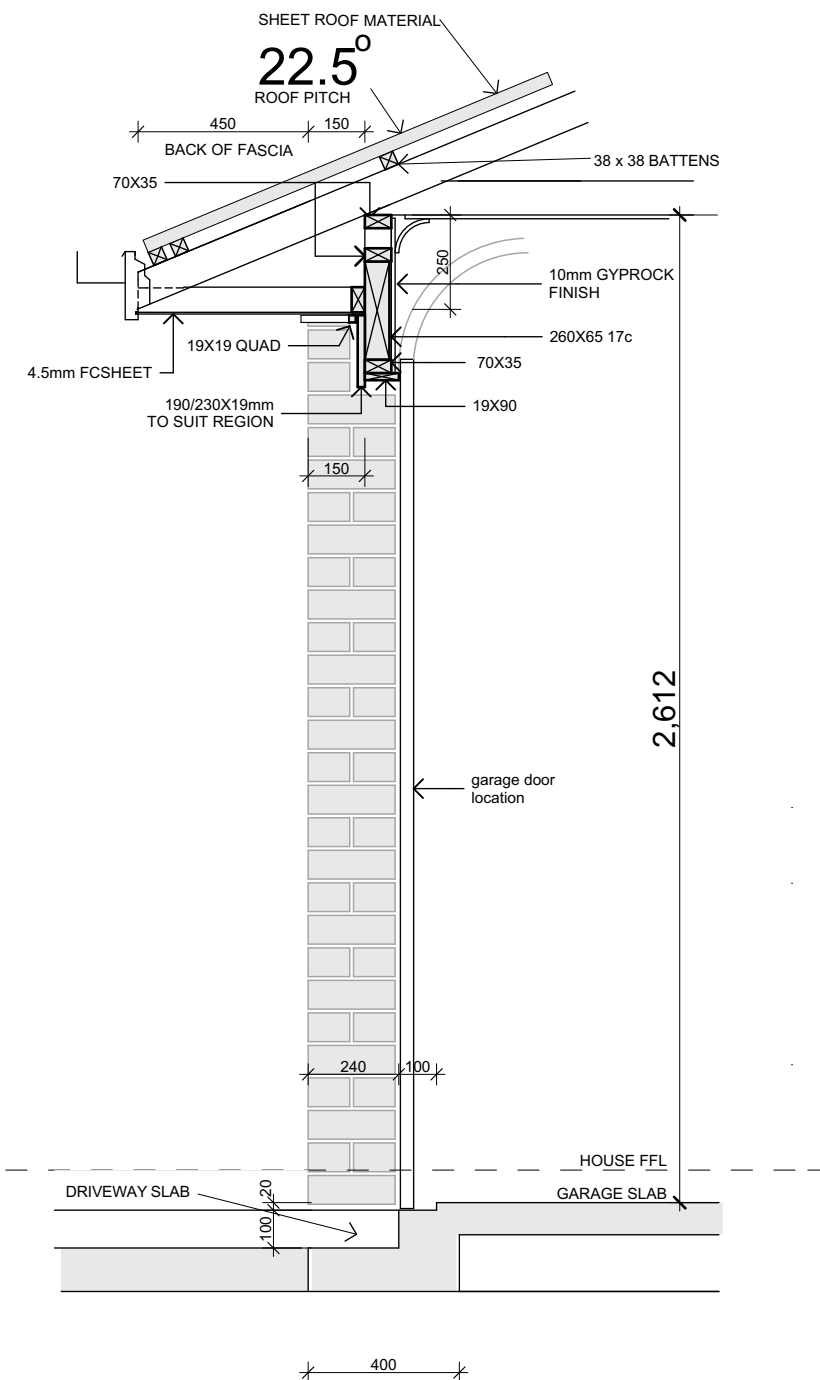


**GARAGE OPENING
A03**

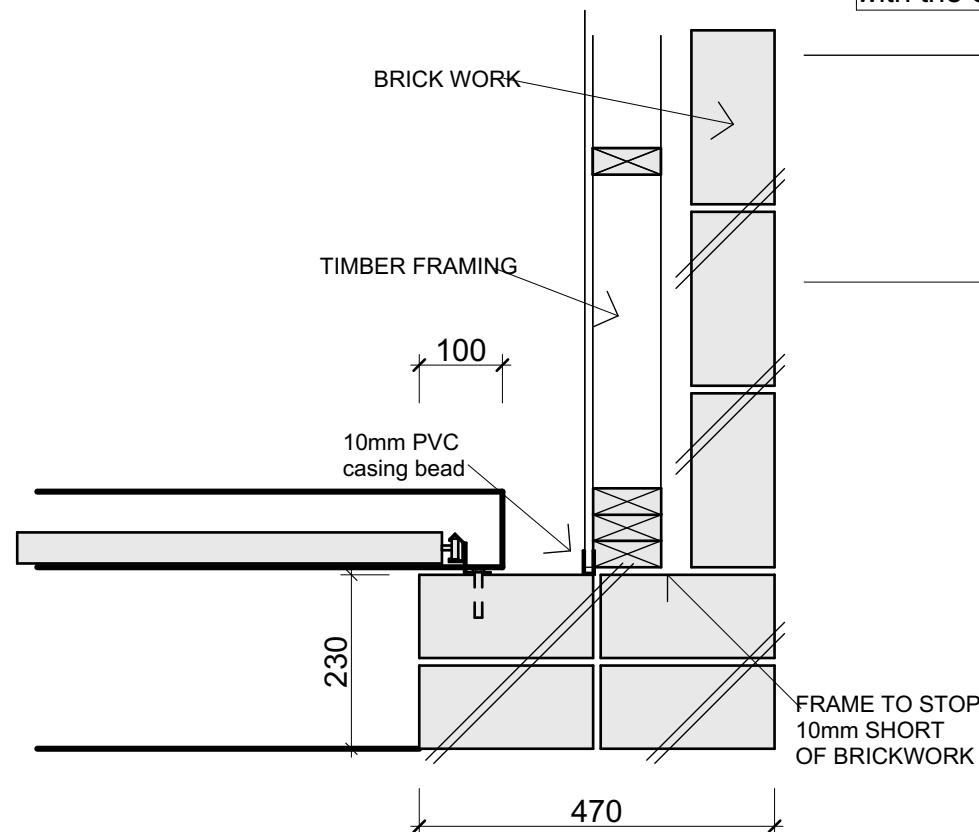

**EXTERNAL CORNER
A02**

SCALE 1:10

A02

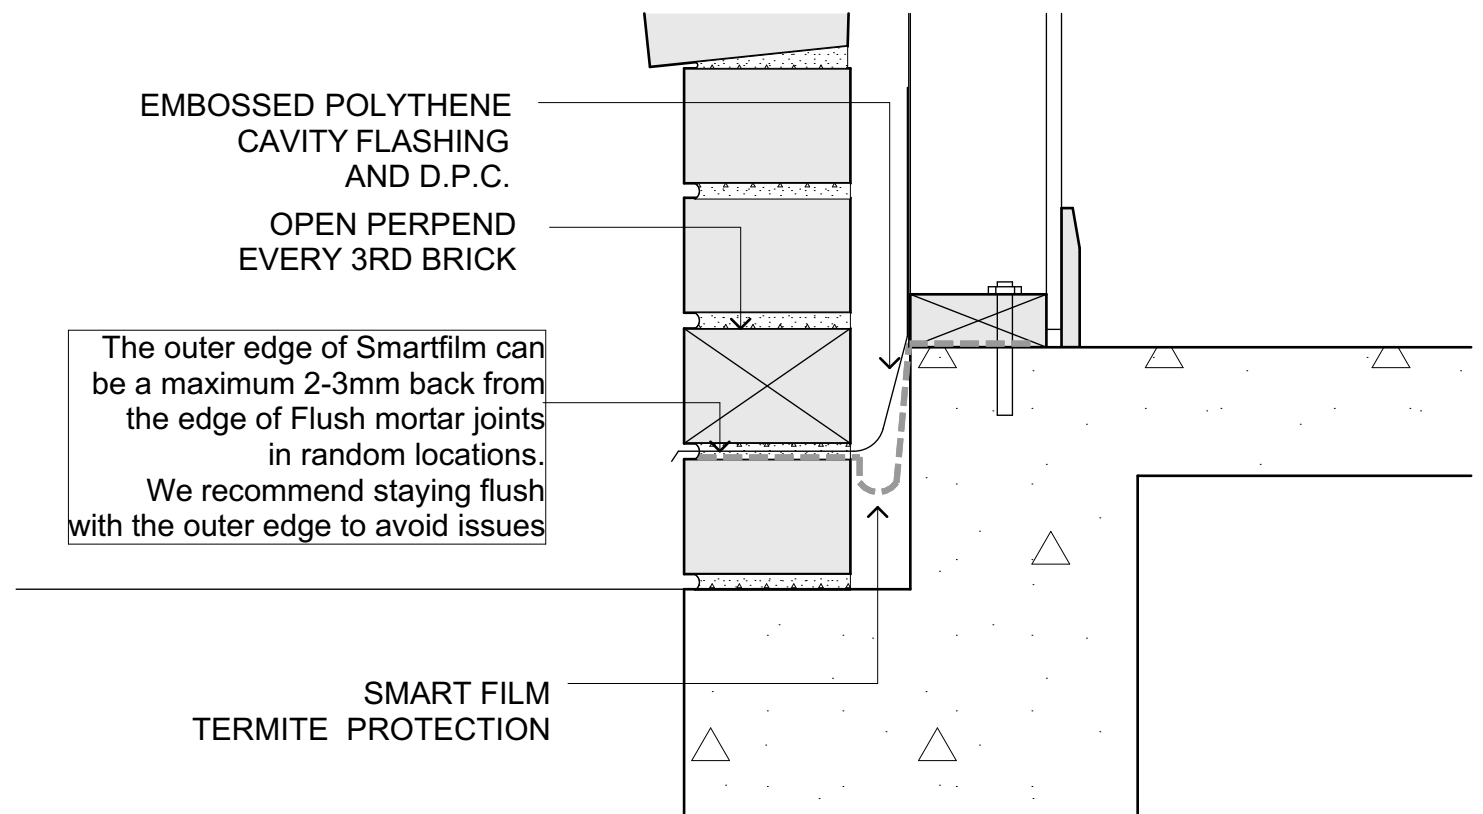

EMBOSSSED POLYTHENE
CAVITY FLASHING
AND D.P.C.
OPEN PERPEND
EVERY 3RD BRICK

The outer edge of Smartfilm can
be a maximum 2-3mm back from
the edge of Flush mortar joints
in random locations.
We recommend staying flush
with the outer edge to avoid issues

SMART FILM
TERMITE PROTECTION


IRONED JOINTS
Termite Protection

EMBOSSSED POLYTHENE
CAVITY FLASHING
AND D.P.C.
OPEN PERPEND
EVERY 3RD BRICK

The outer edge of Smartfilm can
be a maximum 2-3mm back from
the edge of Flush mortar joints
in random locations.
We recommend staying flush
with the outer edge to avoid issues

SMART FILM
TERMITE PROTECTION

FLUSH MORTAR JOINTS
Termite Protection

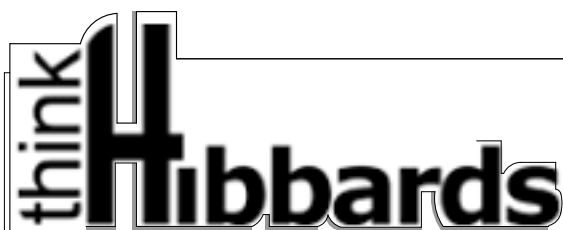


Address:
130 West High Street
Coffs Harbour NSW 2450
Hibbards P/L ABN 22 057 895 020
E:coffs@hibbards.com.au
P:(02) 6650 3300
F:(02) 6651 7044
W: https://hibbardhomes.com.au/

COPYRIGHT & NOTES
figured dimensions to be used in reference to scaling - all
dimensions to be checked on site .Copying of this plan is
strictly prohibited without written permission of Hibbard
Homes . All boundaries and contours subject to survey
DESIGN KIATO 225 SG22 W02 RHG


JOB ADDRESS
**LOT 1808 ZILLIE CLOSE
DUBBO NSW 2830**
PROPOSAL NEW DWELLING **DP:** 1318131

drawing title		GARAGE DOOR /CORNER/TERMITE PROTECTION			
date	issue	description		JOB No.	11439
09/01/26	1	ISSUED FOR CC APPROVAL		SCALE	1:20,5 printed to A3 size
				DRAWN	ML
				DATE	13/01/2026
				WIND	'N2'
				SITE	
				revision	1
				PAGE	16


drawing title			FLOOR DETAILS			
date	issue	description		JOB No.	11439	revision
09/01/26	1	ISSUED FOR CC APPROVAL		SCALE	NTS	1
				DRAWN	ML	PAGE
				DATE	13/01/2026	17
				WIND	'N2'	SITE

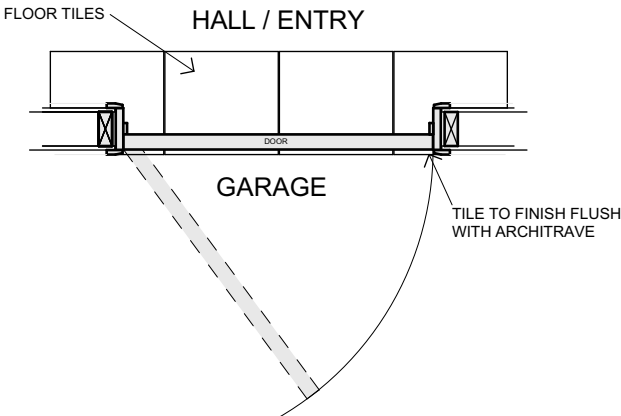


INTERNAL BEAM - HOUSE/GARAGE
THRU DOOR PLAN
A02a7

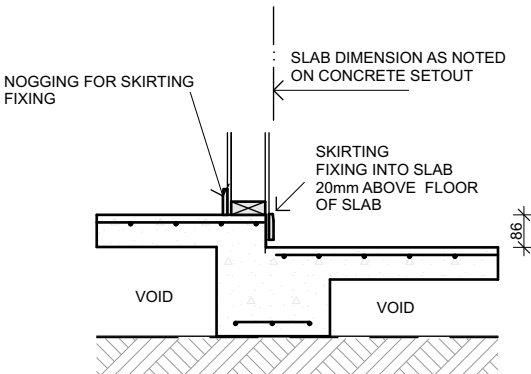


INTERNAL BEAM - HOUSE/GARAGE
THRU WALL
A02a5

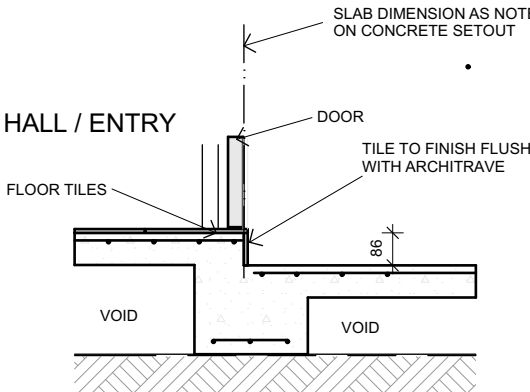

INTERNAL BEAM - HOUSE/GARAGE
THRU DOOR
A02a6

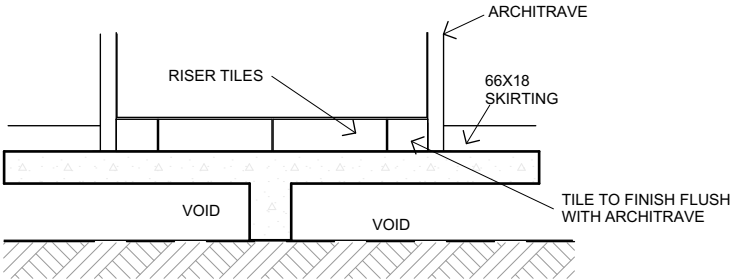


INTERNAL BEAM - HOUSE/GARAGE
THRU DOOR ELEVATION
A02a9

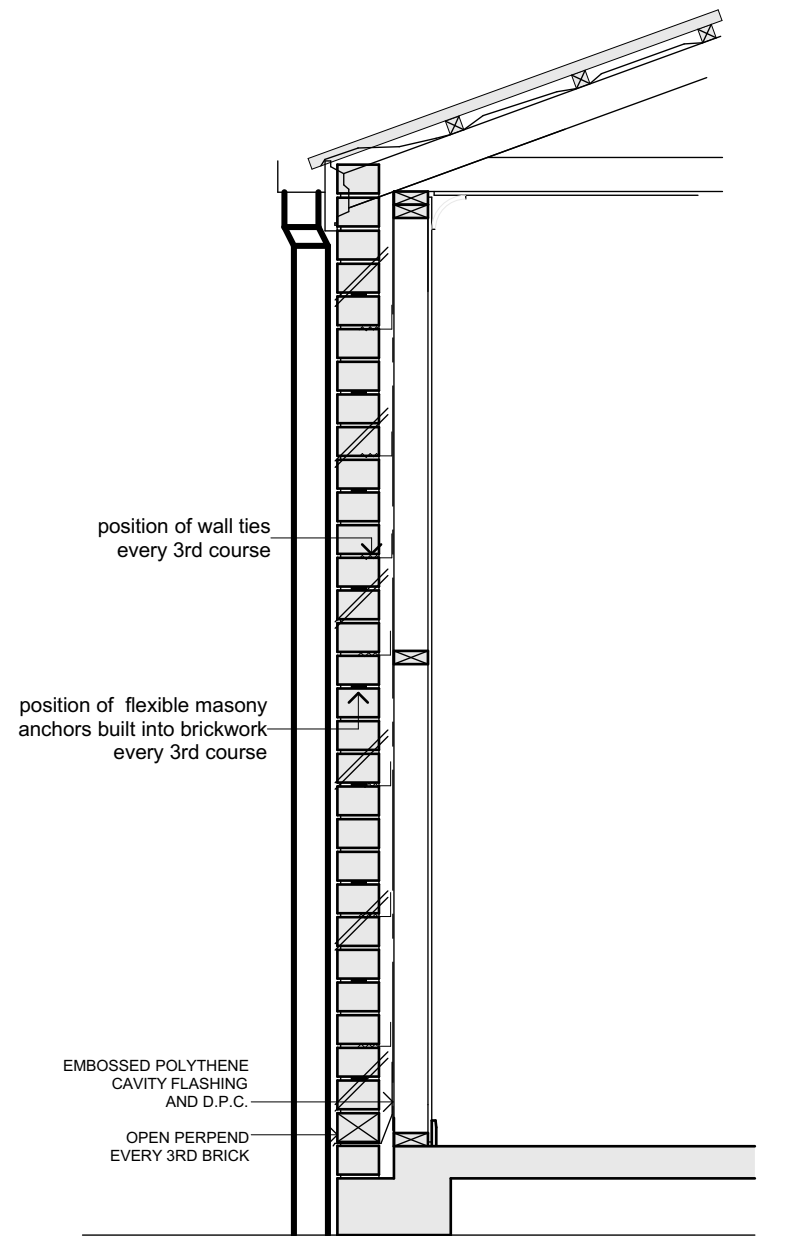

VERTICAL ARTICULATION JOINT
SECTION

Note :
articulation joints required nomore than 6000mm centres
in a straight , continuos walls having no openings

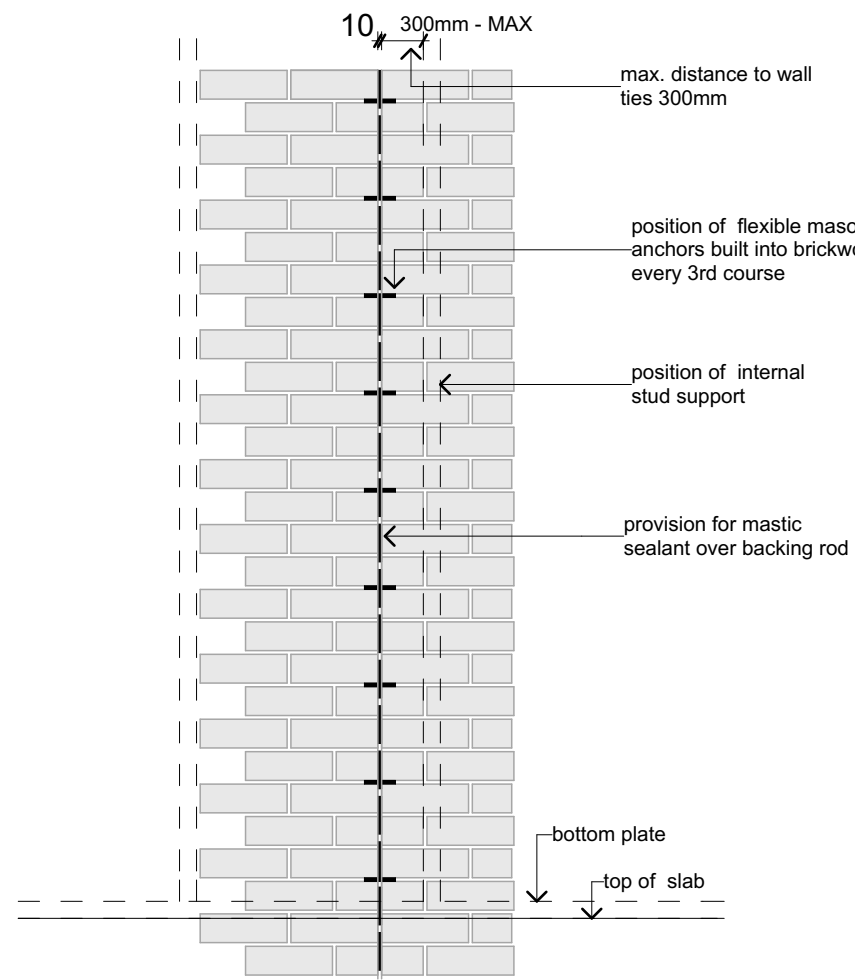

VERTICAL ARTICULATION JOINT
ELEVATION

