

All documents here within are subject to Australian Copyright Laws.

© THIS DRAWING AND THE CONCEPTS REMAIN THE PROPERTY OF DESIGNS AT M. ANY UNAUTHORISED USE OF THIS DRAWING, AS TO THE WHOLE OR PART MAY RENDER THE USER LIABLE TO AN ACTION FOR DAMAGES. CONSEQUENTIAL EVENTS OR DAMAGES ARISING FROM UNWARRANTED OR UNAUTHORISED USE SHALL NOT RENDER DESIGNS AT M LIABLE.

Refer to consultant documentation when directed

- BASIX/Nathers Consultant -
- Surveyor -
- Structural Engineer -
- Civil Engineer -
- Planning Consultant -
- Hydraulic Engineer
- Landscape Designer -
- Mechanical Engineer -

Person ID	Transmittal Set Name	Date	Drawn by



Drawn | Checked

Client ROHAN & JULIE OFFORD

5 McLACHLAN STREET
ORANGE

Site: LOT 21 - SECTION 5 - DP8196

DRAWING TITLE :
**CONSTRUCTION CERTIFICATE
EXISTING SITE PLAN**

PROJECT NAME :

PROPOSED MULTI-RESIDENTIAL UNIT DEVELOPMENT

REVISION NO


DRAWING NO

CC01


PROJECT NO. 22-041

DATE: February 2023

CHECK COPY - NOT FOR SUBMISSION

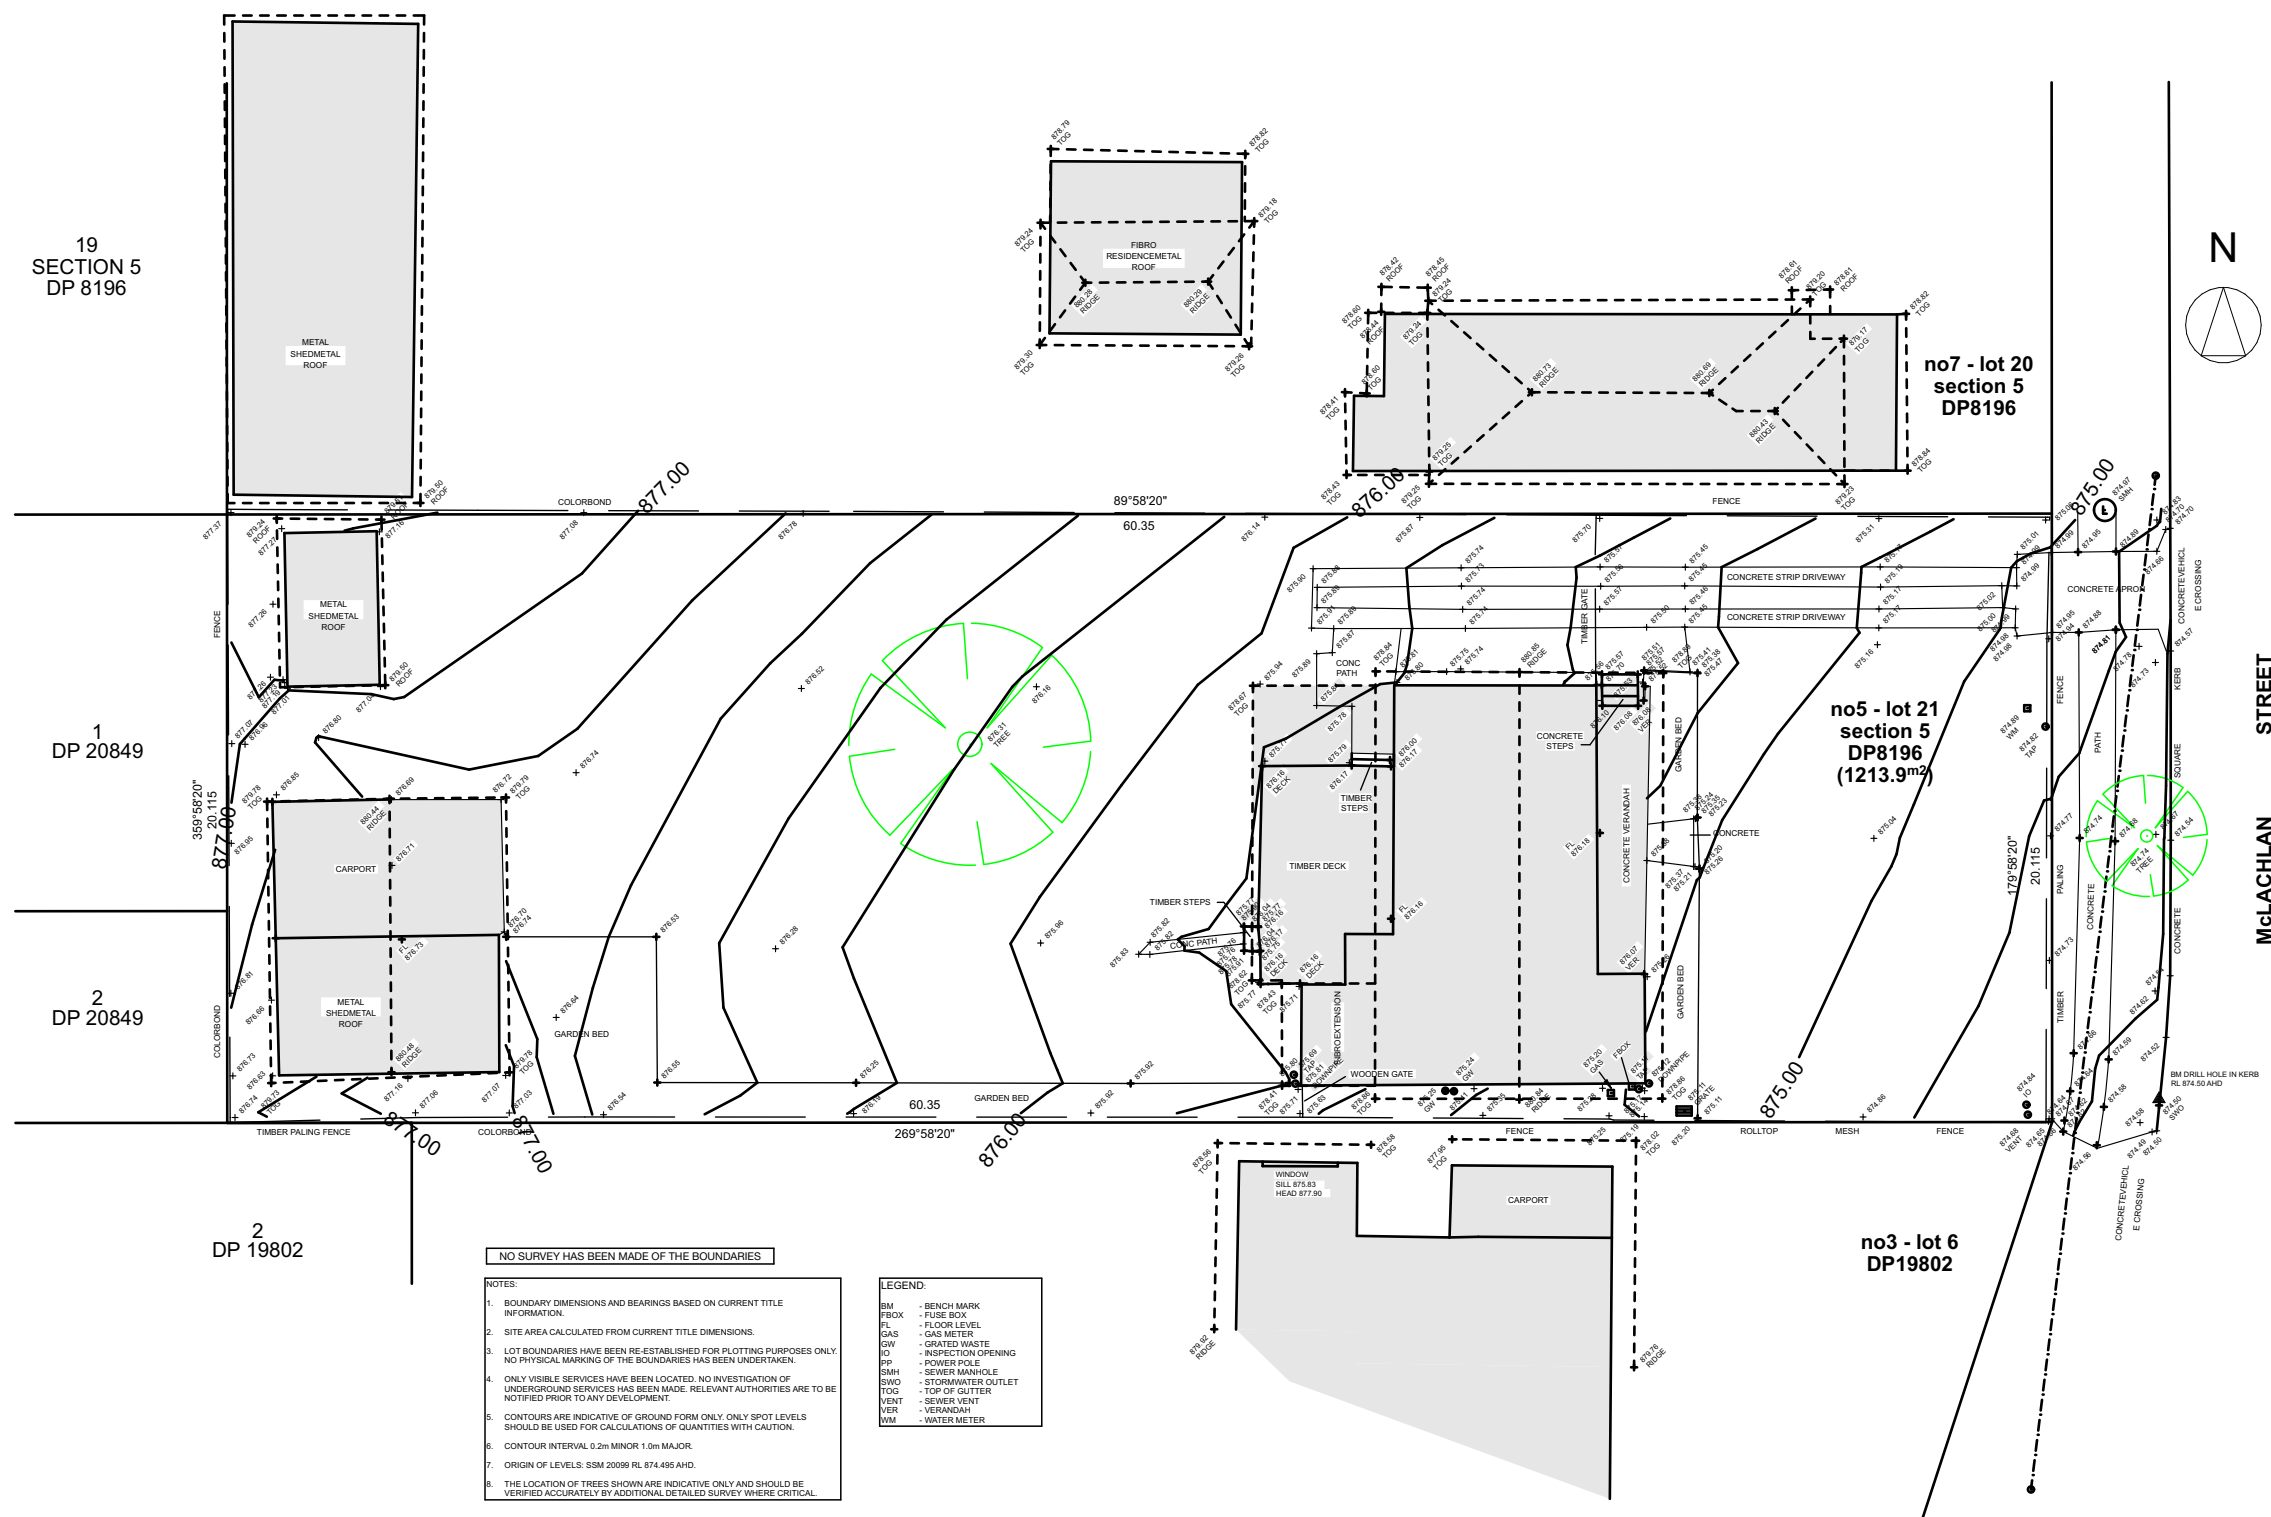

EXISTING SITE PLAN
1:250

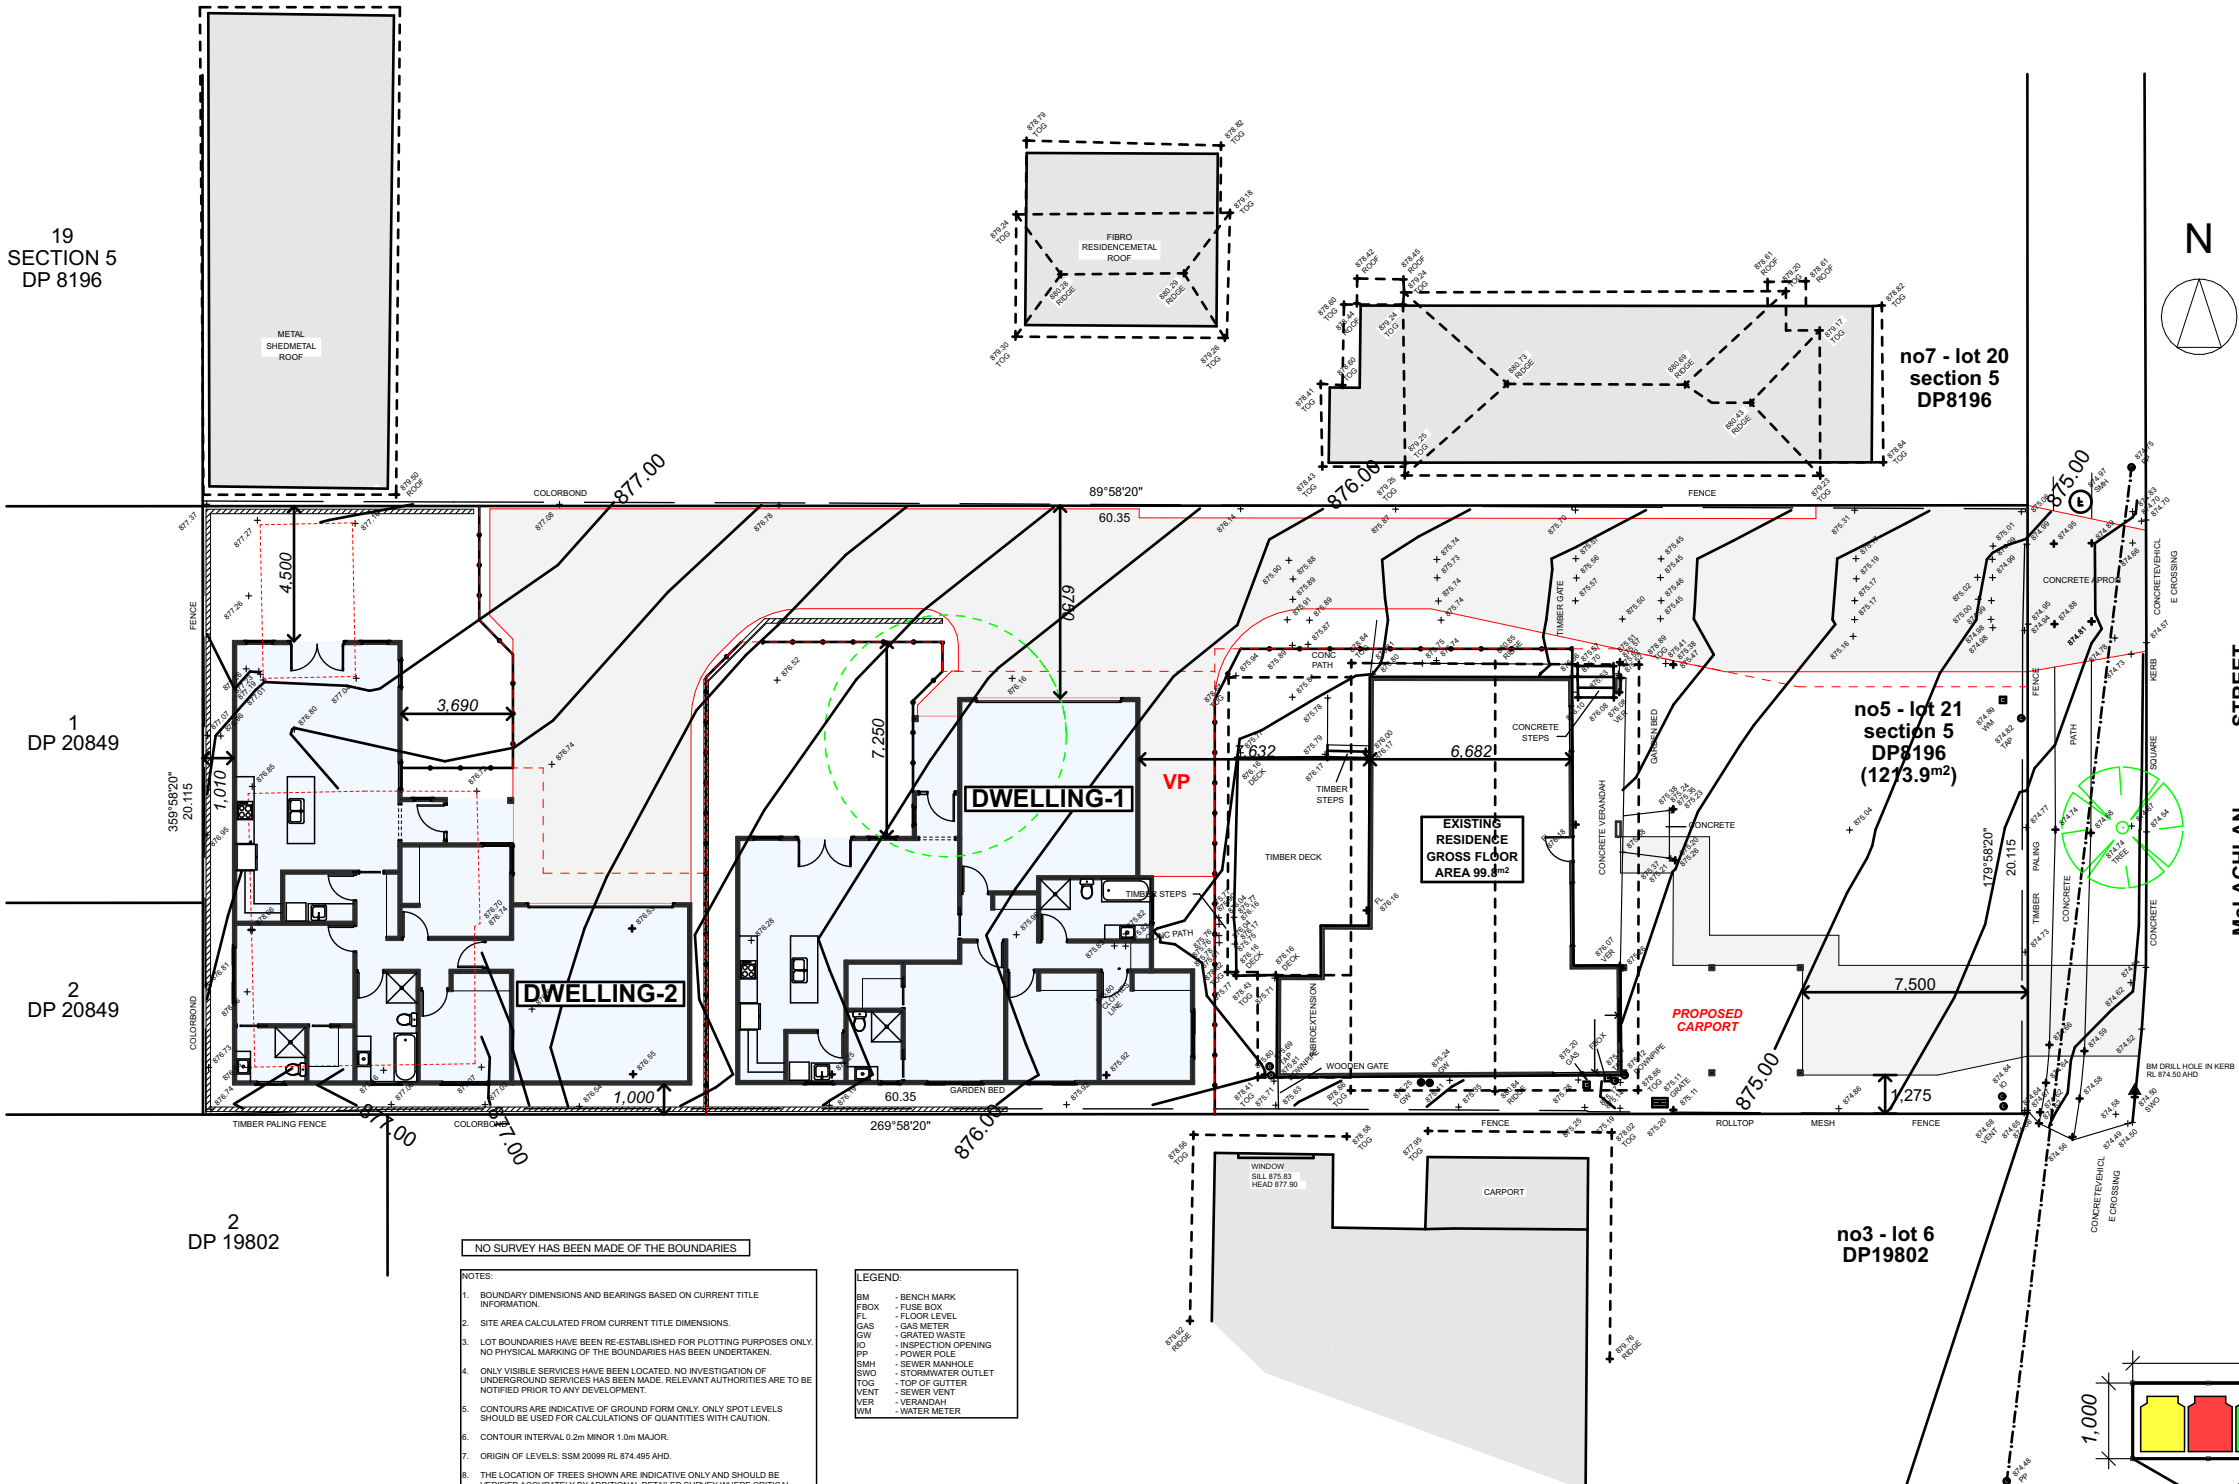

PROPOSED SITE PLAN
1:250

LEGEND:



BM	- BENCH MARK
PROK	- FUSE BOX
FL	- FLOOR LEVEL
GAS	- GAS METER
GW	- GRATED WASTE
IO	- INSPECTION OPENING
PP	- POWER POLE
SMH	- SEWER MANHOLE
SWO	- STORMWATER OUTLET
TG	- TOP OF GUTTER
VENT	- SEWER VENT
VER	- VERANDAH
WM	- WATER METER

BASIX commitments:

Shower head rating	3 star
Toilet rating	4 star
Kitchen taps	4 star
Bathroom taps	4 star
Alternate water	3,000L rainwater tank (min.) & 100m2 roof area connected
Alternate water connections	WCs, washing machine, 1 external tap
HWS	gas instantaneous (6 stars)
Cooling – living / bedroom	Nil
Heating – living / bedroom	Gas fixed flued heater (3.5 stars)
Zoning	bedrooms / living
Fluoro/LED light globes	throughout (dedicated)
Bath fan	ducted, manual on/off
Kitchen range hood	ducted, manual on/off
Laundry fan	ducted, interlocked to light (unit 2 only)
Hot plates / oven	gas / electric
Outdoor clothesline	yes

Thermal Efficiency summary:

Roof	Medium (SA >0.475<0.7) & reflective sarking
Ceiling insulation	R4.0 (except garage)
External wall insulation	R2.5 and vapour permeable sarking (except garage)
Internal wall insulation	R2.5 (walls shared with garage)
Floor insulation	225mm waffle pod slab
Infiltration	Draught stoppers & foam seals on all external doors & internal garage door. Draught stoppers on all exhaust fans.
Downlights	Downlights to be IC-F rated to permit coverage with insulation.
Window / glass door type	Single glazed sliding w/aluminium frame U=6.70 & SHGC=0.70 (+or- 5%) Single glazed hinged w/aluminium frame U=6.70 & SHGC=0.57 (+or- 5%)

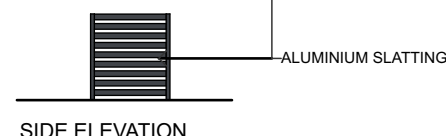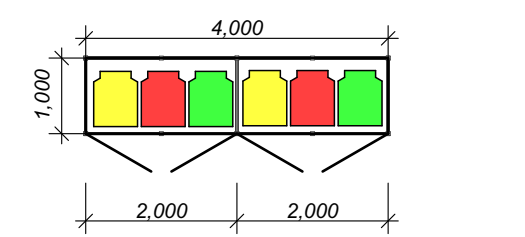

GARBAGE ENCLOSURE
1:100

CHECK COPY - NOT FOR SUBMISSION

NOTE
The Builder shall check all dimensions and levels on site prior to construction. Notify any errors, discrepancies or omissions to the Building Designer. Refer to written dimensions only. Do not scale drawings. Drawings shall not be used for construction purposes until issued for construction. This drawing reflects a design by Designs AT M and is to be used only for work when authorised in writing by Designs AT M.

All boundaries and contours are subject to survey drawing. All levels to Australian Height Data. It is the contractors responsibility to confirm all measurements on site and locations of any services prior to work on site.

All documents here within are subject to Australian Copyright Laws.

© THIS DRAWING AND THE CONCEPTS REMAIN THE PROPERTY OF DESIGNS AT M. ANY UNAUTHORISED USE OF THIS DRAWING, AS TO THE WHOLE OR PART MAY RENDER THE USER LIABLE TO AN ACTION FOR DAMAGES, CONSEQUENTIAL EVENTS OR DAMAGES ARISING FROM UNWARRANTED OR UNAUTHORISED USE SHALL NOT RENDER DESIGNS AT M LIABLE.

- Project Partners**
Refer to consultant documentation when directed
- BASIX/Nathers Consultant -
 - Surveyor -
 - Structural Engineer -
 - Civil Engineer -
 - Planning Consultant -
 - Hydraulic Engineer -
 - Landscape Designer -
 - Mechanical Engineer -

Revision No.	Transmittal Set Name	Date	Drawn by



designsatm
BUILDING DESIGNERS
ASSOCIATION OF AUSTRALIA
7 Aminya Place
Orange NSW 2800
+612 6361 7461
0409 982 793
office@designsatm.com.au
www.designsatm.com.au

Drawn | Checked |

Client: ROHAN & JULIE OFFORD

5 McLACHLAN STREET
ORANGE

Site: LOT 21 - SECTION 5 - DP8196

DRAWING TITLE:
**CONSTRUCTION CERTIFICATE
PROPOSED SITE PLAN**

PROJECT NAME:
**PROPOSED MULTI-RESIDENTIAL
UNIT DEVELOPMENT**

REVISION NO.

DRAWING NO.

CC02

PROJECT NO. 22-041
DATE: February 2023

NOTE
The Builder shall check all dimensions and levels on site prior to construction. Notify any errors, discrepancies or omissions to the Building Designer. Refer to written dimensions only. Do not scale drawings. Drawings shall not be used for construction purposes until issued for construction. This drawing reflects a design by Designs AT M and is to be used only for work when authorised in writing by Designs AT M.

All boundaries and contours are subject to survey drawing . All levels to Australian Height Data. It is the contractors responsibility to confirm all measurements on site and locations of any services prior to work on site.

All documents here within are subject to Australian Copyright Laws.

© THIS DRAWING AND THE CONCEPTS REMAIN THE PROPERTY OF DESIGNS AT M. ANY UNAUTHORISED USE OF THIS DRAWING, AS TO THE WHOLE OR PART MAY RENDER THE USER LIABLE TO AN ACTION FOR DAMAGES, CONSEQUENTIAL EVENTS OR DAMAGES ARISING FROM UNWARRANTED OR UNAUTHORISED USE SHALL NOT RENDER DESIGNS AT M LIABLE.

- Project Partners**
Refer to consultant documentation when directed
- BASIX/Nathers Consultant -
 - Surveyor -
 - Structural Engineer -
 - Civil Engineer -
 - Planning Consultant -
 - Hydraulic Engineer
 - Landscape Designer -
 - Mechanical Engineer -

Revision No	Transmittal Set Name	Date	Drawn by



designsatm

designsatm

bdaa

BUILDING DESIGNERS ASSOCIATION OF AUSTRALIA

7 Aminya Place
Orange NSW 2800

+612 6361 7461
0409 982 793

office@designsatm.com.au
www.designsatm.com.au

Drawn | Checked |

Client ROHAN & JULIE OFFORD

5 McLACHLAN STREET
ORANGE

Site: LOT 21 - SECTION 5 - DP8196

DRAWING TITLE :
**CONSTRUCTION CERTIFICATE
LANDSCAPING PLAN**

PROJECT NAME :
**PROPOSED MULTI-RESIDENTIAL
UNIT DEVELOPMENT**


REVISION NO.

DRAWING NO.

CC03


PROJECT NO. **22-041**
DATE: February 2023

CHECK COPY - NOT FOR SUBMISSION

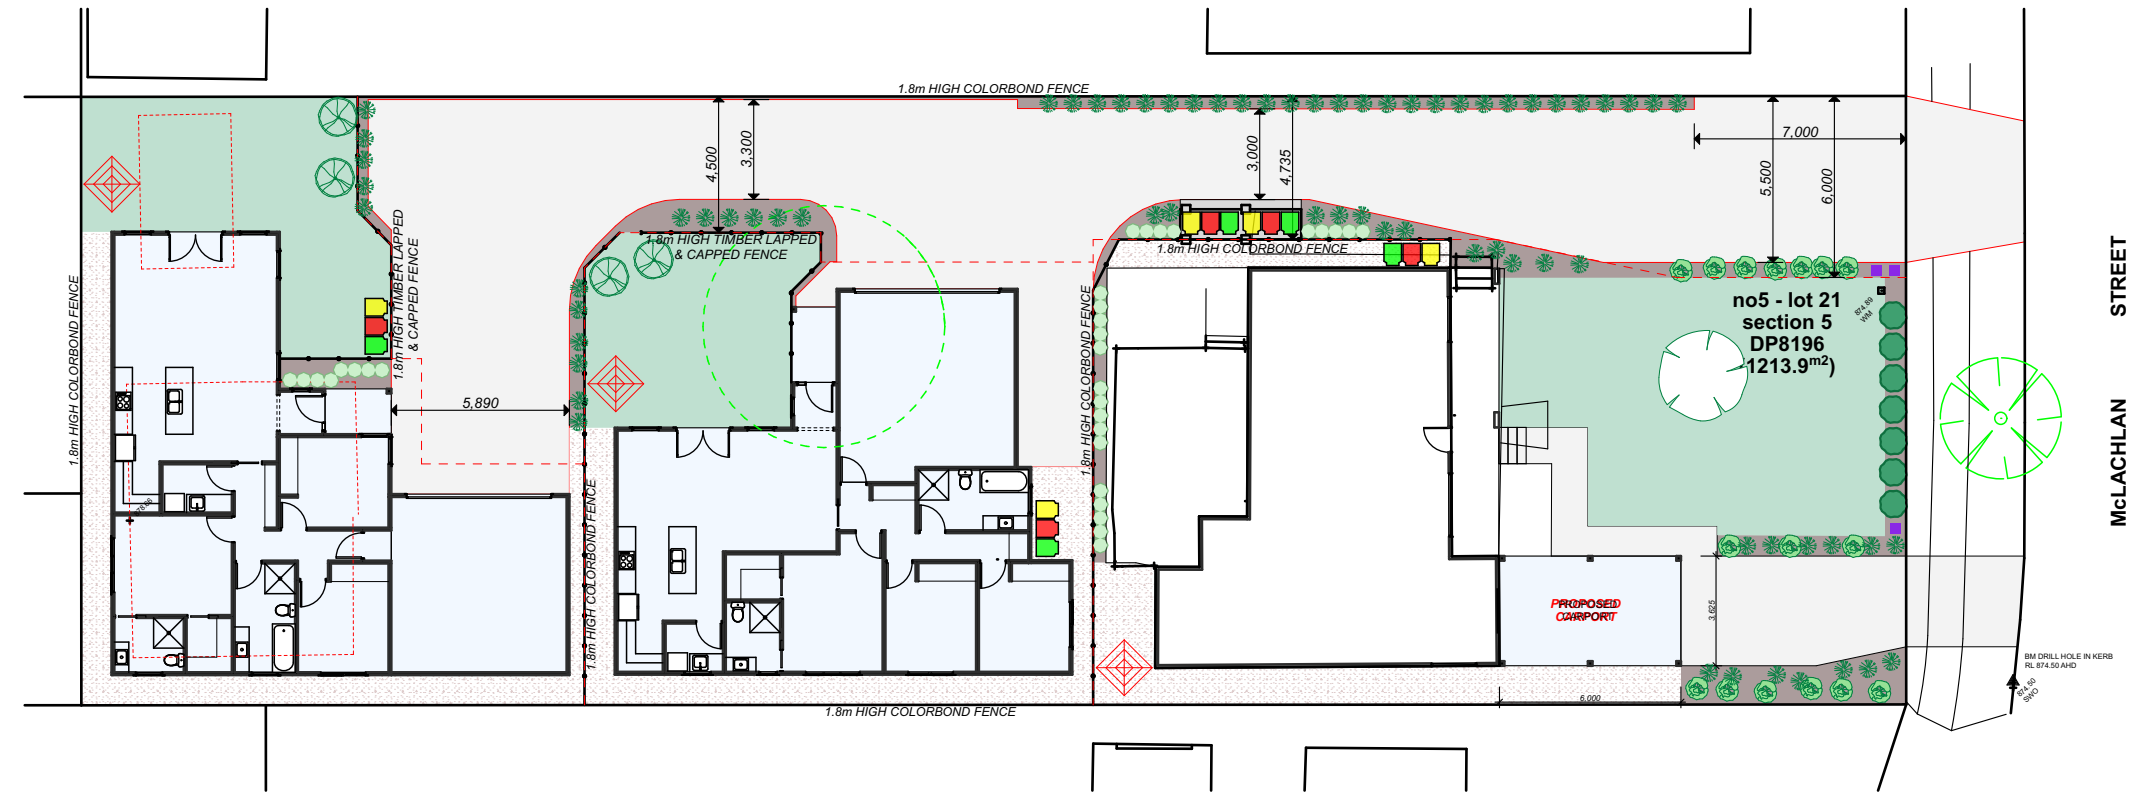


LANDSCAPING PLAN
1:250

Planting Schedule:				
	Botanical Name	Common Name	Estimated Mature Size (HxW meters)	Pot Size
	Large Tree:			
	Melaleuca Linarifolia (N)	Snow in Summer	7.0 x 4.0	25L
	Callistemon Viminalis (N)	Drooping Bottlebrush	8.0 x 4.0	25L
	Fraxinus Excelsior	Golden Ash	12.0 x 4.0	25L
	Small Tree:			
	Magnolia Stellata	Star Magnolia	3.0 x 3.0	25L
	Pyrus Calleryana	Capital Pear	11.0 x 3.0	25L
	Melaleuca Ericifolia (N)	Swamp Melaleuca	3.0 x 3.0	25L
	Tall Hedges: 2m+			
	Westringia fruticosa - "Nakings" (N)	Coastal Rosemary	2.5 x 1.5	200cm
	Callistemon Citrinus (N)	Red Bottlebrush	3.0 x 2.0	200cm
	Pittosporum - Odratissimum	Silver Sheen	4.5 x 3.0	200cm
	Tall Hedges: 1m			
	Westringia fruticosa "Smokey" (N)	Coastal Rosemary	1.0 x 1.0	200cm
	Westringia fruticosa "Grey Box" (N)	Coastal Rosemary	0.3 x 0.3	150cm
	Philotheca myoporoides "Flower Girl" (N)	Native Wax Flower	1.2 x 1.0	150cm
	Grasses			
	Lomandra longifolia (N)	Mat Rush	1.2 x 1.0	150cm
	Dianella revoluta (N)	Little Rev	2.0 x 1.5	150cm
	Liriodendron			
	Groundcovers:			
	Myoporum parvifolium (N)	Creeping Boobialla	0.5 x 0.5	150cm
	Brachyscome Mulfolida (N)	Cut Leafed Daisy	0.5 x 1.5	150cm
	Gazania Pink	African Daisy	0.3 x 1.0	150cm
	Turf: to suit position			
	Tall Fescue			
	Kikuyu			
	Soft Leaf Buffalo			
	All Gardens to be mulched			
	Plantings are a combination of the above types. Plants use in reference to Orange City Councils Parks, Gardens & Your Garden Guide 02/2007			
	Selected gravel pathways - eg. ANL long Hill Salt and Pepper Gravel 10mm			
	Waste bins - Green, red & yellow lid bins			
	Clothes Line			
	Mail box			
	Existing trees to be removed			

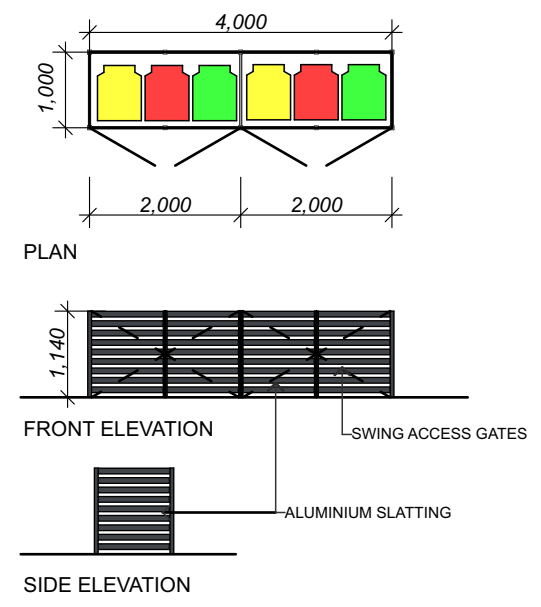

GARBAGE ENCLOSURE
1:100

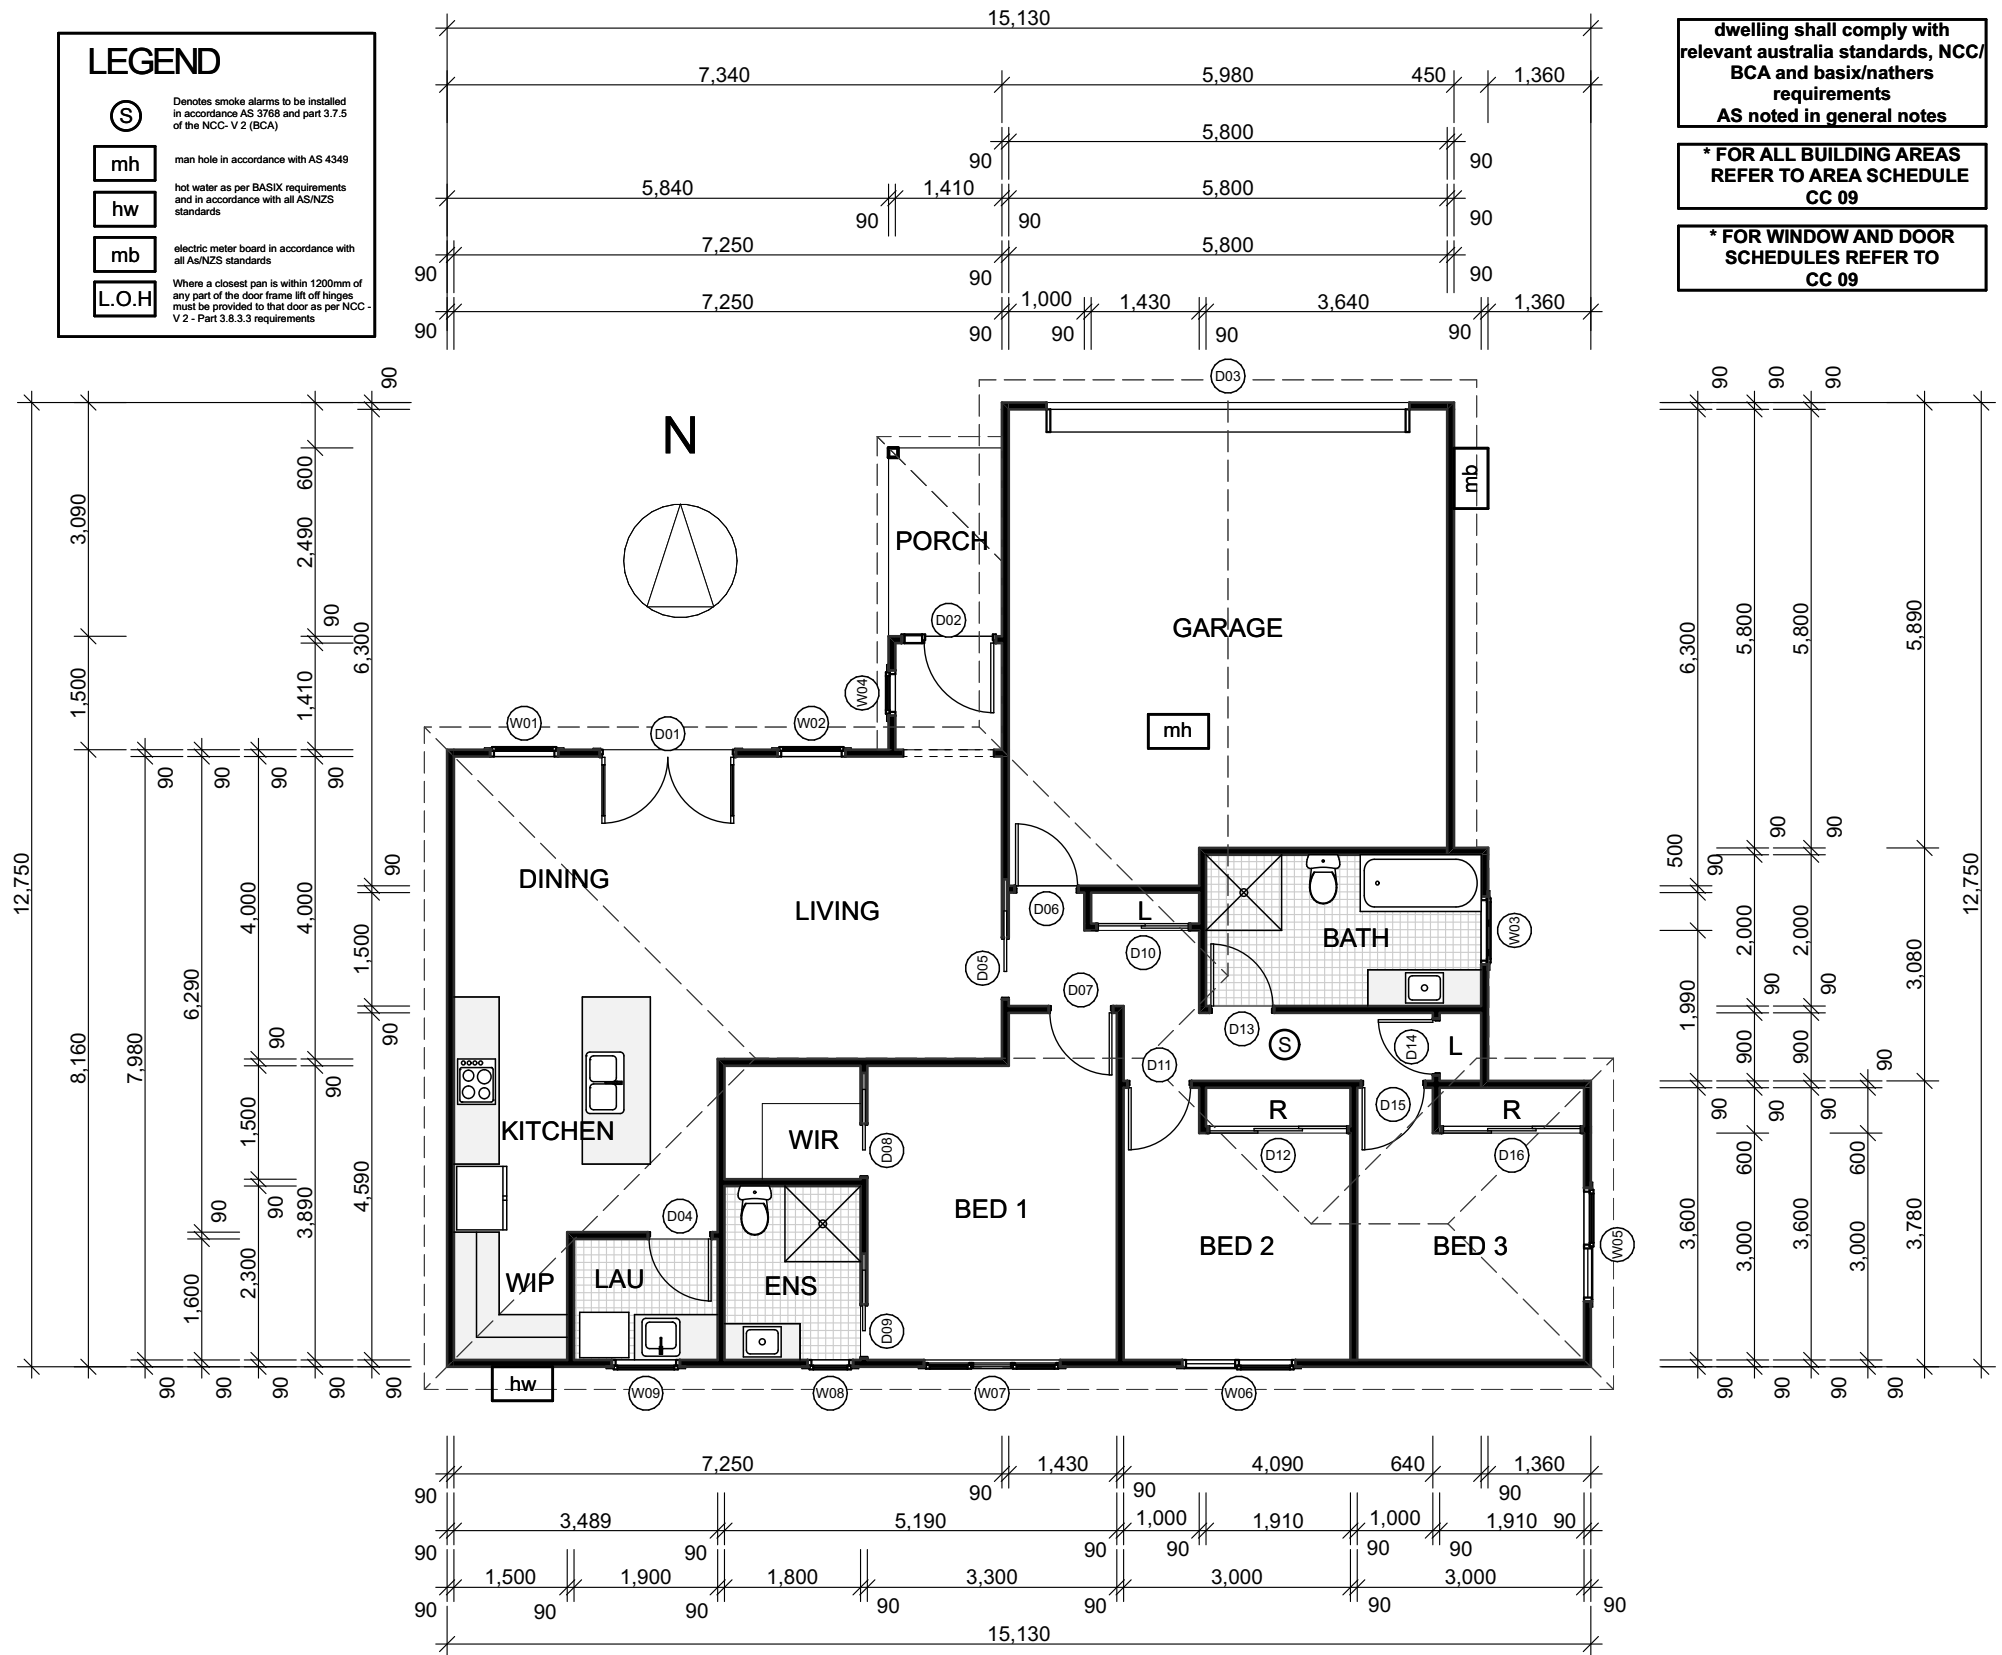

DOOR LIST		
ID	W x H	ELEVATION
D01	1,800×2,100	
D02	1,250×2,040	
D03	4,800×2,200	
D04	820×2,040	
D05	820×2,040	
D06	820×2,040	
D07	820×2,040	
D08	720×2,040	
D09	720×2,040	
D10	1,240×2,040	
D11	820×2,040	
D12	1,860×2,040	
D13	820×2,040	
D14	720×2,040	
D15	820×2,040	
D16	1,860×2,040	

WINDOW LIST		
ID	W x H	ELEVATION
W01	900×1,800	
W02	900×1,800	
W03	900×1,200	
W04	600×1,800	
W05	1,500×1,200	
W06	1,500×1,200	
W07	1,800×1,800	
W08	600×1,200	
W09	900×1,200	

CHECK COPY - NOT FOR SUBMISSION

\\Volumes\Shared\DA\2022\22041 - ROHAN & JULIE OFFORD\ARCHITECTURAL PLANS\CONSTRUCTION CERTIFICATE\22041CC.plt

NOTE
The Builder shall check all dimensions and levels on site prior to construction. Notify any errors, discrepancies or omissions to the Building Designer. Refer to written dimensions only. Do not scale drawings. Drawings shall not be used for construction purposes until issued for construction. This drawing reflects a design by Designs AT M and is to be used only for work when authorised in writing by Designs AT M.

All boundaries and contours are subject to survey drawing . All levels to Australian Height Data. It is the contractors responsibility to confirm all measurements on site and locations of any services prior to work on site.

All documents here within are subject to Australian Copyright Laws.

© THIS DRAWING AND THE CONCEPTS REMAIN THE PROPERTY OF DESIGNS AT M. ANY UNAUTHORISED USE OF THIS DRAWING, AS TO THE WHOLE OR PART MAY RENDER THE USER LIABLE TO AN ACTION FOR DAMAGES, CONSEQUENTIAL EVENTS OR DAMAGES ARISING FROM UNWARRANTED OR UNAUTHORISED USE SHALL NOT RENDER DESIGNS AT M LIABLE.

Project Partners
Refer to consultant documentation when directed
- BASIX/Nathers Consultant -
- Surveyor -
- Structural Engineer -
- Civil Engineer -
- Planning Consultant -
- Hydraulic Engineer
- Landscape Designer -
- Mechanical Engineer -

Revision No.	Transmittal Set Name	Date	Drawn by



designsatm
7 Aminya Place
Orange NSW 2800
+612 6361 7461
0409 982 793
office@designsatm.com.au
www.designsatm.com.au

Drawn | Checked |

Client ROHAN & JULIE OFFORD

5 McLACHLAN STREET
ORANGE

Site: LOT 21 - SECTION 5 - DP8196

DRAWING TITLE :
**CONSTRUCTION CERTIFICATE
FLOOR PLAN - DWELLING 1**

PROJECT NAME :

**PROPOSED MULTI-RESIDENTIAL
UNIT DEVELOPMENT**

REVISION NO.


DRAWING NO.

CC04

PROJECT NO. **22-041**

DATE: February 2023

AREA SCHEDULE	
ZONE	CALCULATED AREA
GARAGE - D1	36.53
GARAGE - D2	35.22
LIVING - D1	110.38

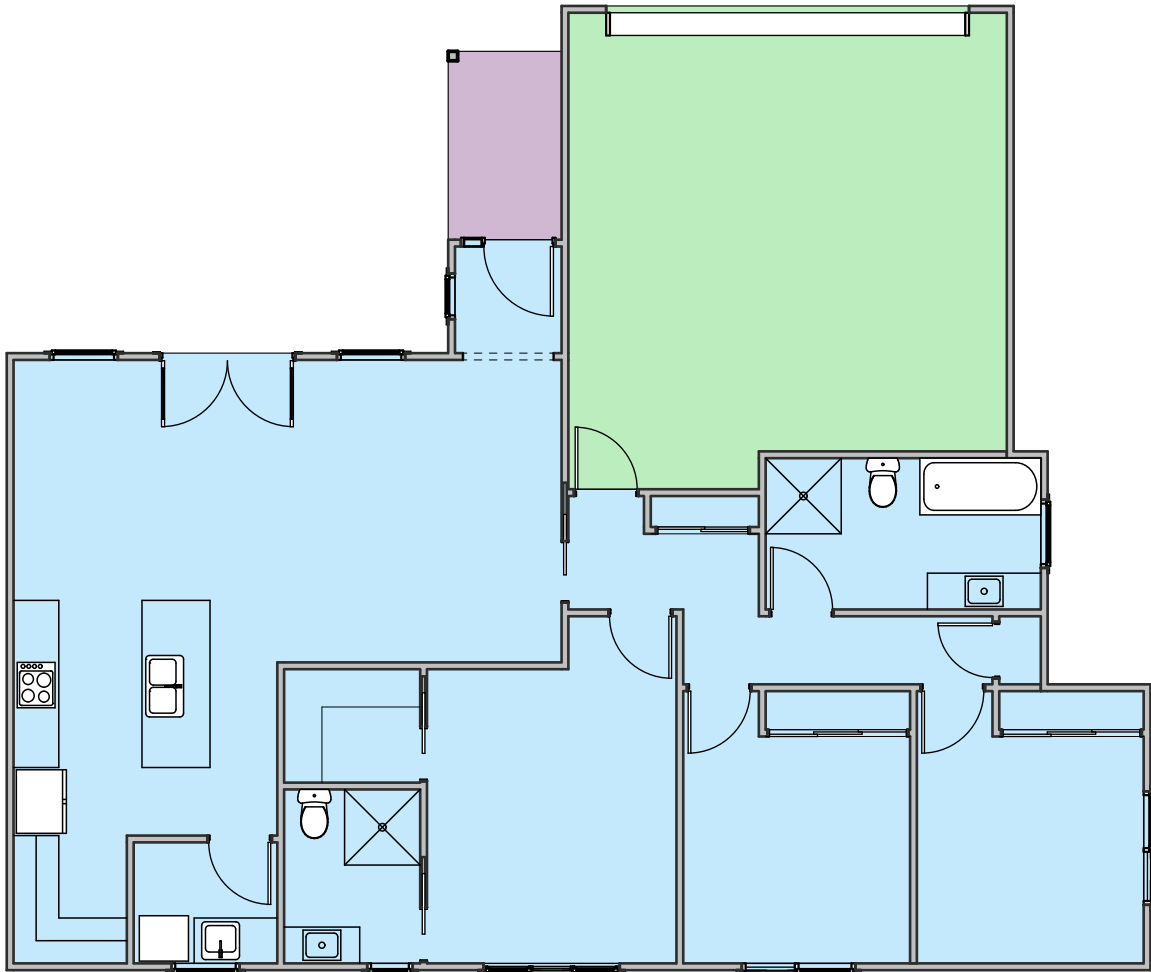

AREA SCHEDULE - DWELLING 1
1:100

CHECK COPY - NOT FOR SUBMISSION

NOTE
The Builder shall check all dimensions and levels on site prior to construction. Notify any errors, discrepancies or omissions to the Building Designer. Refer to written dimensions only. Do not scale drawings. Drawings shall not be used for construction purposes until issued for construction. This drawing reflects a design by Designs AT M and is to be used only for work when authorised in writing by Designs AT M.

All boundaries and contours are subject to survey drawing .
All levels to Australian Height Data. It is the contractors responsibility to confirm all measurements on site and locations of any services prior to work on site.

All documents here within are subject to Australian Copyright Laws.

© THIS DRAWING AND THE CONCEPTS REMAIN THE PROPERTY OF DESIGNS AT M. ANY UNAUTHORISED USE OF THIS DRAWING, AS TO THE WHOLE OR PART MAY RENDER THE USER LIABLE TO AN ACTION FOR DAMAGES, CONSEQUENTIAL EVENTS OR DAMAGES ARISING FROM UNWARRANTED OR UNAUTHORISED USE SHALL NOT RENDER DESIGNS AT M LIABLE.

- Project Partners**
Refer to consultant documentation when directed
- BASIX/Nathers Consultant -
 - Surveyor -
 - Structural Engineer -
 - Civil Engineer -
 - Planning Consultant -
 - Hydraulic Engineer
 - Landscape Designer -
 - Mechanical Engineer -

Revision No	Transmittal Set Name	Date	Drawn by



M

designsatm

bdaa

BUILDING DESIGNERS
ASSOCIATION OF AUSTRALIA

7 Aminya Place
Orange NSW 2800
+612 6361 7461
0409 982 793
office@designsatm.com.au
www.designsatm.com.au

Drawn | Checked |

Client ROHAN & JULIE OFFORD

5 McLACHLAN STREET
ORANGE

Site: LOT 21 - SECTION 5 - DP8196

DRAWING TITLE :
**CONSTRUCTION CERTIFICATE
AREA SCHEDULE - DWELLING 1**


PROJECT NAME :
**PROPOSED MULTI-RESIDENTIAL
UNIT DEVELOPMENT**

REVISION NO.


DRAWING NO.

CC05


PROJECT NO. **22-041**
DATE: February 2023

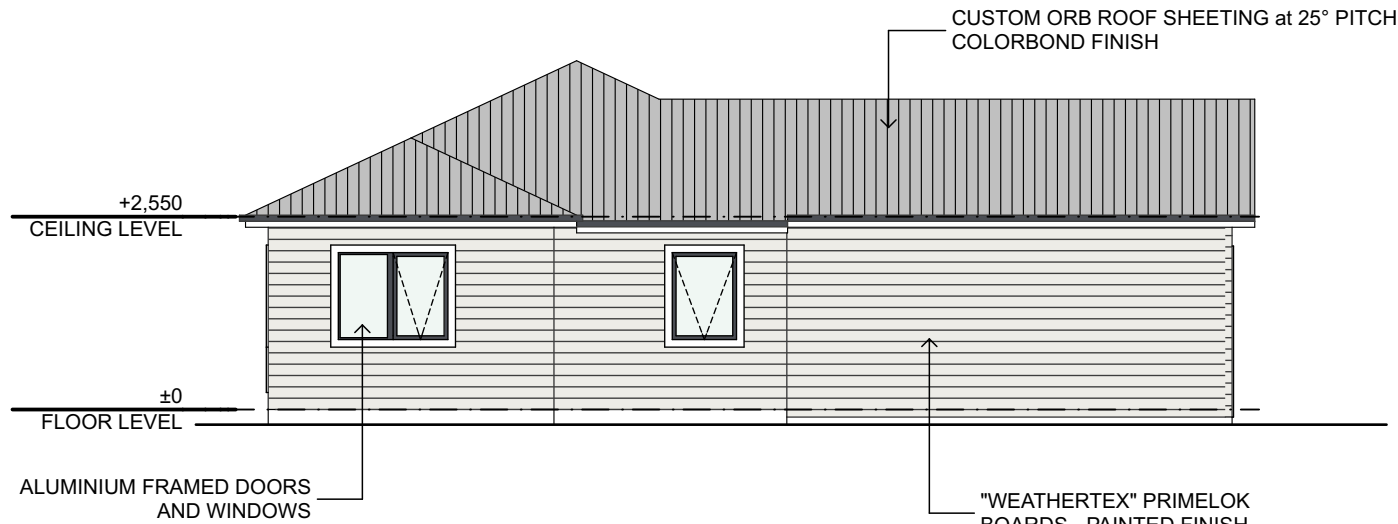

EAST ELEVATION - DWELLING 1
1:100

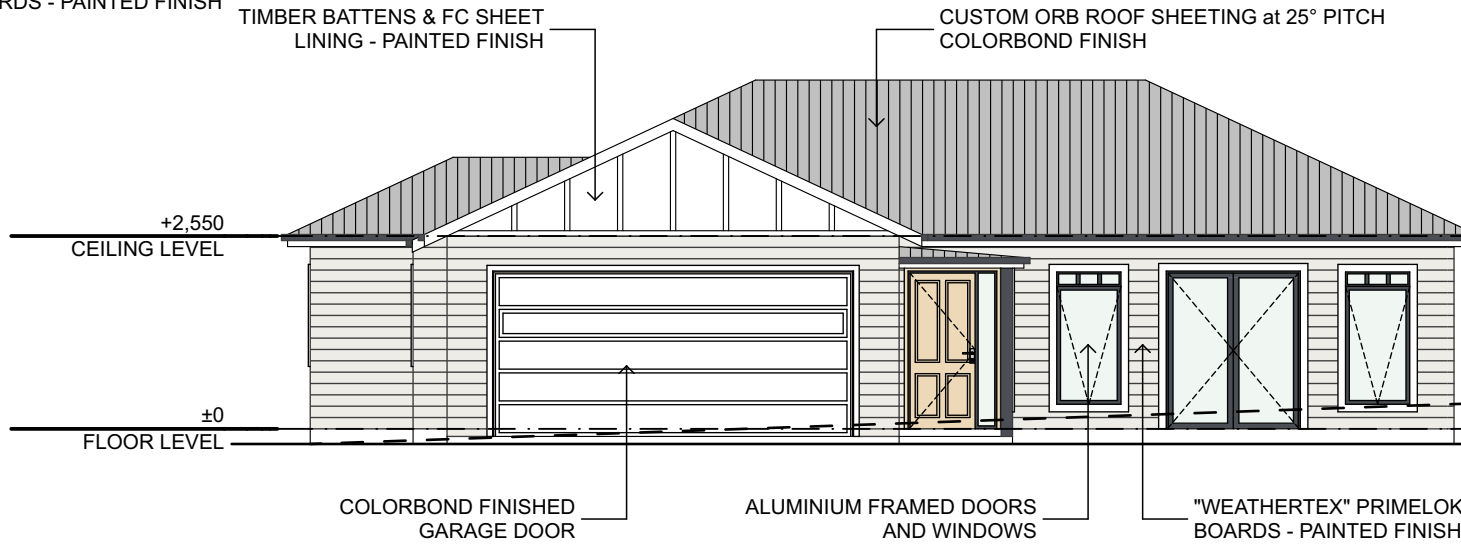

NORTH ELEVATION - DWELLING 1
1:100

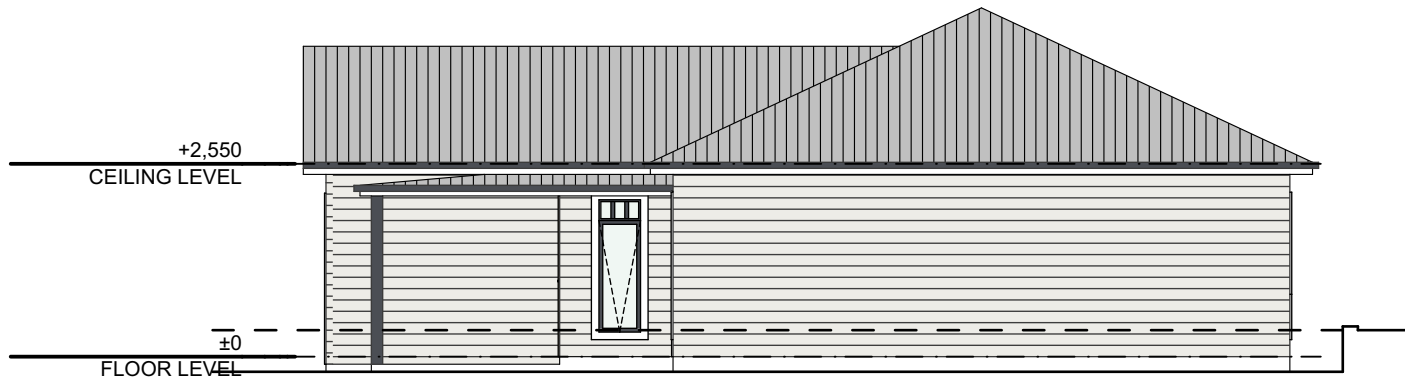

WEST ELEVATION - DWELLING 1
1:100



SOUTH ELEVATION - DWELLING 1
1:100

CHECK COPY - NOT FOR SUBMISSION

/Volumes/Shared/DAM/22222041 - ROHAN & JULIE OFFORD/ARCHITECTURAL PLANS/ CONSTRUCTION CERTIFICATE/22041CC.pln

NOTE
The Builder shall check all dimensions and levels on site prior to construction. Notify any errors, discrepancies or omissions to the Building Designer. Refer to written dimensions only. Do not scale drawings. Drawings shall not be used for construction purposes until issued for construction. This drawing reflects a design by Designs AT M and is to be used only for work when authorised in writing by Designs AT M.

All boundaries and contours are subject to survey drawing . All levels to Australian Height Data. It is the contractors responsibility to confirm all measurements on site and locations of any services prior to work on site.

All documents here within are subject to Australian Copyright Laws.

© THIS DRAWING AND THE CONCEPTS REMAIN THE PROPERTY OF DESIGNS AT M. ANY UNAUTHORISED USE OF THIS DRAWING, AS TO THE WHOLE OR PART MAY RENDER THE USER LIABLE TO AN ACTION FOR DAMAGES, CONSEQUENTIAL EVENTS OR DAMAGES ARISING FROM UNWARRANTED OR UNAUTHORISED USE SHALL NOT RENDER DESIGNS AT M LIABLE.

- Project Partners**
Refer to consultant documentation when directed
- BASIX/Nathers Consultant -
 - Surveyor -
 - Structural Engineer -
 - Civil Engineer -
 - Planning Consultant -
 - Hydraulic Engineer
 - Landscape Designer -
 - Mechanical Engineer -

Revision No	Transmittal Set Name	Date	Drawn by



M

designsatm

bdaa

BUILDING DESIGNERS
ASSOCIATION OF AUSTRALIA

7 Aminya Place
Orange NSW 2800
+612 6361 7461
0409 982 793
office@designsatm.com.au
www.designsatm.com.au

Drawn | Checked |

Client ROHAN & JULIE OFFORD

5 McLACHLAN STREET
ORANGE

Site: LOT 21 - SECTION 5 - DP8196

DRAWING TITLE :
**CONSTRUCTION CERTIFICATE
ELEVATIONS - DWELLING 1**

PROJECT NAME :

**PROPOSED MULTI-RESIDENTIAL
UNIT DEVELOPMENT**

REVISION NO.

DRAWING NO.


CC06

PROJECT NO. **22-041**

DATE: February 2023

Technical drawing of a rectangular floor plan. The overall dimensions are 15,140 (width) and 5,890 (depth). The drawing shows a rectangular area with several internal divisions and angles marked as 90 degrees. The dimensions are as follows:

- Overall width: 15,140
- Overall depth: 5,890
- Internal width segments (from left to right): 5,560, 1,500, 2,190, 5,890.
- Internal depth segments (from top to bottom): 5,380, 5,380, 5,380, 1,500, 2,300, 1,000, 400, 3,600, 5,800.
- Angles marked as 90 degrees are shown at the corners and along the internal divisions.

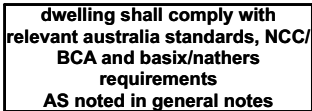

*** FOR ALL BUILDING AREAS
REFER TO AREA SCHEDULE
CC 05**

*** FOR WINDOW AND DOOR
SCHEDULES REFER TO
CC 05**

WINDOW LIST		
ID	W x H	ELEVATION
W10	900×1,800	
W11	900×1,800	
W12	900×1,800	
W13	900×1,800	
W14	600×1,800	
W15	900×1,800	
W16	900×1,800	
W17	1,500×1,200	
W18	900×1,200	
W19	900×1,200	
W20	1,800×1,800	

/Volumes/Shared/DAM2022/22041 - ROHAN & JULIE OFFORD/ARCHITECTURAL PLANS/
CONSTRUCTION CERTIFICATE/22041CC.pln

All boundaries and contours are subject to survey drawing .
All levels to Australian Height Data. It is the contractors
responsibility to confirm all measurements on site and
locations of any services prior to work on site.

© THIS DRAWING AND THE CONCEPTS REMAIN THE PROPERTY OF DESIGNS AT M. ANY UNAUTHORISED USE OF THIS DRAWING, AS TO THE WHOLE OR PART MAY RENDER THE USER LIABLE TO AN ACTION FOR DAMAGES, CONSEQUENTIAL EVENTS OR DAMAGES ARISING FROM UNWARRANTED OR UNAUTHORISED USE SHALL NOT RENDER DESIGNS AT M LIABLE.

Project Partners

Refer to consultant documentation when directed

- BASIX/Nathers Consultant -
- Surveyor -
- Structural Engineer -
- Civil Engineer -
- Planning Consultant -
- Hydraulic Engineer
- Landscape Designer -
- Mechanical Engineer -

Revision ID	Transmittal Set Name	Date	Drawn by



0008020130 02 Sep 2022

Assessor marc kiho

Accreditation No. 20094

Address

5 McLachlan St, Orange,
NSW, 2800



hstar.com.au



ABSA
Accredited Training
Continuously Improving

Assessment completed, all quality assurance
period as part of the ABSA quality audit system

Accreditation Period: 31/03/2022-31/03/2023

Assessor Name: Marc Kihio

Assessor Number: 29084

Assessor Signature: *[Signature]*

 This Accredited Assessor
is authorised to assess
candidates against the
requirements of the
11 Skills for the
21st Century



designsatm

bdag
BUILDING DESIGNERS
ASSOCIATION OF AUSTRALIA

7 Aminya Place
Orange NSW 2800
+612 6361 7461
0409 982 793

office@designsatm.com.au
www.designsatm.com.au

Drawn | Checked |

Client ROHAN & JULIE OFFORD

5 McLACHLAN STREET
ORANGE

Site: LOT 21 - SECTION 5 - DP8196

DRAWING TITLE :
**CONSTRUCTION CERTIFICATE
FLOOR PLAN - DWELLING 2**

PROJECT NAME :

PROPOSED MULTI-RESIDENTIAL UNIT DEVELOPMENT

REVISION NO.

DRAWING NO.

CC07

PROJECT NO. 22-041


DATE: February 2023

FLOOR PLAN - DWELLING 2
1:100

BASIC commitments:	
Shower head rating	3 star
9 Shower rating	4 star
10 Kitchen taps	4 star
Bedroom taps	4 star
Alternate water	3,000L, rainwater tank (min.) & 100m2 roof area connected
Watering machine connections	WCs, washing machine, 1 external tap
RWS	gas instantaneous (6 stars)
Cooling – living / bedroom	N/A
Heating – living / bedroom	N/A
Zoning	bedrooms / living
Thurcoild light globes	Kitchen food feed heater (3.5 stars)
Bath fan	throughout (deducted)
Kitchen range hood	ducted, manual on/off
Laundry fan	ducted, manual on/off
Hot plates / oven	ducted, interlocked to lift unit (only)
Outdoor clothesline	g / electric

Thermal Efficiency summary:	
Roof	Medium (SA >0.475-0.7) & reflective sarking
Ceiling insulation	R4.0 (except garage)
External wall insulation	R2.5 and vapour permeable sarking (except garage)
Internal wall insulation	R2.5 (walls shared with garage)
Floor insulation	225mm waffle pad slab
Infiltration	Draught stoppers & foam seals on all external doors & internal garage door. Draught stoppers on all exhaust fans
Downlights	Downlights to be IC-fitted to prevent coverage with insulation. Single glazed hipwall aluminium frame U=6.70 & SHGC=0.70 (var-5%)
Window / glass door type	Single glazed hipwall aluminium frame U=6.70 & SHGC=0.70 (var-5%)

AREA SCHEDULE	
ZONE	CALCULATED AREA
LIVING - D2	113.08
PORCH - D1	3.74
PORCH - D2	3.29

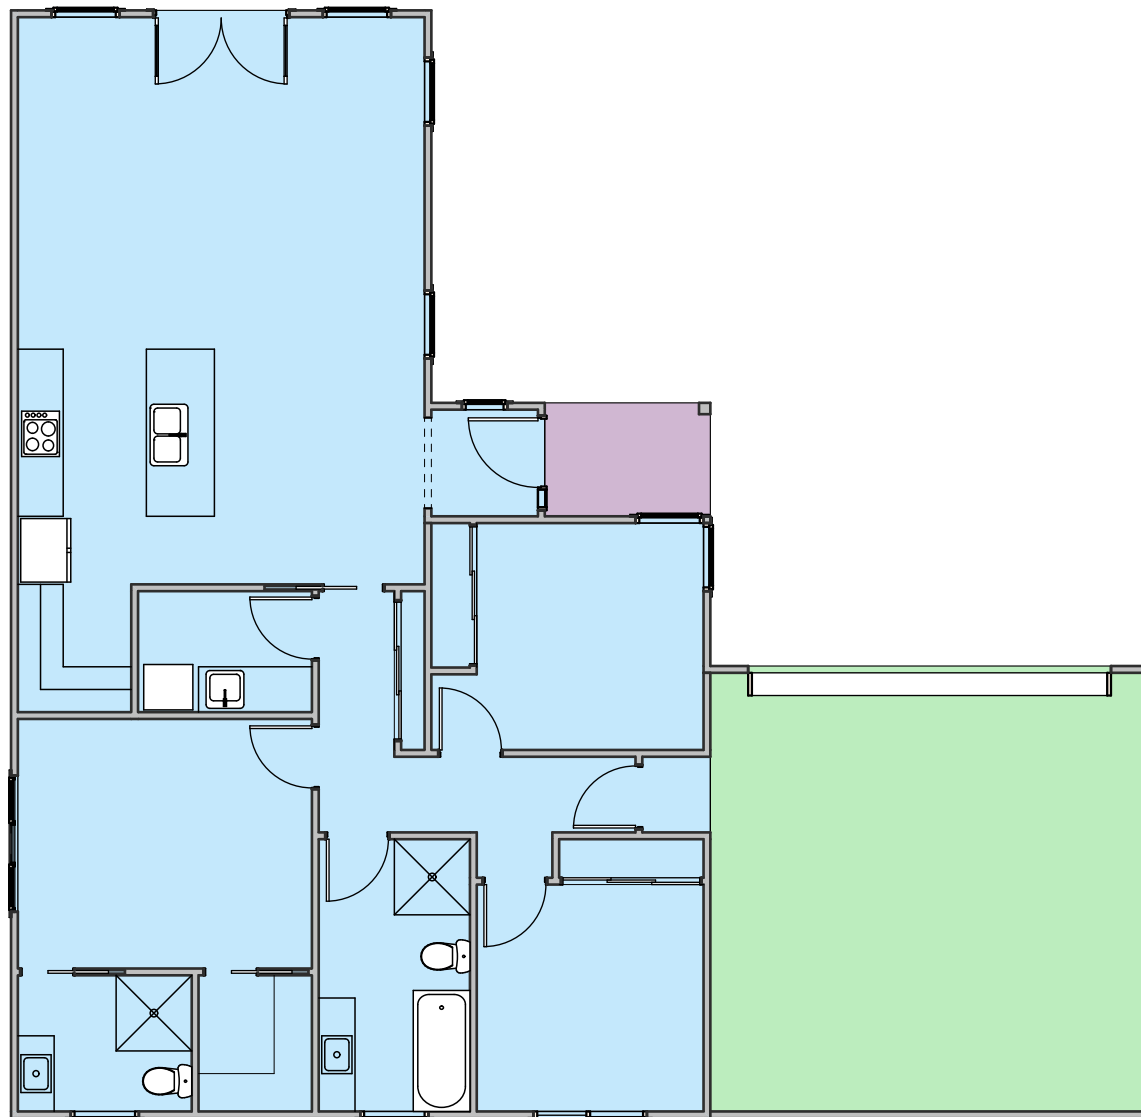

AREA SCHEDULE - DWELLING 2
1:100

CHECK COPY - NOT FOR SUBMISSION

\\Volumes\Shared\DAM2022\22041 - ROHAN & JULIE OFFORD\ARCHITECTURAL PLANS\CONSTRUCTION CERTIFICATE\22041CC.pln

NOTE

The Builder shall check all dimensions and levels on site prior to construction. Notify any errors, discrepancies or omissions to the Building Designer. Refer to written dimensions only. Do not scale drawings. Drawings shall not be used for construction purposes until issued for construction. This drawing reflects a design by Designs AT M and is to be used only for work when authorised in writing by Designs AT M.

All boundaries and contours are subject to survey drawing .
All levels to Australian Height Data. It is the contractors
responsibility to confirm all measurements on site and
locations of any services prior to work on site.

All documents here within are subject to Australian Copyright Laws.

© THIS DRAWING AND THE CONCEPTS REMAIN THE PROPERTY OF DESIGNS AT M. ANY UNAUTHORISED USE OF THIS DRAWING, AS TO THE WHOLE OR PART MAY RENDER THE USER LIABLE TO AN ACTION FOR DAMAGES, CONSEQUENTIAL EVENTS OR DAMAGES ARISING FROM UNWARRANTED OR UNAUTHORISED USE SHALL NOT RENDER DESIGNS AT M LIABLE.

Project Partners

Refer to consultant documentation when directed

- BASIS/Nathers Consultant -
- Surveyor -
- Structural Engineer -
- Civil Engineer -
- Planning Consultant -
- Hydraulic Engineer
- Landscape Designer -
- Mechanical Engineer -

Revision ID	Transmittal Set Name	Date	Drawn by



Drawn | Checked |

Client ROHAN & JULIE OFFORD

5 McLACHLAN STREET
ORANGE

Site: LOT 21 - SECTION 5 - DP8196

DRAWING TITLE :
CONSTRUCTION CERTIFICATE
AREA SCHEDULE - DWELLING 2

PROJECT NAME :

PROPOSED MULTI-RESIDENTIAL UNIT DEVELOPMENT



REVISION NO.

DRAWING NO.

CC08


PROJECT NO. 22-041

DATE: February 2023

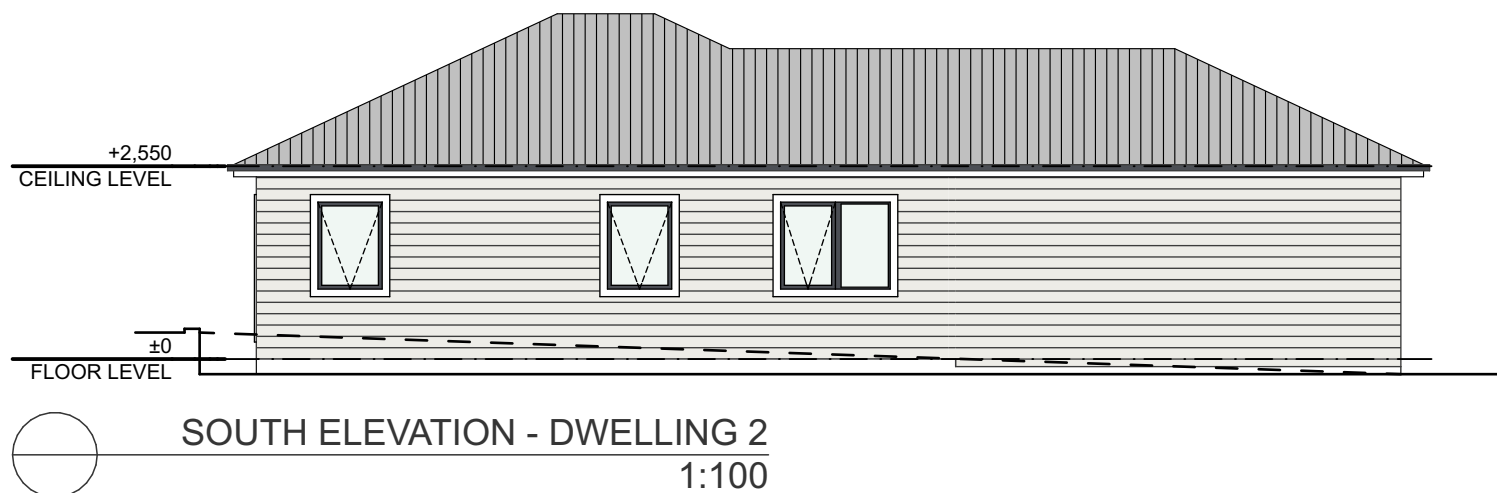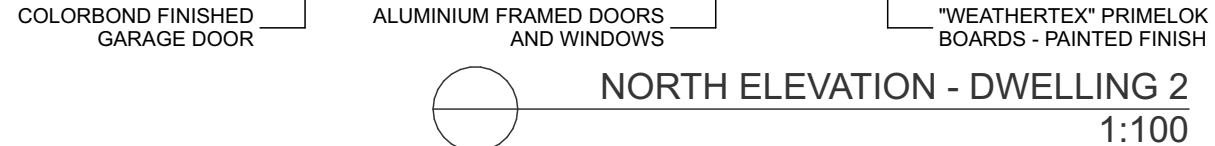


PROJECT NO. **22-041**
DATE: February 2023


CHECK COPY - NOT FOR SUBMISSION

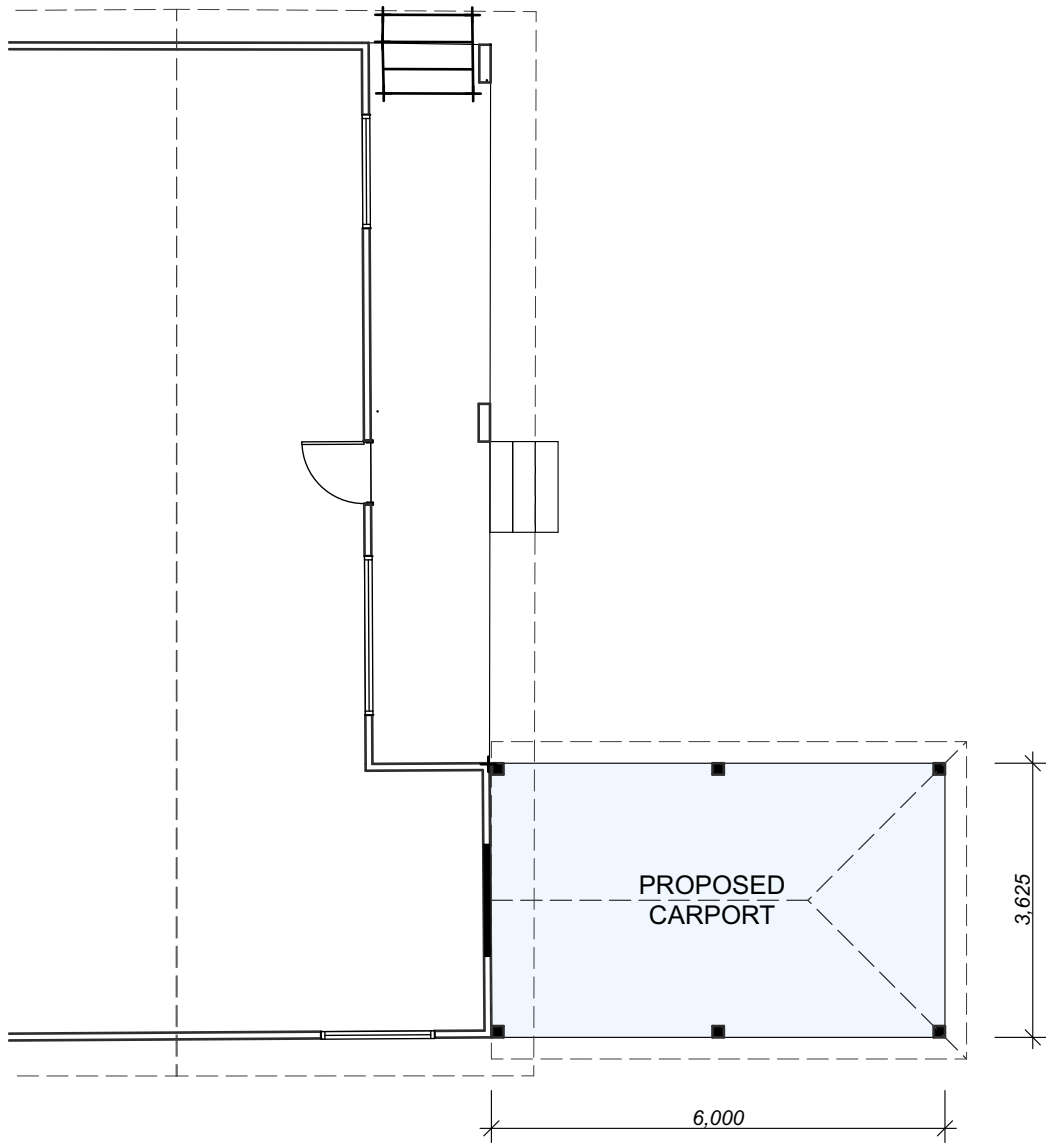


CARPORT FLOOR PLAN
1:100

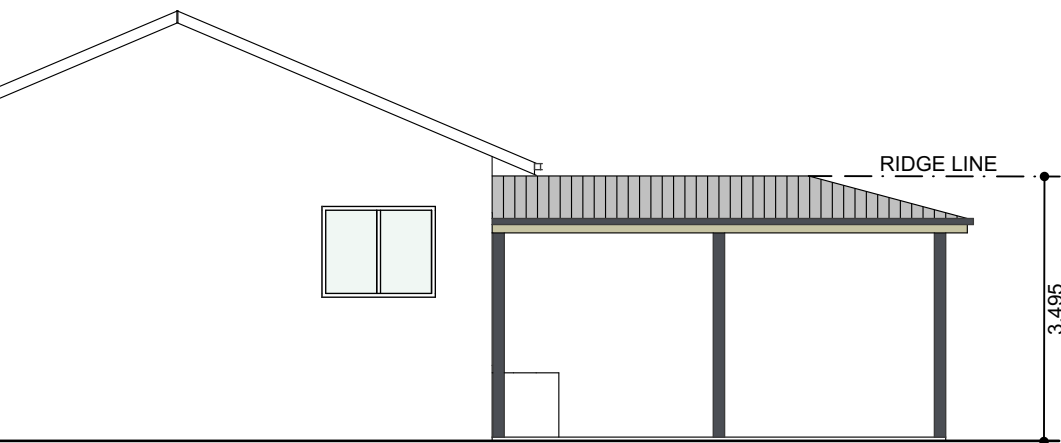

SOUTH ELEVATION - CARPORT
1:100

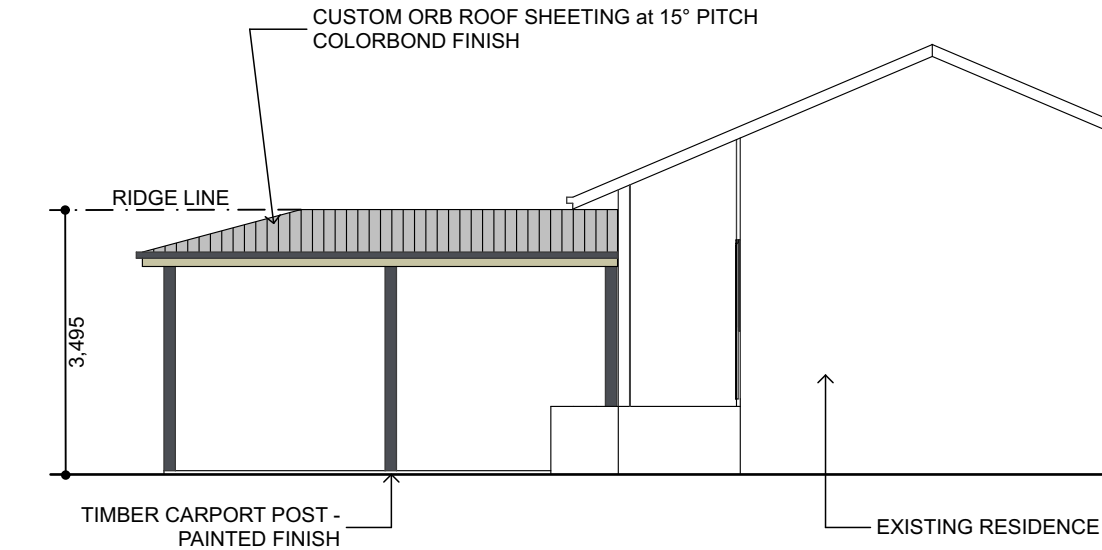

NORTH ELEVATION - CARPORT
1:100

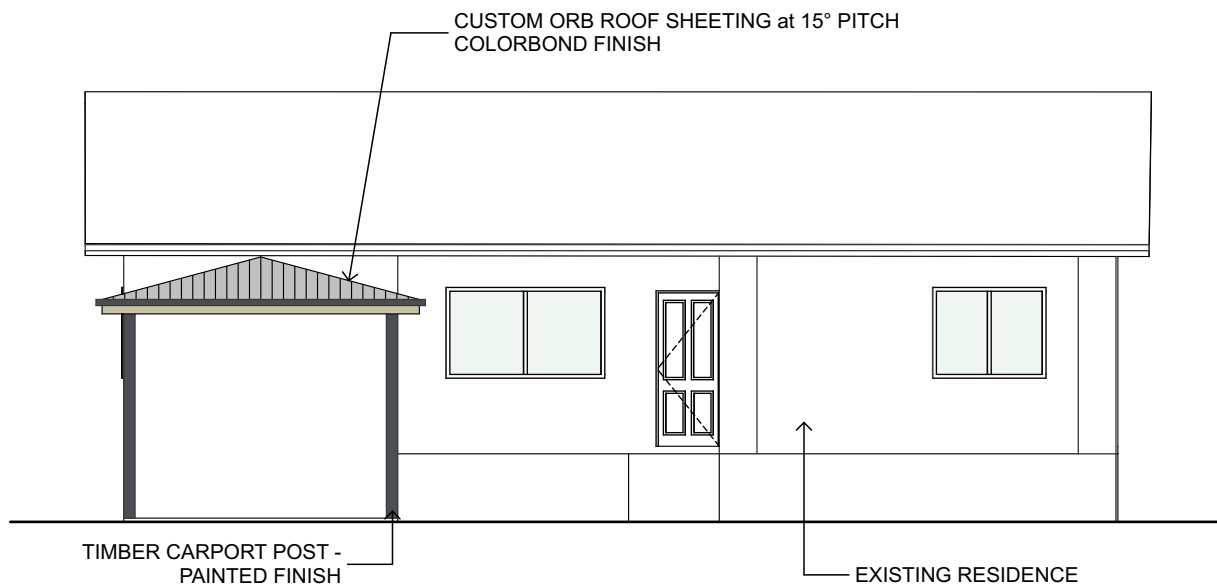

EAST ELEVATION - CARPORT
1:100

CHECK COPY - NOT FOR SUBMISSION

NOTE
The Builder shall check all dimensions and levels on site prior to construction. Notify any errors, discrepancies or omissions to the Building Designer. Refer to written dimensions only. Do not scale drawings. Drawings shall not be used for construction purposes until issued for construction. This drawing reflects a design by Designs AT M and is to be used only for work when authorised in writing by Designs AT M.

All boundaries and contours are subject to survey drawing . All levels to Australian Height Data. It is the contractors responsibility to confirm all measurements on site and locations of any services prior to work on site.

All documents here within are subject to Australian Copyright Laws.

© THIS DRAWING AND THE CONCEPTS REMAIN THE PROPERTY OF DESIGNS AT M. ANY UNAUTHORISED USE OF THIS DRAWING, AS TO THE WHOLE OR PART MAY RENDER THE USER LIABLE TO AN ACTION FOR DAMAGES, CONSEQUENTIAL EVENTS OR DAMAGES ARISING FROM UNWARRANTED OR UNAUTHORISED USE SHALL NOT RENDER DESIGNS AT M LIABLE.

Project Partners

Refer to consultant documentation when directed

- BASIX/Nathers Consultant -
- Surveyor -
- Structural Engineer -
- Civil Engineer -
- Planning Consultant -
- Hydraulic Engineer
- Landscape Designer -
- Mechanical Engineer -

Revision No.	Transmittal Set Name	Date	Drawn by



Drawn | Checked MP | NBKP

Client ROHAN & JULIE OFFORD

5 McLACHLAN STREET
ORANGE

Site: LOT 21 - SECTION 5 - DP8196

DRAWING TITLE :
**CONSTRUCTION CERTIFICATE
CARPORT PLAN & ELEVATIONS**

PROJECT NAME :

**PROPOSED MULTI-RESIDENTIAL
UNIT DEVELOPMENT**

REVISION NO.

DRAWING NO.

CC10

PROJECT NO. **22-041**
DATE: February 2023

GENERAL NOTES

GENERAL

All building work and construction is to comply with the relevant sections of the National Construction Code - Class 1 & Class 10 - Building Code of Australia

PLANS

Plans are not to be amended by any other person other than Designs AT m personal

Plans remain the property of Designs AT m

DIMENSIONS

All dimensions show in millimeters unless noted otherwise DO NOT SCALE from drawing.

All dimension & levels are to be confirmed on site prior to construction

TIMBER FRAMING

All timber used in the building shall be strictly in accordance with the provisions of AS 1684-2010, national timber framing code.

STAIRWAYS

Construction of any stairways & balustrades shall comply with the requirements of the NCC- V2 - Part 3.9.1

STRUCTURAL ELEMENTS

All structural concrete & steelwork to be desinged by a qualified structural engineer.

INSULATION

Wall & Ceiling insulation refer to BASIX / NATHERS certificate

CONSTRUCTION OF SANITARY COMPARTMENTS

Where a closest pan is within 1200mm of any part of the door frame lift off hinges must be provided to that door as per NCC - V 2 - Part 3.8.3.3 requirements

DAMP PROOFING OF FLOORS ON THE GROUND

At least 1 Bathroom: individual fan, not ducted, operation control: manual switch on/off.

Vapour barrier in accordance with AS 2870 NCC - V 2 Part 3.2.2.6 to prevent moisture reaching the upper surface of the floor.

SMOKE DETECTION

Smoke detectors to be installed in accordance in accordance with NCC - V 2 - Part 3.7.2 and AS 3786 and 1670.

VENTILATION

Kitchen: individual fan, ducted to facade or roof, operation control: manual switch on/off.

Laundry: natural ventilation only, or no laundry, operation control: manual switch on/off.

In accordance with NCC - V2 - Part 3.8.5

WET AREAS

Water proofing of wet areas must comply with the NCC - V2 - 3.8.1 and relevant parts of A.S. 3740

TERMITE PROTECTION

Termite risk management in accordance with AS 3660.1-2000 and NCC - V2 - 3.1.3 must be provided

MASONRY STRUCTURE

All masonry shall be in accordance with AS 3700 - 2011, AS 4773 Parts 1 & 2, and NCC - V2 - 3.3.1







GUTTERS AND DOWNPIPES

All gutters and downpipes shall be in accordance with AS/NZ 3500.3 & AS/NZ 3500.5 and NCC - V2 - 3.5.2

GLAZING

All glazing to comply with NCC - V2 - Part 3.6 in accordance with AS 2047 and AS 1288

PLANS TO BE READ IN CONJUNCTION WITH BASIX/NATHERS CERTIFICATE

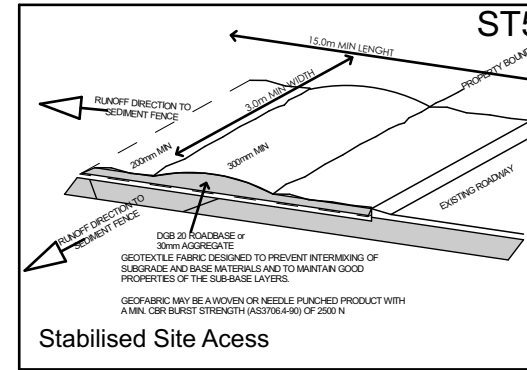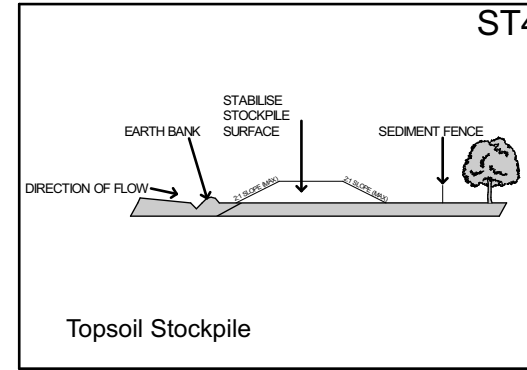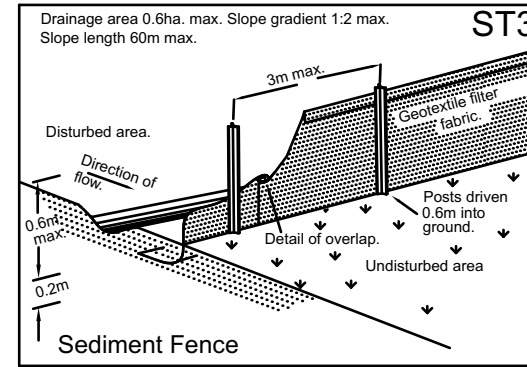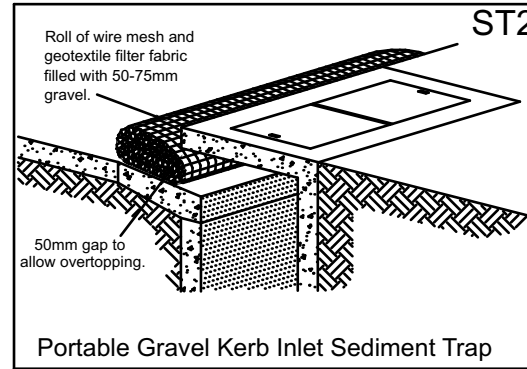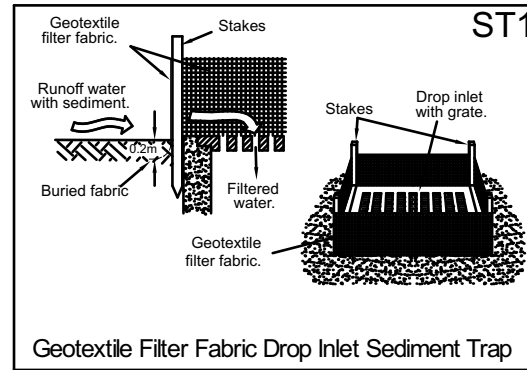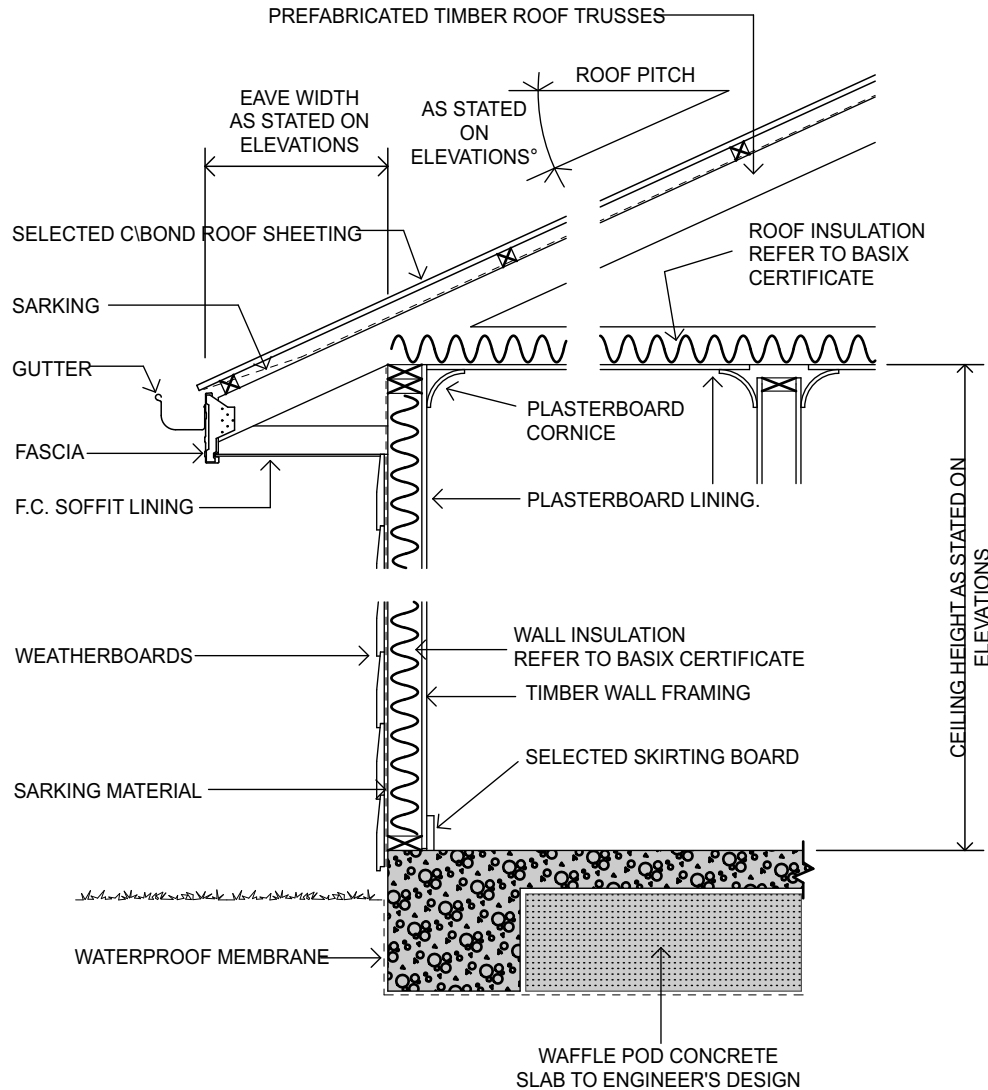

CHECK COPY - NOT FOR SUBMISSION

NOTE
The Builder shall check all dimensions and levels on site prior to construction. Notify any errors, discrepancies or omissions to the Building Designer. Refer to written dimensions only. Do not scale drawings. Drawings shall not be used for construction purposes until issued for construction. This drawing reflects a design by Designs AT M and is to be used only for work when authorised in writing by Designs AT M.

All boundaries and contours are subject to survey drawing . All levels to Australian Height Data. It is the contractors responsibility to confirm all measurements on site and locations of any services prior to work on site.

All documents here within are subject to Australian Copyright Laws.

© THIS DRAWING AND THE CONCEPTS REMAIN THE PROPERTY OF DESIGNS AT M. ANY UNAUTHORISED USE OF THIS DRAWING, AS TO THE WHOLE OR PART MAY RENDER THE USER LIABLE TO AN ACTION FOR DAMAGES, CONSEQUENTIAL EVENTS OR DAMAGES ARISING FROM UNWARRANTED OR UNAUTHORISED USE SHALL NOT RENDER DESIGNS AT M LIABLE.

Project Partners

Refer to consultant documentation when directed

- BASIX/Nathers Consultant -
- Surveyor -
- Structural Engineer -
- Civil Engineer -
- Planning Consultant -
- Hydraulic Engineer
- Landscape Designer -
- Mechanical Engineer -

Position	Transmittal Set Name	Date	Drawn by



Drawn | Checked |

Client ROHAN & JULIE OFFORD

5 McLACHLAN STREET
ORANGE

Site: LOT 21 - SECTION 5 - DP8196

DRAWING TITLE :
**CONSTRUCTION CERTIFICATE
DETAILS**

PROJECT NAME :

**PROPOSED MULTI-RESIDENTIAL
UNIT DEVELOPMENT**


REVISION NO.

DRAWING NO.

CC11

PROJECT NO. **22-041**

DATE: February 2023

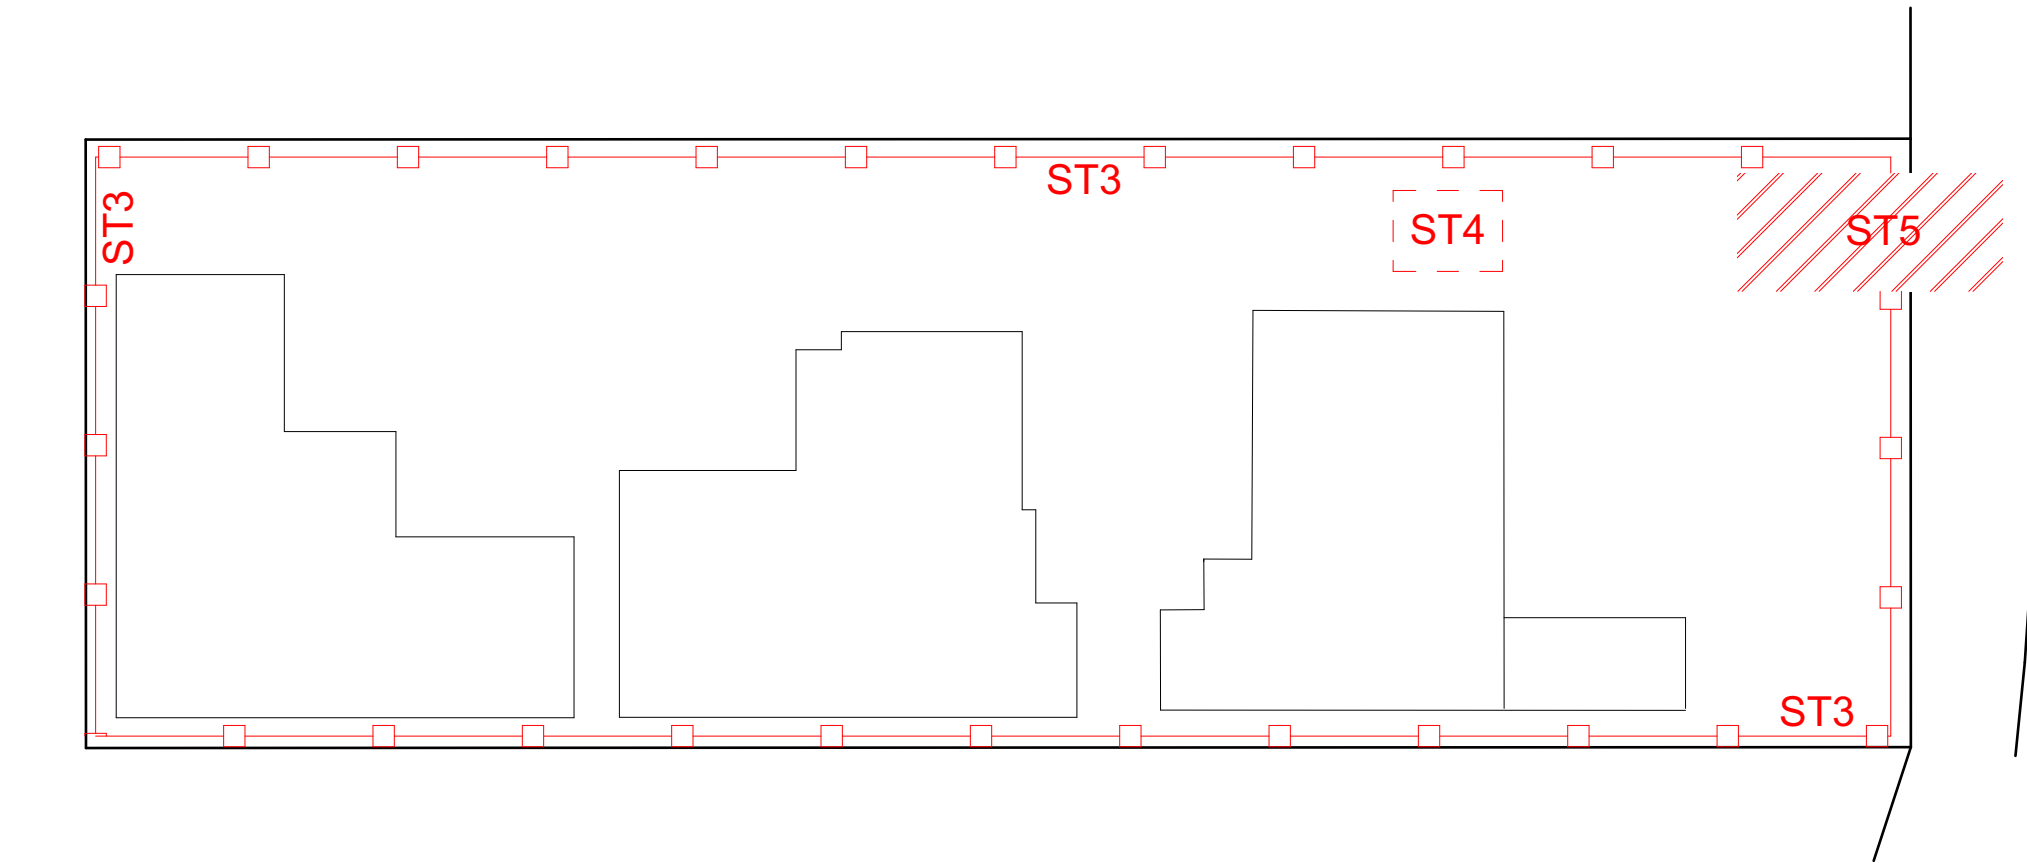

SUBDIVISION PLAN
1:250

CHECK COPY - NOT FOR SUBMISSION

NOTE
The Builder shall check all dimensions and levels on site prior to construction. Notify any errors, discrepancies or omissions to the Building Designer. Refer to written dimensions only. Do not scale drawings. Drawings shall not be used for construction purposes until issued for construction. This drawing reflects a design by Designs AT M and is to be used only for work when authorised in writing by Designs AT M.

All boundaries and contours are subject to survey drawing . All levels to Australian Height Data. It is the contractors responsibility to confirm all measurements on site and locations of any services prior to work on site.

All documents here within are subject to Australian Copyright Laws.

© THIS DRAWING AND THE CONCEPTS REMAIN THE PROPERTY OF DESIGNS AT M. ANY UNAUTHORISED USE OF THIS DRAWING, AS TO THE WHOLE OR PART MAY RENDER THE USER LIABLE TO AN ACTION FOR DAMAGES, CONSEQUENTIAL EVENTS OR DAMAGES ARISING FROM UNWARRANTED OR UNAUTHORISED USE SHALL NOT RENDER DESIGNS AT M LIABLE.

- Project Partners**
Refer to consultant documentation when directed
- BASIX/Nathers Consultant -
 - Surveyor -
 - Structural Engineer -
 - Civil Engineer -
 - Planning Consultant -
 - Hydraulic Engineer
 - Landscape Designer -
 - Mechanical Engineer -

Revision No.	Transmittal Set Name	Date	Drawn by





designsatm



bdaa
BUILDING DESIGNERS
ASSOCIATION OF AUSTRALIA

7 Aminya Place
Orange NSW 2800
+612 6361 7461
0409 982 793
office@designsatm.com.au
www.designsatm.com.au

Drawn | Checked |

Client **ROHAN & JULIE OFFORD**

5 McLACHLAN STREET
ORANGE

Site: **LOT 21 - SECTION 5 - DP8196**

DRAWING TITLE :
**CONSTRUCTION CERTIFICATE
EROSION CONTROL PLAN**


PROJECT NAME :
**PROPOSED MULTI-RESIDENTIAL
UNIT DEVELOPMENT**

REVISION NO.

DRAWING NO.

CC12

PROJECT NO. **22-041**
DATE: February 2023

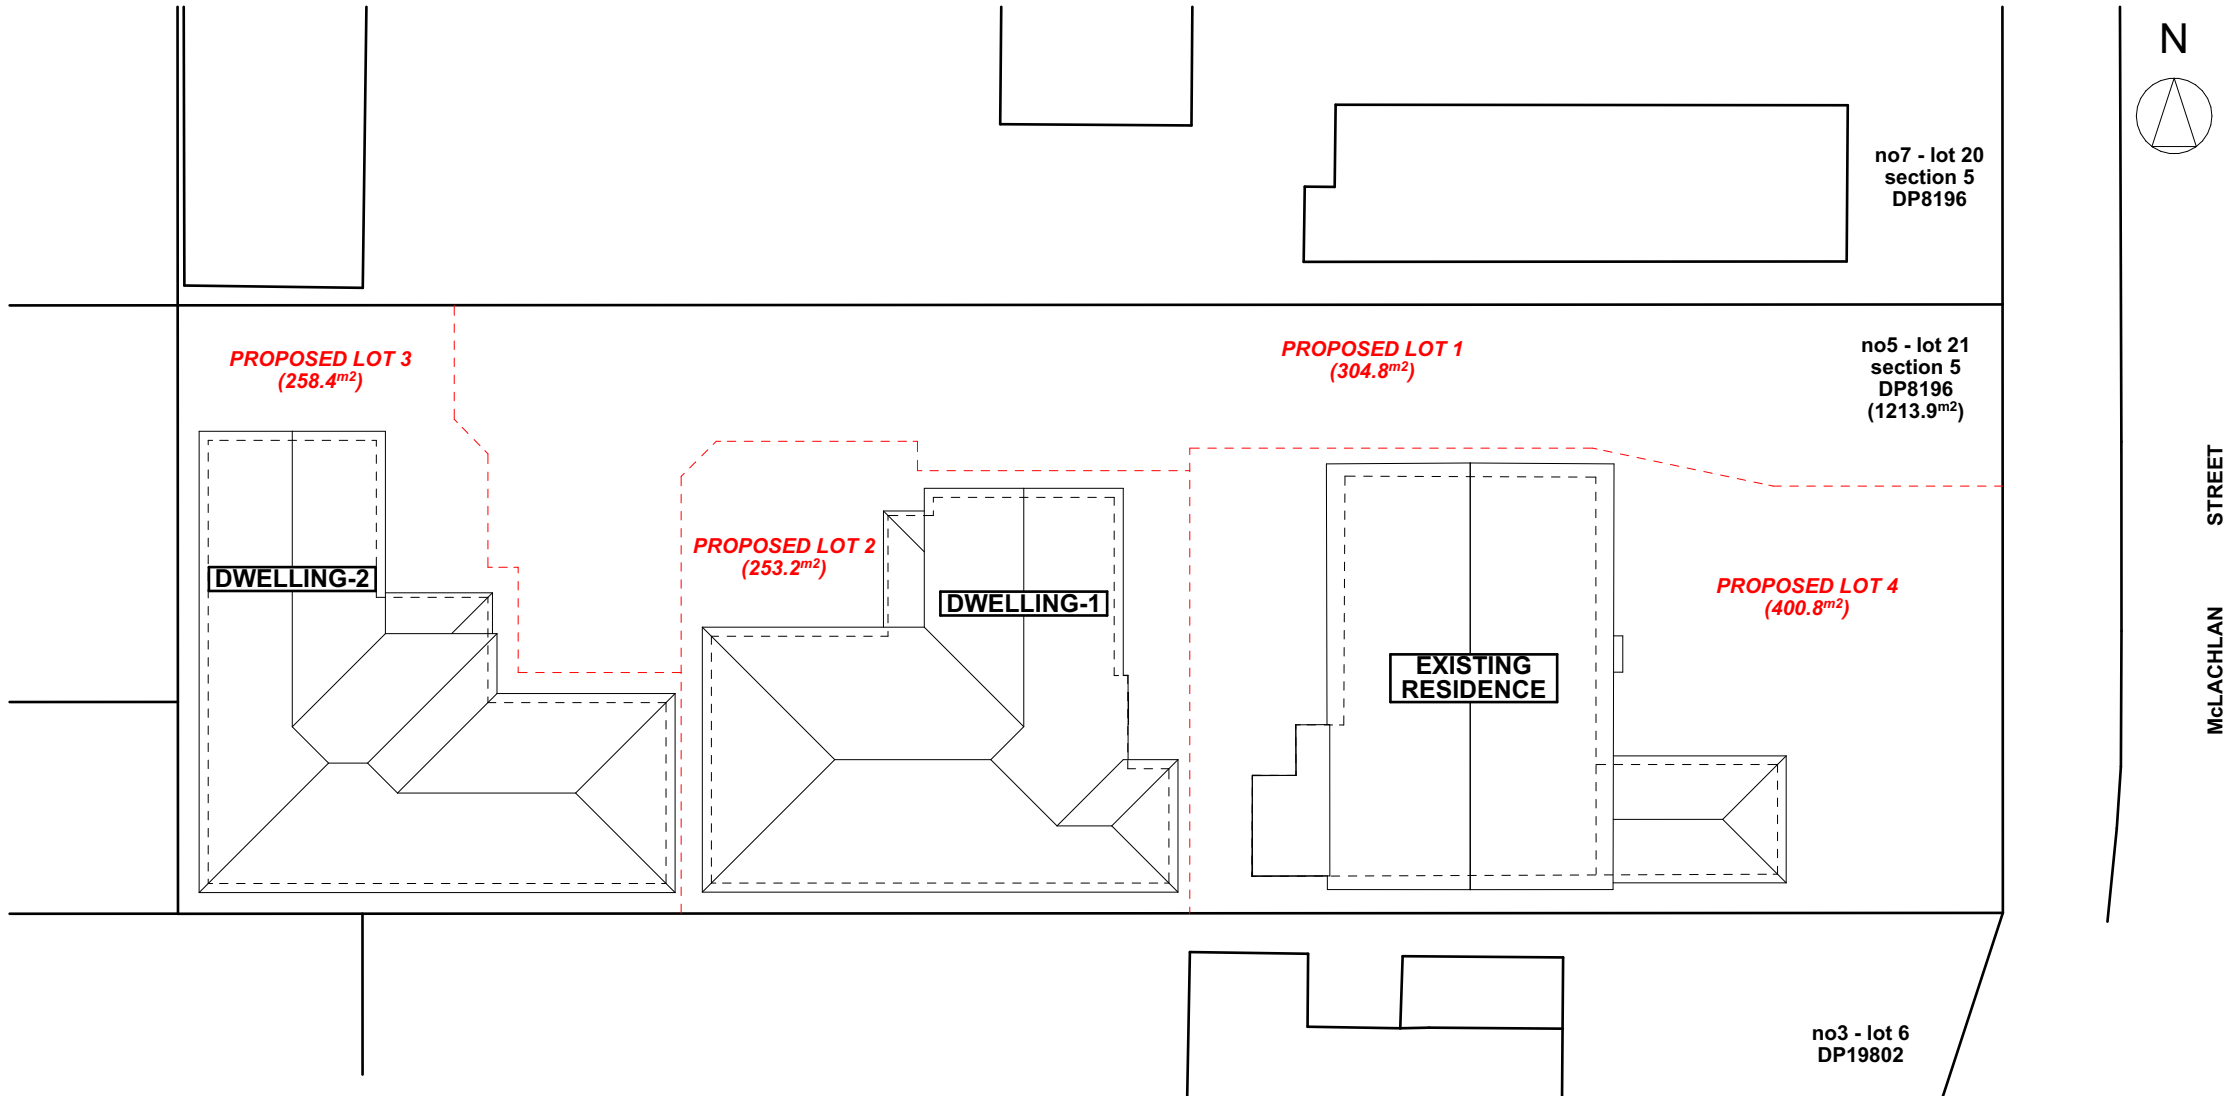

SUBDIVISION PLAN
1:250

CHECK COPY - NOT FOR SUBMISSION

Volume:Shared\DA\2222222041 - ROHAN & JULIE OFFORD\ARCHITECTURAL PLANS\CONSTRUCTION CERTIFICATE\22041CC.gn

NOTE
The Builder shall check all dimensions and levels on site prior to construction. Notify any errors, discrepancies or omissions to the Building Designer. Refer to written dimensions only. Do not scale drawings. Drawings shall not be used for construction purposes until issued for construction. This drawing reflects a design by Designs AT M and is to be used only for work when authorised in writing by Designs AT M.

All boundaries and contours are subject to survey drawing . All levels to Australian Height Data. It is the contractors responsibility to confirm all measurements on site and locations of any services prior to work on site.

All documents here within are subject to Australian Copyright Laws.

© THIS DRAWING AND THE CONCEPTS REMAIN THE PROPERTY OF DESIGNS AT M. ANY UNAUTHORISED USE OF THIS DRAWING, AS TO THE WHOLE OR PART MAY RENDER THE USER LIABLE TO AN ACTION FOR DAMAGES, CONSEQUENTIAL EVENTS OR DAMAGES ARISING FROM UNWARRANTED OR UNAUTHORISED USE SHALL NOT RENDER DESIGNS AT M LIABLE.

Project Partners
Refer to consultant documentation when directed
- BASIX/Nathers Consultant -
- Surveyor -
- Structural Engineer -
- Civil Engineer -
- Planning Consultant -
- Hydraulic Engineer
- Landscape Designer -
- Mechanical Engineer -

Revision No.	Transmittal Set Name	Date	Drawn by



0008020130 02 Sep 2022

Assessor: marc kiho
Accreditation No. 20094
Address
5 McLachlan St., Orange,
NSW, 2800

hstar.com.au



ABSA
Accreditation No. 310305002-310305003
Assessor Name: Marc Kiho
Assessment Number: 20094



designsatm

office@designsatm.com.au
www.designsatm.com.au



bdaa
BUILDING DESIGNERS
ASSOCIATION OF AUSTRALIA

7 Aminya Place
Orange NSW 2800
+612 6361 7461
0409 982 793

Drawn | Checked |

Client **ROHAN & JULIE OFFORD**

5 McLACHLAN STREET
ORANGE

Site: **LOT 21 - SECTION 5 - DP8196**

DRAWING TITLE :
**CONSTRUCTION CERTIFICATE
SUBDIVISION PLAN**

PROJECT NAME :
**PROPOSED MULTI-RESIDENTIAL
UNIT DEVELOPMENT**

REVISION NO.

DRAWING NO.
CC13

PROJECT NO. **22-041**
DATE: February 2023