

THIS DRAWING IS SUBJECT TO COPYRIGHT LAWS AND  
MAY NOT BE COPIED WITHOUT THE WRITTEN PERMISSION  
OF THRIVE HOMES PTY LTD-ACN 613 679 333



NOTES:

\* ALL DIMENSIONS ARE IN MILLIMETERS

\* DO NOT SCALE THE DRAWING - USE WRITTEN  
DIMENSIONS

\* IT IS THE RESPONSIBILITY OF THE OWNER TO  
ENSURE THAT THE LAYOUT AND ALL SPECIAL  
INCLUSIONS ARE CORRECT

\* THRIVE HOMES PTY. LIMITED WILL TAKE NO  
RESPONSIBILITY FOR ANY VERBAL DISCUSSIONS  
OR INSTRUCTIONS. ALL CHANGES AND SPECIAL  
INCLUSIONS MUST BE DOCUMENTED IN WRITING.

\* THIS DRAWING IS SUBJECT TO COPYRIGHT LAWS  
AND MAY NOT BE COPIED WITHOUT THE WRITTEN  
PERMISSION OF THRIVE HOMES PTY. LIMITED -  
ACN 613 679 333

SCHEDULE OF DRAWINGS:

| SHEET | CONTENTS              |
|-------|-----------------------|
| 01    | COVER SHEET           |
| 02    | SITE PLAN             |
| 03    | FLOOR PLAN            |
| 04    | ROOF PLAN             |
| 05    | ELEVATIONS 1-2        |
| 06    | ELEVATIONS 3-4        |
| 07    | SECTIONS & BASIX      |
| 08    | WET AREA PLANS        |
| 09    | SLAB SETOUT PLAN      |
| 10    | SEDIMENT CONTROL PLAN |
| 11    | STORMWATER PLAN       |
| D01   | SLAB DETAILS 1        |
| D02   | SLAB DETAILS 2        |
| D03   | WALL OPENINGS DETAILS |
| D04   | TYPICAL EAVES DETAILS |

AMENDMENTS

| ISS | DESCRIPTION                                                        | BY         | DATE     |
|-----|--------------------------------------------------------------------|------------|----------|
| A   | LODGEMENT PLANS                                                    | PG<br>(BM) | 30.09.25 |
| B   | AMENDED LODGEMENT PLAN<br>(REPORTS & CC RFI)                       | PG<br>(BM) | 10.02.26 |
| C   | AMENDED LODGEMENT PLAN<br>(HYBRID FRAME CONSTRUCTION<br>WITH PODS) | PG<br>(BM) | 05.03.26 |
| D   | AMENDED LODGEMENT PLAN<br>(HYBRID FRAME CONSTRUCTION<br>WITH PODS) | PG<br>(BM) | 14.04.26 |
| E   | CONSTRUCTION PLANS                                                 | BM         | 23.04.26 |
|     |                                                                    |            |          |

CONSTRUCTION PLANS - CDC

SIGNATURE: \_\_\_\_\_

HYBRID FRAME CONSTRUCTION WITH PODS

NOTES:

PLEASE NOTE: DETAILS SHOWN ON THESE PLANS ARE INTENDED  
TO BE ACCURATE - HOWEVER INFORMATION WRITTEN INTO  
INDIVIDUAL CONTRACTS WILL TAKE PRECEDENCE OVER PLANS  
\* ALL DIMENSIONS ARE IN MILLIMETRES  
\* DO NOT SCALE - USE WRITTEN DIMENSIONS  
\* ALL DIMENSIONS ARE TO STRUCTURAL FRAMES ONLY  
EXCLUDING FINISHED SURFACES

**ThriveHomes**  
LEVEL 7, 5 RIDER BOULEVARD  
RHODES NSW 2138  
TELEPHONE 02 8758 4800  
FAX 02 9300 5646  
  
Builder's licence No. 301349C

CLIENT:  
THRIVE HOMES

SITE ADDRESS:  
LOT 186 (DP 1304135)  
NO. 39 KEIGHTLEY AVENUE, WINDRADYNE  
BATHURST, NSW 2795

HOUSE TYPE: ALLIRA 25  
FACADE: COVE  
TYPE: DOUBLE GARAGE  
SPECIFICATION: STANDARD

DRAWING TITLE:  
COVER SHEET

DRAWN BY: DD  
DATE DRAWN: 23.04.26

COUNCIL AREA:  
BATHURST

JOB No:  
T001734

SCALE:

DRWG No:  
01

ISSUE:  
E

## LEGEND

- HOT WATER TANK
- WATER NETTER
- TELECOM PIT
- MANHOLE (SEWER/STORMWATER)
- SEWER TERMINAL MAINTENANCE SHAFT
- SEWER MAINTENANCE SHAFT
- VEHICLE CROSSING
- KERB INLET PIT
- LIGHT POLE
- ELECTRICITY POLE
- ELECTRICITY PILLAR
- HYDRANT
- STOP VALVE
- KERB OUTLET
- SERVICE CONDUIT
- TREE (DIA/HEIGHT)
- GARDEN BED
- SHRUB
- DENOTES TELEPHONE BOOTH

## SITE NOTES:

BEFORE STARTING WORK ON SITE CHECK FOLLOWING:

- SERVICE LOCATIONS
  - SEWER CONNECTION POSITION
  - DRIVEWAY ALIGNMENT & LEVELS
- \*N2 WIND CATEGORY\***

DP ○ INDICATES DOWNPIPE LOCATION

### CDC TREE PLANTING REQUIREMENT:

- CLIENT TO PLANT TREE TO FRONT YARD THAT WILL REACH A HEIGHT OF 5M AT MATURITY
- CLIENT TO PLANT TREE TO REAR YARD THAT WILL REAR A HEIGHT OF 8M AT MATURITY

**1100mm FALL ACROSS BUILDING ENVELOPE**

GARAGE INTERNAL DIMENSION  
5550mm (W) x 5550mm (D)

**\*\*B.A.S\*\***  
(BUILDING ADJACENT TO SEWER)  
**ORDER SEWER PEGOUT**

THIS DRAWING IS SUBJECT TO COPYRIGHT LAWS AND  
MAY NOT BE COPIED WITHOUT THE WRITTEN PERMISSION  
OF THRIVE HOMES PTY LTD-ACN 613 679 333

| SITE CALCULATIONS CDC                                   |        |                |
|---------------------------------------------------------|--------|----------------|
| GROUND FLOOR                                            | 184.41 | m <sup>2</sup> |
| GARAGE AREA                                             | 33.37  | m <sup>2</sup> |
| TOTAL GROSS FLOOR AREA<br>(EXCLUDING GARAGE CONCESSION) | 199.78 | m <sup>2</sup> |
|                                                         |        |                |
| SITE AREA                                               | 637.50 | m <sup>2</sup> |
| BUILDING FOOTPRINT<br>(INCLUDING UNENCLOSED AREA)       | 237.34 | m <sup>2</sup> |
| DRIVEWAY & PATH                                         | 34.70  | m <sup>2</sup> |
| CROSSOVER                                               | 17.15  | m <sup>2</sup> |
|                                                         |        |                |
| TOTAL FRONT AREA                                        | 80.26  | m <sup>2</sup> |
| FRONT LANDSCAPE AREA                                    | 56.76  | %              |
| TOTAL LANDSCAPE AREA                                    | 365.46 | m <sup>2</sup> |
| LANDSCAPE AREA (%)                                      | 57.33  | %              |

### SEPP 2017 REQUIREMENTS CDC

|   |        |                |
|---|--------|----------------|
| SITE AREA   | 637.50 | m <sup>2</sup> |
| MAXIMUM GROSS FLOOR AREA   | 335.00 | m <sup>2</sup> |
| MINIMUM LANDSCAPED AREA   | 30.00  | %              |
| <small>- GROSS FLOOR AREA MEANS THE SUM OF THE FLOOR AREA OF EACH FLOOR OF A BUILDING MEASURED FROM THE INTERNAL FACE OF EXTERNAL WALLS</small> |        |                |
| <small>- LANDSCAPED AREA MUST HAVE A MINIMUM WIDTH AND LENGTH OF 1.5M</small>                                                                   |        |                |

KEIGHTLEY AVENUE

COVERED FINISHED COLOURED  
SEALED CONCRETE DRIVEWAY &  
FRONT PATH, PLAIN CONCRETE  
CROSSOVER BY THRIVE HOMES.  
COLOUR SEAL TO DRIVEWAY  
WITHIN BOUNDARY ONLY  
(EXCLUDING ACT)

3 x 900W FULLY BRICK  
STEPS WITH TILED FINISH

APPROX. LOCATION  
OF 5m TREE

SURVEY BENCHMARK  
(DRILLHOLE IN KERR  
RL: 689.071)

APPROX. LOCATION  
OF SEWER MAIN


LINE OF ENCROACHMENT  
ARTICULATION ZONE = 3.0m (CDC)

LINE OF MIN. FRONT  
SETBACK = 4.5m (CDC)

AREA OF ALL BUILDING  
ELEMENTS IN THE ARTICULATION  
ZONE = 5.13m<sup>2</sup>(20.09%)  
SHOWN IN RED HATCH

AREA OF ARTICULATION  
ZONE = 25.53m<sup>2</sup>  
SHOWN IN GREEN HATCH

24m<sup>2</sup> (6m x 4m) PRINCIPAL  
PRIVATE OPEN SPACE .  
MAX GRADIENT 1:50 -  
OWNER TO PROVIDE MINOR  
EARTHWORKS AFTER  
HANDOVER TO ACHIEVE  
GRADIENT, IF REQUIRED

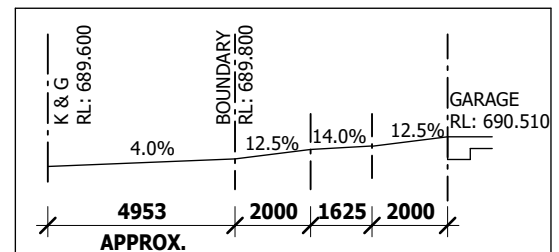

NOTE: DRIVEWAY TO COMPLY WITH AS2890.1:2004;



The Essential First Step

### NOTES:

PLEASE NOTE: DETAILS SHOWN ON THESE PLANS ARE INTENDED  
TO BE ACCURATE - HOWEVER INFORMATION WRITTEN INTO  
INDIVIDUAL CONTRACTS WILL TAKE PRECEDENCE OVER PLANS

- \* ALL DIMENSIONS ARE IN MILLIMETRES
- \* DO NOT SCALE - USE WRITTEN DIMENSIONS
- \* ALL DIMENSIONS ARE TO STRUCTURAL FRAMES ONLY  
EXCLUDING FINISHED SURFACES

**ThriveHomes**

LEVEL 7, 5 RIDER BOULEVARD  
RHODES NSW 2138  
TELEPHONE 02 8758 4800  
FAX 02 9300 5646

Builder's licence No. 301349C

### CLIENT:

THRIVE HOMES

### SITE ADDRESS:

LOT 186 (DP 1304135)  
NO. 39 KEIGHTLEY AVENUE, WINDRADYNE  
BATHURST, NSW 2795

### HOUSE TYPE:

ALLIRA 25

### FACADE:

COVE

### TYPE:

DOUBLE GARAGE

### SPECIFICATION:

STANDARD

### DRAWING TITLE:

SITE PLAN

### DRAWN BY:

DD

### DATE DRAWN:

23.04.26

### SCALE:

1 : 200

### COUNCIL AREA:

BATHURST

### DRWG No:

02

### JOB No:

T001734

### ISSUE:


E

- ALL EXTERNAL DOORS TO BE FITTED WITH DRAFT EXCLUSION DEVICE
- WC DOORS TO BE FITTED WITH LIFT-OFF HINGES
- WINDOW OPENING SIZES TO BE CHECKED BEFORE FRAMES ARE CONSTRUCTED
- TIMBER TRUSSES TO SATISFY AS 1684 SAA TIMBER FRAMING CODE
- STEEL FRAMES TO SATISFY AS / NZS 4600
- ROOF SPACE TO BE VENTILATED BY EAVE VENTS
- 2040mm DOOR HEIGHTS THROUGHOUT INCLUDING ROBES AND LINEN.
- 2150mm HIGH SQ.SET OPENINGS.

[illegible]

**DWELLING TO BE BUILT IN ACCORDANCE WITH NCC 2022:**

- SMOKE ALARMS TO PART 9.5.1 OF THE BCA
- MECHANICAL VENTILATION TO PART 10.6.2 (C) & 10.8.2 OF THE BCA TO ALL WET AREAS
- WATERPROOFING TO COMPLY WITH PART 10.2 OF THE BCA
- GLAZING TO BE IN ACCORDANCE WITH PART 8.2 OF THE BCA
- CONDENSATION MANAGEMENT TO COMPLY WITH PART 10.8 OF THE BCA

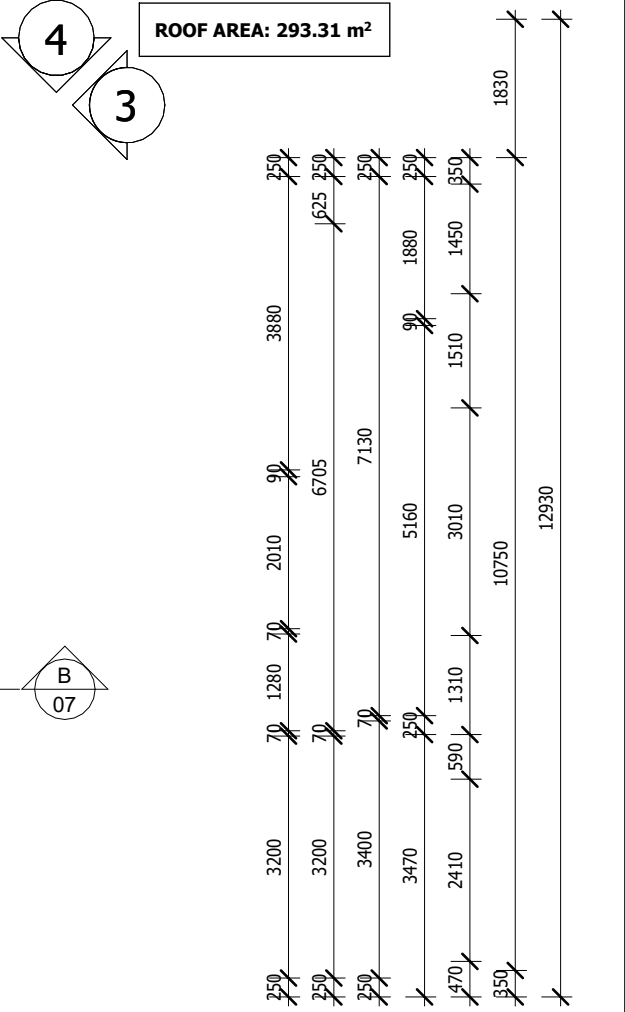

**ROOF AREA: 293.31 m<sup>2</sup>**

| FLOOR AREAS  |                       |
|--------------|-----------------------|
| GROUND FLOOR | 184.41 m <sup>2</sup> |
| GARAGE       | 33.37 m <sup>2</sup>  |
| ALFRESCO     | 11.45 m <sup>2</sup>  |
| PORCH        | 8.10 m <sup>2</sup>   |
| <b>TOTAL</b> | 237.34 m <sup>2</sup> |

PLEASE NOTE: DETAILS SHOWN ON THESE PLANS ARE INTENDED TO BE ACCURATE - HOWEVER INFORMATION WRITTEN INTO INDIVIDUAL CONTRACTS WILL TAKE PRECEDENCE OVER PLANS

- \* ALL DIMENSIONS ARE IN MILLIMETRES
- \* DO NOT SCALE - USE WRITTEN DIMENSIONS
- \* ALL DIMENSIONS ARE TO STRUCTURAL FRAMES ONLY EXCLUDING FINISHED SURFACES



Builder's licence No. 301349C

LOT 186 (DP 1304135)  
NO. 39 KEIGHTLEY AVENUE, WINDRADYNE  
BATHURST, NSW 2795

DRAWING TITLE:  
FLOOR PLAN

JOB No:  
**T001734**

ISSUE:

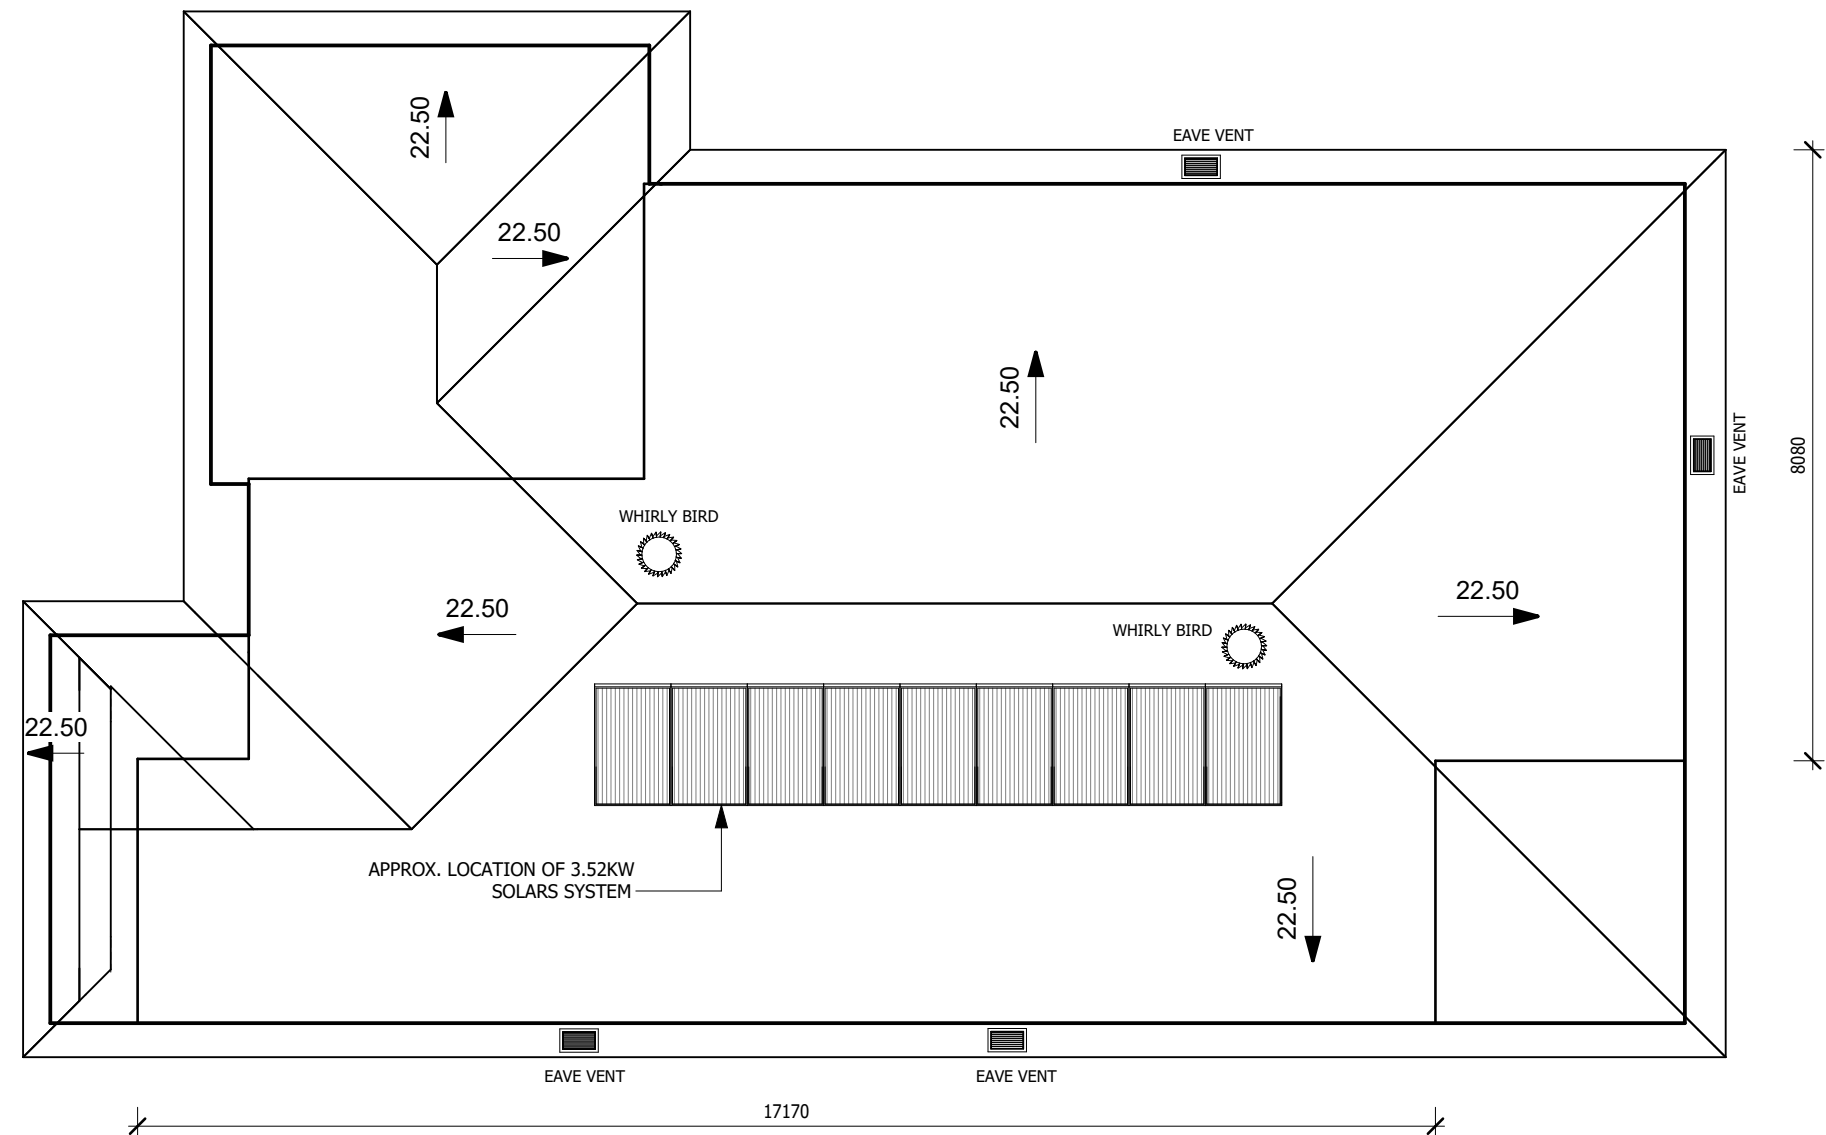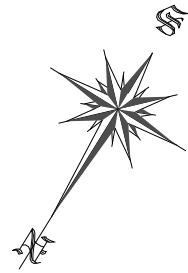

| CONDENSATION CALCULATIONS                                                                             |             |             |              |            |
|---|-------------|-------------|--------------|------------|
| *Whirlybirds must be placed not more 900mm below the ridge height or highest point of the roof space. |             |             |              |            |
|   | ROOF PITCH  | ROOF LENGTH | WHIRLY BIRDS | EAVE VENTS |
| LOWER ROOF                                                                                            | 22.5° PITCH | 16.995(m)   | 2            | 4          |

NOTES:

PLEASE NOTE: DETAILS SHOWN ON THESE PLANS ARE INTENDED TO BE ACCURATE - HOWEVER INFORMATION WRITTEN INTO INDIVIDUAL CONTRACTS WILL TAKE PRECEDENCE OVER PLANS

- \* ALL DIMENSIONS ARE IN MILLIMETRES
- \* DO NOT SCALE - USE WRITTEN DIMENSIONS
- \* ALL DIMENSIONS ARE TO STRUCTURAL FRAMES ONLY EXCLUDING FINISHED SURFACES

**ThriveHomes**  
LEVEL 7, 5 RIDER BOULEVARD  
RHODES NSW 2138  
TELEPHONE 02 8758 4800  
FAX 02 9300 5646  
  
Builder's licence No. 301349C

CLIENT:  
THRIVE HOMES

SITE ADDRESS:  
LOT 186 (DP 1304135)  
NO. 39 KEIGHTLEY AVENUE, WINDRADYNE  
BATHURST, NSW 2795

HOUSE TYPE: ALLIRA 25  
FACADE: COVE  
TYPE: DOUBLE GARAGE  
SPECIFICATION: STANDARD

DRAWING TITLE:  
ROOF PLAN

|                           |                         |                   |
|---------------------------|-------------------------|-------------------|
| DRAWN BY:<br>DD           | DATE DRAWN:<br>23.04.26 | SCALE:<br>1 : 100 |
| COUNCIL AREA:<br>BATHURST |                         | DRWG No:<br>04    |
| JOB No:<br>T001734        |                         | ISSUE:<br>E       |



THIS DRAWING IS SUBJECT TO COPYRIGHT LAWS AND  
MAY NOT BE COPIED WITHOUT THE WRITTEN PERMISSION  
OF THRIVE HOMES PTY LTD-ACN 613 679 333


WINDOW HEAD HEIGHTS TO BE 2143H FROM FFL UNLESS  
STATED OTHERWISE.

CEILING HEIGHT NOMINAL TO FRAME HEIGHT, SUBJECT TO  
SELECTED FLOOR FINISH.


ARTICULATION JOINT REQUIRES ADDITIONAL STUD FOR  
BRICK TIES.

NYLON MESH FLYSCREENS TO ALL OPENING WINDOWS,  
SLIDING AND STACKER DOORS (EXCLUDING HINGED DOORS)

CSR WALL WRAP TO EXTERNAL WALLS

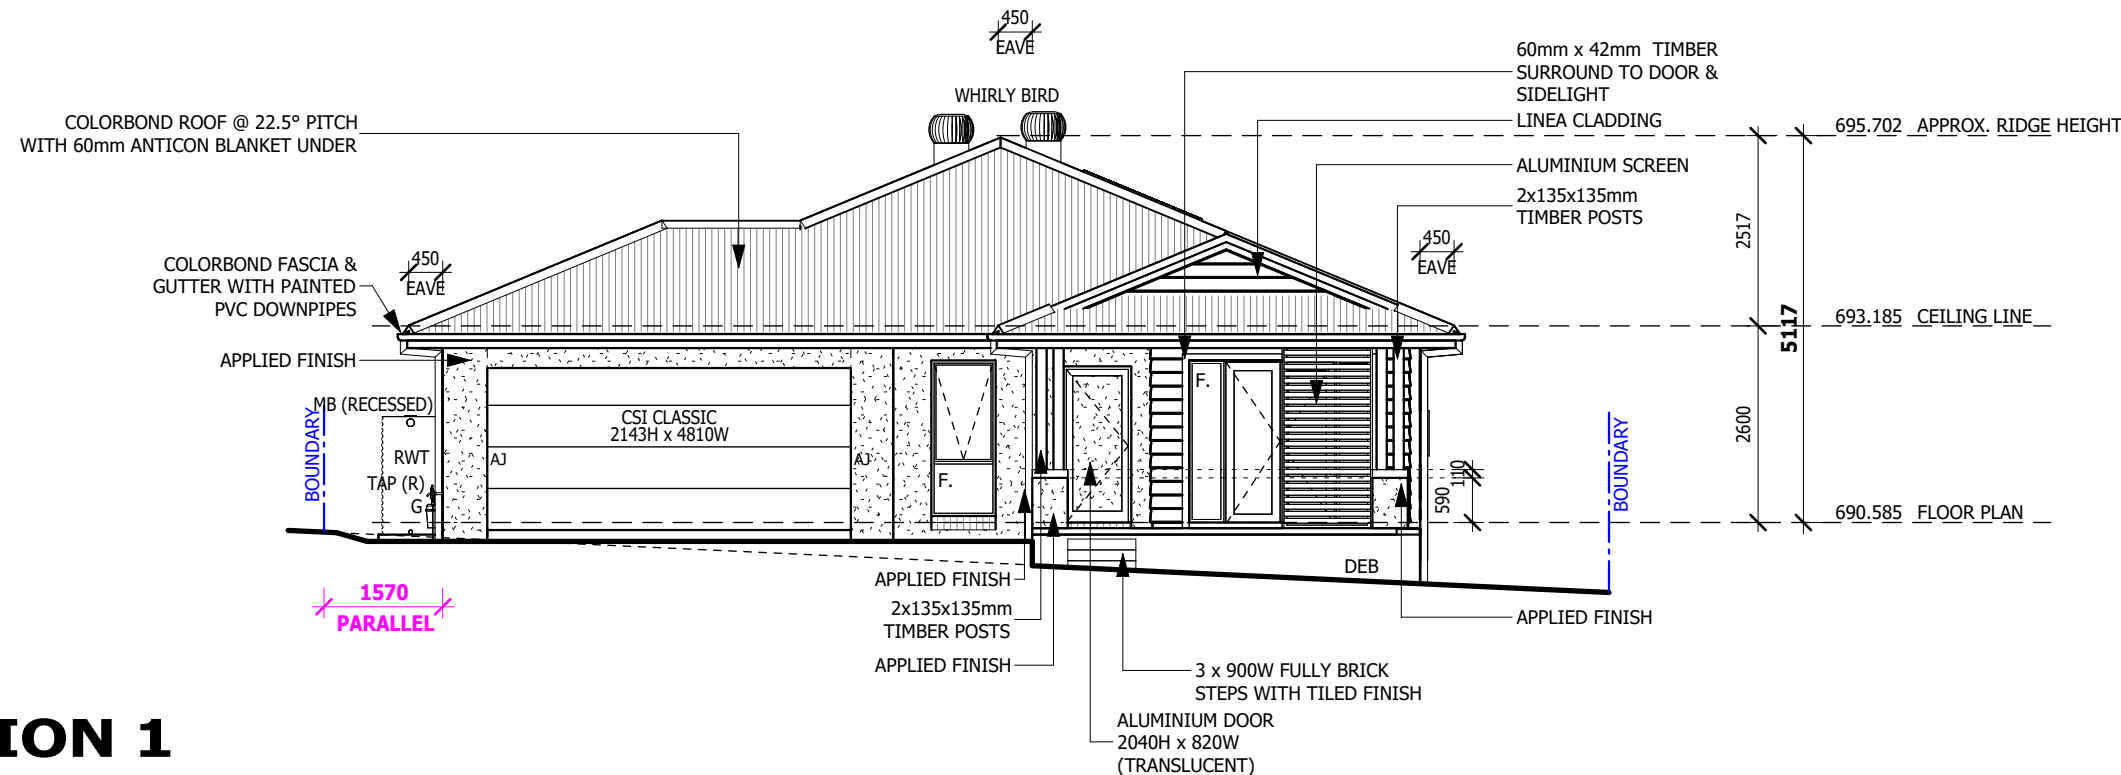

ELEVATION 1

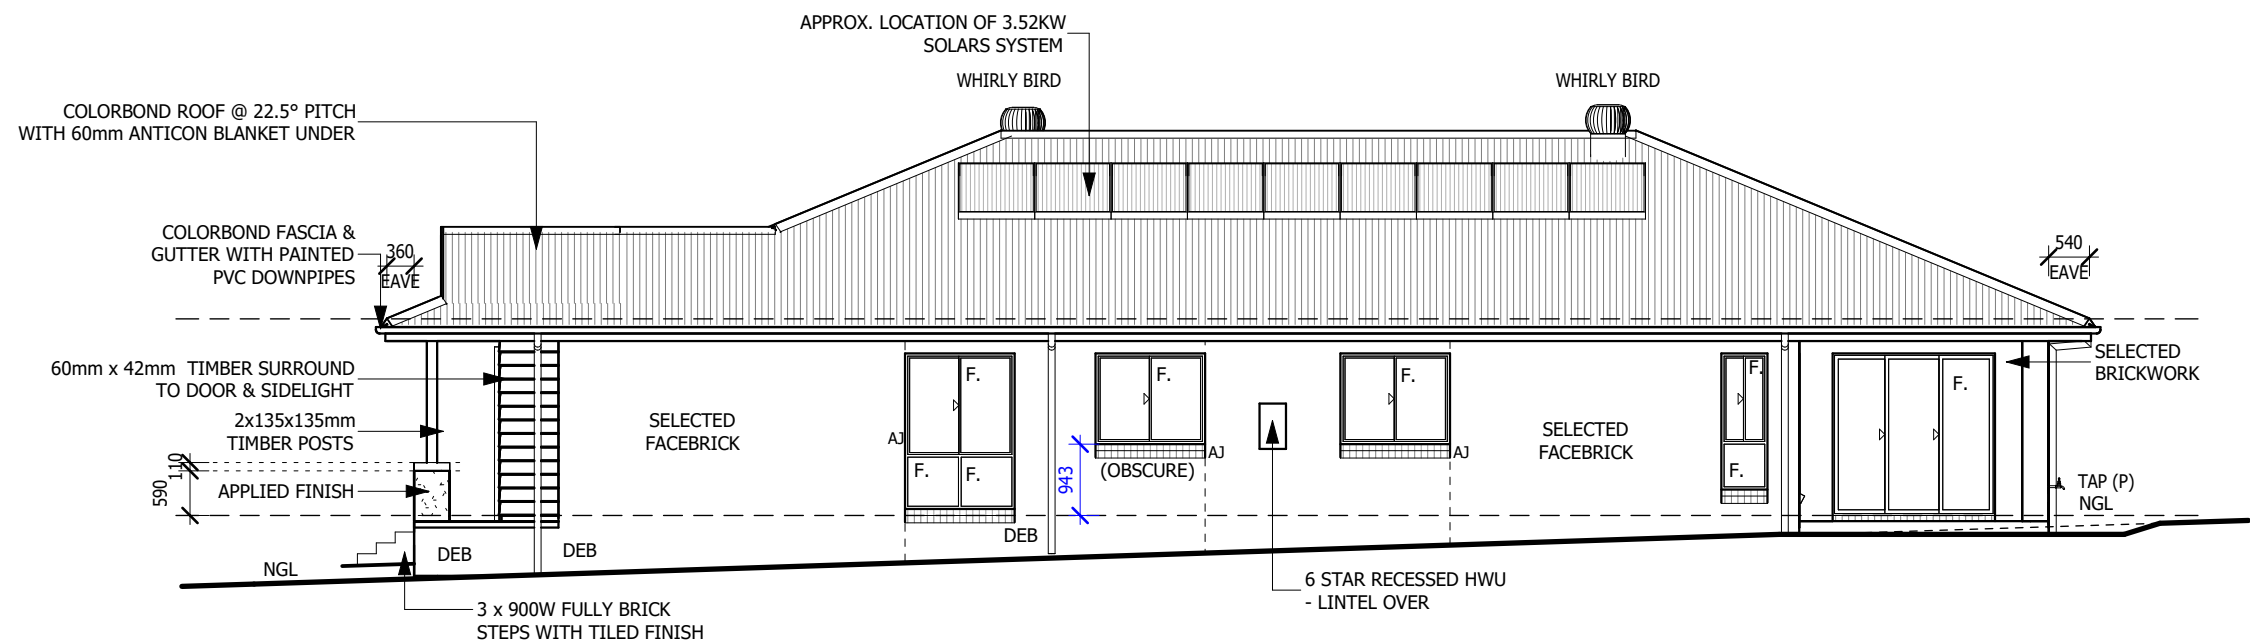

ELEVATION 2

NOTES:

PLEASE NOTE: DETAILS SHOWN ON THESE PLANS ARE INTENDED TO BE ACCURATE - HOWEVER INFORMATION WRITTEN INTO INDIVIDUAL CONTRACTS WILL TAKE PRECEDENCE OVER PLANS

- \* ALL DIMENSIONS ARE IN MILLIMETRES
- \* DO NOT SCALE - USE WRITTEN DIMENSIONS
- \* ALL DIMENSIONS ARE TO STRUCTURAL FRAMES ONLY EXCLUDING FINISHED SURFACES

**ThriveHomes**  
LEVEL 7, 5 RIDER BOULEVARD  
RHODES NSW 2138  
TELEPHONE 02 8758 4800  
FAX 02 9300 5646  
  
Builder's licence No. 301349C

CLIENT:  
THRIVE HOMES

SITE ADDRESS:  
LOT 186 (DP 1304135)  
NO. 39 KEIGHTLEY AVENUE, WINDRADYNE  
BATHURST, NSW 2795

HOUSE TYPE: ALLIRA 25  
FACADE: COVE  
TYPE: DOUBLE GARAGE  
SPECIFICATION: STANDARD  
  
DRAWING TITLE:  
ELEVATIONS 1-2

|                           |                         |                   |
|---------------------------|-------------------------|-------------------|
| DRAWN BY:<br>DD           | DATE DRAWN:<br>23.04.26 | SCALE:<br>1 : 100 |
| COUNCIL AREA:<br>BATHURST |                         | DRWG No:<br>05    |
| JOB No:<br>T001734        |                         | ISSUE:<br>E       |

THIS DRAWING IS SUBJECT TO COPYRIGHT LAWS AND  
MAY NOT BE COPIED WITHOUT THE WRITTEN PERMISSION  
OF THRIVE HOMES PTY LTD-ACN 613 679 333


WINDOW HEAD HEIGHTS TO BE 2143H FROM FFL UNLESS  
STATED OTHERWISE.

CEILING HEIGHT NOMINAL TO FRAME HEIGHT, SUBJECT TO  
SELECTED FLOOR FINISH.


ARTICULATION JOINT REQUIRES ADDITIONAL STUD FOR  
BRICK TIES.

NYLON MESH FLYSCREENS TO ALL OPENING WINDOWS,  
SLIDING AND STACKER DOORS (EXCLUDING HINGED DOORS)

CSR WALL WRAP TO EXTERNAL WALLS

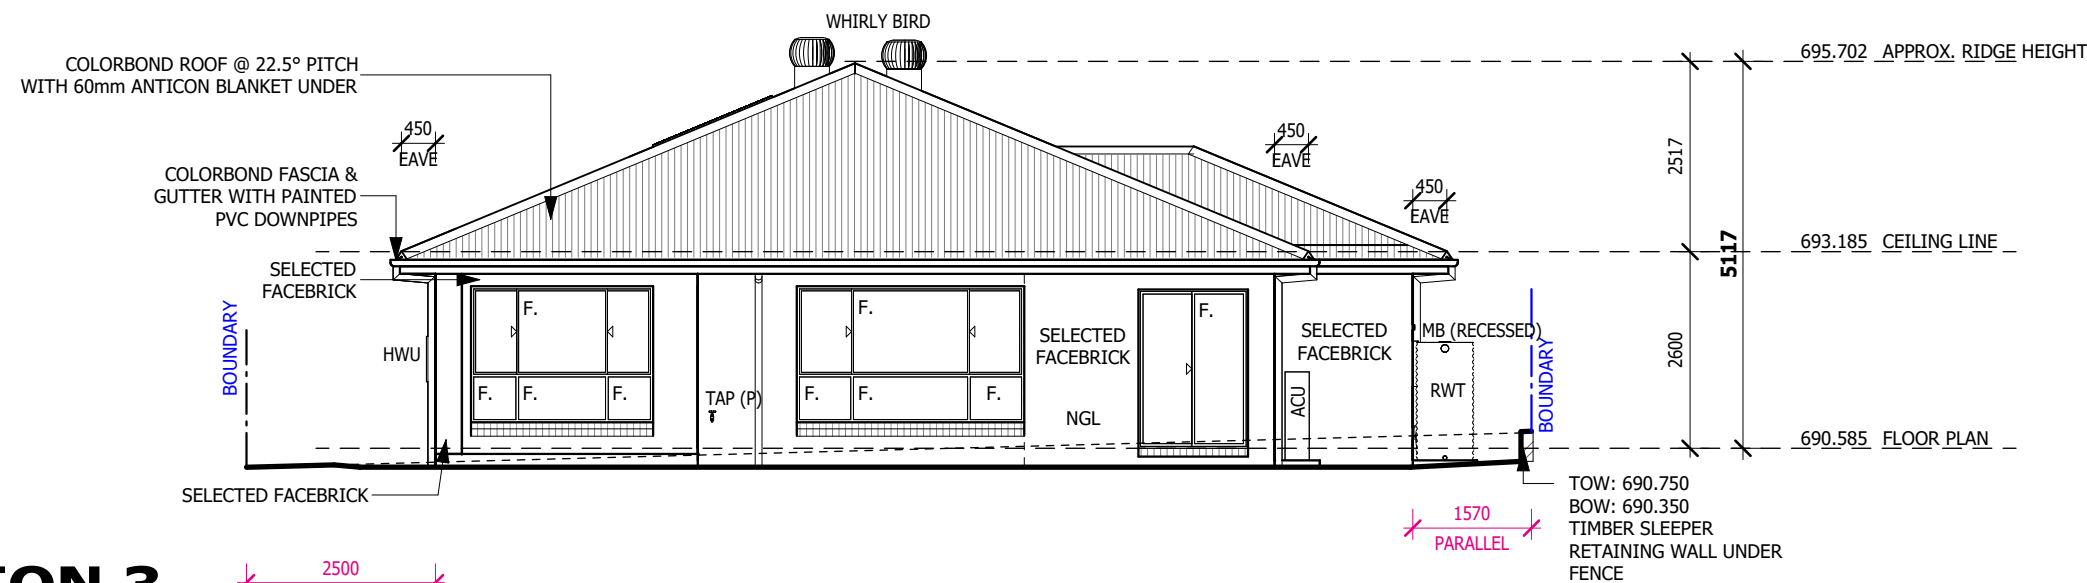

ELEVATION 3

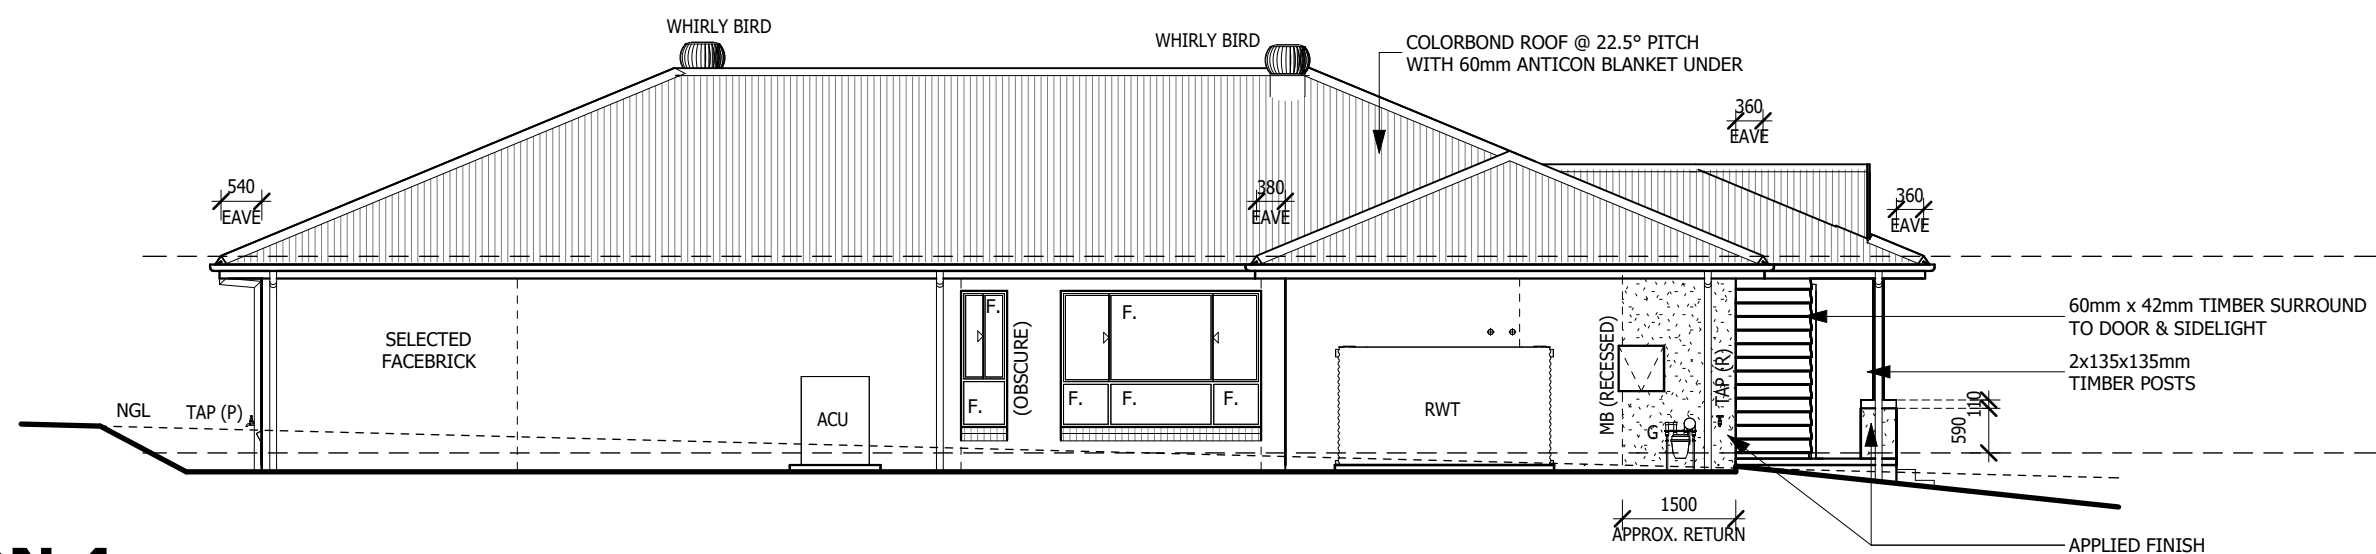

ELEVATION 4


|   |   |   |                         |                               |                      |                |
|---|---|---|-------------------------|-------------------------------|----------------------|----------------|
| NOTES:<br><br>PLEASE NOTE: DETAILS SHOWN ON THESE PLANS ARE INTENDED TO BE ACCURATE - HOWEVER INFORMATION WRITTEN INTO INDIVIDUAL CONTRACTS WILL TAKE PRECEDENCE OVER PLANS<br>* ALL DIMENSIONS ARE IN MILLIMETRES<br>* DO NOT SCALE - USE WRITTEN DIMENSIONS<br>* ALL DIMENSIONS ARE TO STRUCTURAL FRAMES ONLY EXCLUDING FINISHED SURFACES | <b>ThriveHomes</b><br>LEVEL 7, 5 RIDER BOULEVARD<br>RHODES NSW 2138<br>TELEPHONE 02 8758 4800<br>FAX 02 9300 5646<br><br>Builder's licence No. 301349C | CLIENT:<br>THRIVE HOMES                                                                            | HOUSE TYPE: ALLIRA 25   | DRAWN BY: DD                  | DATE DRAWN: 23.04.26 | SCALE: 1 : 100 |
|   |   | SITE ADDRESS:<br>LOT 186 (DP 1304135)<br>NO. 39 KEIGHTLEY AVENUE, WINDRADYNE<br>BATHURST, NSW 2795 | FACADE: COVE            | COUNCIL AREA: BATHURST        |                      | DRWG No: 06    |
|   |   |   | TYPE: DOUBLE GARAGE     | JOB No: T001734               |                      | ISSUE: E       |
|   |   |   | SPECIFICATION: STANDARD | DRAWING TITLE: ELEVATIONS 3-4 |                      |                |




**INSULATION NOTE:**

- R6.0 BULK INSULATION BATTS TO CEILING WITH R3.0 WHERE 6.0 WILL NOT FIT TO CEILINGS WITH ROOF OVER (EXCLUDING CEILINGS OVER GARAGE, PORCH & ALFRESCO)
- WALL WRAP TO EXTERNAL WALLS.
- R2.5 TO EXTERNAL WALLS OF HOUSE & R2.2 TO INTERNAL WALLS BETWEEN HOUSE & GARAGE (EXCLUDES EXTERNAL WALLS OF GARAGE)

**SECTION A-A**

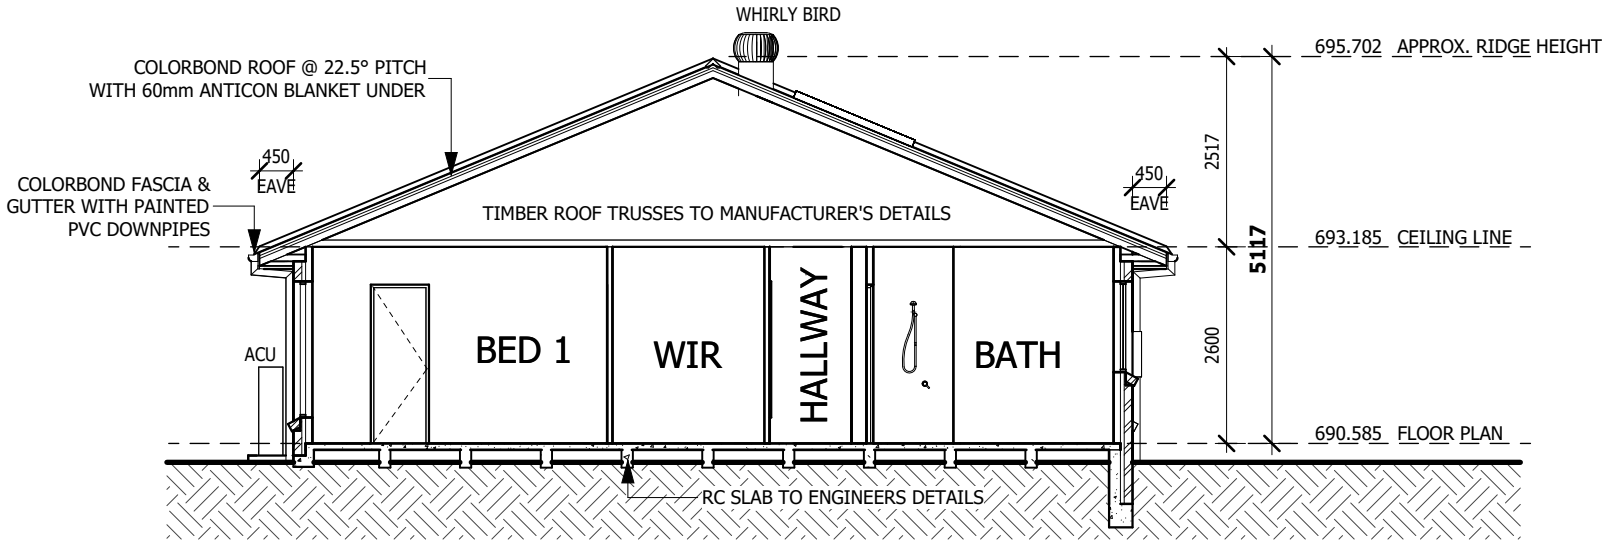

**SECTION B-B**

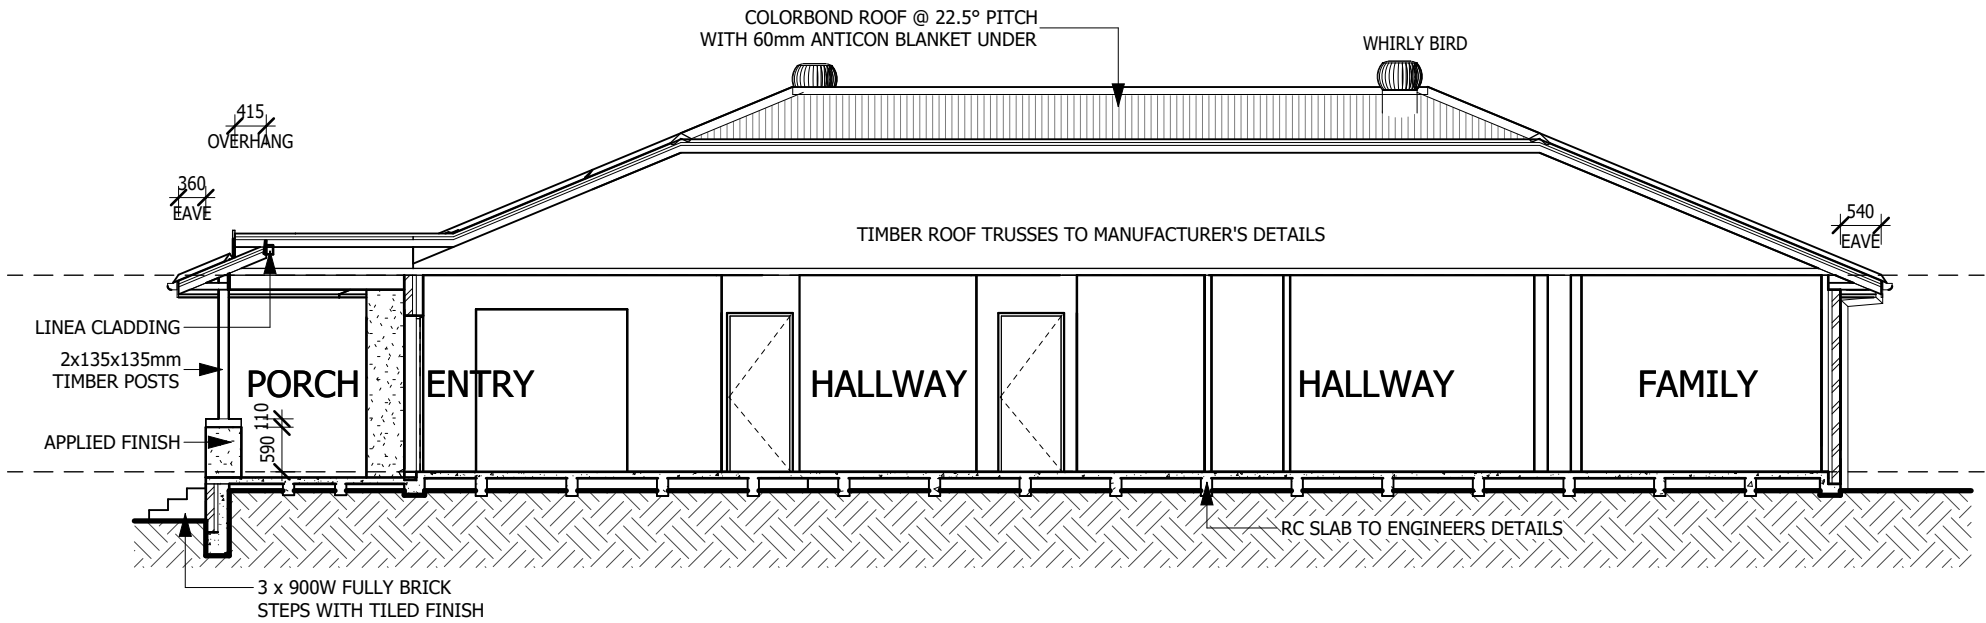

| BASIX COMMITMENTS                        |               |                       |                                                                                         |   |                                                                                         |
|------------------------------------------|---------------|-----------------------|-----------------------------------------------------------------------------------------|---|-----------------------------------------------------------------------------------------|
| PROJECT DETAILS                          |               |                       | STORMWATER                                                                              | ENERGY   | NATURAL LIGHTING                                                                        |
| Site area                                | 638           | m <sup>2</sup>        | Rainwater tank to collect at least 175.8 m <sup>2</sup> of rain run off from roof area  | <b>ACTIVE COOLING/HEATING 1-phase</b>   | Applicant must provide a window or skylight for natural lighting to 2 bathrooms/toilets |
| Roof area                                | 293.0         | m <sup>2</sup>        | Rainwater tank to be connected to all toilets with in the development                   | Cooling system with day/night zoning for bedrooms & living areas with an EER 3.0 STAR                                                                    |                                                                                         |
| Number of bedrooms                       | 4             |                       | Rainwater tank to be connected to cold water tap to supply water to the washing machine | Heating system with day/night zoning for bedrooms & living areas with an EER 3.5 STAR                                                                    |                                                                                         |
| Total area of vegetation (garden & lawn) | 367           | m <sup>2</sup>        | Rainwater to be connected to at least one outdoor tap for garden watering               |   | <b>COOKING (KITCHEN APPLIANCES)</b>                                                     |
| ABSA Certificate Number (if applicable)  | #HR-OZ68P2-03 |                       | Rainwater to have a capacity of at least 3000LTR                                        |   | Install a gas cooktop and electric oven                                                 |
| Net conditioned floor area               | 160.7         | m <sup>2</sup>        |                                                                                         | <b>VENTILATION</b>   |                                                                                         |
| Net Unconditioned floor area             | 11.7          | m <sup>2</sup>        | <b>WATER</b>                                                                            | At least 1 Bathroom: individual fan, ducted to façade or roof: manual switch on/off                                                                      | <b>DESIGN ENHANCEMENT</b>                                                               |
| Concession claimed (if applicable)       | N/A           |                       | All showers with in the development are to have a minimum rating of 4 star showerheads  | Kitchen: individual fan, ducted to façade or roof: manual switch on/off                                                                                  | Install a fixed outdoor clothes drying line                                             |
| Cooling load (if applicable)             | 8             | MJ/m <sup>2</sup> /pa | Each toilet is to have a flushing system of no less than a 4 star rating                | Laundry: natural ventilation only, or no laundry; Operation control: n/a                                                                                 |                                                                                         |
| Heating load (if applicable)             | 147           | MJ/m <sup>2</sup> /pa | All basin taps to have a minimum rating of 4 star rating                                | <b>ARTIFICIAL LIGHTING</b>   |                                                                                         |
|                                          |               |                       | All taps in the kitchen are to have a minimum rating of 4 star                          | The applicant must ensure that a minimum of 80% of light fixtures are fitted with fluorescent, compact fluorescent, or light-emitting-diode (LED) lamps. |                                                                                         |
|                                          |               |                       | <b>HOT WATER</b>                                                                        |   | <b>INSULATION</b>                                                                       |
|                                          |               |                       | Gas instantaneous hot water system with a performance of 6 stars                        |   | External wall [excluding garage]: R2.5                                                  |
|                                          |               |                       |                                                                                         |   | Ceiling [excluding garage & alfresco]: R6.0                                             |

NOTES:

PLEASE NOTE: DETAILS SHOWN ON THESE PLANS ARE INTENDED TO BE ACCURATE - HOWEVER INFORMATION WRITTEN INTO INDIVIDUAL CONTRACTS WILL TAKE PRECEDENCE OVER PLANS

- \* ALL DIMENSIONS ARE IN MILLIMETRES
- \* DO NOT SCALE - USE WRITTEN DIMENSIONS
- \* ALL DIMENSIONS ARE TO STRUCTURAL FRAMES ONLY EXCLUDING FINISHED SURFACES

**ThriveHomes**  
LEVEL 7, 5 RIDER BOULEVARD  
RHODES NSW 2138  
TELEPHONE 02 8758 4800  
FAX 02 9300 5646  
  
Builder's licence No. 301349C

CLIENT:  
THRIVE HOMES

SITE ADDRESS:  
LOT 186 (DP 1304135)  
NO. 39 KEIGHTLEY AVENUE, WINDRADYNE  
BATHURST, NSW 2795

HOUSE TYPE: ALLIRA 25  
FACADE: COVE  
TYPE: DOUBLE GARAGE  
SPECIFICATION: STANDARD

DRAWING TITLE:  
SECTIONS & BASIX

DRAWN BY:  
DD

DATE DRAWN:  
23.04.26

SCALE:  
1 : 100

COUNCIL AREA:  
BATHURST

DRWG No:  
07

JOB No:  
T001734

ISSUE:  
E

## LAUNDRY / WC


- PROVIDE SKIRTING TILE TO PERIMETER WALLS OF LAUNDRY & WC
- LAUNDRY SPLASH BACK - FOUR TILE HEIGHT OVER LAUNDRY TUB
- WM TAPS UNDER TUB

## BATHROOM / ENSUITE

- PROVIDE FULL HIGH TILES TO MAIN BATHROOM BEDROOM 1 ENSUITE (EXCLUDING SEPARATE WC)
- SEMI-FRAMELESS SHOWER SCREEN WITH PIVOT DOOR @ 2000 HIGH.
- APPROXIMATELY 900mm HIGH DIRECT FIX MIRROR TO WIDTH OF VANITY
- WALL MOUNTED TAPS & SPOUT TO BATH
- BASIN MOUNTED TAPS TO VANITIES.
- 20mm C'STONE BENCHTOP TO VANITIES.
- FLOOR MOUNTED VANITIES WITH KICK BOARD

### LEGEND:

70mm STEPDOWN TO WET AREAS

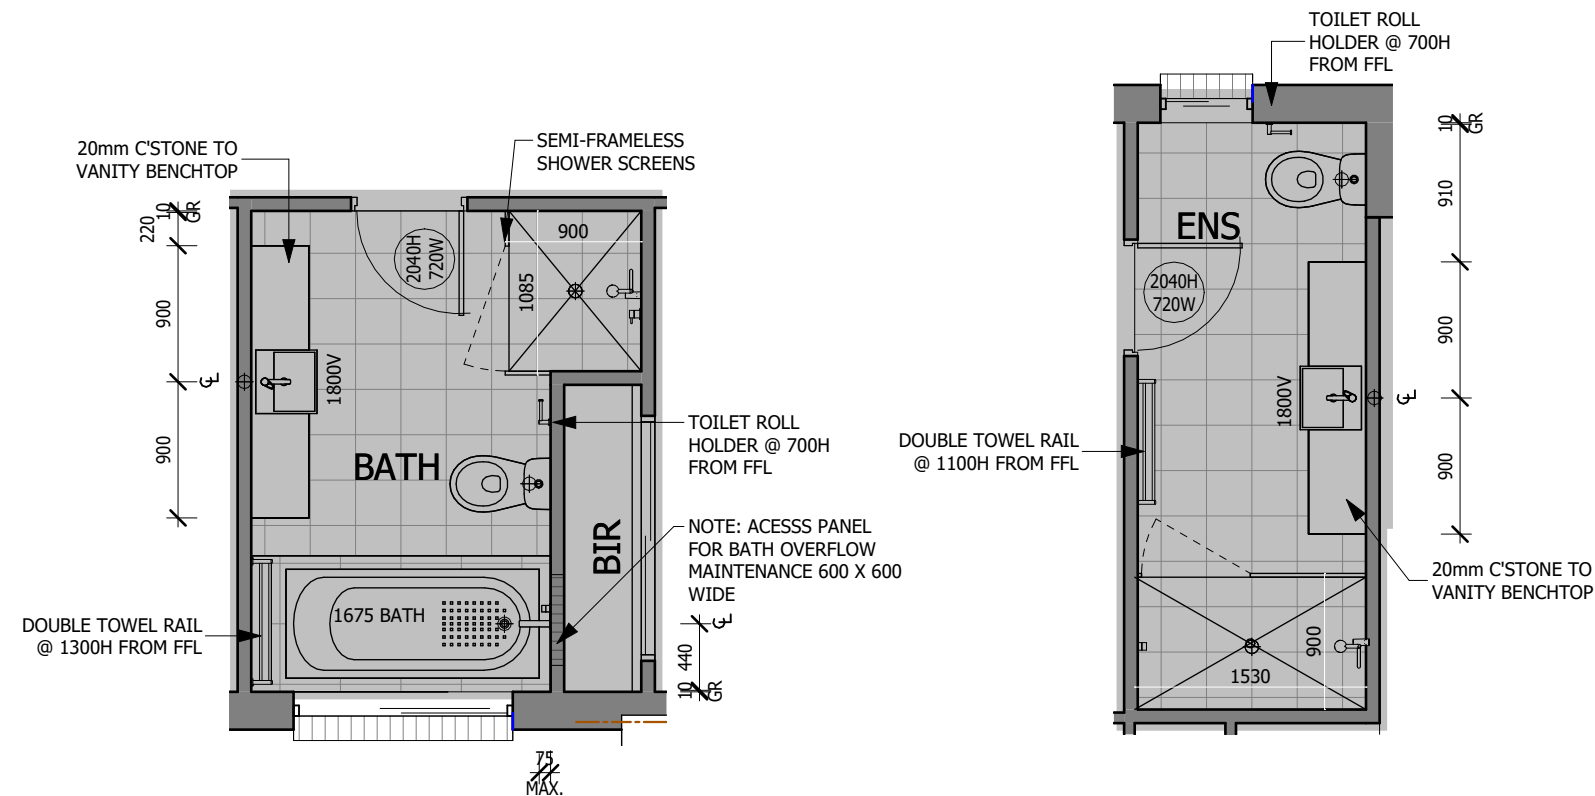

MAIN BATH

BED 1 ENSUITE

L'DRY

### NOTES:

PLEASE NOTE: DETAILS SHOWN ON THESE PLANS ARE INTENDED TO BE ACCURATE - HOWEVER INFORMATION WRITTEN INTO INDIVIDUAL CONTRACTS WILL TAKE PRECEDENCE OVER PLANS

- \* ALL DIMENSIONS ARE IN MILLIMETRES
- \* DO NOT SCALE - USE WRITTEN DIMENSIONS
- \* ALL DIMENSIONS ARE TO STRUCTURAL FRAMES ONLY EXCLUDING FINISHED SURFACES

**ThriveHomes**  
LEVEL 7, 5 RIDER BOULEVARD  
RHODES NSW 2138  
TELEPHONE 02 8758 4800  
FAX 02 9300 5646  
Builder's licence No. 301349C

CLIENT:  
THRIVE HOMES

SITE ADDRESS:  
LOT 186 (DP 1304135)  
NO. 39 KEIGHTLEY AVENUE, WINDRADYNE  
BATHURST, NSW 2795

HOUSE TYPE: ALLIRA 25  
FACADE: COVE  
TYPE: DOUBLE GARAGE  
SPECIFICATION: STANDARD

DRAWING TITLE:  
WET AREA PLANS

DRAWN BY:  
DD

DATE DRAWN:  
23.04.26

SCALE:  
1 : 50

COUNCIL AREA:  
BATHURST

DRWG No:  
08

JOB No:  
T001734


ISSUE:  
E



**LEGEND:**

70mm STEPDOWN TO WET AREAS

NOTE: SLAB EDGE TO BE RENDERED  
TO MATCH FINISH ABOVE

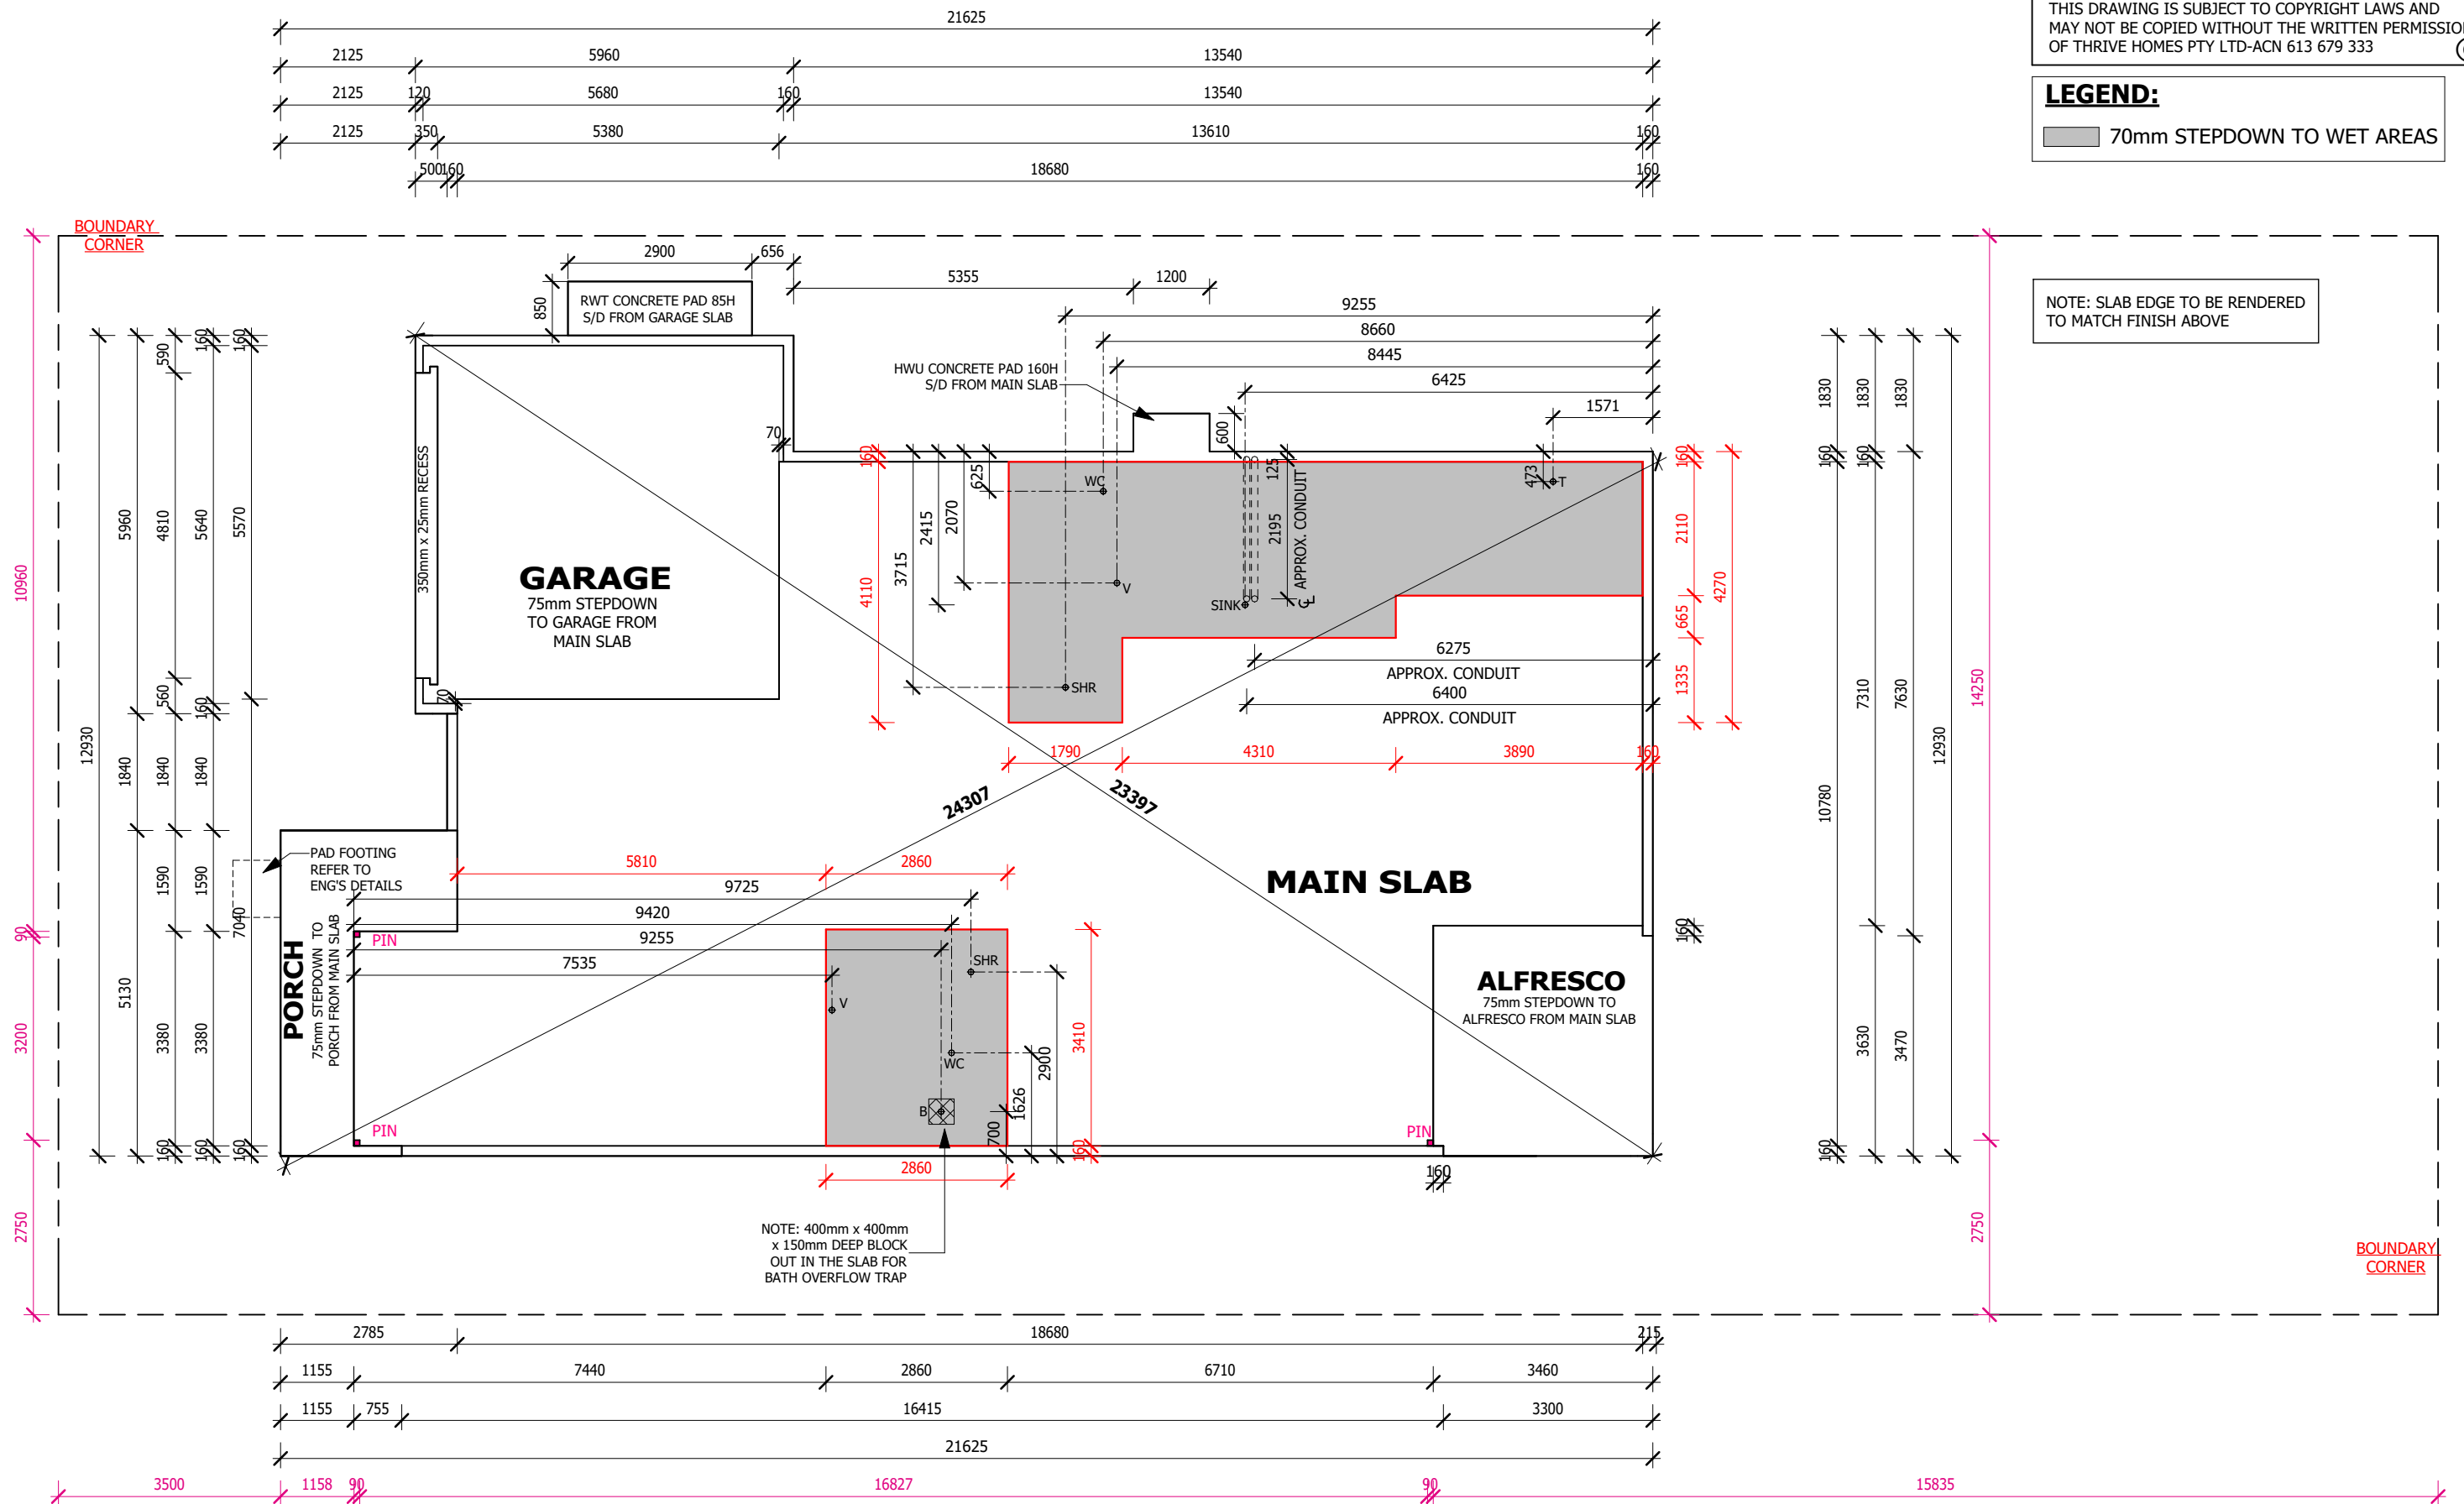

**NOTES:**

PLEASE NOTE: DETAILS SHOWN ON THESE PLANS ARE INTENDED  
TO BE ACCURATE - HOWEVER INFORMATION WRITTEN INTO  
INDIVIDUAL CONTRACTS WILL TAKE PRECEDENCE OVER PLANS  
\* ALL DIMENSIONS ARE IN MILLIMETRES  
\* DO NOT SCALE - USE WRITTEN DIMENSIONS  
\* ALL DIMENSIONS ARE TO STRUCTURAL FRAMES ONLY  
EXCLUDING FINISHED SURFACES

**ThriveHomes**  
LEVEL 7, 5 RIDER BOULEVARD  
RHODES NSW 2138  
TELEPHONE 02 8758 4800  
FAX 02 9300 5646  
Builder's licence No. 301349C

CLIENT:  
**THRIVE HOMES**

SITE ADDRESS:  
LOT 186 (DP 1304135)  
NO. 39 KEIGHTLEY AVENUE, WINDRADYNE  
BATHURST, NSW 2795

HOUSE TYPE: ALLIRA 25  
FACADE: COVE  
TYPE: DOUBLE GARAGE  
SPECIFICATION: STANDARD

DRAWING TITLE:  
**SLAB SETOUT PLAN**

DRAWN BY:  
DD

DATE DRAWN:  
23.04.26

SCALE:  
1 : 100

COUNCIL AREA:  
**BATHURST**


DRWG No:  
**09**

JOB No:  
**T001734**

ISSUE:  
**E**




KEIGHTLEY AVENUE

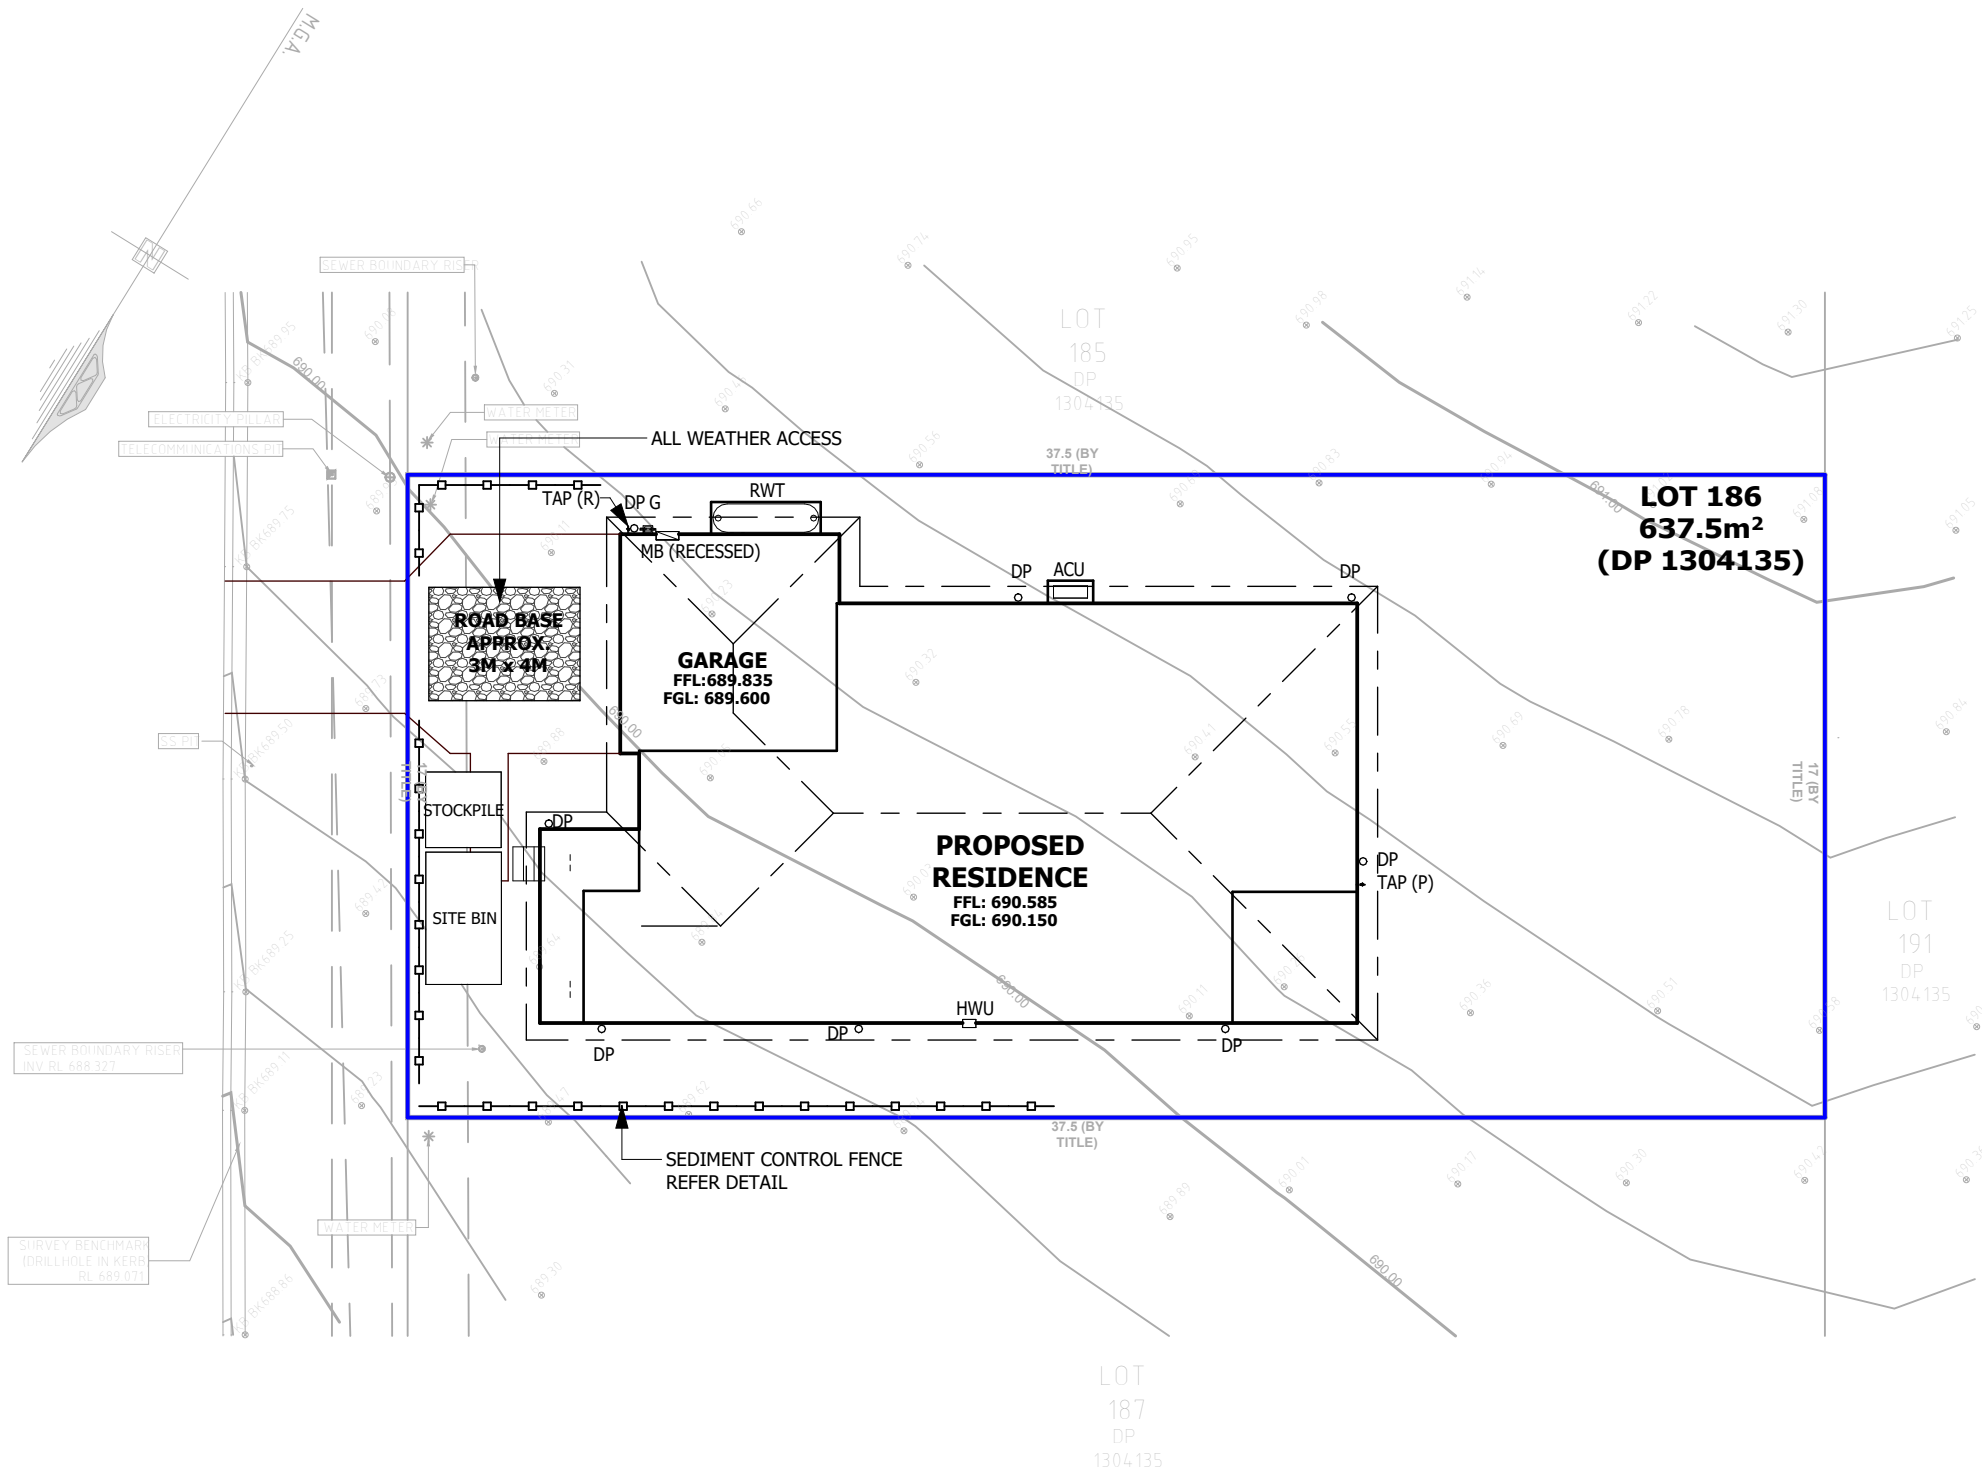

**SEDIMENT CONTROL**

INSTALL SEDIMENT CONTROL STRUCTURES IN LOCATIONS INDICATED ON THIS DRAWING AND AS OTHERWISE REQUIRED TO CONTROL SEDIMENT DURING ALL EXCAVATIONS AND WHILST AREAS OF THE SITE ARE EXPOSED TO EROSION. REVIEW CONTROL MEASURES AND MAINTAIN STRUCTURES DURING CONSTRUCTION.

IF ADDITIONAL MEASURES ARE REQUIRED FOR EROSION AND CONTROL OR BY COUNCIL REQUIREMENTS, REFER TO "URBAN EROSION AND SEDIMENT CONTROL" GUIDELINES PREPARED BY THE DEPARTMENT OF CONSERVATION AND LAND MANAGEMENT.

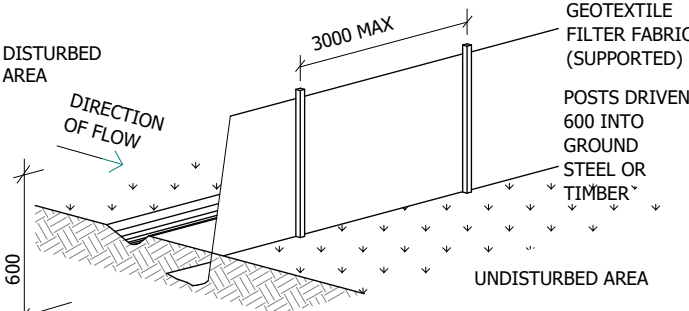

**SEDIMENT FENCE DETAIL**

SUITABLE FOR DRAINAGE AREA OF 0.6HA MAX AND  
SLOPE GRADIENT OF 1:2 MAX WITH LENGTH OF 60M MAX



The Essential First Step

**NOTES:**

PLEASE NOTE: DETAILS SHOWN ON THESE PLANS ARE INTENDED TO BE ACCURATE - HOWEVER INFORMATION WRITTEN INTO INDIVIDUAL CONTRACTS WILL TAKE PRECEDENCE OVER PLANS

- \* ALL DIMENSIONS ARE IN MILLIMETRES
- \* DO NOT SCALE - USE WRITTEN DIMENSIONS
- \* ALL DIMENSIONS ARE TO STRUCTURAL FRAMES ONLY EXCLUDING FINISHED SURFACES

**ThriveHomes**  
LEVEL 7, 5 RIDER BOULEVARD  
RHODES NSW 2138  
TELEPHONE 02 8758 4800  
FAX 02 9300 5646  
Builder's licence No. 301349C

CLIENT:  
THRIVE HOMES

SITE ADDRESS:  
LOT 186 (DP 1304135)  
NO. 39 KEIGHTLEY AVENUE, WINDRADYNE  
BATHURST, NSW 2795

HOUSE TYPE: ALLIRA 25  
FACADE: COVE  
TYPE: DOUBLE GARAGE  
SPECIFICATION: STANDARD

DRAWING TITLE:  
SEDIMENT CONTROL PLAN

DRAWN BY:  
DD

DATE DRAWN:  
23.04.26

SCALE:  
1 : 200


COUNCIL AREA:  
BATHURST

DRWG No:  
10

JOB No:  
T001734

ISSUE:  
E

# KEIGHTLEY AVENUE

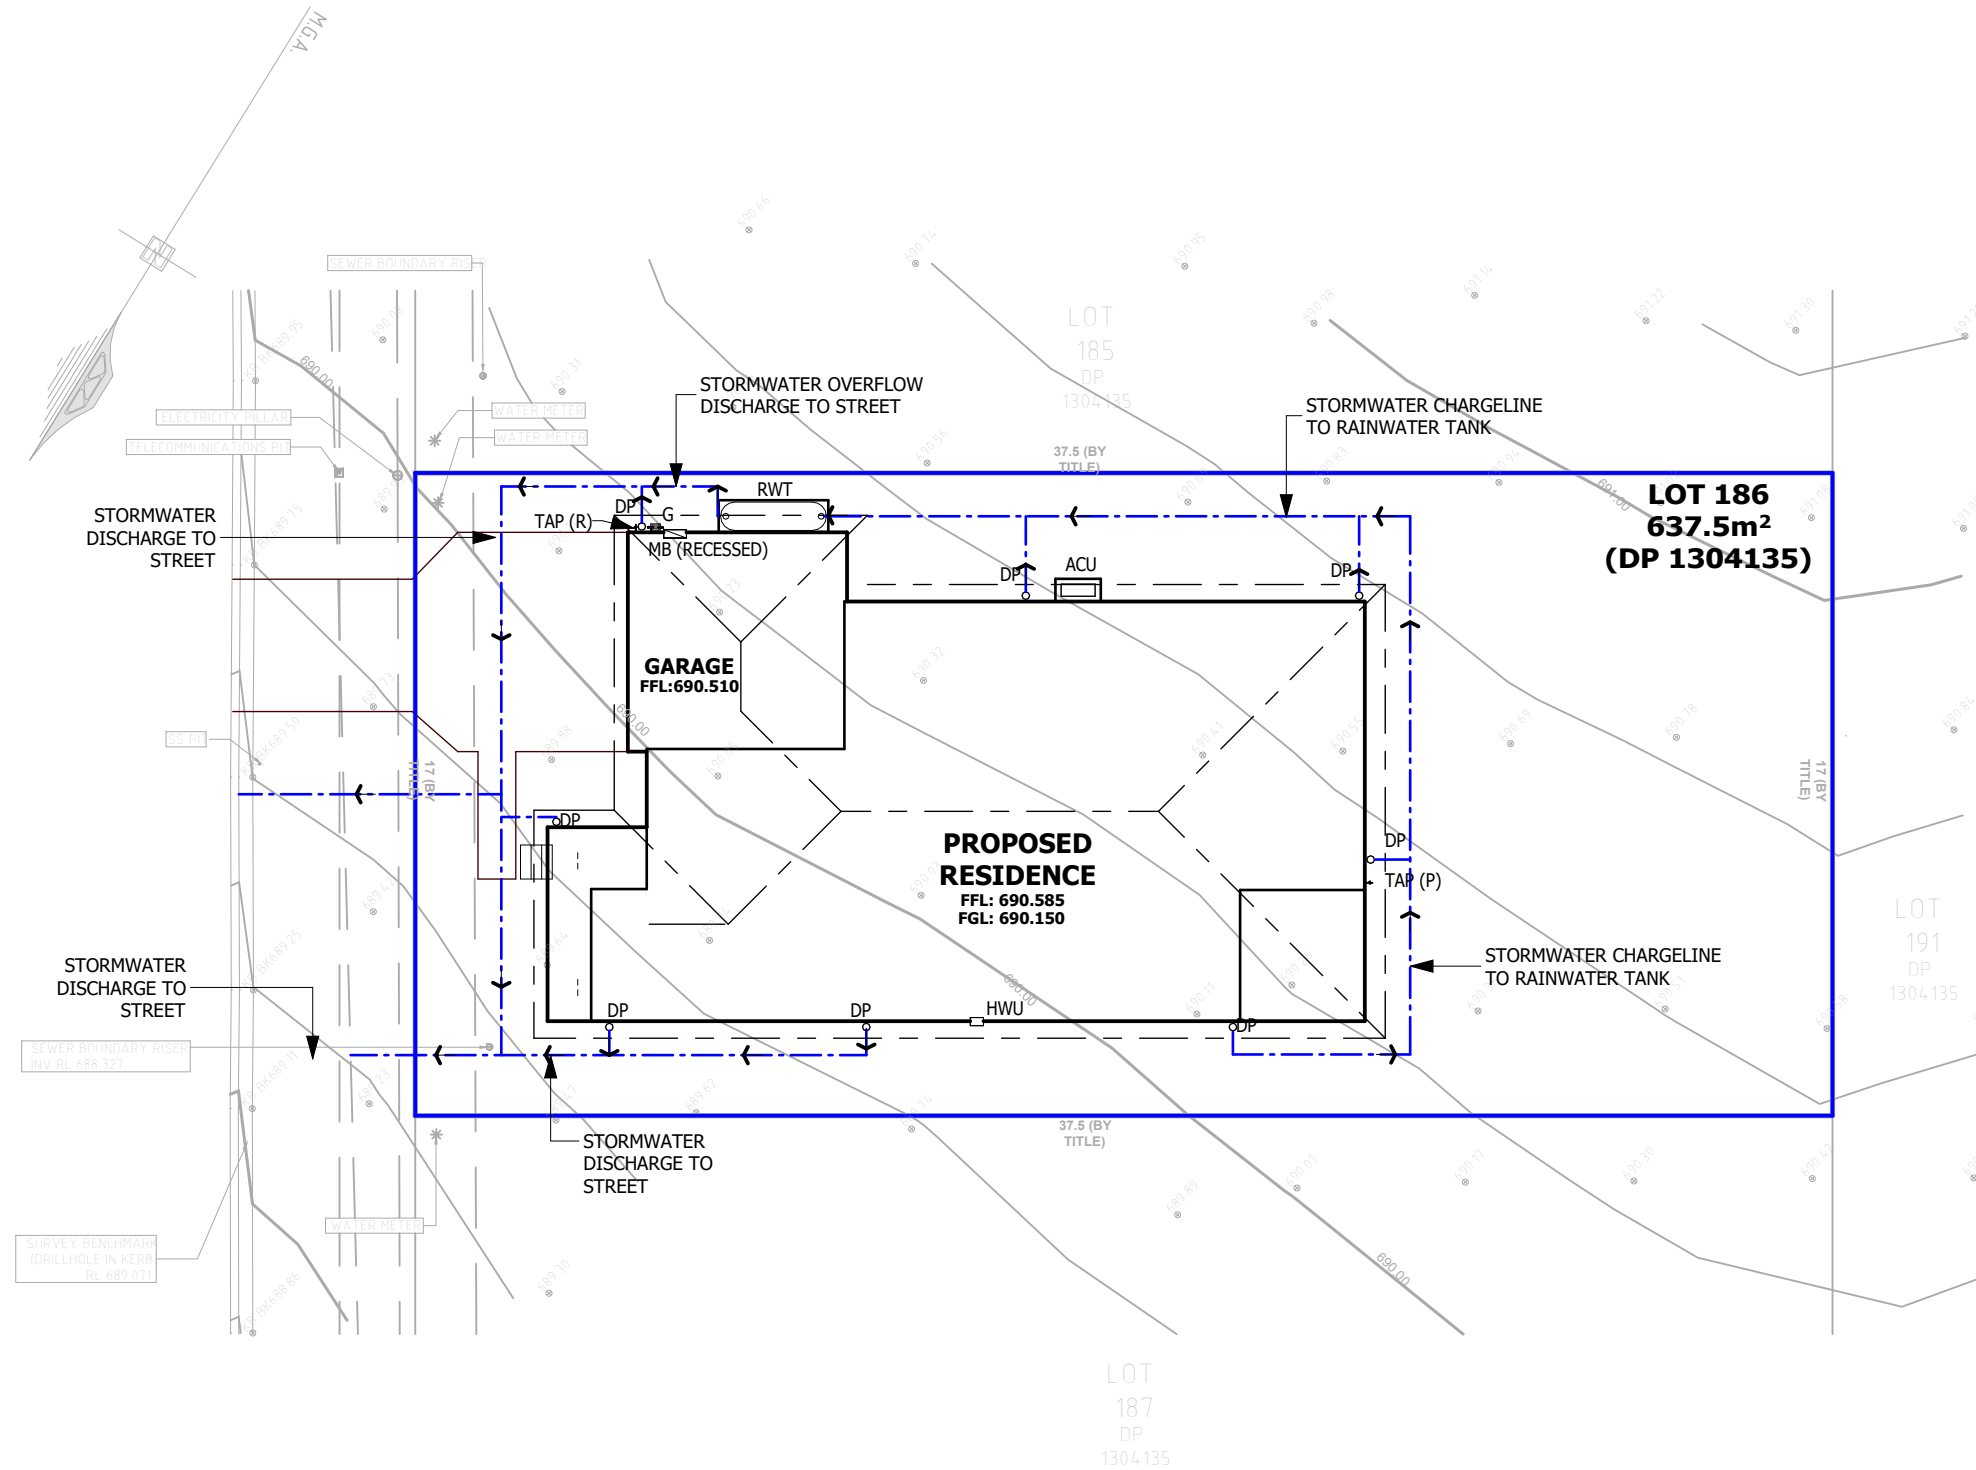

## NOTES:

PLEASE NOTE: DETAILS SHOWN ON THESE PLANS ARE INTENDED TO BE ACCURATE - HOWEVER INFORMATION WRITTEN INTO INDIVIDUAL CONTRACTS WILL TAKE PRECEDENCE OVER PLANS

- \* ALL DIMENSIONS ARE IN MILLIMETRES
- \* DO NOT SCALE - USE WRITTEN DIMENSIONS
- \* ALL DIMENSIONS ARE TO STRUCTURAL FRAMES ONLY EXCLUDING FINISHED SURFACES


**ThriveHomes**  
LEVEL 7, 5 RIDER BOULEVARD  
RHODES NSW 2138  
TELEPHONE 02 8758 4800  
FAX 02 9300 5646  
Builder's licence No. 301349C

CLIENT:  
THRIVE HOMES


SITE ADDRESS:  
LOT 186 (DP 1304135)  
NO. 39 KEIGHTLEY AVENUE, WINDRADYNE  
BATHURST, NSW 2795

HOUSE TYPE: ALLIRA 25  
FACADE: COVE  
TYPE: DOUBLE GARAGE  
SPECIFICATION: STANDARD  
DRAWING TITLE:  
STORMWATER PLAN


|                           |                         |                   |
|---------------------------|-------------------------|-------------------|
| DRAWN BY:<br>DD           | DATE DRAWN:<br>23.04.26 | SCALE:<br>1 : 200 |
| COUNCIL AREA:<br>BATHURST |                         | DRWG No:<br>11    |
| JOB No:<br>T001734        |                         | ISSUE:<br>E       |

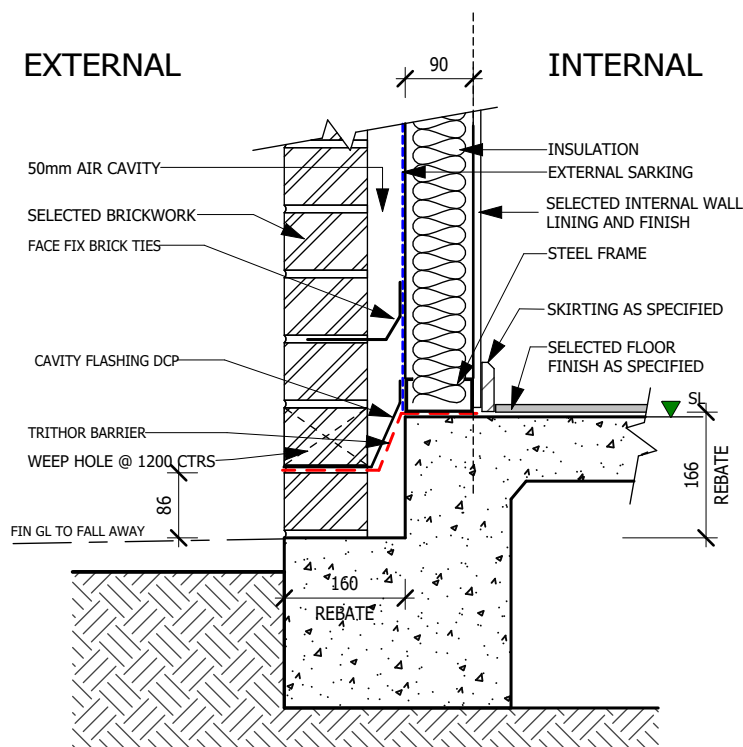


**1** BRICK VENEER REBATE DETAIL  
SCALE: 1 : 10

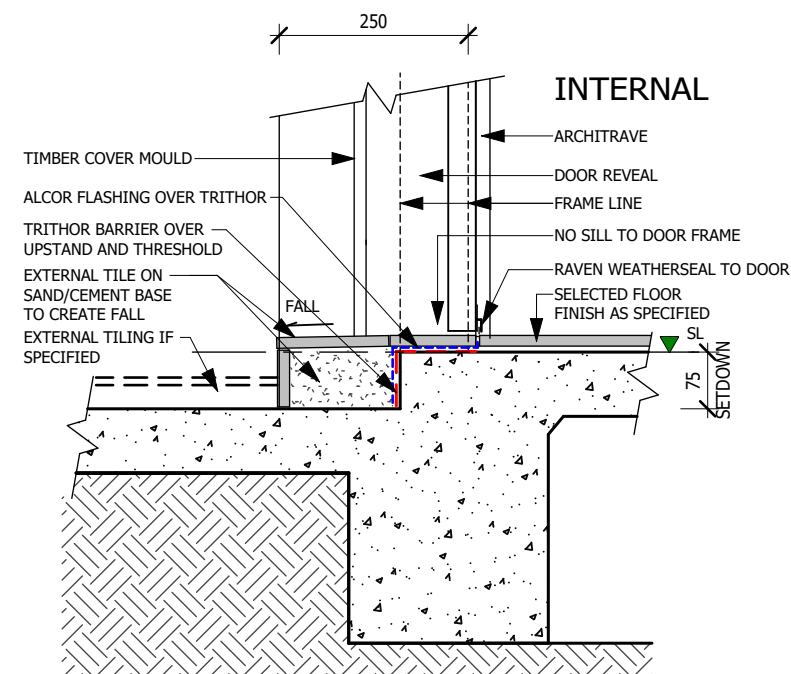

**2** BRICK VENEER PORCH ENTRY DOOR  
SCALE: 1 : 10

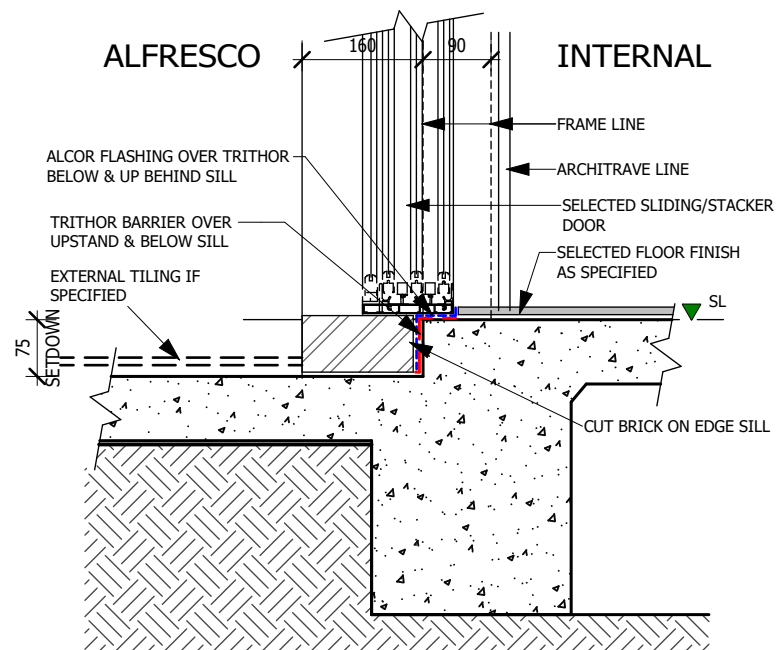

**3** ALFRESCO DOOR - BRICK VENEER  
SCALE: 1 : 10

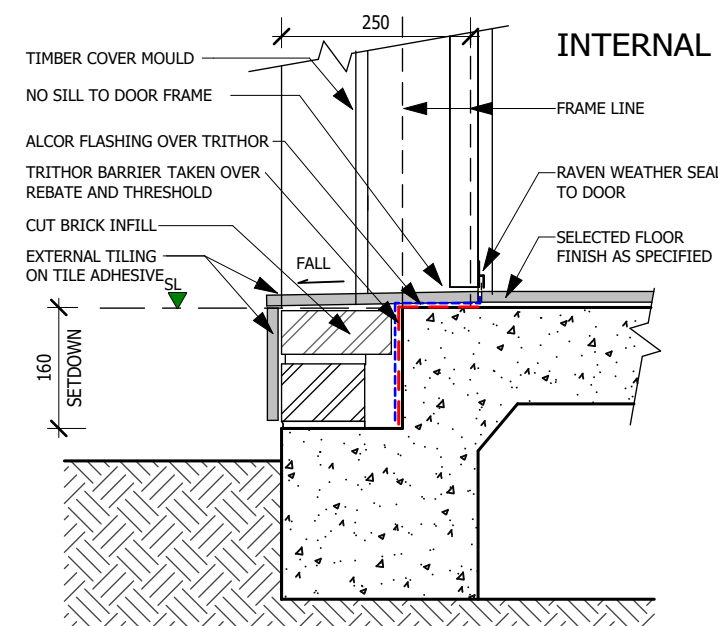

**4** LAUNDRY TIMBER DOOR  
SCALE: 1 : 10

**NOTE:** DETAILS ARE APPLICABLE TO ALL ARCHITECTURAL CONDITIONS NOT SPECIFICALLY DETAILED OR REFERENCED ON ARCHITECTURAL DRAWINGS.

**NOTES:**

PLEASE NOTE: DETAILS SHOWN ON THESE PLANS ARE INTENDED TO BE ACCURATE - HOWEVER INFORMATION WRITTEN INTO INDIVIDUAL CONTRACTS WILL TAKE PRECEDENCE OVER PLANS  
\* ALL DIMENSIONS ARE IN MILLIMETRES  
\* DO NOT SCALE - USE WRITTEN DIMENSIONS  
\* ALL DIMENSIONS ARE TO STRUCTURAL FRAMES ONLY EXCLUDING FINISHED SURFACES

**ThriveHomes**

LEVEL 7, 5 RIDER BOULEVARD,  
RHODES NSW 2138,  
TELEPHONE 02 8758 4800,  
FAX 02 9300 5646

Builder's licence No. 301349C


CLIENT:  
**THRIVE HOMES**

SITE ADDRESS:  
LOT 186 (DP 1304135)  
NO. 39 KEIGHTLEY AVENUE,  
WINDRADYNE  
BATHURST, NSW 2795


HOUSE TYPE: ALLIRA 25  
FACADE: COVE  
TYPE: DOUBLE GARAGE  
SPECIFICATION: STANDARD  
DRAWING TITLE:  
SLAB DETAILS 1

|               |             |        |
|---------------|-------------|--------|
| DRAWN BY:     | DATE DRAWN: | SCALE: |
| DH            | 14.04.26    | 1 : 10 |
| COUNCIL AREA: | DRWG No:    |        |
| BATHURST      | D01         |        |
| JOB No:       | ISSUE:      |        |
| T001734       | E           |        |




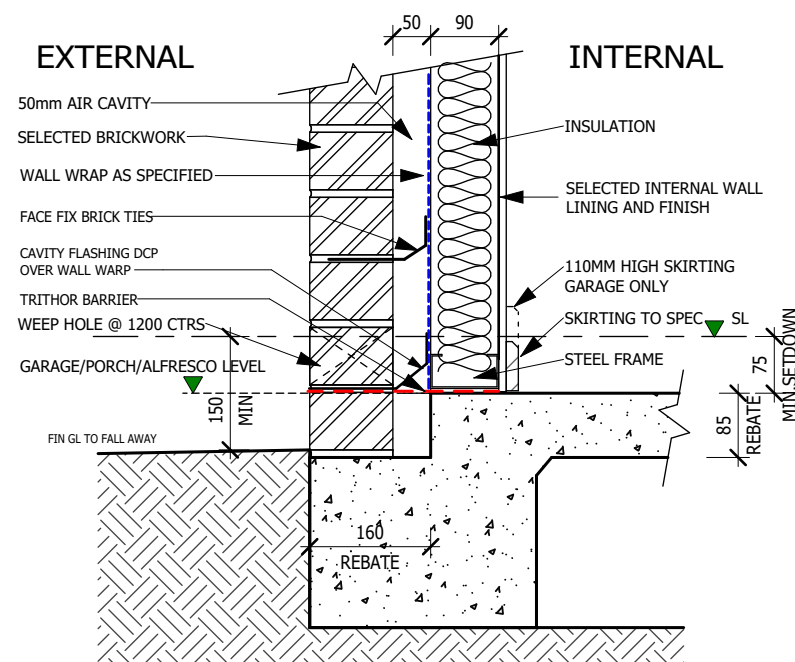


**1** GARAGE REBATE (SIDE) & PORCH/ALFRESCO  
SCALE: 1 : 10

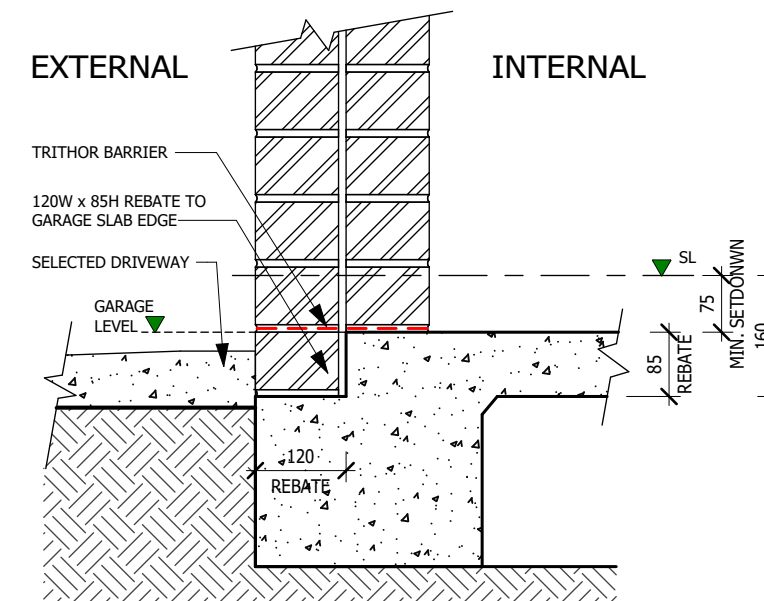

**2** GARAGE REBATE (FRONT SIDE OF DOOR)  
SCALE: 1 : 10

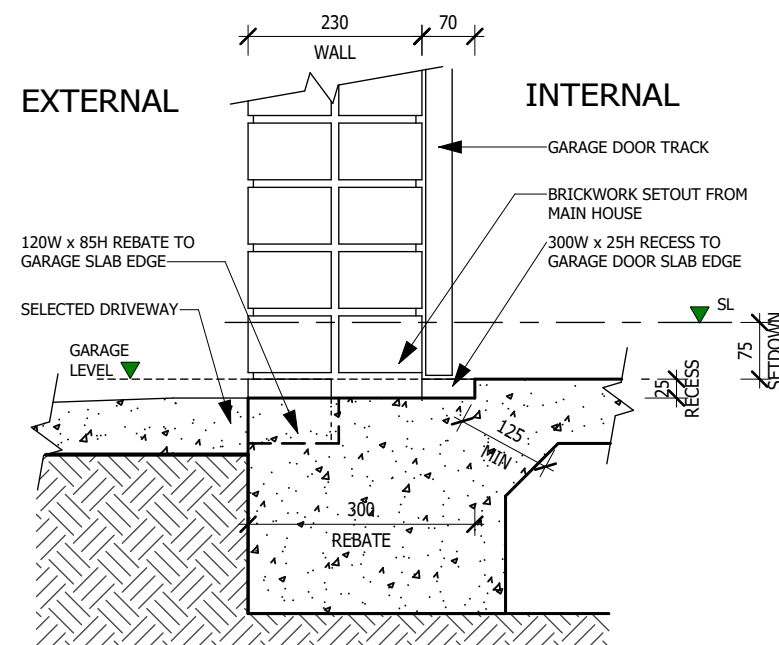

**3** GARAGE RECESS (FRONT THROUGH RECESS)  
SCALE: 1 : 10

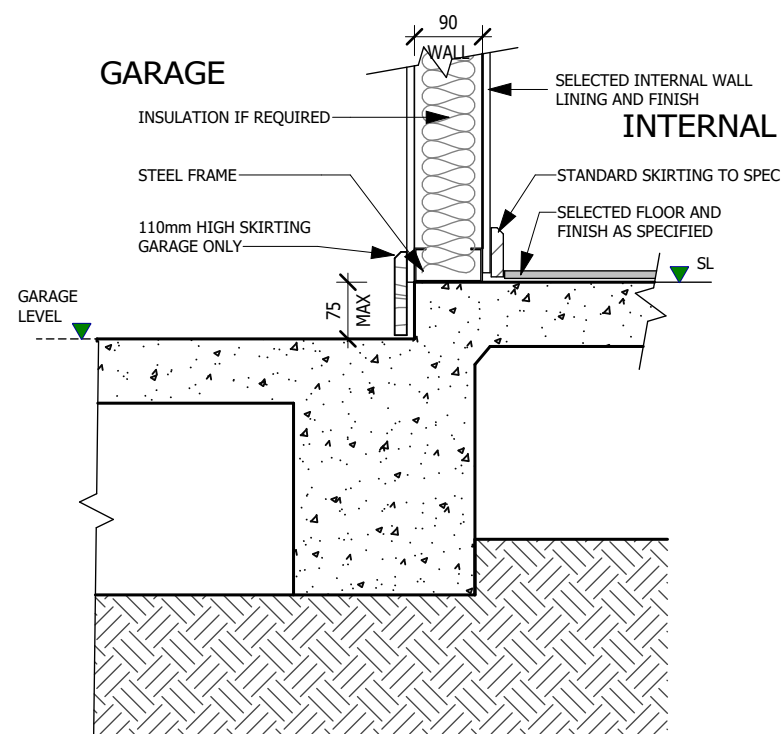

**4** INTERNA GARAGE STEP - 75MM STEP ONLY1  
SCALE: 1 : 10

NOTES:

PLEASE NOTE: DETAILS SHOWN ON THESE PLANS ARE INTENDED TO BE ACCURATE - HOWEVER INFORMATION WRITTEN INTO INDIVIDUAL CONTRACTS WILL TAKE PRECEDENCE OVER PLANS  
\* ALL DIMENSIONS ARE IN MILLIMETRES  
\* DO NOT SCALE - USE WRITTEN DIMENSIONS  
\* ALL DIMENSIONS ARE TO STRUCTURAL FRAMES ONLY EXCLUDING FINISHED SURFACES

**ThriveHomes**

LEVEL 7, 5 RIDER BOULEVARD,  
RHODES NSW 2138,  
TELEPHONE 02 8758 4800,  
FAX 02 9300 5646


Builder's licence No. 301349C

CLIENT:  
THRIVE HOMES


SITE ADDRESS:  
LOT 186 (DP 1304135)  
NO. 39 KEIGHTLEY AVENUE,  
WINDRADYNE  
BATHURST, NSW 2795

HOUSE TYPE: ALLIRA 25  
FACADE: COVE  
TYPE: DOUBLE GARAGE  
SPECIFICATION: STANDARD  
DRAWING TITLE:  
SLAB DETAILS 2


|                           |                         |                  |
|---------------------------|-------------------------|------------------|
| DRAWN BY:<br>DH           | DATE DRAWN:<br>14.04.26 | SCALE:<br>1 : 10 |
| COUNCIL AREA:<br>BATHURST |                         | DRWG No:<br>D02  |
| JOB No:<br>T001734        |                         | ISSUE:<br>E      |

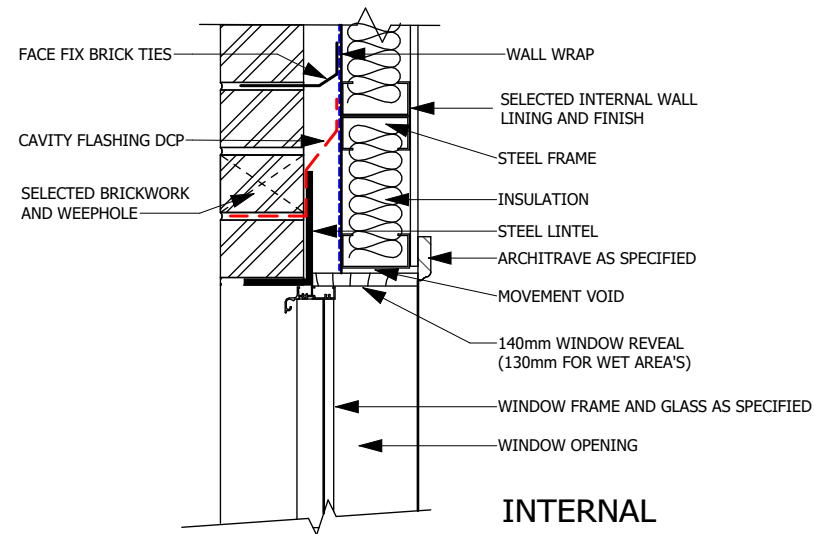


**1** WINDOW HEAD - BRICK VENEER  
SCALE: 1 : 10

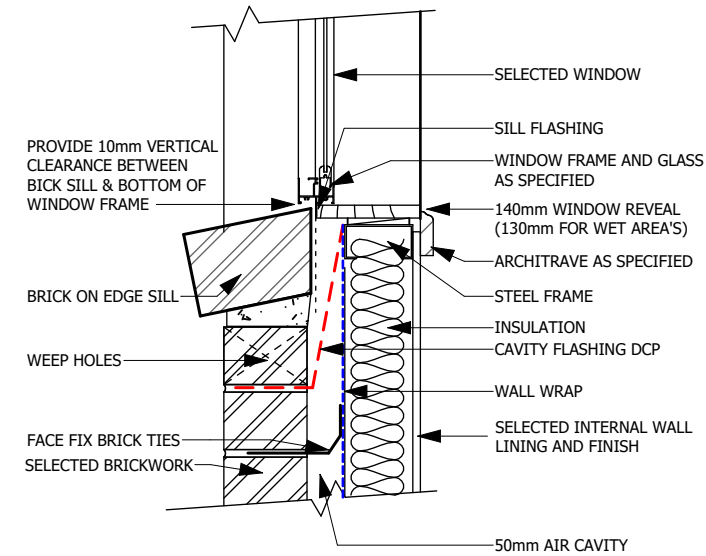

**2** WINDOW SILL - BRICK VENEER  
SCALE: 1 : 10

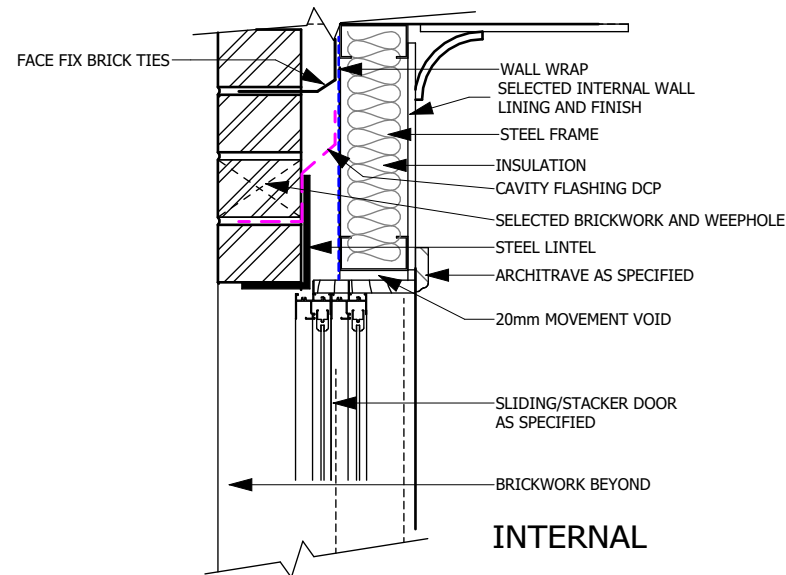

**3** SLIDING DOOR HEAD - BV2  
SCALE: 1 : 10

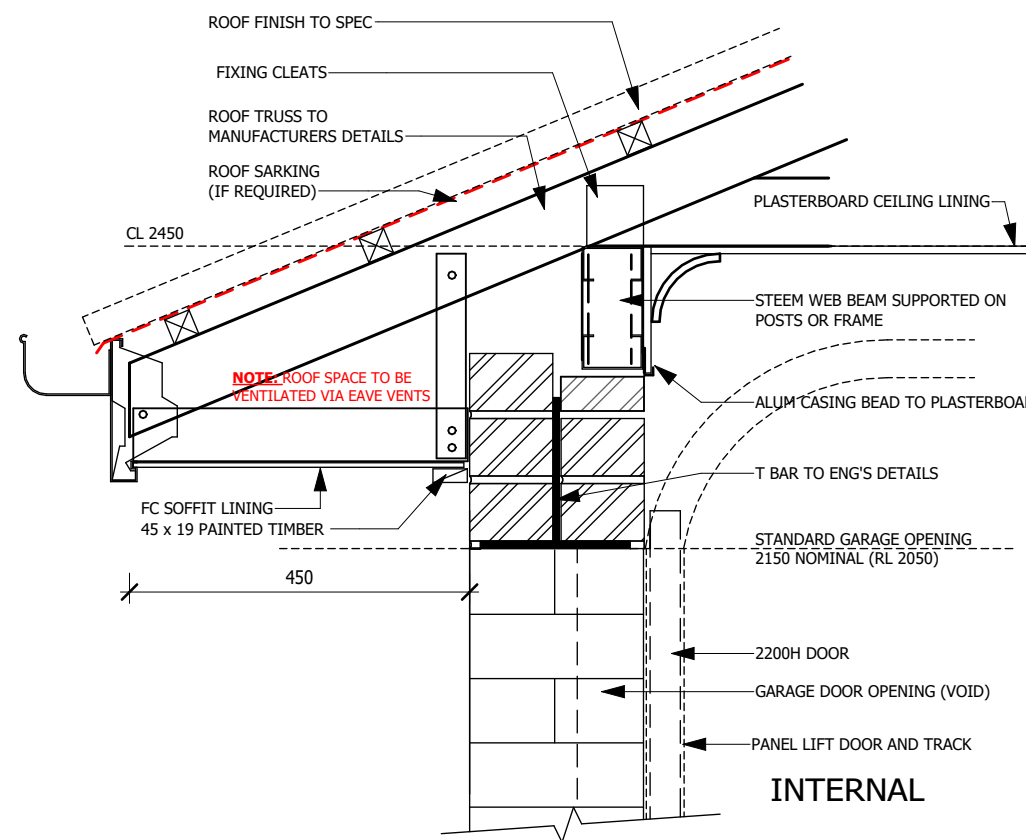

**4** GARAGE DOOR HEAD DETAIL EAVES ABOVE  
SCALE: 1 : 10

NOTES:

PLEASE NOTE: DETAILS SHOWN ON THESE PLANS ARE INTENDED TO BE ACCURATE - HOWEVER INFORMATION WRITTEN INTO INDIVIDUAL CONTRACTS WILL TAKE PRECEDENCE OVER PLANS  
\* ALL DIMENSIONS ARE IN MILLIMETRES  
\* DO NOT SCALE - USE WRITTEN DIMENSIONS  
\* ALL DIMENSIONS ARE TO STRUCTURAL FRAMES ONLY EXCLUDING FINISHED SURFACES

**ThriveHomes**

LEVEL 7, 5 RIDER BOULEVARD,  
RHODES NSW 2138,  
TELEPHONE 02 8758 4800,  
FAX 02 9300 5646



Builder's licence No. 301349C

CLIENT:  
**THRIVE HOMES**

SITE ADDRESS:  
LOT 186 (DP 1304135)  
NO. 39 KEIGHTLEY AVENUE,  
WINDRADYNE  
BATHURST, NSW 2795

HOUSE TYPE: ALLIRA 25  
FACADE: COVE  
TYPE: DOUBLE GARAGE  
SPECIFICATION: STANDARD  
DRAWING TITLE:  
WALL OPENINGS DETAILS

|                           |                         |                  |
|---------------------------|-------------------------|------------------|
| DRAWN BY:<br>DH           | DATE DRAWN:<br>14.04.26 | SCALE:<br>1 : 10 |
| COUNCIL AREA:<br>BATHURST |                         | DRWG No:<br>D03  |
| JOB No:<br>T001734        |                         | ISSUE:<br>E      |

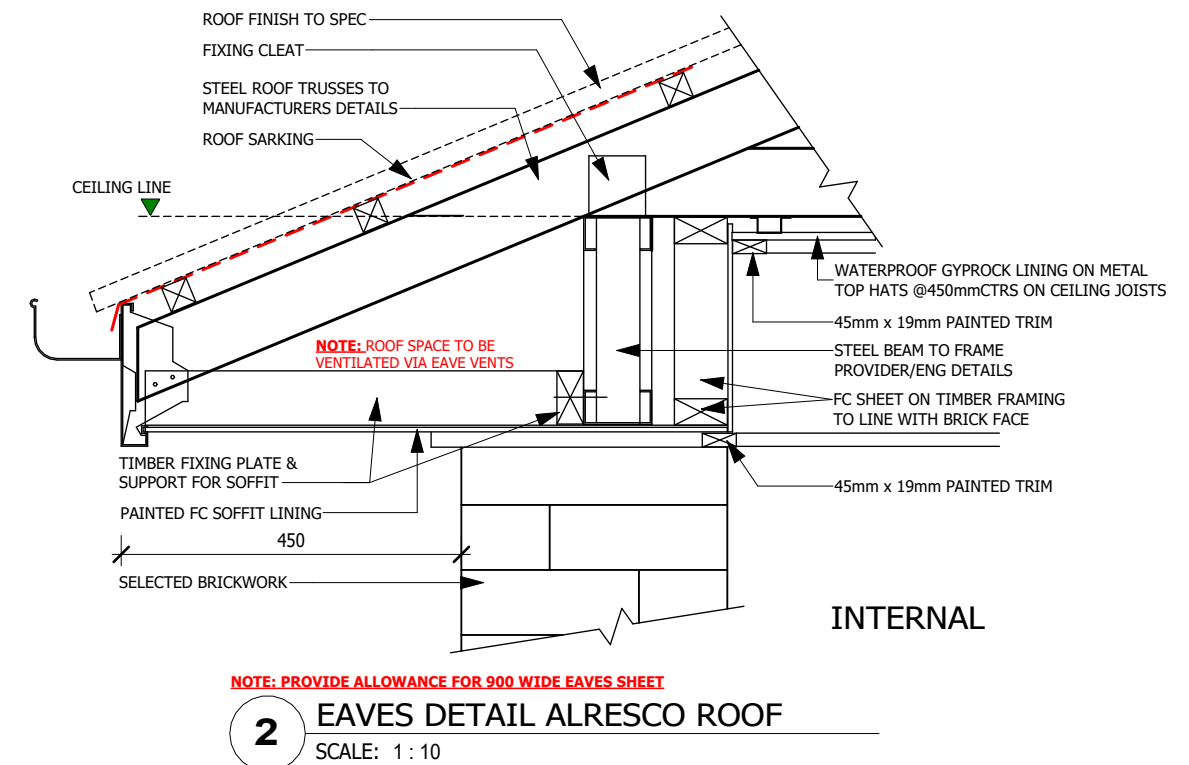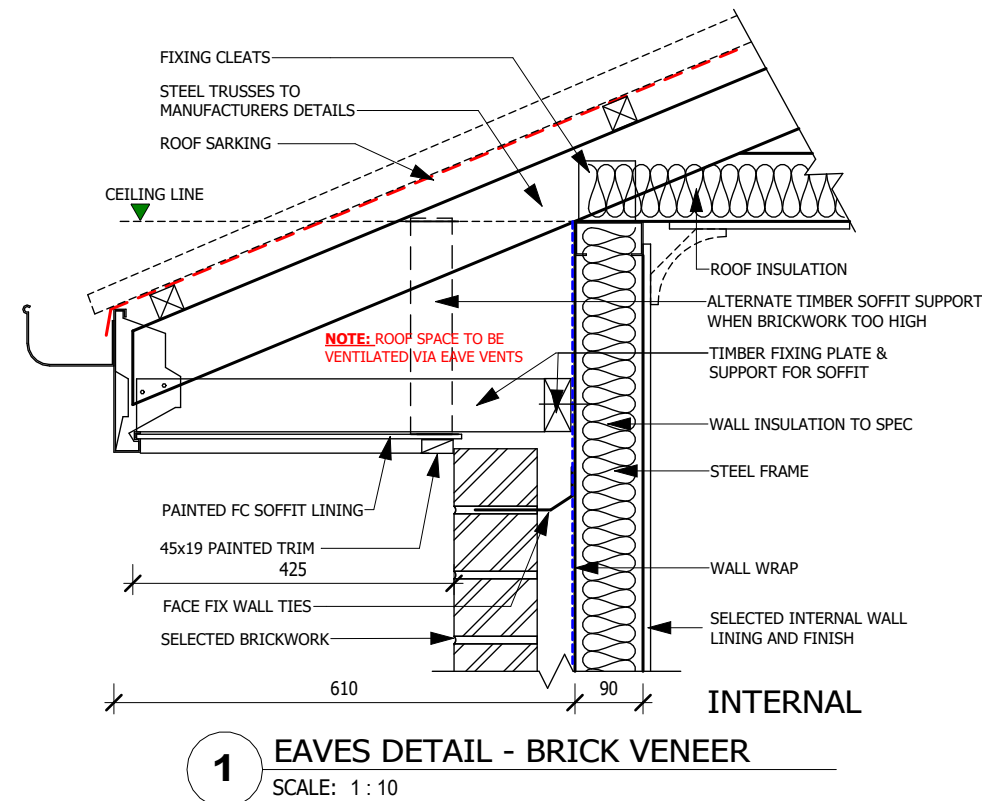

NOTES:

PLEASE NOTE: DETAILS SHOWN ON THESE PLANS ARE INTENDED TO BE ACCURATE - HOWEVER INFORMATION WRITTEN INTO INDIVIDUAL CONTRACTS WILL TAKE PRECEDENCE OVER PLANS

- \* ALL DIMENSIONS ARE IN MILLIMETRES
- \* DO NOT SCALE - USE WRITTEN DIMENSIONS
- \* ALL DIMENSIONS ARE TO STRUCTURAL FRAMES ONLY EXCLUDING FINISHED SURFACES

**ThriveHomes**

LEVEL 7, 5 RIDER BOULEVARD,  
RHODES NSW 2138,  
TELEPHONE 02 8758 4800,  
FAX 02 9300 5646

Builder's licence No. 301349C

CLIENT:  
**THRIVE HOMES**

SITE ADDRESS:  
LOT 186 (DP 1304135)  
NO. 39 KEIGHTLEY AVENUE,  
WINDRADYNE  
BATHURST, NSW 2795

HOUSE TYPE: ALLIRA 25  
FACADE: COVE  
TYPE: DOUBLE GARAGE  
SPECIFICATION: STANDARD  
DRAWING TITLE:  
TYPICAL EAVES DETAILS

|                           |                         |                  |
|---------------------------|-------------------------|------------------|
| DRAWN BY:<br>DH           | DATE DRAWN:<br>14.04.26 | SCALE:<br>1 : 10 |
| COUNCIL AREA:<br>BATHURST |                         | DRWG No:<br>D04  |
| JOB No:<br>T001734        |                         | ISSUE:<br>E      |