

THIS DRAWING IS SUBJECT TO COPYRIGHT LAWS AND MAY NOT BE COPIED WITHOUT THE WRITTEN PERMISSION OF THRIVE HOMES PTY LTD-ACN 613 679 333

NOTES:

* ALL DIMENSIONS ARE IN MILLIMETERS

* DO NOT SCALE THE DRAWING - USE WRITTEN DIMENSIONS

* IT IS THE RESPONSIBILITY OF THE OWNER TO ENSURE THAT THE LAYOUT AND ALL SPECIAL INCLUSIONS ARE CORRECT

* THRIVE HOMES PTY. LIMITED WILL TAKE NO RESPONSIBILITY FOR ANY VERBAL DISCUSSIONS OR INSTRUCTIONS. ALL CHANGES AND SPECIAL INCLUSIONS MUST BE DOCUMENTED IN WRITING.

* THIS DRAWING IS SUBJECT TO COPYRIGHT LAWS AND MAY NOT BE COPIED WITHOUT THE WRITTEN PERMISSION OF THRIVE HOMES PTY. LIMITED - ACN 613 679 333

SCHEDULE OF DRAWINGS:	
SHEET	CONTENTS
01	COVER SHEET
02	SITE PLAN
03	FLOOR PLAN
04	ROOF PLAN
05	ELEVATION 1-2
06	ELEVATION 3-4
07	SECTIONS & BASIX
08	WET AREA PLANS
09	SLAB SETOUT PLAN
10	SEDIMENT CONTROL PLAN
11	STORMWATER PLAN
D1	SLAB DETAILS 1
D2	SLAB DETAILS 2
D3	WALL OPENINGS DETAILS
D4	TYPICAL EAVES DETAILS
D5	WET AREA DETAILS

AMENDMENTS			
ISS	DESCRIPTION	BY	DATE
A	LODGEMENT PLANS	PG (BM)	30.10.25
B	AMENDED LODGEMENT PLANS (HYBRID FRAME CONSTRUCTION WITH PODS)	PG (BM)	06.03.26
C	AMENDED LODGEMENT PLANS (BAYTIMBER MARKUPS)	PG (BM)	30.03.26
D	CONSTRUCTION PLANS	BM	13.05.26

CONSTRUCTION PLANS - CDC







SIGNATURE: _____

ThriveHomes

HYBRID FRAME CONSTRUCTION WITH PODS

NOTES: PLEASE NOTE: DETAILS SHOWN ON THESE PLANS ARE INTENDED TO BE ACCURATE - HOWEVER INFORMATION WRITTEN INTO INDIVIDUAL CONTRACTS WILL TAKE PRECEDENCE OVER PLANS * ALL DIMENSIONS ARE IN MILLIMETRES * DO NOT SCALE - USE WRITTEN DIMENSIONS * ALL DIMENSIONS ARE TO STRUCTURAL FRAMES ONLY EXCLUDING FINISHED SURFACES	ThriveHomes LEVEL 7, 5 RIDER BOULEVARD RHODES NSW 2138 TELEPHONE 02 8758 4800 FAX 02 9300 5646 Builder's licence No. 301349C	CLIENT: THRIVE HOMES	HOUSE TYPE: HELIX 24 FACADE: HUNTLEE	DRAWN BY: HN	DATE DRAWN: 13.05.26	SCALE:
		SITE ADDRESS: LOT 187 (DP 1304135) No. 41 KEIGHTLEY AVENUE, WINDRADYNE BATHURST, NSW 2795	TYPE: DOUBLE GARAGE SPECIFICATION: EVOQUE	COUNCIL AREA: BATHURST		DRWG No: 01
		DRAWING TITLE: COVER SHEET	JOB No: T001735		ISSUE: D	

LEGEND

      -  HOT WATER TANK
-  WATER NETTER
-  TELECOM PIT
-  MANHOLE (SEWER/STORMWATER)
-  SEWER TERMINAL MAINTENANCE SHAFT
-  SEWER MAINTENANCE SHAFT
-  VEHICLE CROSSING
-  KERB INLET PIT
-  LIGHT POLE
-  ELECTRICITY POLE
-  ELECTRICITY PILLAR
-  HYDRANT
-  STOP VALVE
-  KERB OUTLET
-  SERVICE CONDUIT
-  TREE (DIA/HEIGHT)
-  GARDEN BED
-  SHRUB
-  DENOTES TELEPHONE BOOTH

GARAGE INTERNAL DIMENSION
5500mm (W) x 5500mm (D)

****B.A.S****
(BUILDING ADJACENT TO SEWER)
ORDER SEWER PEGOUT

CDC TREE PLANTING REQUIREMENT:
A) CLIENT TO PLANT TREE TO FRONT YARD THAT
WILL REACH A HEIGHT OF 5M AT MATURITY
B) CLIENT TO PLANT TREE TO REAR YARD THAT
WILL REAR A HEIGHT OF 8M AT MATURITY

THIS DRAWING IS SUBJECT TO COPYRIGHT LAWS AND
MAY NOT BE COPIED WITHOUT THE WRITTEN PERMISSION
OF THRIVE HOMES PTY LTD-ACN 613 679 333


SITE NOTES:

- BEFORE STARTING WORK ON SITE CHECK FOLLOWING:
- SERVICE LOCATIONS
 - SEWER CONNECTION POSITION
 - DRIVEWAY ALIGNMENT & LEVELS
- *N2 WIND CATEGORY***
DPO INDICATES DOWNPIPE LOCATION

SITE CALCULATIONS CDC (EXCLUDING EXTERNAL WALLS & VOIDS)		
GROUND FLOOR	166.72	m ²
GARAGE AREA	30.25	m ²
TOTAL GROSS FLOOR AREA (EXCLUDING GARAGE CONCESSION)	178.97	m ²
SITE AREA	637.50	m ²
BUILDING FOOTPRINT (INCLUDING UNENCLOSED AREA)	238.07	m ²
DRIVEWAY & PATH	33.74	m ²
CROSSOVER	15.02	m ²
TOTAL FRONT AREA	80.03	m ²
FRONT LANDSCAPE AREA	57.84	%
TOTAL LANDSCAPE AREA	365.69	m ²
LANDSCAPE AREA (%)	57.36	%

SEPP 2017 REQUIREMENTS INLAND CDC		
SITE AREA	637.50	m ²
MAXIMUM GROSS FLOOR AREA	335.00	m ²
MINIMUM LANDSCAPED AREA	191.25	m ²
- GROSS FLOOR AREA MEANS THE SUM OF THE FLOOR AREA OF EACH FLOOR OF A BUILDING MEASURED FROM THE INTERNAL FACE OF EXTERNAL WALLS		
- LANDSCAPED AREA MUST HAVE A MINIMUM WIDTH AND LENGTH OF 1.5M		

KEIGHTLEY AVENUE

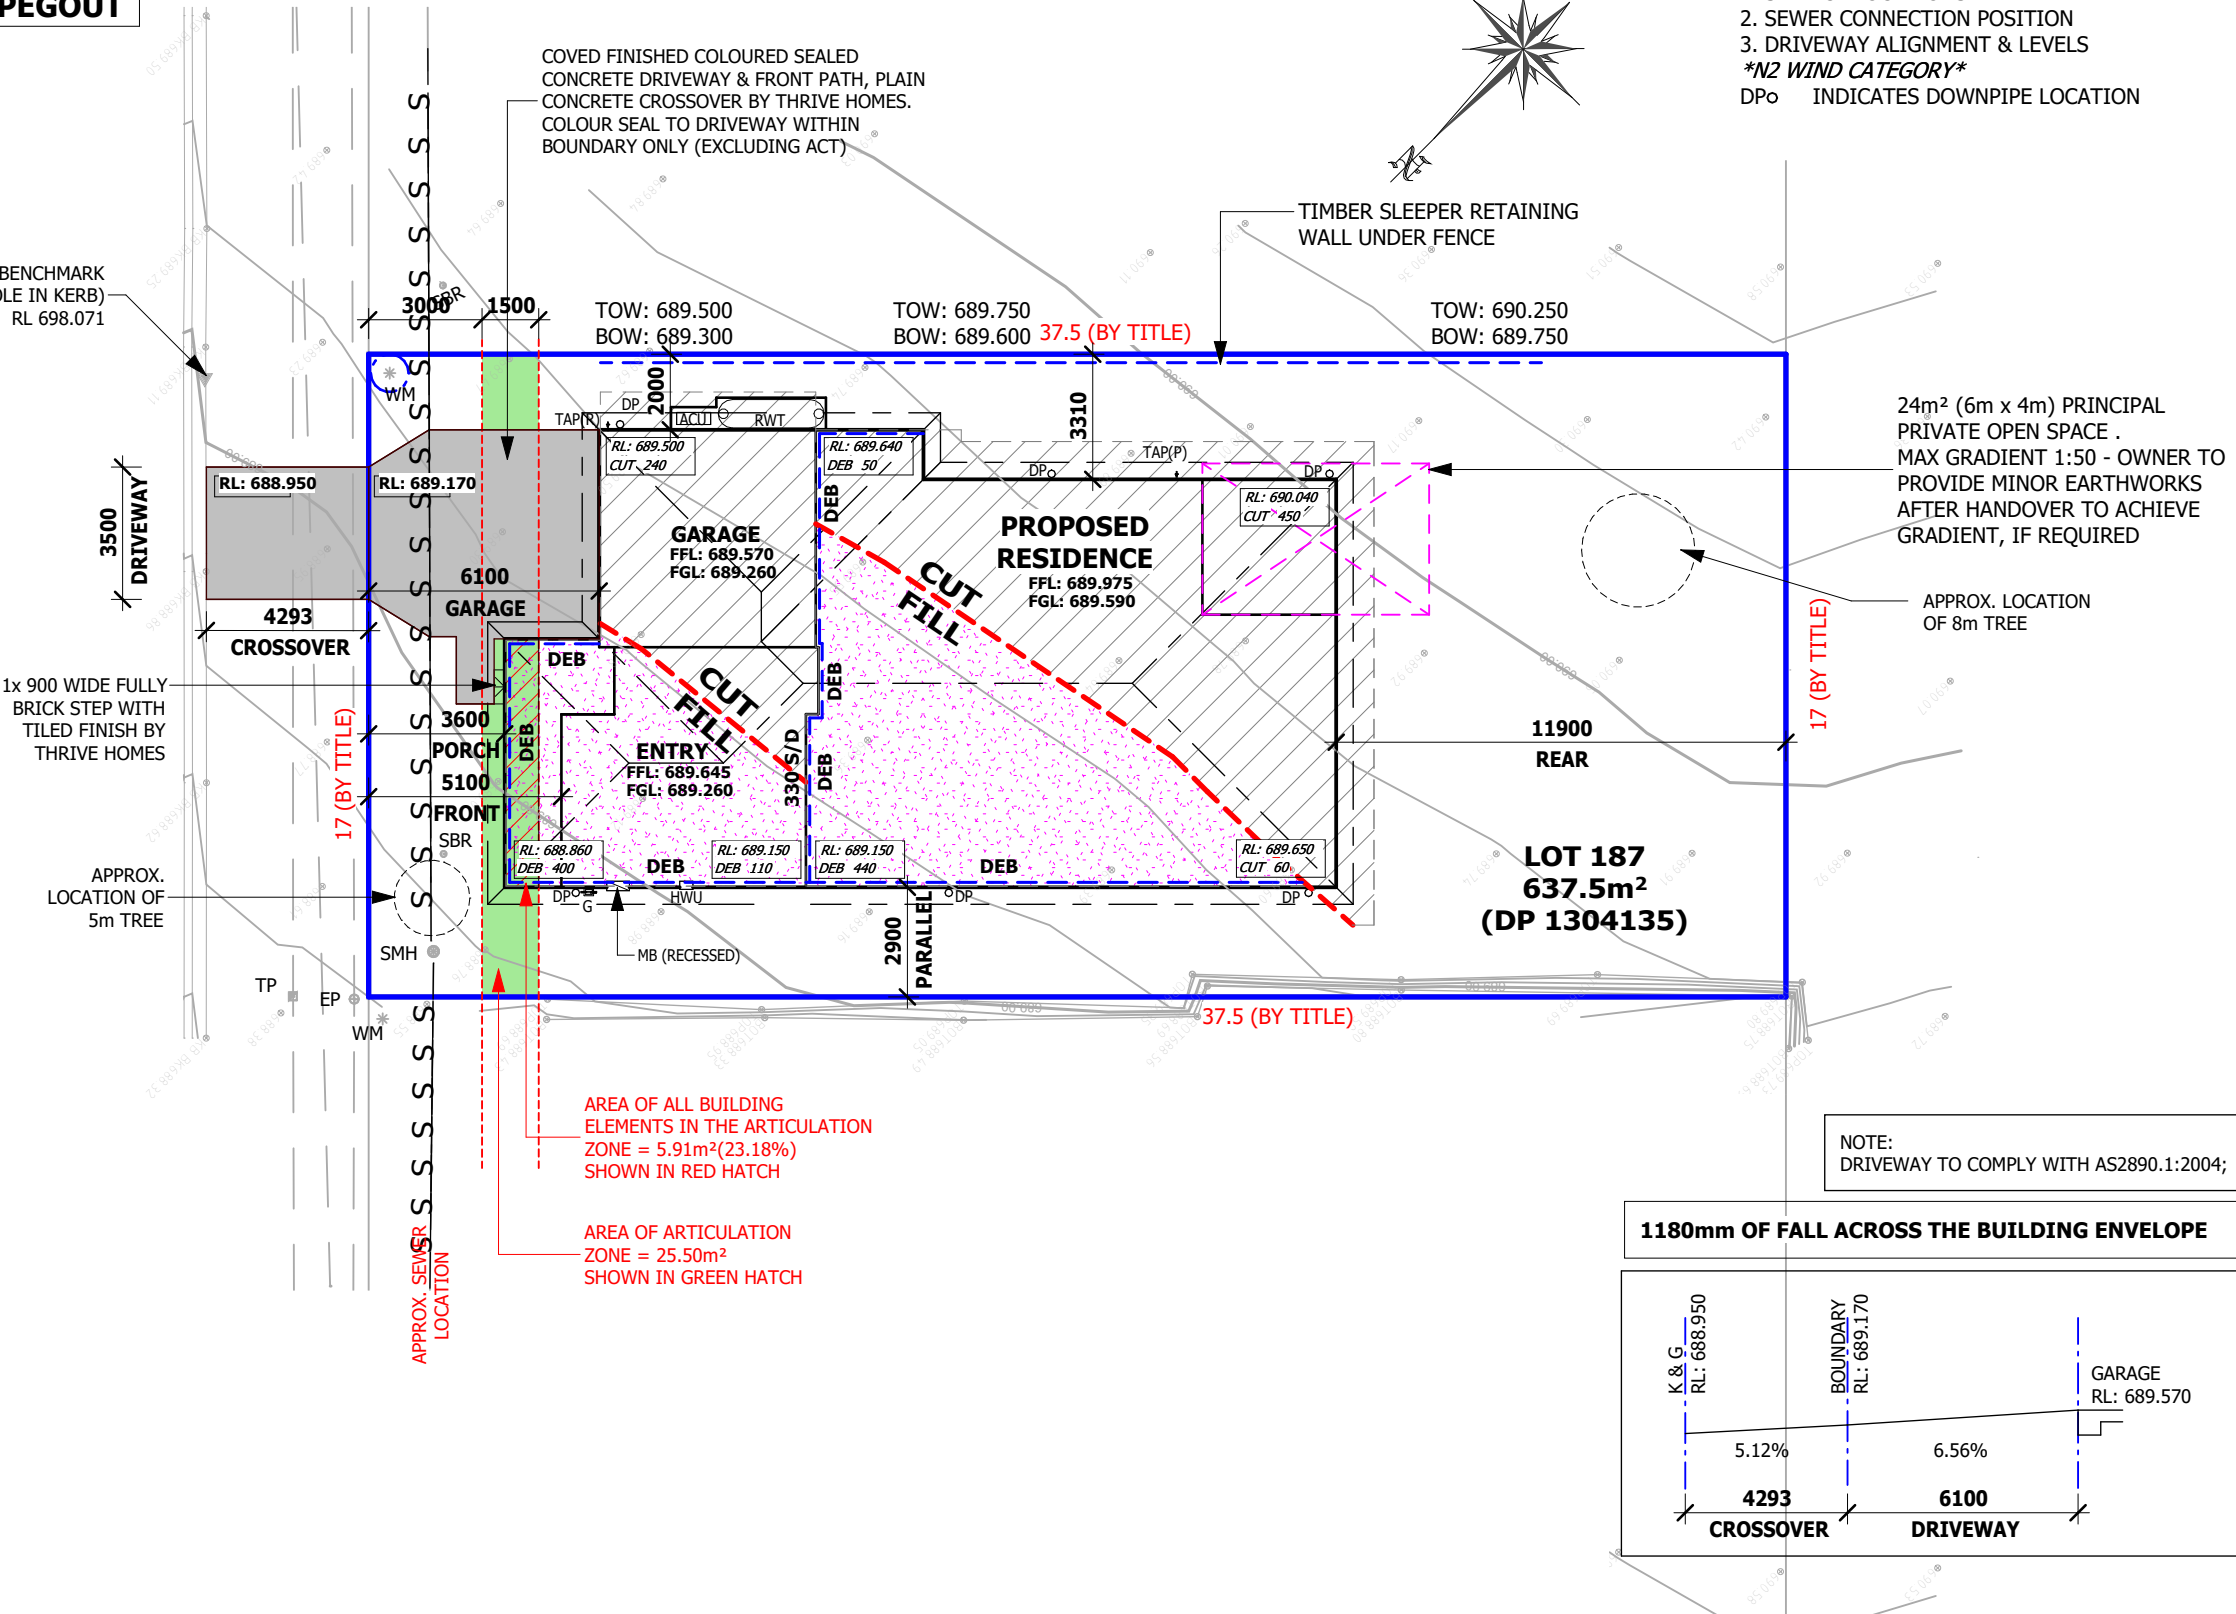

NOTES:

PLEASE NOTE: DETAILS SHOWN ON THESE PLANS ARE INTENDED TO BE ACCURATE - HOWEVER INFORMATION WRITTEN INTO INDIVIDUAL CONTRACTS WILL TAKE PRECEDENCE OVER PLANS

- * ALL DIMENSIONS ARE IN MILLIMETRES
- * DO NOT SCALE - USE WRITTEN DIMENSIONS
- * ALL DIMENSIONS ARE TO STRUCTURAL FRAMES ONLY EXCLUDING FINISHED SURFACES

ThriveHomes
LEVEL 7, 5 RIDER BOULEVARD
RHODES NSW 2138
TELEPHONE 02 8758 4800
FAX 02 9300 5646
Builder's licence No. 301349C

CLIENT:
THRIVE HOMES

SITE ADDRESS:
LOT 187 (DP 1304135)
No. 41 KEIGHTLEY AVENUE, WINDRADYNE
BATHURST, NSW 2795

HOUSE TYPE: HELIX 24
FACADE: HUNTLEE
TYPE: DOUBLE GARAGE
SPECIFICATION: EVOQUE
DRAWING TITLE:
SITE PLAN


DRAWN BY: HN	DATE DRAWN: 13.05.26	SCALE: 1 : 200
COUNCIL AREA: BATHURST		DRWG No: 02
JOB No: T001735		ISSUE: D

INCLUDING

1 2

- | 12100 | |
|-----------------|-----------------|
| 250 | 250 |
| 470 | 470 |
| 1070 | 1070 |
| 2650 | 2650 |
| 4200 | 4200 |
| 4200 | 4200 |
| 2320 | 2320 |
| 2320 | 2320 |
| 4330 | 4330 |
| 4420 | 4420 |
| 160 | 160 |
| 6570 | 6570 |
| 5630 | 5630 |
| 2650 | 2650 |
| 4200 | 4200 |
| 4200 | 4200 |
| 2320 | 2320 |
| 2320 | 2320 |
| 4330 | 4330 |
| 4420 | 4420 |
| 160 | 160 |
| 980 | 980 |
| 150 | 150 |
| 250 | 250 |
| 70 | 70 |
| 1760 | 1760 |
| 250 | 250 |
| 1400 | 1400 |
| 250 | 250 |
| 980 | 980 |
| 150 | 150 |
| 250 | 250 |
| 900 | 900 |
| 350 | 350 |
| 720 | 720 |
| 470 | 470 |
| 5530 | 5530 |
| 5530 | 5530 |
| 4810 | 4810 |
| 5500 | 5500 |
| 5500 | 5500 |
| 5500 | 5500 |
| 5500 | 5500 |
| 3640 | 3640 |
| 180 | 180 |
| 1680 | 1680 |
| 700 | 700 |
| 90 | 90 |
| 980 | 980 |
| REF | REF |

DRAWN BY: HN	DATE DRAWN: 13.05.26	SCALE: 1 : 100
COUNCIL AREA: BATHURST		DRWG No: 03
JOB No: T001735		ISSUE: D

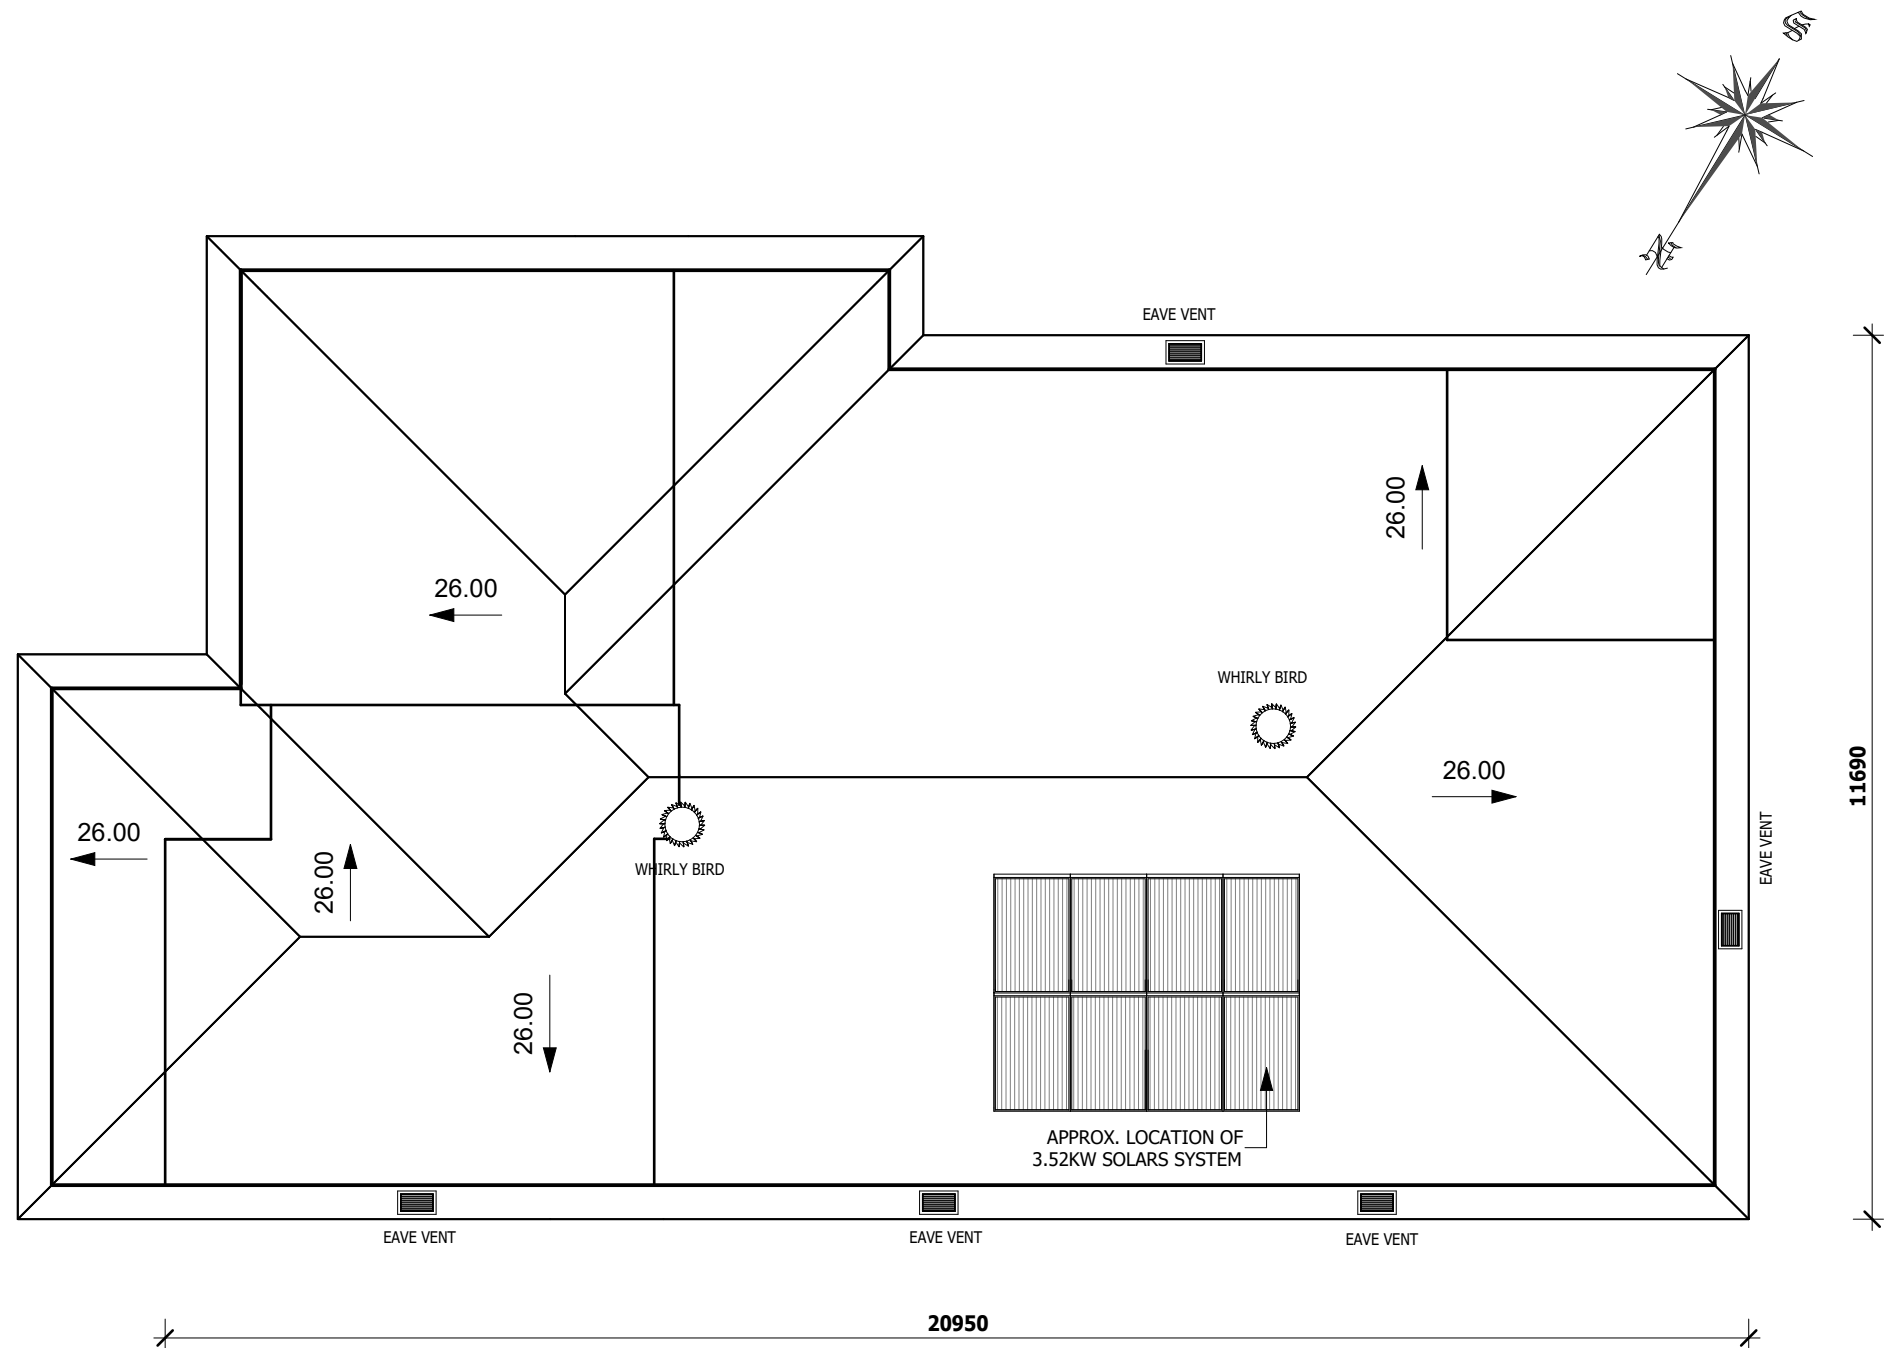

CONDENSATION CALCULATIONS				
*Whirlybirds must be placed not more 900mm below the ridge height or highest point of the roof space.				
	ROOF PITCH	ROOF LENGTH	WHIRLY BIRDS	EAVE VENTS
ROOF	26.0° PITCH	20.95(m)	2	5

NOTES:

PLEASE NOTE: DETAILS SHOWN ON THESE PLANS ARE INTENDED TO BE ACCURATE - HOWEVER INFORMATION WRITTEN INTO INDIVIDUAL CONTRACTS WILL TAKE PRECEDENCE OVER PLANS

- * ALL DIMENSIONS ARE IN MILLIMETRES
- * DO NOT SCALE - USE WRITTEN DIMENSIONS
- * ALL DIMENSIONS ARE TO STRUCTURAL FRAMES ONLY EXCLUDING FINISHED SURFACES

ThriveHomes
LEVEL 7, 5 RIDER BOULEVARD
RHODES NSW 2138
TELEPHONE 02 8758 4800
FAX 02 9300 5646

Builder's licence No. 301349C

CLIENT:
THRIVE HOMES

SITE ADDRESS:
LOT 187 (DP 1304135)
No. 41 KEIGHTLEY AVENUE, WINDRADYNE
BATHURST, NSW 2795

HOUSE TYPE: HELIX 24
FACADE: HUNTLEE
TYPE: DOUBLE GARAGE
SPECIFICATION: EVOQUE

DRAWING TITLE:
ROOF PLAN

DRAWN BY:
HN

DATE DRAWN:
13.05.26


SCALE:
1 : 100

COUNCIL AREA:
BATHURST


DRWG No:
04

JOB No:
T001735

ISSUE:
D

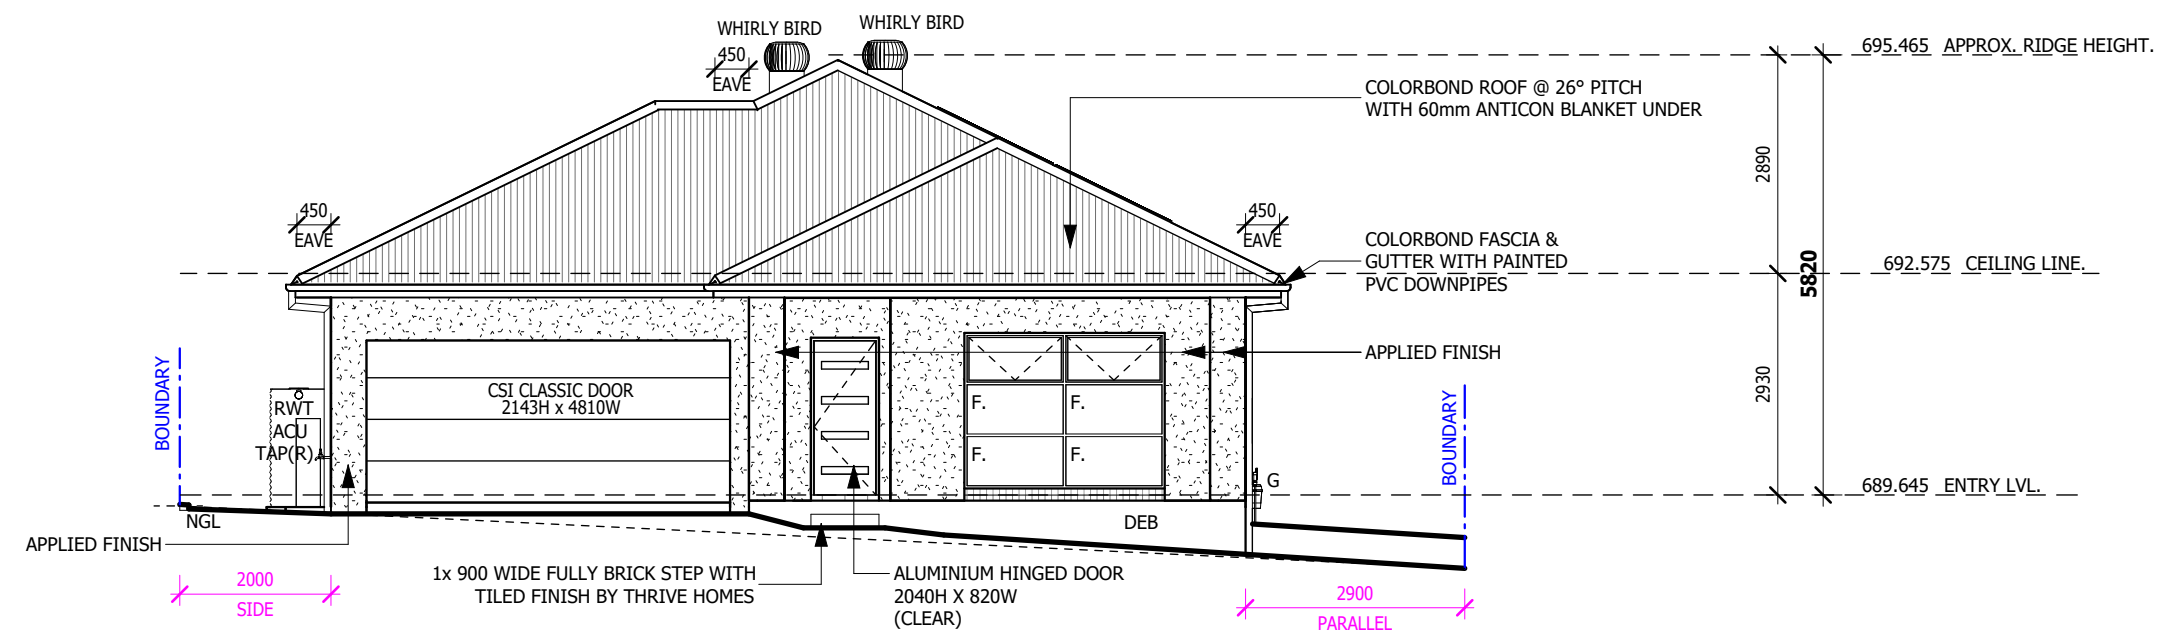

ELEVATION 1

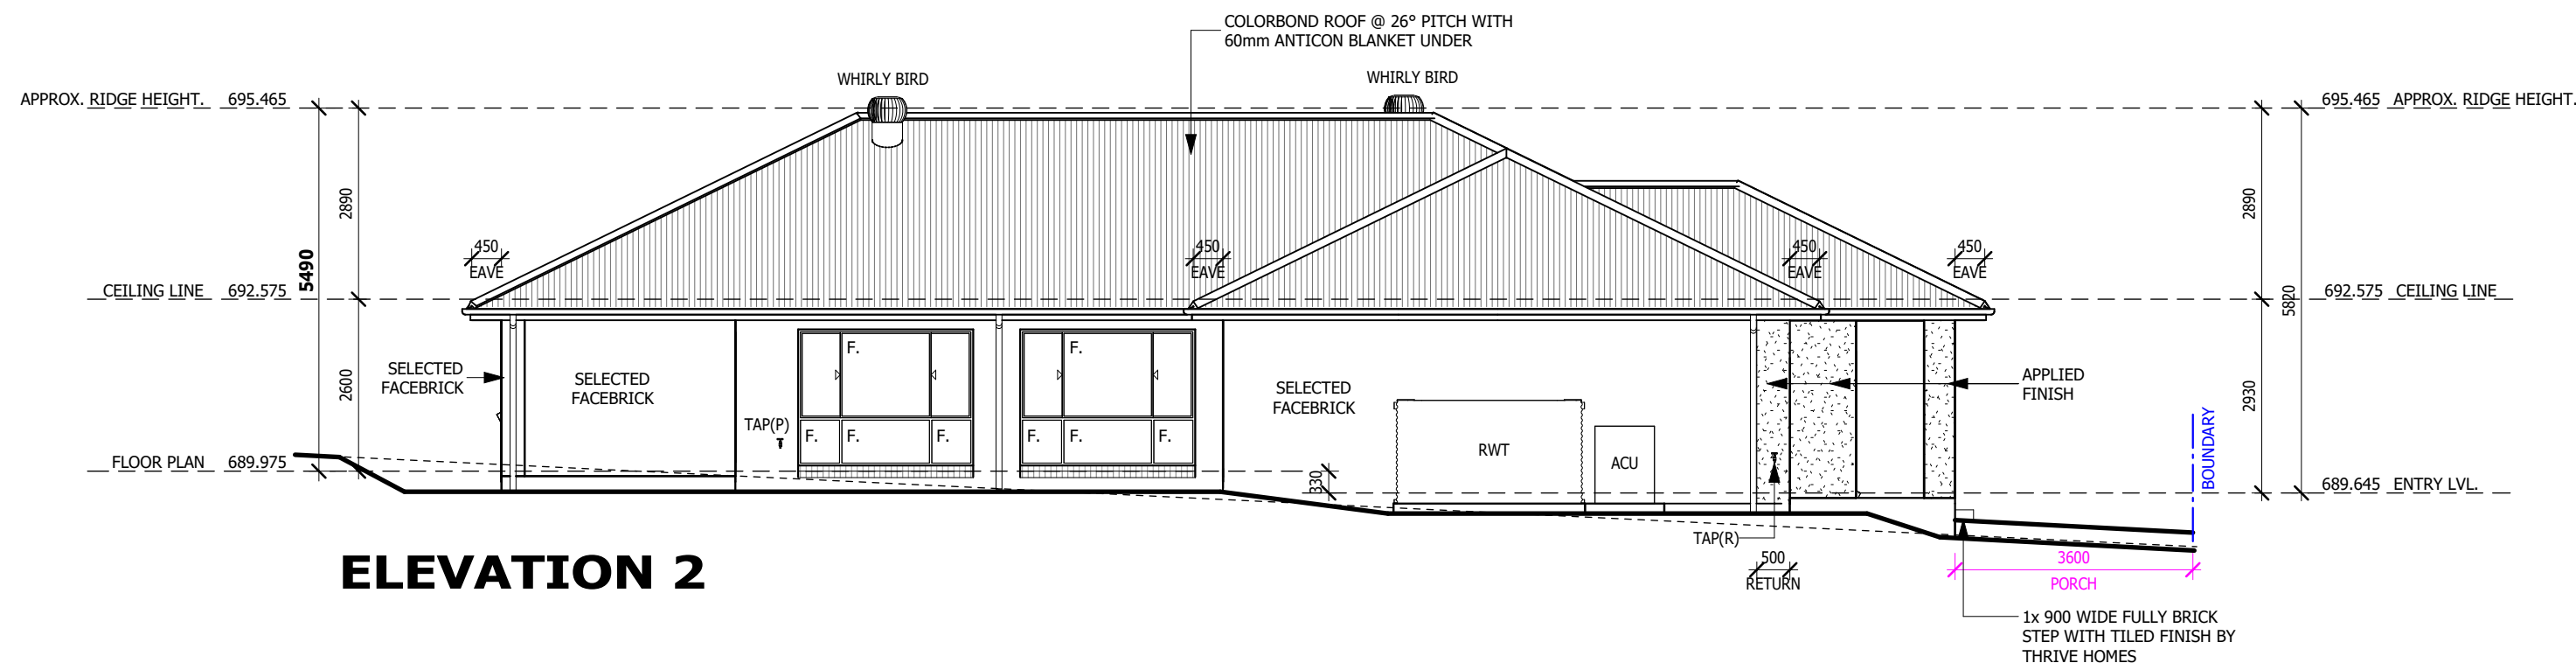

ELEVATION 2

THIS DRAWING IS SUBJECT TO COPYRIGHT LAWS AND MAY NOT BE COPIED WITHOUT THE WRITTEN PERMISSION OF THRIVE HOMES PTY LTD-ACN 613 679 333

WINDOW HEAD HEIGHTS TO BE 2143H FROM FFL UNLESS STATED OTHERWISE.

CEILING HEIGHT NOMINAL TO FRAME HEIGHT, SUBJECT TO SELECTED FLOOR FINISH.

ARTICULATION JOINT REQUIRES ADDITIONAL STUD FOR BRICK TIES.

NYLON MESH FLYSCREENS TO ALL OPENING WINDOWS, SLIDING AND STACKER DOORS (EXCLUDING HINGED DOORS)

CSR WALL WRAP TO EXTERNAL WALLS

NOTES:

PLEASE NOTE: DETAILS SHOWN ON THESE PLANS ARE INTENDED TO BE ACCURATE - HOWEVER INFORMATION WRITTEN INTO INDIVIDUAL CONTRACTS WILL TAKE PRECEDENCE OVER PLANS

- * ALL DIMENSIONS ARE IN MILLIMETRES
- * DO NOT SCALE - USE WRITTEN DIMENSIONS
- * ALL DIMENSIONS ARE TO STRUCTURAL FRAMES ONLY EXCLUDING FINISHED SURFACES

ThriveHomes

LEVEL 7, 5 RIDER BOULEVARD
RHODES NSW 2138
TELEPHONE 02 8758 4800
FAX 02 9300 5646

Builder's licence No. 301349C

CLIENT:
THRIVE HOMES

SITE ADDRESS:
LOT 187 (DP 1304135)
No. 41 KEIGHTLEY AVENUE, WINDRADYNE
BATHURST, NSW 2795

HOUSE TYPE: HELIX 24
FACADE: HUNTLEE
TYPE: DOUBLE GARAGE
SPECIFICATION: EVOQUE

DRAWING TITLE:
ELEVATION 1-2

DRAWN BY: HN	DATE DRAWN: 13.05.26	SCALE: 1 : 100
COUNCIL AREA: BATHURST		DRWG No: 05
JOB No: T001735		ISSUE: D

©



CSR WALL WRAP TO EXTERNAL WALLS



DRAWN BY: HN	DATE DRAWN: 13.05.26	SCALE: 1 : 100
COUNCIL AREA: BATHURST		DRWG No: 06
JOB No: T001735		ISSUE: D

INSULATION NOTE:

- R6.0 BULK INSULATION BATTS TO CEILING WITH R3.0 WHERE 6.0 WILL NOT FIT TO CEILINGS WITH ROOF OVER (EXCLUDING CEILINGS OVER GARAGE, PORCH & ALFRESCO)
- R2.5 INSULATION TO EXTERNAL WALLS & R2.2 INSULATION TO INTERNAL WALLS BETWEEN HOUSE AND GARAGE (EXCLUDES GARAGE EXTERNAL WALLS)
- CSR BRADFORD WALL WRAP TO EXTERNAL WALLS

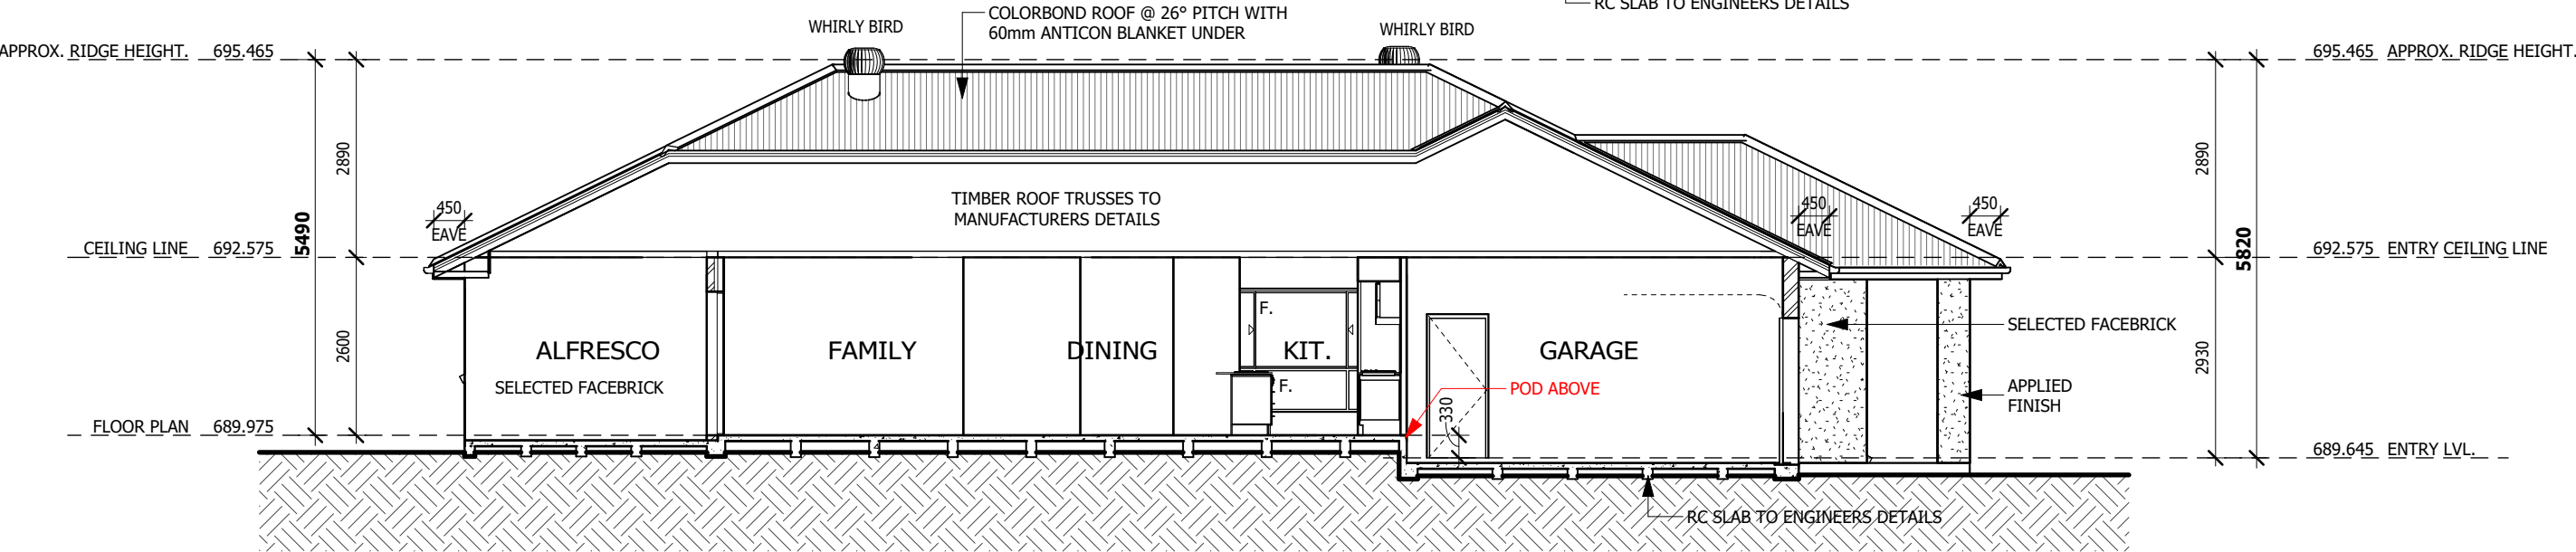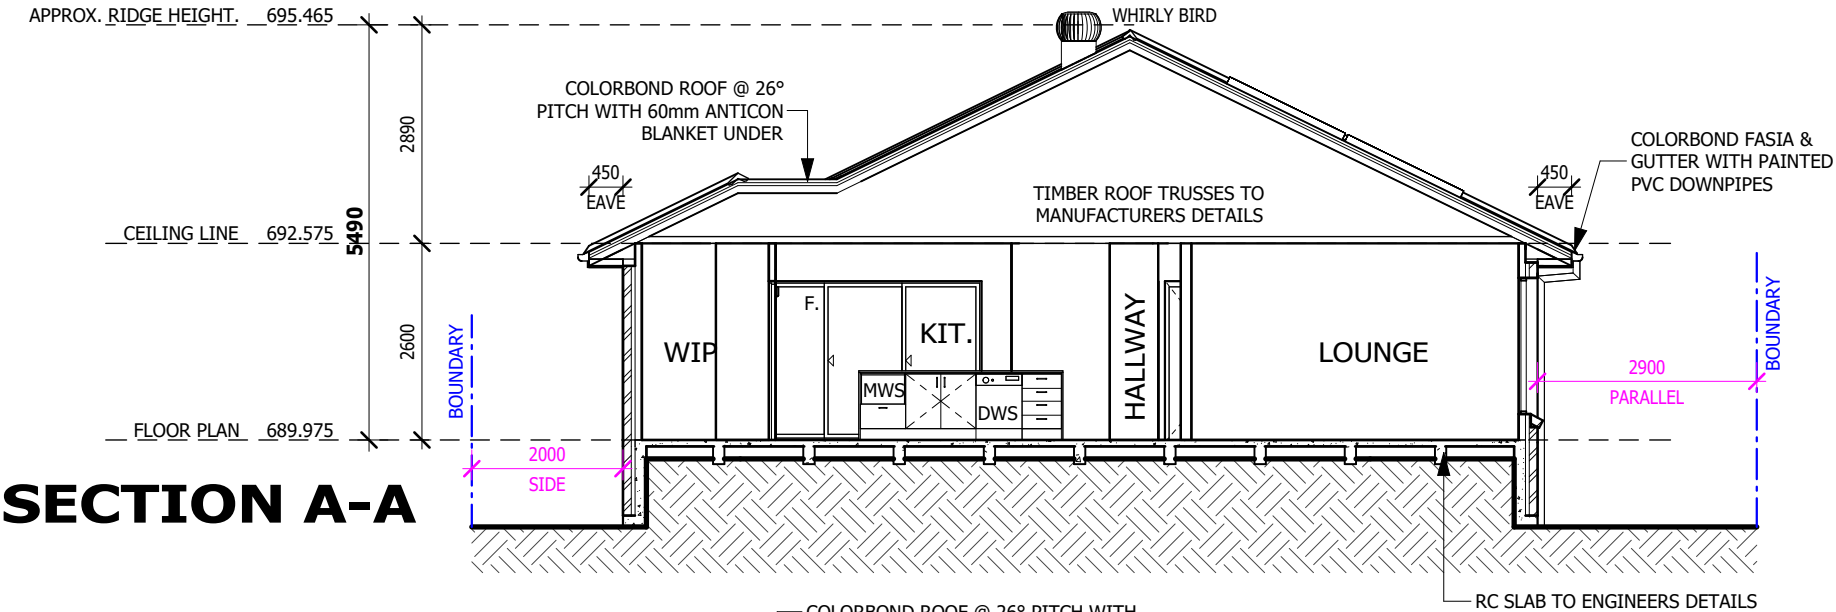

SECTION B-B

BASIX COMMITMENTS

PROJECT DETAILS			STORMWATER	ENERGY	NATURAL LIGHTING
Site area	638	m ²	Rainwater tank to collect at least 180.0 m ² of rain run off from roof area	ACTIVE COOLING/HEATING 1-phase	Applicant must provide a window for natural lighting to 2 bathrooms/toilets
Roof area	300.0	m ²	Rainwater tank to be connected to all toilets with in the development	Cooling system with day/night zoning for bedrooms & living areas with an 3.0 STAR	
Number of bedrooms	4		Rainwater tank to be connected to cold water tap to supply water to the washing machine	Heating system with day/night zoning for bedrooms & living areas with an 3.5 STAR	
Total area of vegetation (garden & lawn)	366	m ²	Rainwater to be connected to at least one outdoor tap for garden watering		COOKING (KITCHEN APPLIANCES)
ABSA Certificate Number (if applicable)	#HR-N5XTV0-02		Rainwater to have a capacity of at least 3000LTR		Install a gas cooktop and electric oven
Net conditioned floor area	157.1	m ²		VENTILATION	
Net Unconditioned floor area	10.4	m ²	WATER	At least 1 Bathroom: individual fan, ducted to façade or roof; Operation: please select	DESIGN ENHANCEMENT
Concession claimed (if applicable)	N/A		All showers with in the development are to have a minimum rating of 4 star showerheads	Kitchen: individual fan, ducted to façade or roof: manual switch on/off	Install a fixed outdoor clothes drying line
Cooling load (if applicable)	12	MJ/m ² /pa	Each toilet is to have a flushing system of no less than a 4 star rating	Laundry: natural ventilation only, or no laundry	
Heating load (if applicable)	143	MJ/m ² /pa	All basin taps to have a minimum rating of 4 star rating	ARTIFICIAL LIGHTING	
			All taps in the kitchen are to have a minimum rating of 4 star	The applicant must ensure that a minimum of 80% of light fixtures are fitted with	
			HOT WATER	fluorescent, compact fluorescent, or light-emitting-diode (LED) lamps.	INSULATION
			Gas instantaneous hot water system with a performance of 6 stars		External wall [excluding garage]: R2.5
					Ceiling [excluding garage & alfresco]: R6.0

NOTES:

PLEASE NOTE: DETAILS SHOWN ON THESE PLANS ARE INTENDED TO BE ACCURATE - HOWEVER INFORMATION WRITTEN INTO INDIVIDUAL CONTRACTS WILL TAKE PRECEDENCE OVER PLANS

- * ALL DIMENSIONS ARE IN MILLIMETRES
- * DO NOT SCALE - USE WRITTEN DIMENSIONS
- * ALL DIMENSIONS ARE TO STRUCTURAL FRAMES ONLY EXCLUDING FINISHED SURFACES

ThriveHomes
LEVEL 7, 5 RIDER BOULEVARD
RHODES NSW 2138
TELEPHONE 02 8758 4800
FAX 02 9300 5646

Builder's licence No. 301349C

CLIENT:
THRIVE HOMES

SITE ADDRESS:
LOT 187 (DP 1304135)
No. 41 KEIGHTLEY AVENUE, WINDRADYNE
BATHURST, NSW 2795

HOUSE TYPE: **HELIX 24**
FACADE: **HUNTLEE**
TYPE: **DOUBLE GARAGE**
SPECIFICATION: **EVOQUE**

DRAWING TITLE:
SECTIONS & BASIX

DRAWN BY: HN	DATE DRAWN: 13.05.26	SCALE: 1 : 100
COUNCIL AREA: BATHURST		DRWG No: 07
JOB No: T001735		ISSUE: D

LEGEND:


70mm STEPDOWN TO WET AREAS

LAUNDRY / WC


- PROVIDE SKIRTING TILE TO PERIMETER WALLS OF LAUNDRY & WC
- LAUNDRY SPLASH BACK - FOUR TILE HEIGHT OVER LAUNDRY TUB
- WM TAPS UNDER TUB

BATHROOM / ENSUITE


- PROVIDE FULL HIGH TILES TO BATHROOM AND ENSUITE (EXCLUDING SEPARATE WC)
- SEMI-FRAMELESS SHOWER SCREEN WITH PIVOT DOOR @ 2000 HIGH.
- APPROXIMATELY 900mm HIGH DIRECT FIX MIRROR TO WIDTH OF VANITY
- FLOATING VANITIES.
- WALL MOUNTED TAPS & SPOUT TO BATH
- BASIN MOUNTED TAPS TO VANITIES.
- 20mm C'STONE BENCHTOP TO VANITIES.
- FLOOR MOUNTED VANITIES WITH KICK BOARD

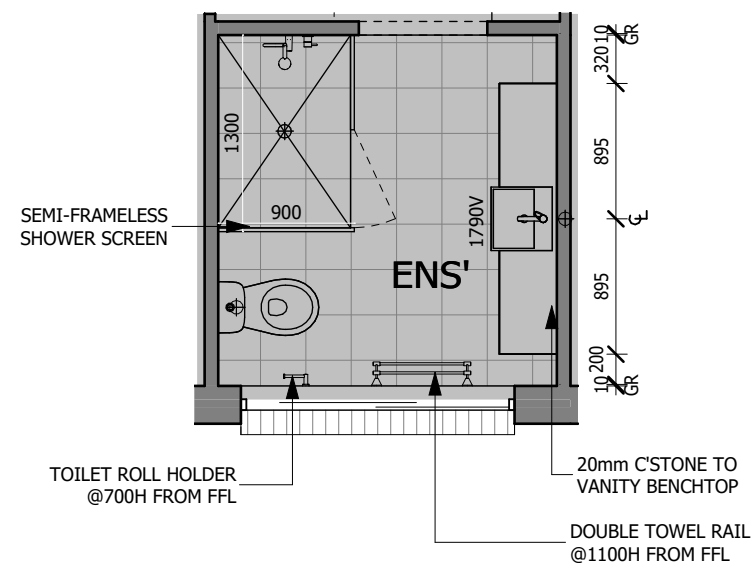

BED 1 ENSUITE

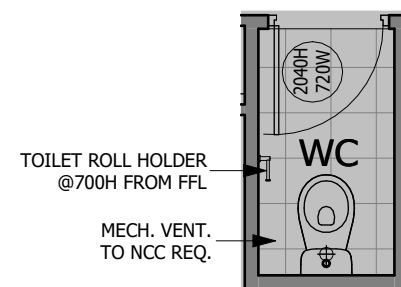

WC

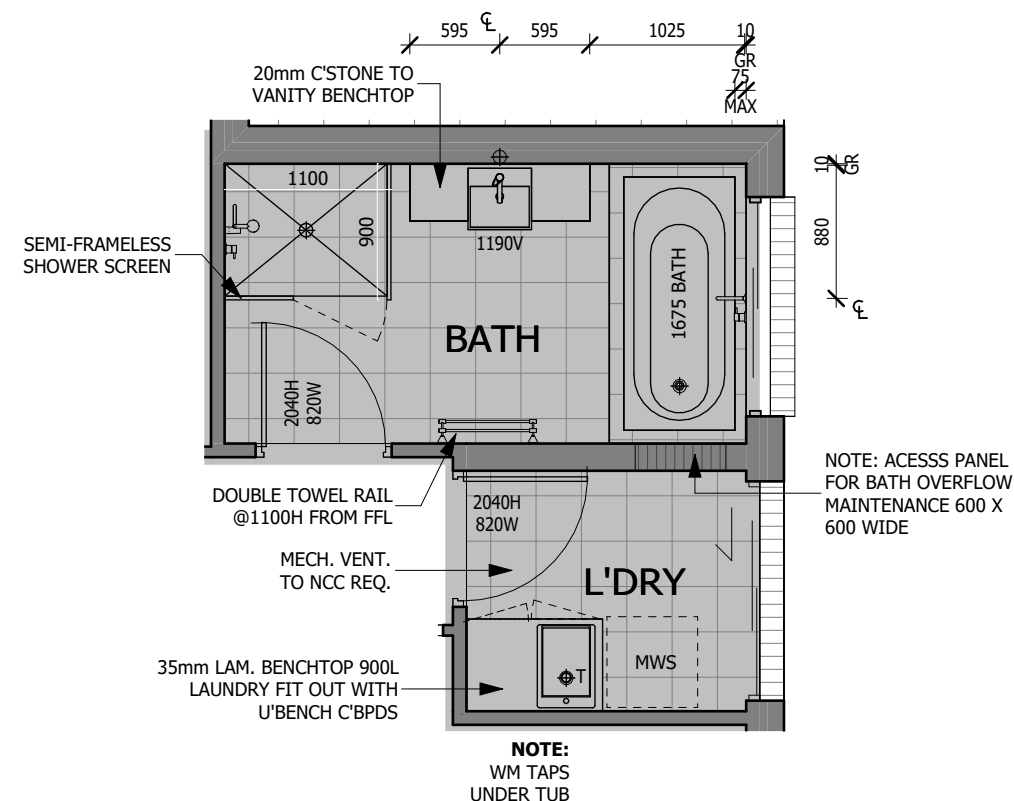

MAIN BATH & LAUNDRY

NOTES:

PLEASE NOTE: DETAILS SHOWN ON THESE PLANS ARE INTENDED TO BE ACCURATE - HOWEVER INFORMATION WRITTEN INTO INDIVIDUAL CONTRACTS WILL TAKE PRECEDENCE OVER PLANS

- * ALL DIMENSIONS ARE IN MILLIMETRES
- * DO NOT SCALE - USE WRITTEN DIMENSIONS
- * ALL DIMENSIONS ARE TO STRUCTURAL FRAMES ONLY EXCLUDING FINISHED SURFACES

ThriveHomes
LEVEL 7, 5 RIDER BOULEVARD
RHODES NSW 2138
TELEPHONE 02 8758 4800
FAX 02 9300 5646
Builder's licence No. 301349C

CLIENT:
THRIVE HOMES

SITE ADDRESS:
LOT 187 (DP 1304135)
No. 41 KEIGHTLEY AVENUE, WINDRADYNE
BATHURST, NSW 2795

HOUSE TYPE: HELIX 24
FACADE: HUNTLEE
TYPE: DOUBLE GARAGE
SPECIFICATION: EVOQUE

DRAWING TITLE:
WET AREA PLANS

DRAWN BY:
HN

DATE DRAWN:
13.05.26

SCALE:
1 : 50

COUNCIL AREA:
BATHURST


DRWG No:
08

JOB No:
T001735

ISSUE:
D

PINS TO BE LOCATED ON INSIDE
EDGE OF BRICKWORK

©

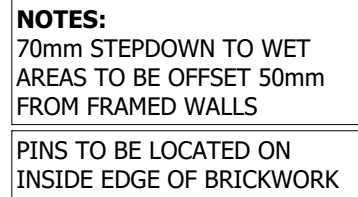

LEGEND:

 70mm STEPDOWN TO WET AREAS

PLEASE NOTE: DETAILS SHOWN ON THESE PLANS ARE INTENDED TO BE ACCURATE - HOWEVER INFORMATION WRITTEN INTO INDIVIDUAL CONTRACTS WILL TAKE PRECEDENCE OVER PLANS

- * ALL DIMENSIONS ARE IN MILLIMETRES
- * DO NOT SCALE - USE WRITTEN DIMENSIONS
- * ALL DIMENSIONS ARE TO STRUCTURAL FRAMES ONLY EXCLUDING FINISHED SURFACES

ThriveHomes
LEVEL 7, 5 RIDER BOULEVARD
RHODES NSW 2138
TELEPHONE 02 8758 4800
FAX 02 9300 5646



Builder's licence No. 301349C

SITE ADDRESS:
LOT 187 (DP 1304135)
No. 41 KEIGHTLEY AVENUE, WINDRADYNE
BATHURST, NSW 2795

HOUSE TYPE:	HELIX 24
FACADE:	HUNTLEE
TYPE:	DOUBLE GARAGE
SPECIFICATION:	EVOQUE
DRAWING TITLE:	SLAB SETOUT PLAN

DRAWN BY: HN	DATE DRAWN: 13.05.26	SCALE: 1 : 100
COUNCIL AREA: BATHURST		DRWG No: 09
JOB No: T001735		ISSUE: D


(B) EASEMENT TO DRAIN WATER 2 WIDE & VARIABLE WIDTH

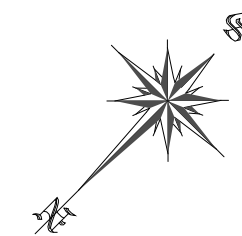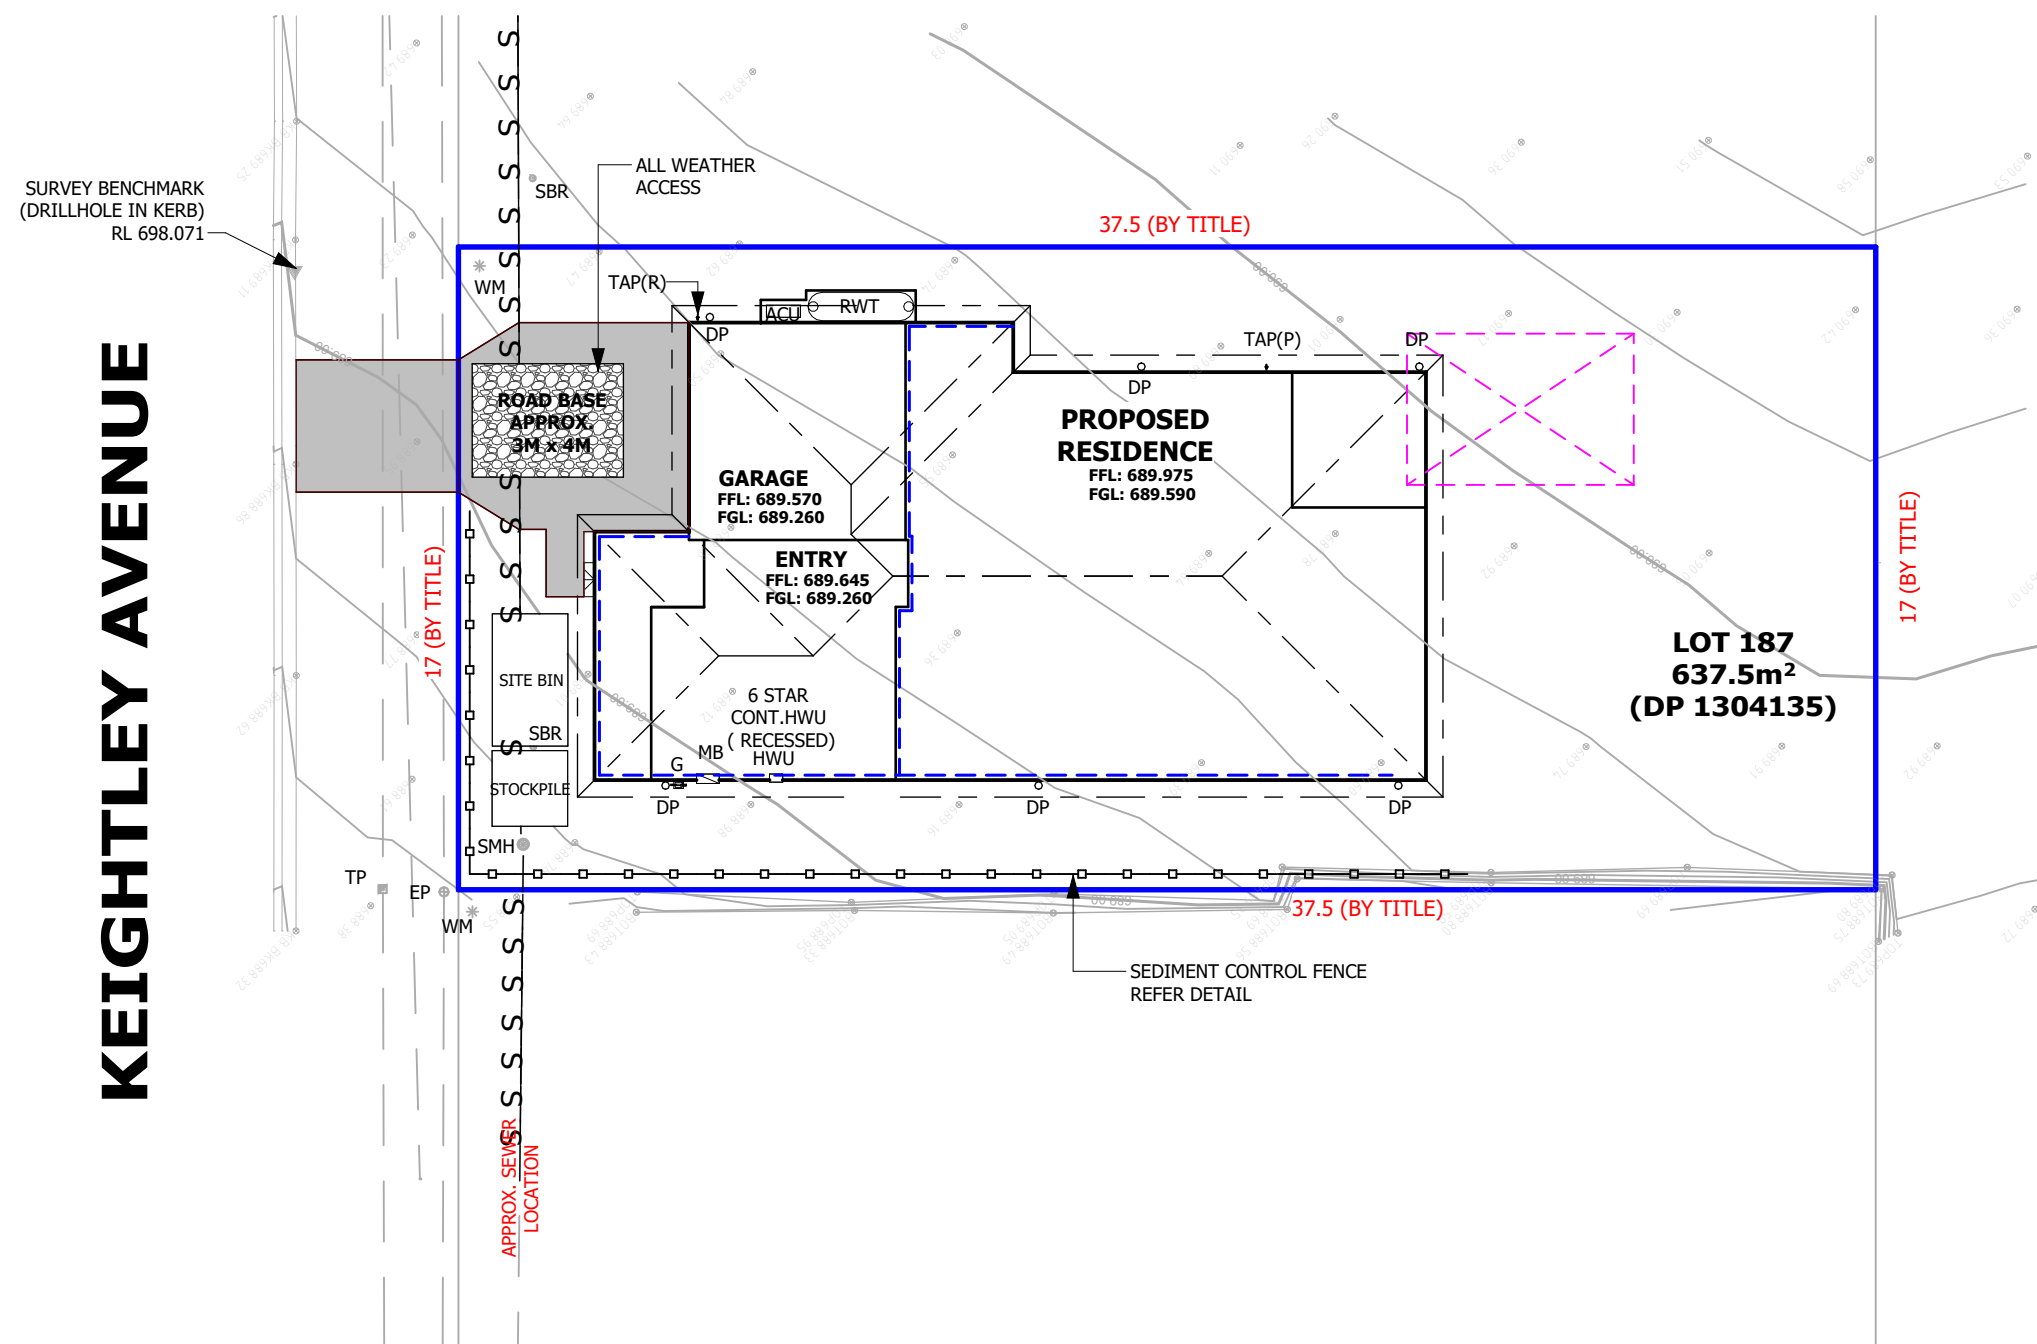

SEDIMENT CONTROL

INSTALL SEDIMENT CONTROL STRUCTURES IN LOCATIONS INDICATED ON THIS DRAWING AND AS OTHERWISE REQUIRED TO CONTROL SEDIMENT DURING ALL EXCAVATIONS AND WHILST AREAS OF THE SITE ARE EXPOSED TO EROSION. REVIEW CONTROL MEASURES AND MAINTAIN STRUCTURES DURING CONSTRUCTION.

IF ADDITIONAL MEASURES ARE REQUIRED FOR EROSION AND CONTROL OR BY COUNCIL REQUIREMENTS, REFER TO "URBAN EROSION AND SEDIMENT CONTROL" GUIDELINES PREPARED BY THE DEPARTMENT OF CONSERVATION AND LAND MANAGEMENT.

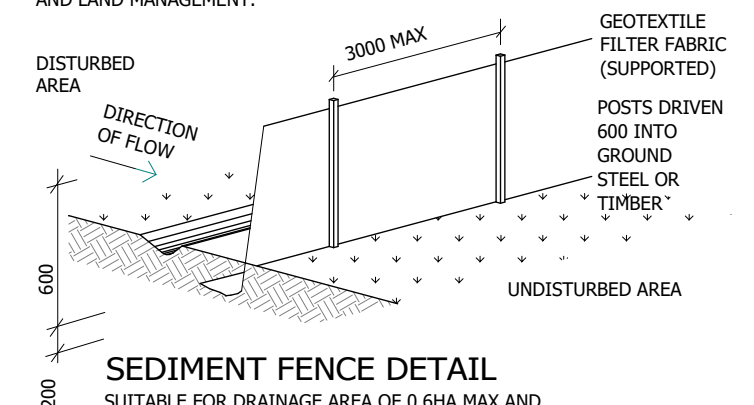

SEDIMENT FENCE DETAIL

SUITABLE FOR DRAINAGE AREA OF 0.6HA MAX AND
SLOPE GRADIENT OF 1:2 MAX WITH LENGTH OF 60M MAX



The Essential First Step

NOTES:

PLEASE NOTE: DETAILS SHOWN ON THESE PLANS ARE INTENDED TO BE ACCURATE - HOWEVER INFORMATION WRITTEN INTO INDIVIDUAL CONTRACTS WILL TAKE PRECEDENCE OVER PLANS

- * ALL DIMENSIONS ARE IN MILLIMETRES
- * DO NOT SCALE - USE WRITTEN DIMENSIONS
- * ALL DIMENSIONS ARE TO STRUCTURAL FRAMES ONLY EXCLUDING FINISHED SURFACES

ThriveHomes
LEVEL 7, 5 RIDER BOULEVARD
RHODES NSW 2138
TELEPHONE 02 8758 4800
FAX 02 9300 5646
Builder's licence No. 301349C


CLIENT:
THRIVE HOMES

SITE ADDRESS:
**LOT 187 (DP 1304135)
No. 41 KEIGHTLEY AVENUE, WINDRADYNE
BATHURST, NSW 2795**


HOUSE TYPE: **HELIX 24**
FACADE: **HUNTLEE**
TYPE: **DOUBLE GARAGE**
SPECIFICATION: **EVOQUE**
DRAWING TITLE:
SEDIMENT CONTROL PLAN

DRAWN BY: HN	DATE DRAWN: 13.05.26	SCALE: 1 : 200
COUNCIL AREA: BATHURST		DRWG No: 10
JOB No: T001735		ISSUE: D

(B) EASEMENT TO DRAIN WATER 2 WIDE & VARIABLE WIDTH

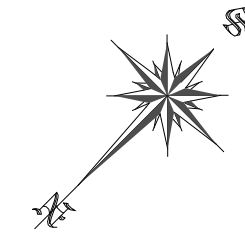

KEIGHTLEY AVENUE

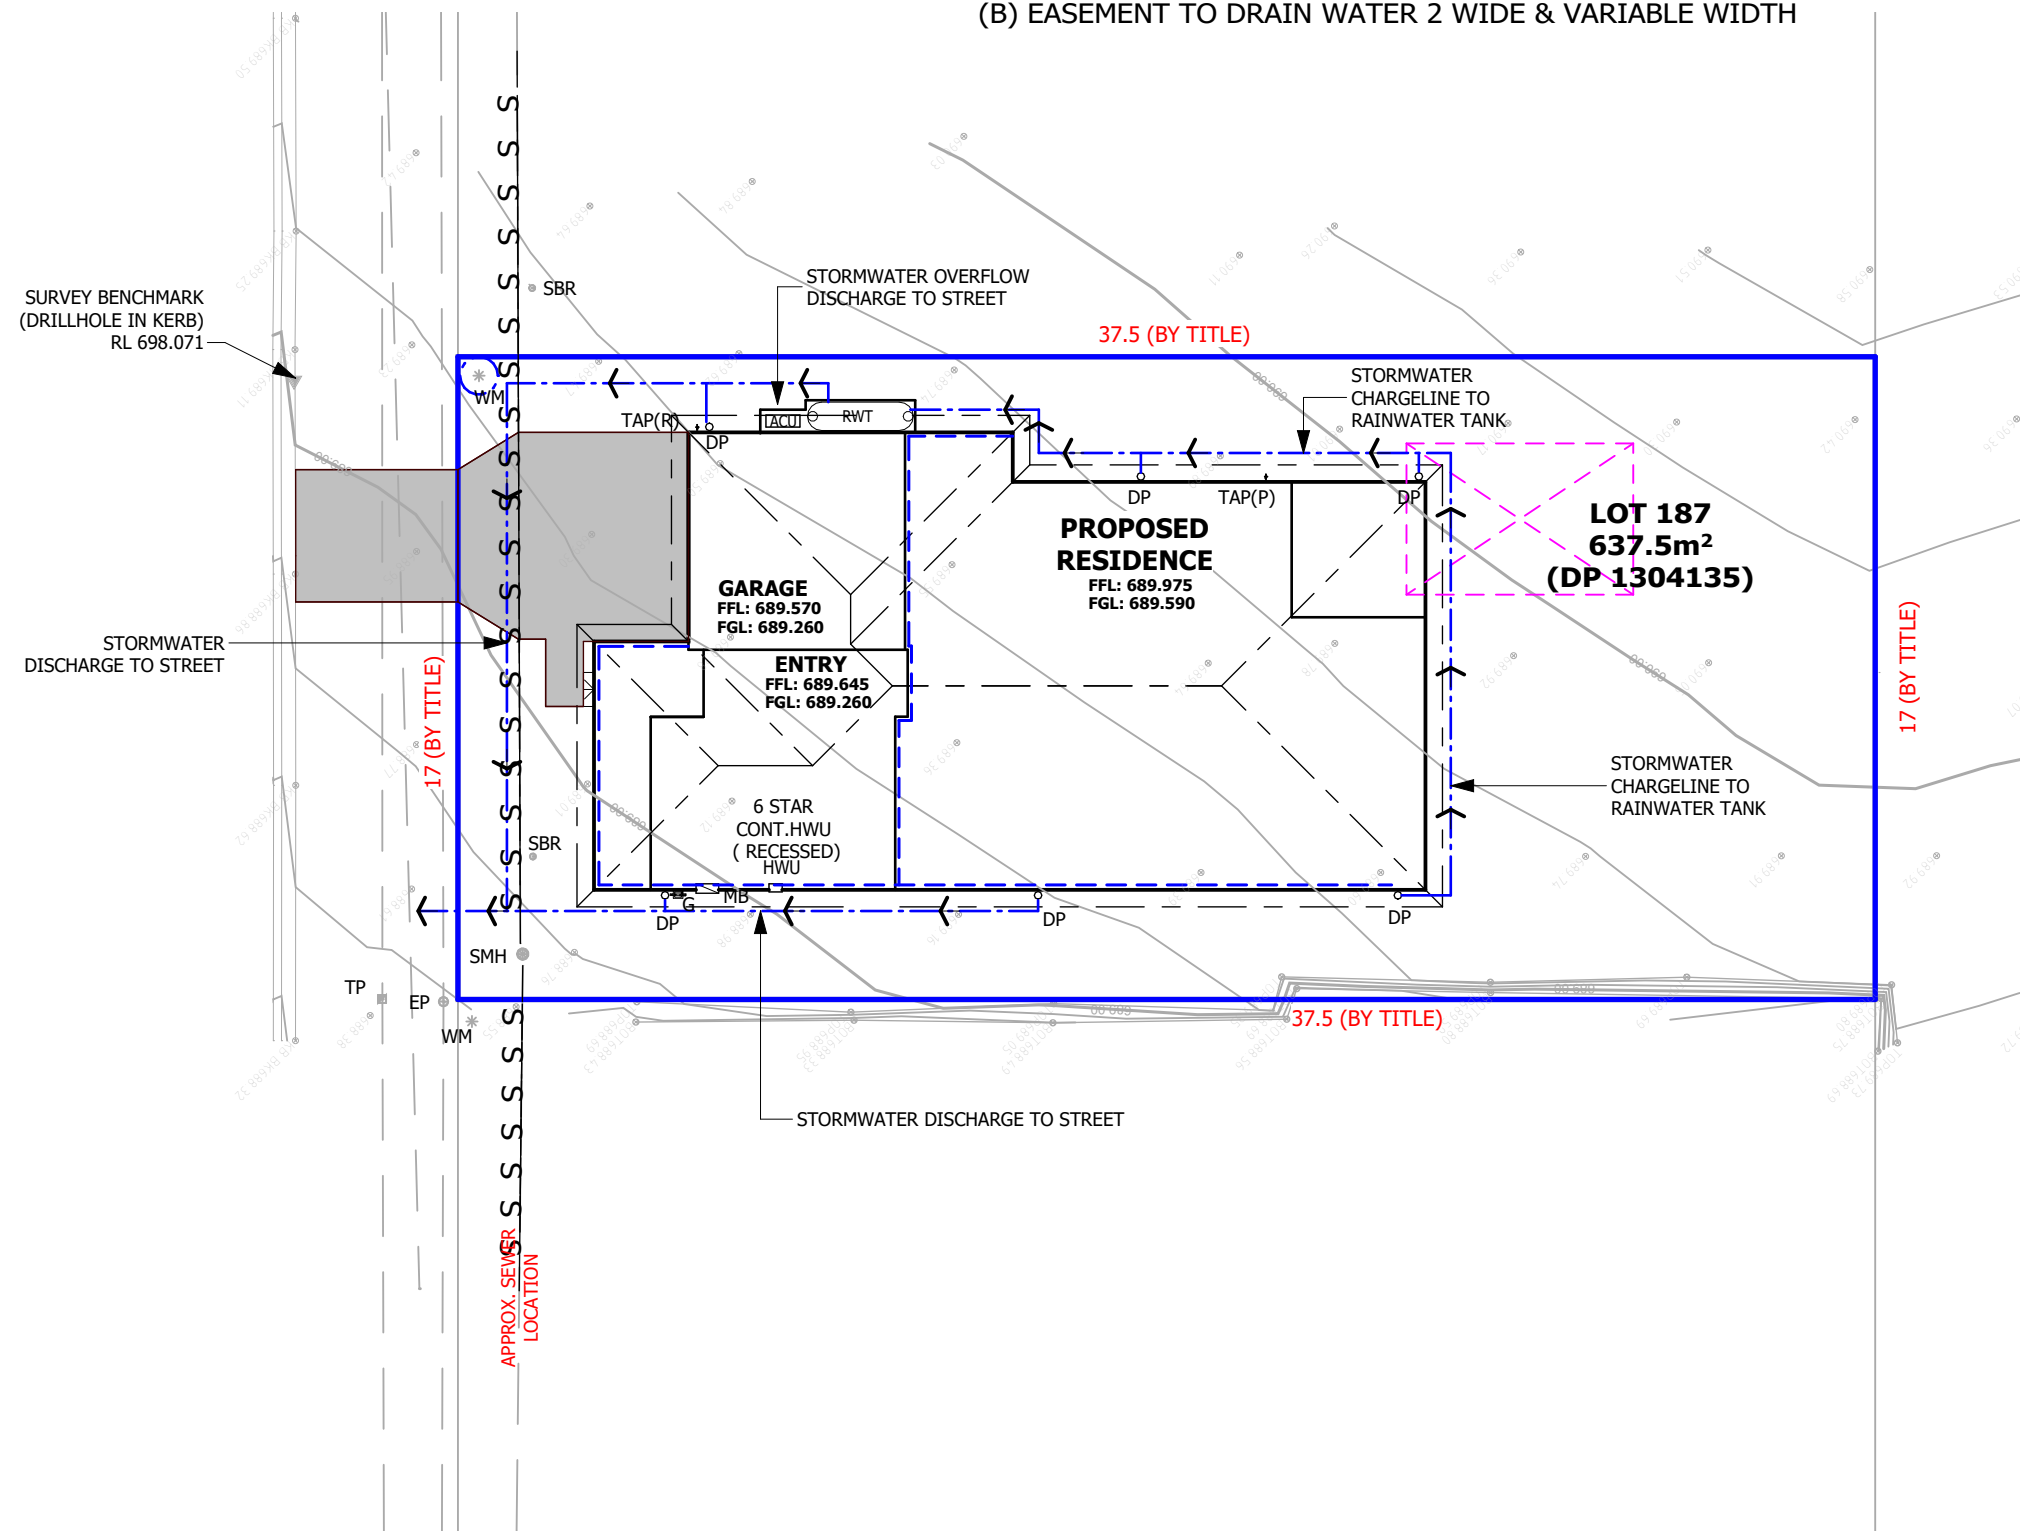

The Essential First Step

NOTES:

PLEASE NOTE: DETAILS SHOWN ON THESE PLANS ARE INTENDED TO BE ACCURATE - HOWEVER INFORMATION WRITTEN INTO INDIVIDUAL CONTRACTS WILL TAKE PRECEDENCE OVER PLANS
* ALL DIMENSIONS ARE IN MILLIMETRES
* DO NOT SCALE - USE WRITTEN DIMENSIONS
* ALL DIMENSIONS ARE TO STRUCTURAL FRAMES ONLY EXCLUDING FINISHED SURFACES


ThriveHomes
LEVEL 7, 5 RIDER BOULEVARD
RHODES NSW 2138
TELEPHONE 02 8758 4800
FAX 02 9300 5646
Builder's licence No. 301349C

CLIENT:
THRIVE HOMES


SITE ADDRESS:
LOT 187 (DP 1304135)
No. 41 KEIGHTLEY AVENUE, WINDRADYNE
BATHURST, NSW 2795

HOUSE TYPE: HELIX 24
FACADE: HUNTLEE
TYPE: DOUBLE GARAGE
SPECIFICATION: EVOQUE
DRAWING TITLE:
STORMWATER PLAN


DRAWN BY: HN	DATE DRAWN: 13.05.26	SCALE: 1 : 200
COUNCIL AREA: BATHURST		DRWG No: 11
JOB No: T001735		ISSUE: D

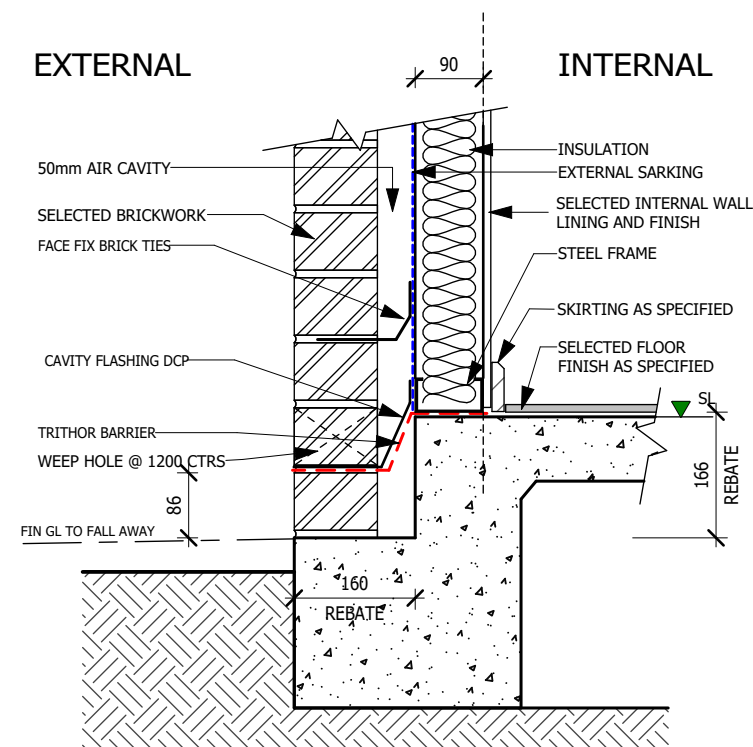


1 BRICK VENEER REBATE DETAIL
SCALE: 1 : 10

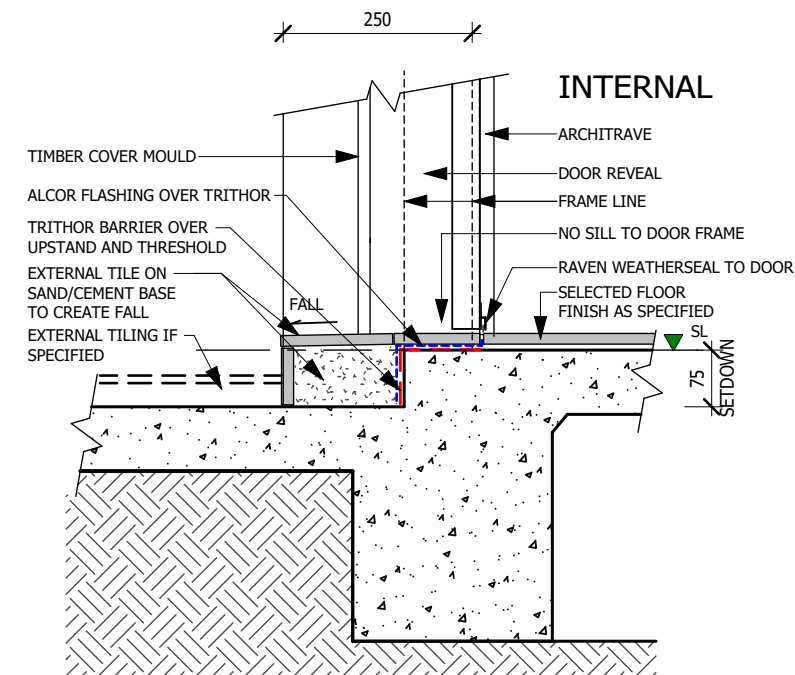

2 BRICK VENEER PORCH ENTRY DOOR
SCALE: 1 : 10

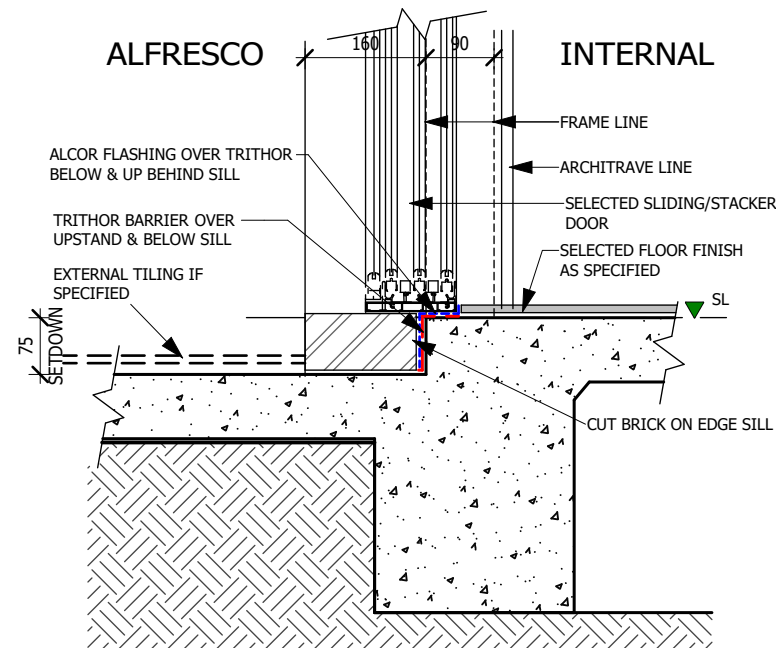

3 ALFRESCO DOOR - BRICK VENEER
SCALE: 1 : 10

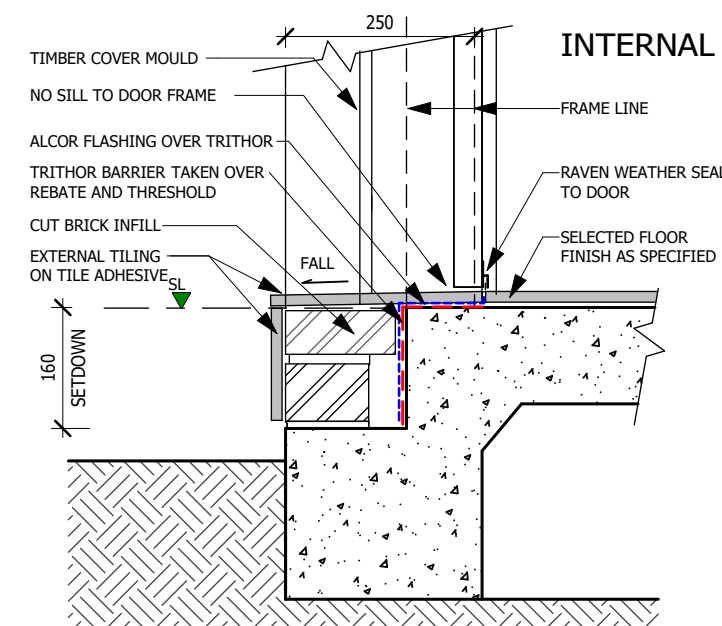

4 LAUNDRY TIMBER DOOR
SCALE: 1 : 10

NOTE: DETAILS ARE APPLICABLE TO ALL ARCHITECTURAL CONDITIONS NOT SPECIFICALLY DETAILED OR REFERENCED ON ARCHITECTURAL DRAWINGS.

NOTES:

PLEASE NOTE: DETAILS SHOWN ON THESE PLANS ARE INTENDED TO BE ACCURATE - HOWEVER INFORMATION WRITTEN INTO INDIVIDUAL CONTRACTS WILL TAKE PRECEDENCE OVER PLANS
* ALL DIMENSIONS ARE IN MILLIMETRES
* DO NOT SCALE - USE WRITTEN DIMENSIONS
* ALL DIMENSIONS ARE TO STRUCTURAL FRAMES ONLY EXCLUDING FINISHED SURFACES

ThriveHomes

LEVEL 7, 5 RIDER BOULEVARD,
RHODES NSW 2138,
TELEPHONE 02 8758 4800,
FAX 02 9300 5646


Builder's licence No. 301349C

CLIENT:
THRIVE HOMES


SITE ADDRESS:
LOT 187 (DP 1304135)
No. 41 KEIGHTLEY AVENUE,
WINDRADYNE
BATHURST, NSW 2795

HOUSE TYPE: HELIX 24
FACADE: HUNTLEE
TYPE: DOUBLE GARAGE
SPECIFICATION: EVOQUE
DRAWING TITLE:
SLAB DETAILS 1


DRAWN BY:	DATE DRAWN:	SCALE:
HN	25.02.26	1 : 10
COUNCIL AREA:	DRWG No:	
BATHURST	D1	
JOB No:	ISSUE:	
T001735	D	

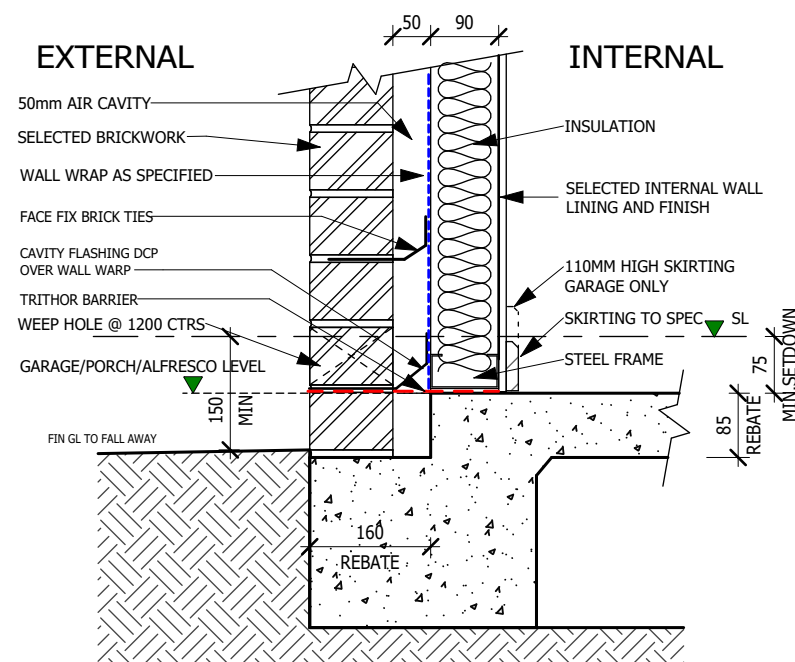


1 GARAGE REBATE (SIDE) & PORCH/ALFRESCO
SCALE: 1 : 10

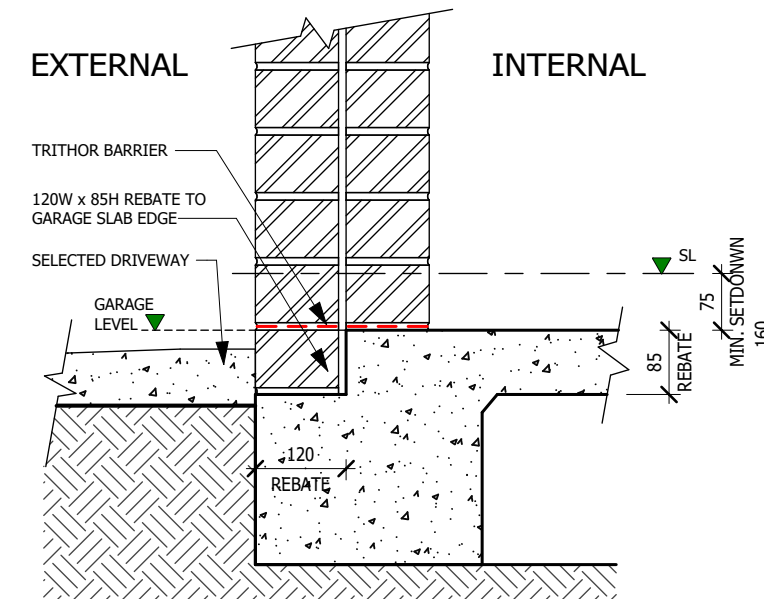

2 GARAGE REBATE (FRONT SIDE OF DOOR)
SCALE: 1 : 10

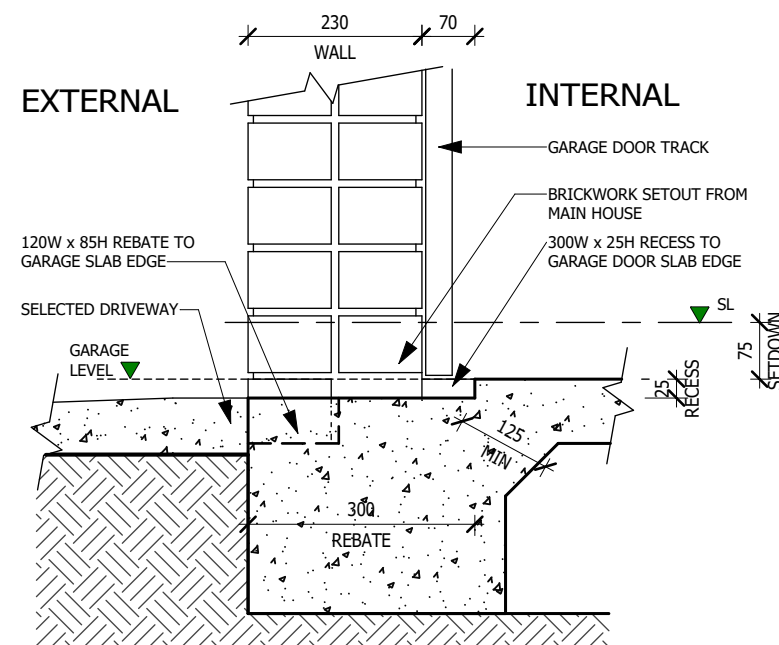

3 GARAGE RECESS (FRONT THROUGH RECESS)
SCALE: 1 : 10

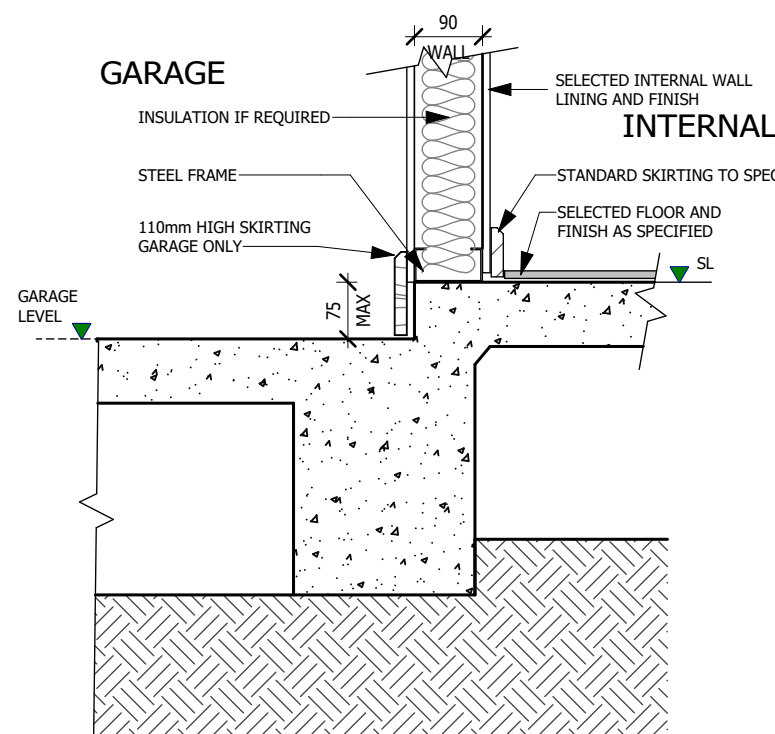

4 INTERNA GARAGE STEP - 75MM STEP ONLY
SCALE: 1 : 10

NOTES:

PLEASE NOTE: DETAILS SHOWN ON THESE PLANS ARE INTENDED
TO BE ACCURATE - HOWEVER INFORMATION WRITTEN INTO
INDIVIDUAL CONTRACTS WILL TAKE PRECEDENCE OVER PLANS
* ALL DIMENSIONS ARE IN MILLIMETRES
* DO NOT SCALE - USE WRITTEN DIMENSIONS
* ALL DIMENSIONS ARE TO STRUCTURAL FRAMES ONLY
EXCLUDING FINISHED SURFACES

ThriveHomes

LEVEL 7, 5 RIDER BOULEVARD,
RHODES NSW 2138,
TELEPHONE 02 8758 4800,
FAX 02 9300 5646


Builder's licence No. 301349C

CLIENT:
THRIVE HOMES


SITE ADDRESS:
LOT 187 (DP 1304135)
No. 41 KEIGHTLEY AVENUE,
WINDRADYNE
BATHURST, NSW 2795

HOUSE TYPE: HELIX 24
FACADE: HUNTLEE
TYPE: DOUBLE GARAGE
SPECIFICATION: EVOQUE
DRAWING TITLE:
SLAB DETAILS 2


DRAWN BY: HN	DATE DRAWN: 25.02.26	SCALE: 1 : 10
COUNCIL AREA: BATHURST		DRWG No: D2
JOB No: T001735		ISSUE: D

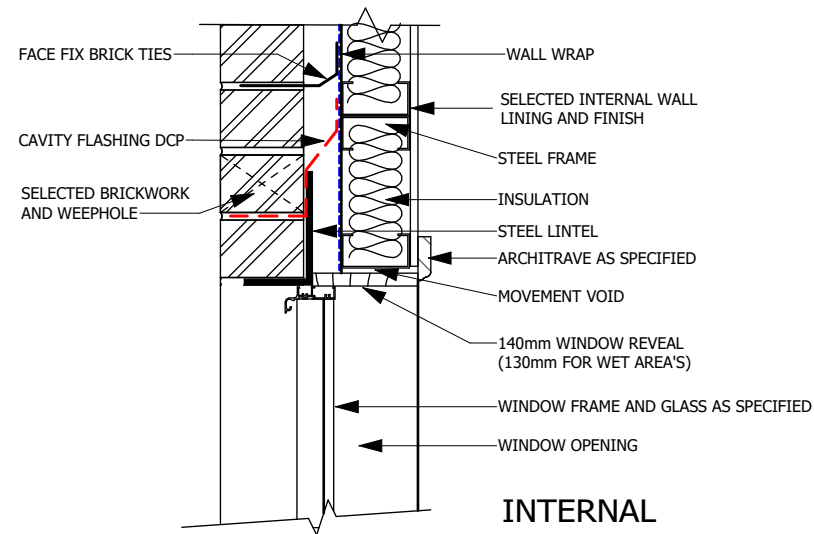


1 WINDOW HEAD - BRICK VENEER
SCALE: 1 : 10

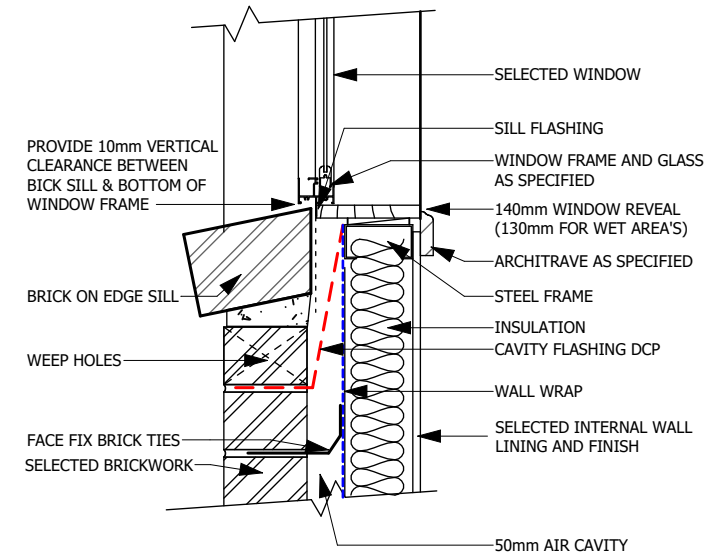

2 WINDOW SILL - BRICK VENEER
SCALE: 1 : 10

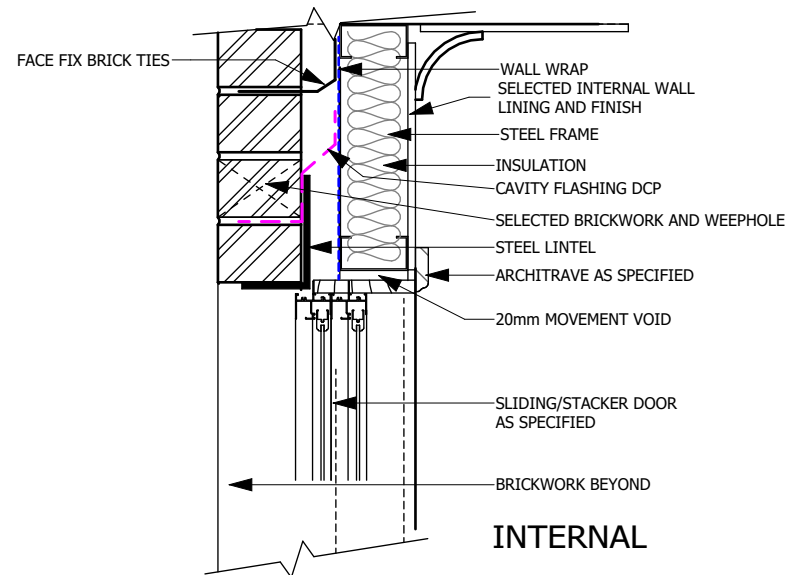

3 SLIDING DOOR HEAD - BV1
SCALE: 1 : 10

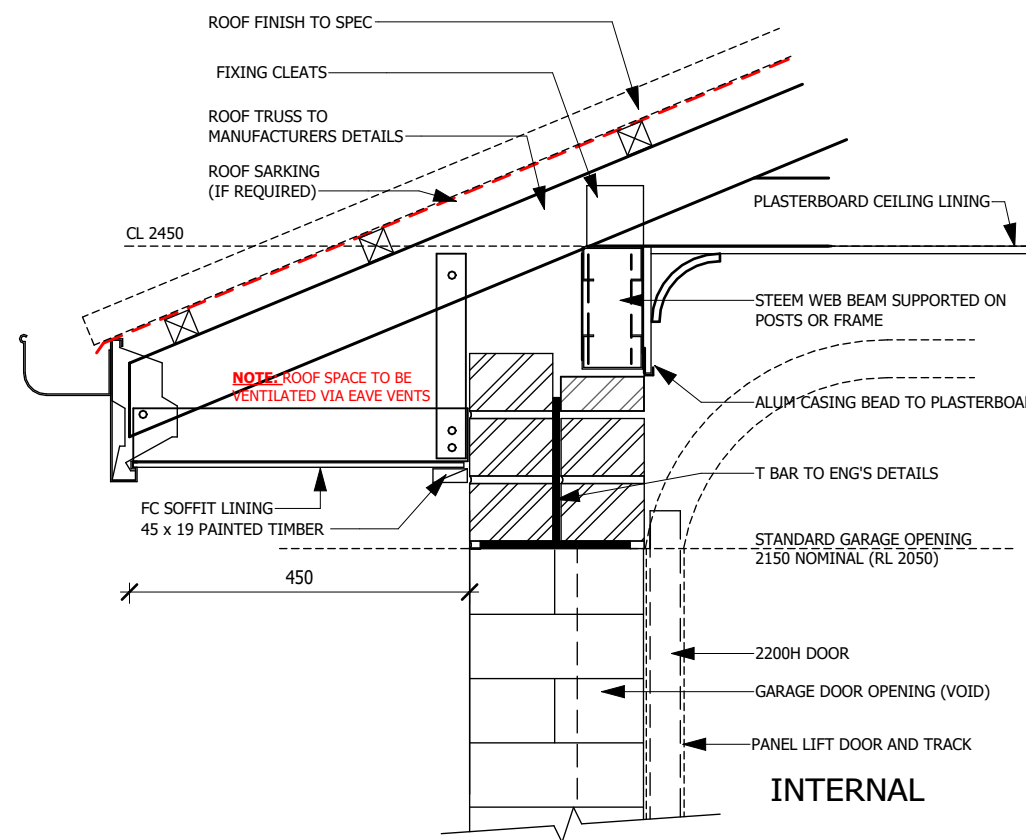

4 GARAGE DOOR HEAD DETAIL EAVES ABOVE
SCALE: 1 : 10

NOTES:

PLEASE NOTE: DETAILS SHOWN ON THESE PLANS ARE INTENDED TO BE ACCURATE - HOWEVER INFORMATION WRITTEN INTO INDIVIDUAL CONTRACTS WILL TAKE PRECEDENCE OVER PLANS
* ALL DIMENSIONS ARE IN MILLIMETRES
* DO NOT SCALE - USE WRITTEN DIMENSIONS
* ALL DIMENSIONS ARE TO STRUCTURAL FRAMES ONLY EXCLUDING FINISHED SURFACES

ThriveHomes

LEVEL 7, 5 RIDER BOULEVARD,
RHODES NSW 2138,
TELEPHONE 02 8758 4800,
FAX 02 9300 5646



Builder's licence No. 301349C

CLIENT:
THRIVE HOMES

SITE ADDRESS:
LOT 187 (DP 1304135)
No. 41 KEIGHTLEY AVENUE,
WINDRADYNE
BATHURST, NSW 2795

HOUSE TYPE: HELIX 24
FACADE: HUNTLEE
TYPE: DOUBLE GARAGE
SPECIFICATION: EVOQUE
DRAWING TITLE:
WALL OPENINGS DETAILS

DRAWN BY: HN	DATE DRAWN: 25.02.26	SCALE: 1 : 10
COUNCIL AREA: BATHURST		DRWG No: D3
JOB No: T001735		ISSUE: D

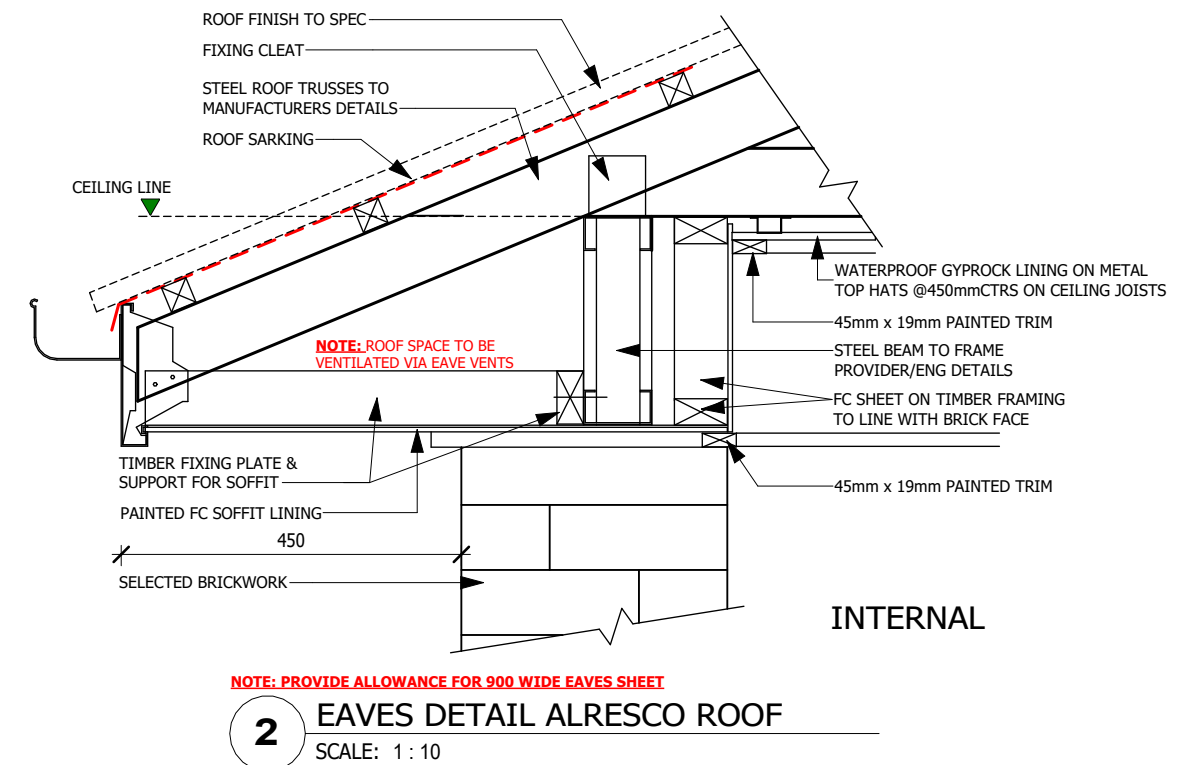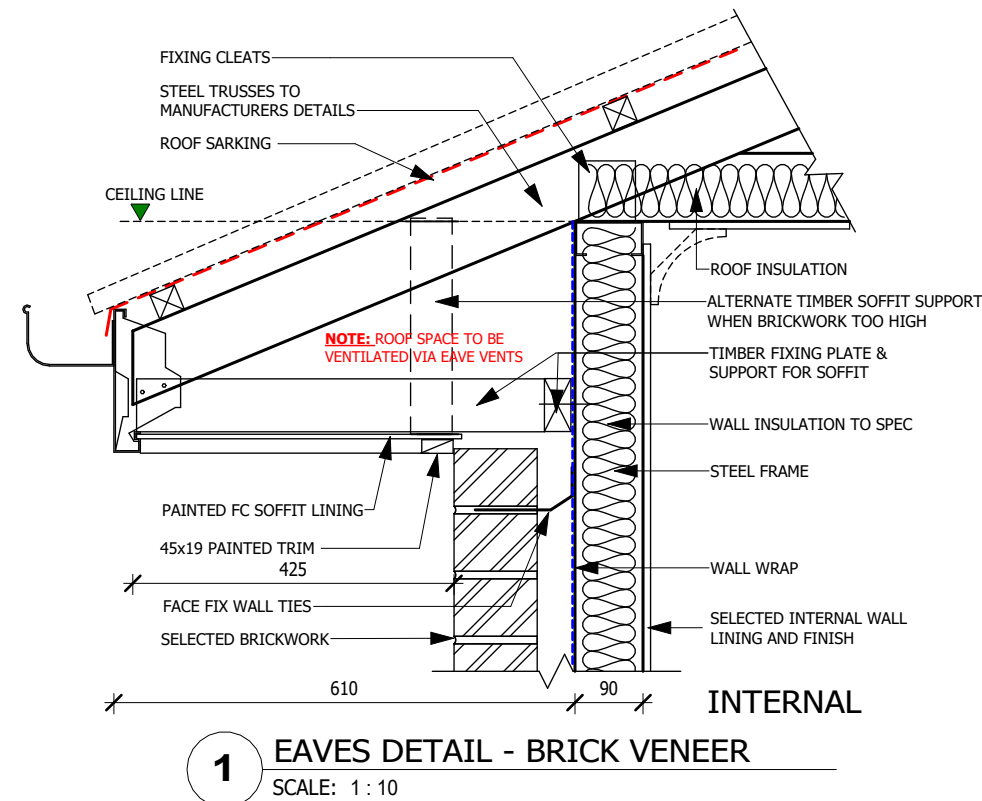

NOTES:

PLEASE NOTE: DETAILS SHOWN ON THESE PLANS ARE INTENDED TO BE ACCURATE - HOWEVER INFORMATION WRITTEN INTO INDIVIDUAL CONTRACTS WILL TAKE PRECEDENCE OVER PLANS

- * ALL DIMENSIONS ARE IN MILLIMETRES
- * DO NOT SCALE - USE WRITTEN DIMENSIONS
- * ALL DIMENSIONS ARE TO STRUCTURAL FRAMES ONLY EXCLUDING FINISHED SURFACES

ThriveHomes

LEVEL 7, 5 RIDER BOULEVARD,
RHODES NSW 2138,
TELEPHONE 02 8758 4800,
FAX 02 9300 5646

Builder's licence No. 301349C

CLIENT:
THRIVE HOMES


SITE ADDRESS:
LOT 187 (DP 1304135)
No. 41 KEIGHTLEY AVENUE,
WINDRADYNE
BATHURST, NSW 2795

HOUSE TYPE: HELIX 24
FACADE: HUNTLEE
TYPE: DOUBLE GARAGE
SPECIFICATION: EVOQUE
DRAWING TITLE:
TYPICAL EAVES DETAILS

DRAWN BY: HN	DATE DRAWN: 25.02.26	SCALE: 1 : 10
COUNCIL AREA: BATHURST		DRWG No: D4
JOB No: T001735		ISSUE: D


IMPORTANT NOTE: FINISHED TILED
HEIGHTS SHOWN ARE SUBJECT TO CHANGE
DEPENDING ON TILE SELECTION.
ALLOW ADJUSTMENTS IF LARGER/THICKER
TILES ARE SELECTED.

NOTE: **HEIGHT DIMENSIONS**
SHOULD BE MARKED FROM THE
MAIN HOUSE FIN. FLOOR LEVEL

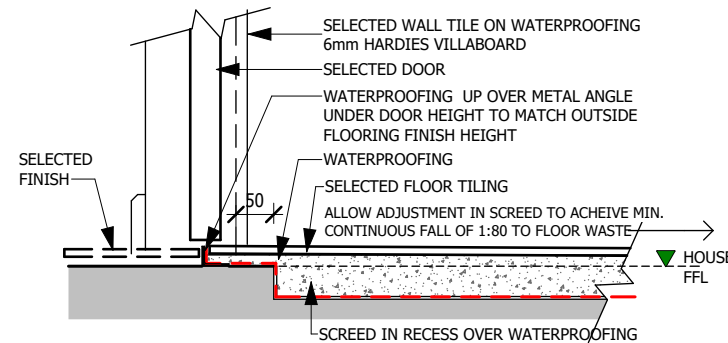


1 WET AREA DOOR THRESHOLD

SCALE: 1 : 10

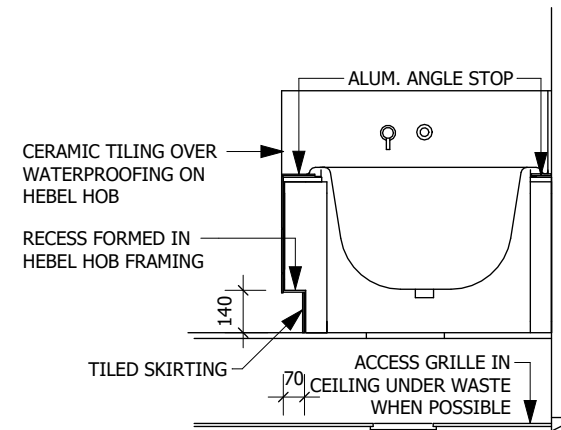

2 BATH WITH WINDOW DETAIL

SCALE: 1 : 25

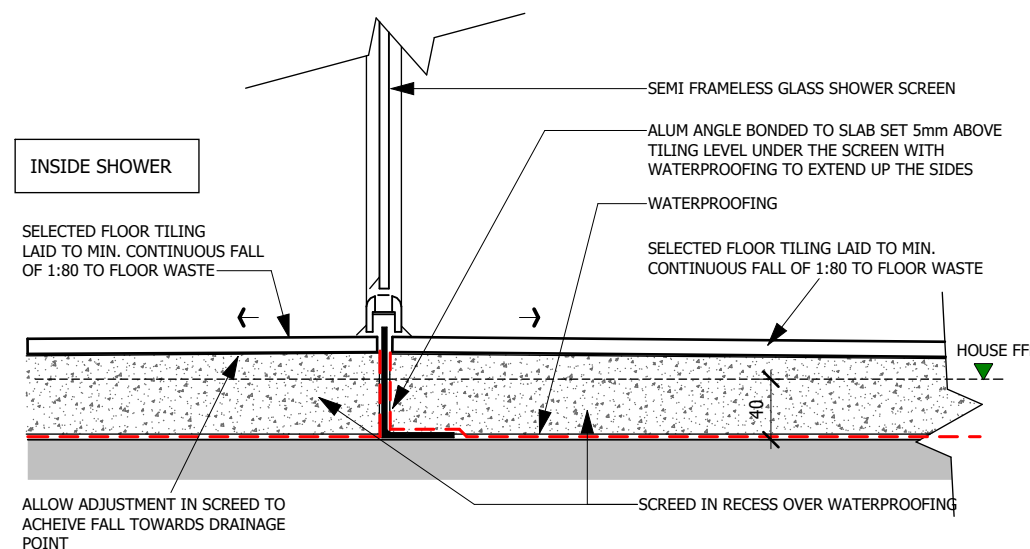

3 SEMI FRAMELESS SHOWER SCREEN DETAIL

SCALE: 1 : 5

NOTES:

PLEASE NOTE: DETAILS SHOWN ON THESE PLANS ARE INTENDED
TO BE ACCURATE - HOWEVER INFORMATION WRITTEN INTO
INDIVIDUAL CONTRACTS WILL TAKE PRECEDENCE OVER PLANS
* ALL DIMENSIONS ARE IN MILLIMETRES
* DO NOT SCALE - USE WRITTEN DIMENSIONS
* ALL DIMENSIONS ARE TO STRUCTURAL FRAMES ONLY
EXCLUDING FINISHED SURFACES

ThriveHomes

LEVEL 7, 5 RIDER BOULEVARD,
RHODES NSW 2138,
TELEPHONE 02 8758 4800,
FAX 02 9300 5646

Builder's licence No. 301349C

CLIENT:
THRIVE HOMES

SITE ADDRESS:
LOT 187 (DP 1304135)
No. 41 KEIGHTLEY AVENUE,
WINDRADYNE
BATHURST, NSW 2795

HOUSE TYPE: HELIX 24
FACADE: HUNTLEE
TYPE: DOUBLE GARAGE
SPECIFICATION: EVOQUE

DRAWING TITLE:
WET AREA DETAILS

DRAWN BY: HN
DATE DRAWN: 25.02.26
SCALE: As indicated

COUNCIL AREA: BATHURST
DRWG No: D5

JOB No: T001735
ISSUE: D