



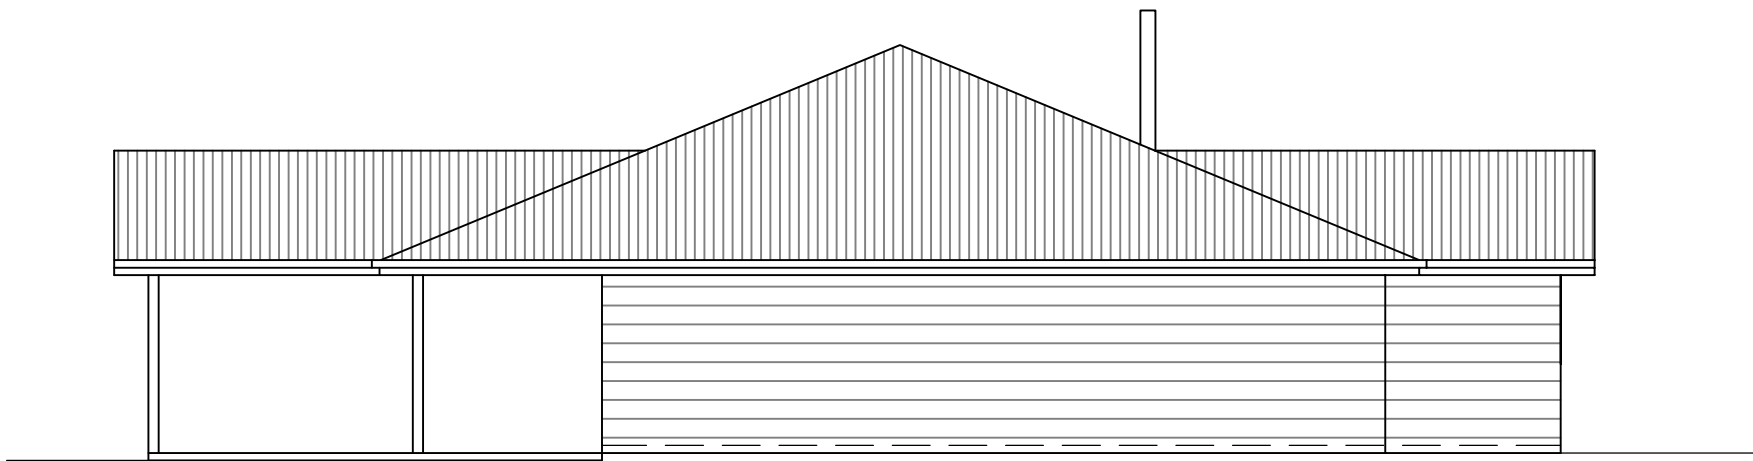

SOUTH ELEVATION
SCALE 1:100

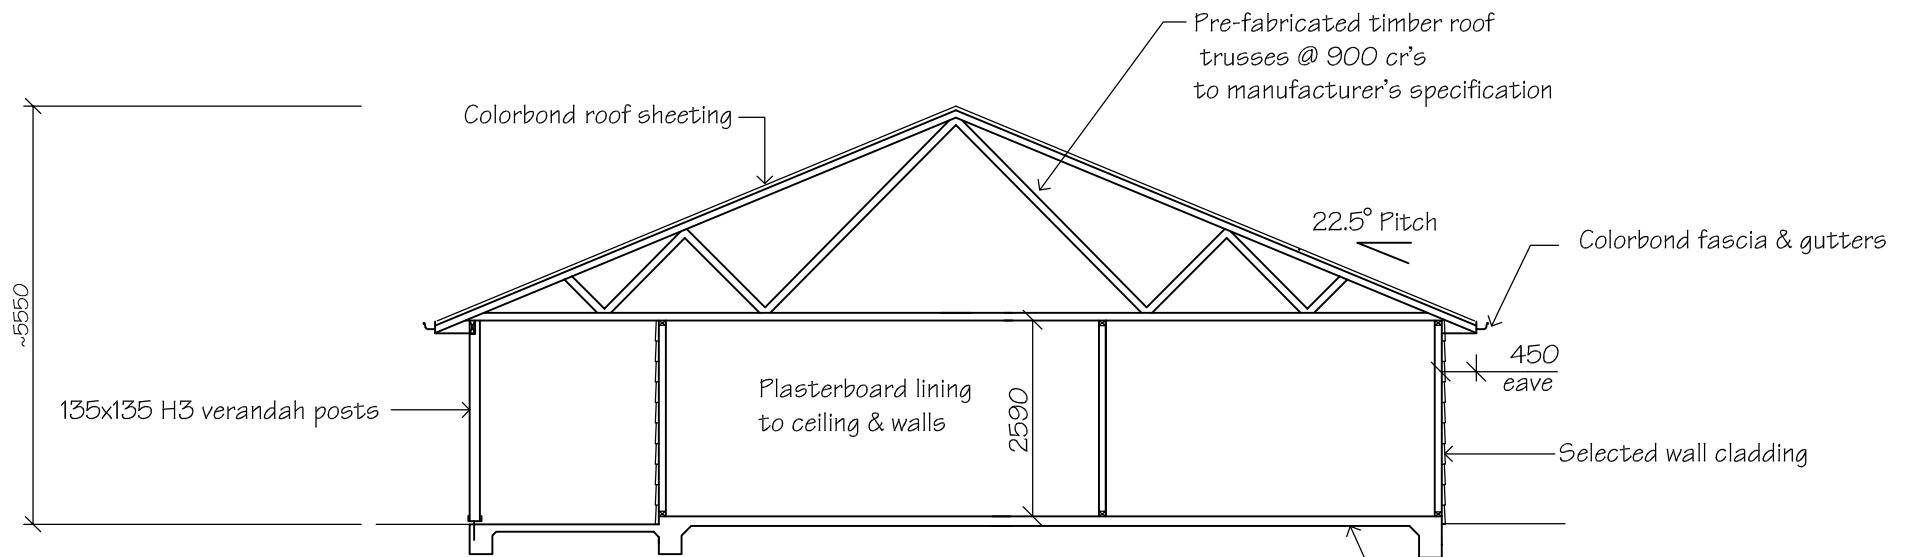

SECTION A-A
SCALE 1:100

BASIX REQUIREMENTS

REFER TO CERTIFICATE No. 17836775

WATER COMMITMENTS


- All showers to have min. 3 star rating showerheads (>7.5-9.0 L/min.)
- Each toilet to have min. 4 star rating flushing system
- All kitchen taps to have min. 4 star rating
- All bathroom basin taps to have min. 4 star rating
- Rainwater tank with a capacity of min. 100000 litres to collect 220m² of roof water and supply water to all fittings
- Maximum area of landscaping = 1000 sq m

THERMAL PERFORMANCE COMMITMENTS

See Insulation & Construction details

ENERGY COMMITMENTS

- Install electric heat pump hot water system (15-20 STC's or better)
- Nom cooling system
- Wood heater to living area
- Bathroom & kitchen exhaust fans to be ducted to roof or facade & operated by manual on/off switch
- Minimum 80% of light fixtures to be to be LED, compact fluorescent or fluorescent.
- Install a photovoltaic system withn the capacity to produce 15 peak kilowatts of electricity on east & west facing roof, as part of the development.
- Install gas cooktop and electric oven.
- Install fixed outdoor clothes drying line.

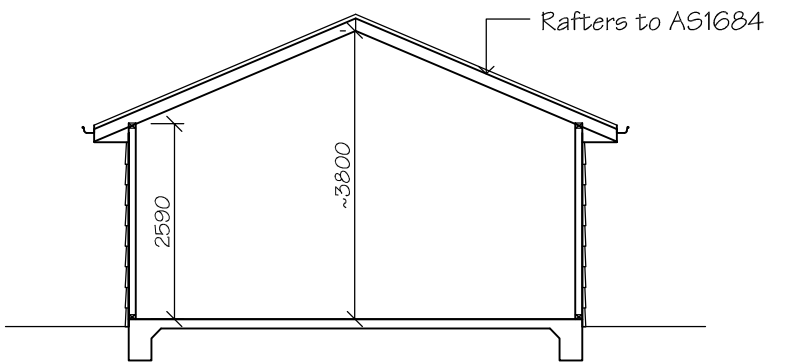


SECTION B-B
SCALE 1:100

Insulation & Construction Details


Roof colour	Dark (SA >0.70)
Roof	Reflective sarking
Ceilings	R5.0
External Walls	R2.7
Internal Walls	R2.5 (internal walls shared with bathroom, laundry, WC)
Floors	R1.5 to underside of slab (Foilboard Slabmate or equivalent) Draught stoppers & foam seals on all external doors. Draught stoppers on all ceiling exhaust fans.
Draught sealing	Draught stopper on wood heater flue.
Ceiling penetrations	Downlights to be IC rated to permit coverage with insulation.
Window / glass door type	Double glazed clear sliding w/aluminium frame U=4.10 & SHGC=0.52 (+or- 5%)
Front door	Solid timber (glass panels <25% of door area)




Project: PROPOSED RESIDENCE & SHED 329 MOUNT RANKIN ROAD MOUNT RANKIN			
Job No. 24.58	DWG. No. 3	Amdt. A	No. in set 7
Scale: AS SHOWN	Date: 14-2-25	File: 2458.dwg	

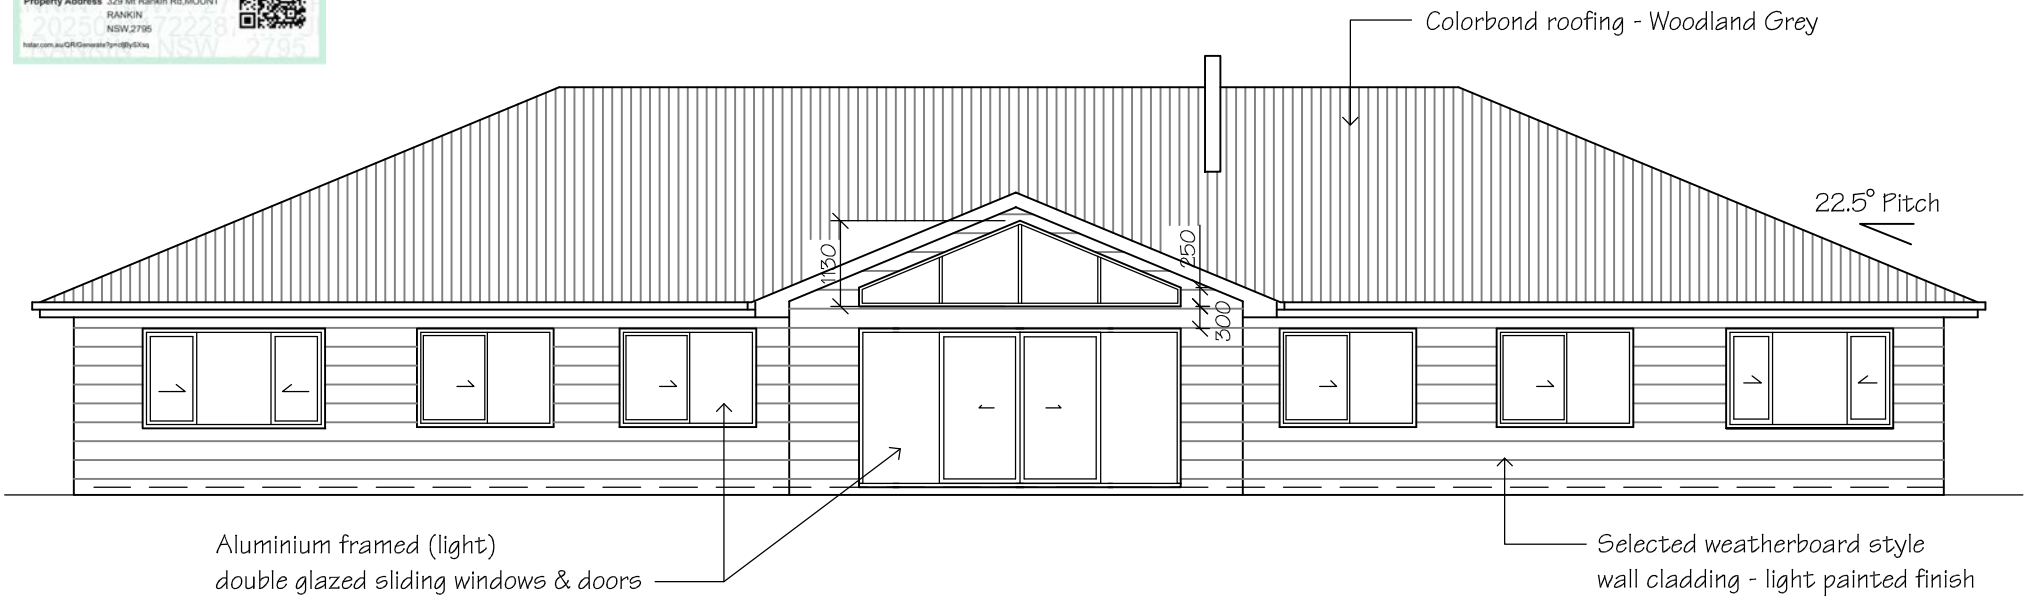

EAST ELEVATION
SCALE 1:100

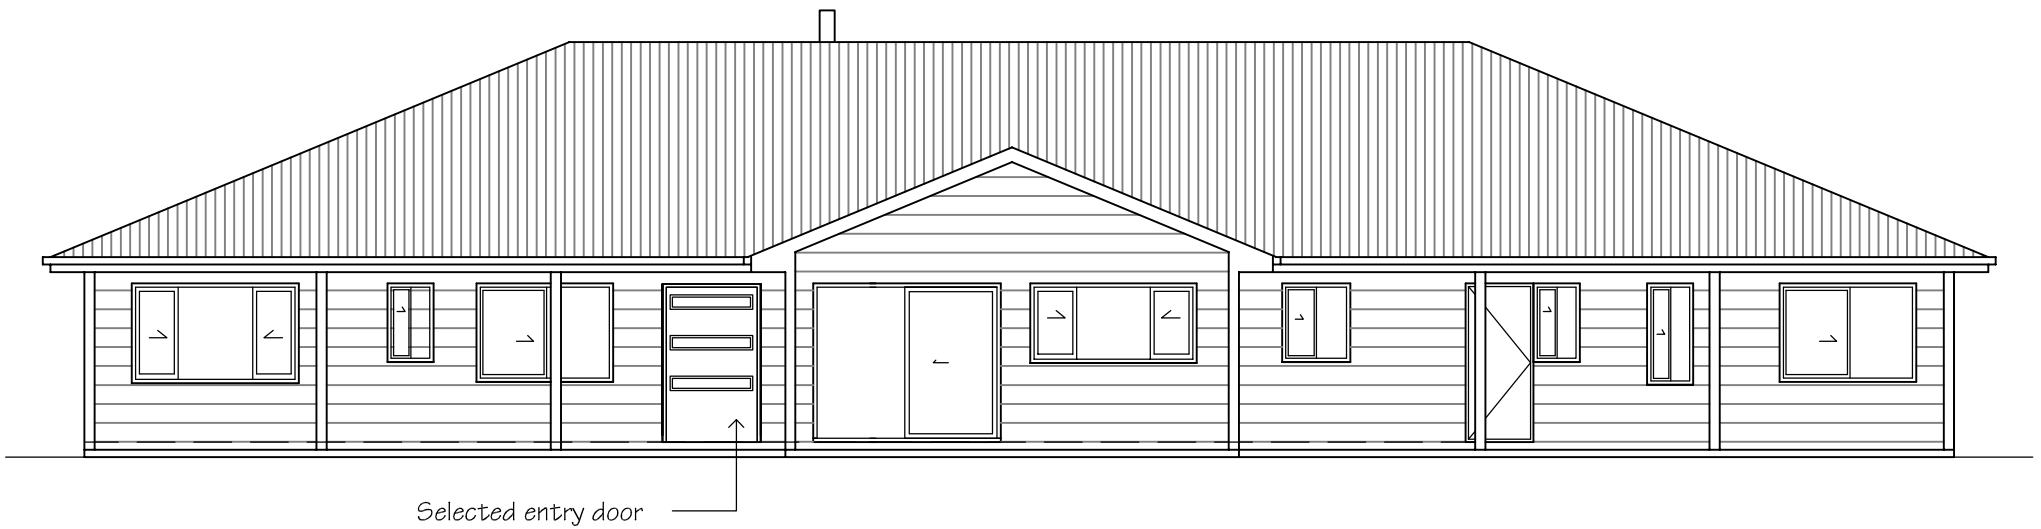


WEST ELEVATION
SCALE 1:100

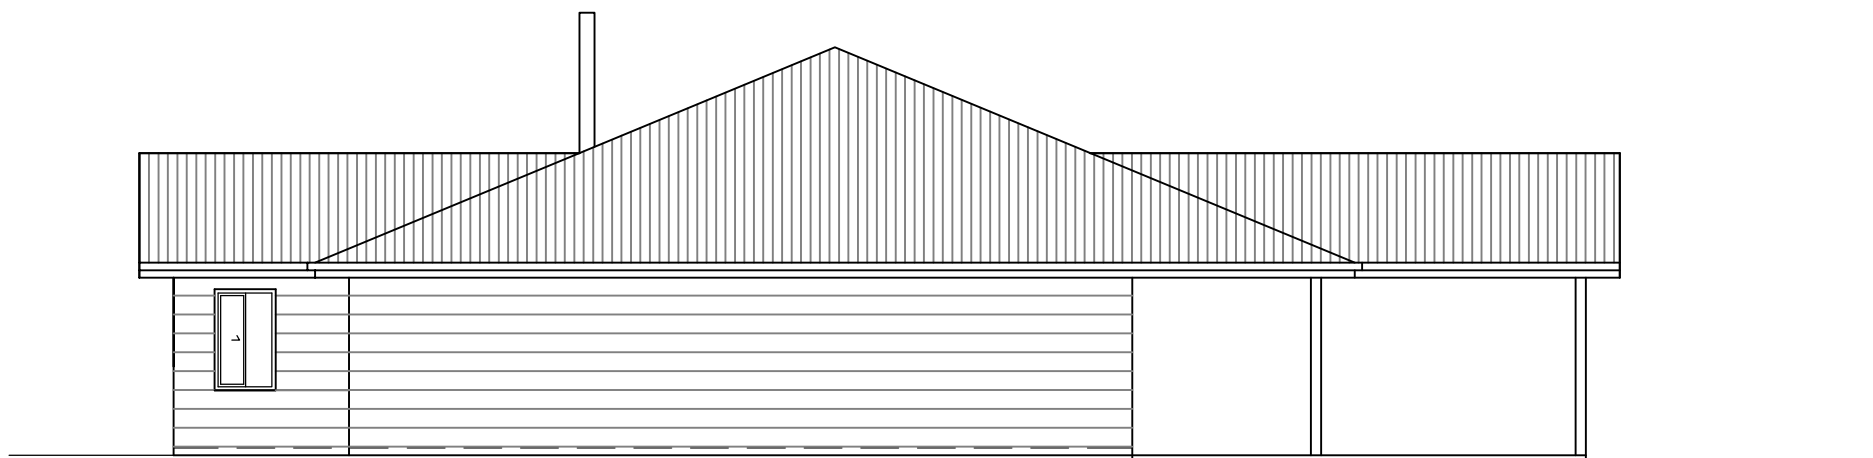


NORTH ELEVATION
SCALE 1:100

Project: PROPOSED RESIDENCE & SHED 329 MOUNT RANKIN ROAD MOUNT RANKIN			
Job No. 24.58	DWG. No. 2	Amdt. A	No. in set 7
Scale: AS SHOWN	Date: 14-2-25	File: 2458.dwg	

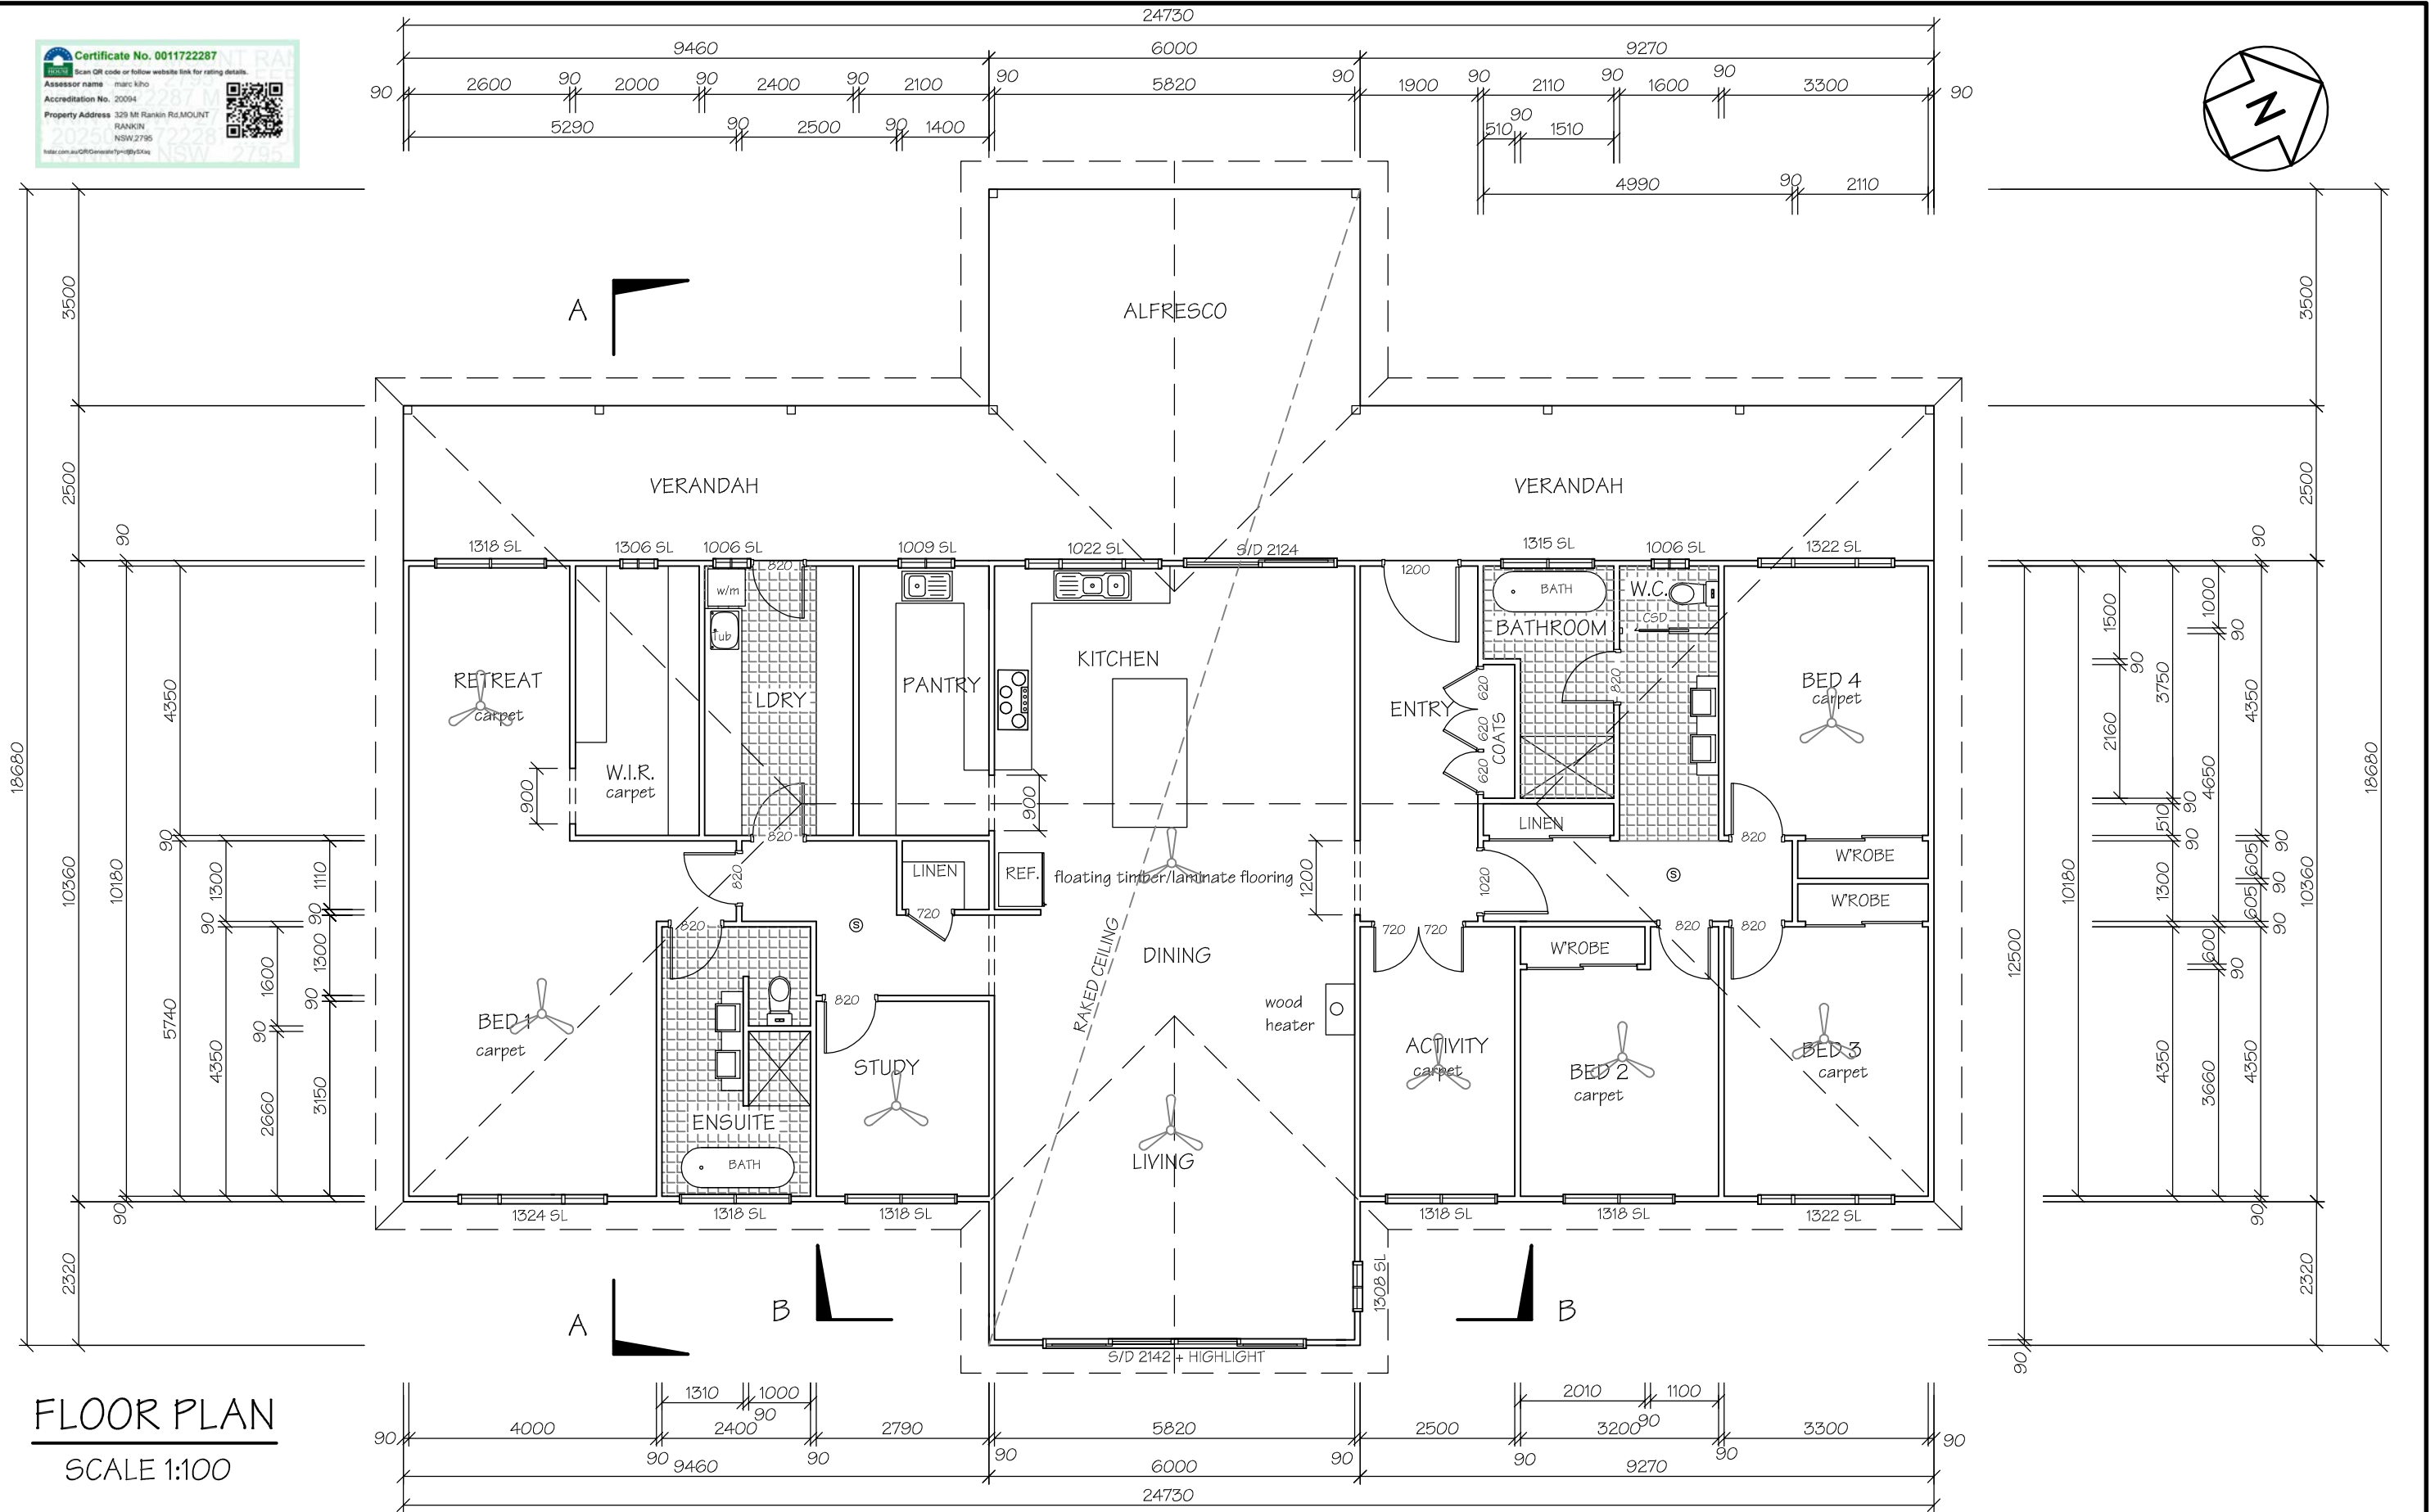

FLOOR PLAN
SCALE 1:100

Ⓢ DENOTES HARD WIRED SMOKE DETECTOR
to comply with AS3786

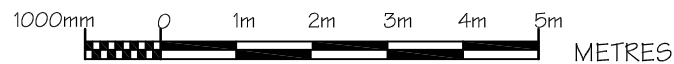

Presentation:

RELIABLE DRAFTING SERVICE

Kate Foody

12 Alexander Street

EGLINTON 2795

ph. 63 371116

mob. 0402608213

A.B.N. 60 167 131 984

email kate@draftingservice.net.au

Project:

PROPOSED RESIDENCE & SHED
329 MOUNT RANKIN ROAD
MOUNT RANKIN

Client:

M. & K. BORG

Floor Areas:

Living: 270.1m²

Alfresco & verandah: 82.2m²

TOTAL: 352.3m²

Job No.

24.58

DWG. No.

1

Amdt.

A

No. in set

7

Scale: AS SHOWN

Date: 14-2-25

File: 2458.dwg